

Примечание:

На столбике слова , "Не копать кабель" наносятся красной краской на светлом фоне. Головка столбика окрашивается в красный цвет.

Рев.	Дата	Назначение ревизии	Проверил	Утвердил
R1	16.10.2026	Выпущено для рассмотрения		

ЗАКАЗЧИК: UTG UZTRANSGAZ | ГЕНЕРАЛЬНЫЙ ПОДРЯДЧИК: UET UZBEKENERGOTAMIR | ПОДРЯДЧИК: PBG Pro Build Generation | ГЕНЕРАЛЬНЫЙ ПРОЕКТИРОВЩИК: EAST WEST ENGINEERING

Изм.	Кол. уч.	Лист.	№док.	Подп.	Дата
ГИП		Кирпичников С.			16.10.26
Нач. отд.		Кабулова Е.			16.10.26
Исполн.		Кабулова Е.			16.10.26
Н.контр.		Кирпичников С.			16.10.26

EWE0426-MGL1-COS-054-DRW-810204-R1

Строительство новых ниток (участков) газопроводов «Газли – Саримой» и «Акчалок – Газли – Нукус» общей протяженностью не менее 275 км

Газопровод Газли-Сарымай (54км)
Перенос ВОЛС

Стадия	Лист	Листов
РД	1	2

Типовые чертежи

ООО "EAST-WEST Engineering"
г. Ташкент 2026г.

Нормы расхода материалов:


Арматура d=12мм: 1.6м x 4шт. = 6.4м Арматура d=4мм: (0.12м x 4шт.) x 8шт. = 3.84м Объем бетона: (0.25м x 0.15м x 0.1м) + (1.1м x 0.15м x 0.15м) = 0.029м Вязальная проволока d=2мм: 0.15м x 30шт.=4.5м


Взам. инв. №

Подпись и дата

Инв.№ подл.

Указательный столбик

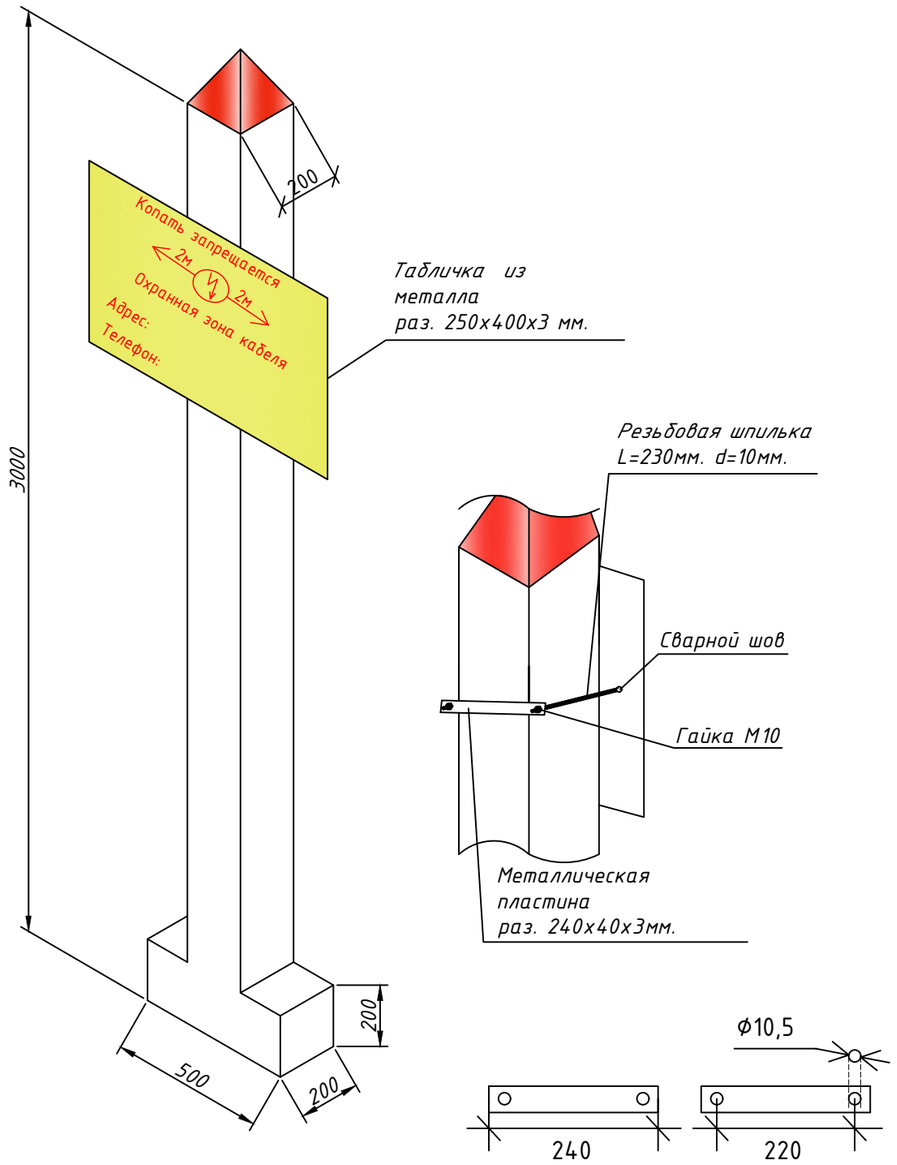

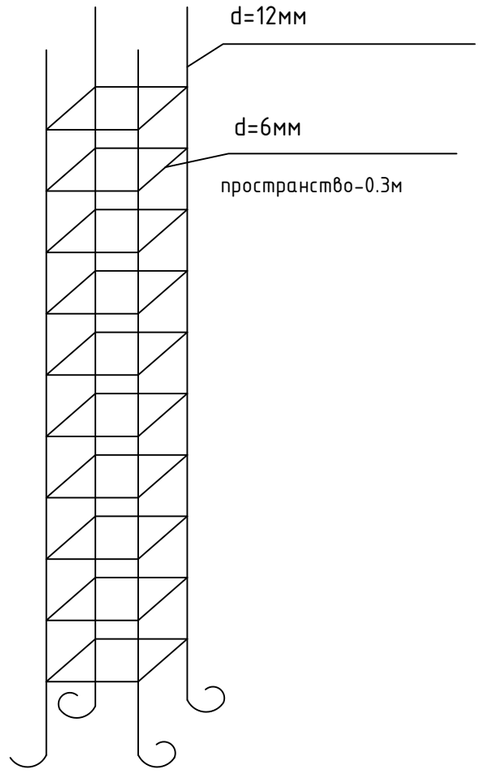

Нормы расхода материалов:

Арматура d=12мм: 3.15м х 4шт. – 12.6м
Арматура d=6мм: (0.18 х 4шт.) х 10шт. – 7.2м
Объем бетона: (0.50мх0.20мх0.20м) + (3.0мх0.2мх0.2м) – 0.14м3
Резьбовая шпилька: 230х10 мм. – 2 шт.
Гайка: М10 – 2 шт.
Металлическая пластина: 240х40х3 мм. – 1 шт.

Примечание:

В указательном столбике должны быть следующие знаки и надписи:
-изображение молнии и слова "Копать запрещается", "Охранная зона кабеля" наносятся красной краской на светлом фоне: "Адрес", "Телефон" – черной.

Рев.	Дата	Назначение ревизии	Проверил	Утвердил
R1	16.10.2026	Выпущено для рассмотрения		

ЗАКАЗЧИК: UTG UZTRANSGAZ | ГЕНЕРАЛЬНЫЙ ПОДРЯДЧИК: UET UZBEKENERGOTAMIR | ПОДРЯДЧИК: PBG Pro Build Generation | ГЕНЕРАЛЬНЫЙ ПРОЕКТИРОВЩИК: EAST WEST ENGINEERING

Изм.	Кол. уч.	Лист.	№док.	Подп.	Дата
ГИП		Кирпичников С.			16.10.26
Нач. отд.		Кабулова Е.			16.10.26
Исполн.		Кабулова Е.			16.10.26
Н.контр.		Кирпичников С.			16.10.26

EWE0426-MGL1-COS-054-DRW-810204-R1

Строительство новых ниток (участков) газопроводов «Газли – Саримой» и «Акчалок – Газли – Нукус» общей протяженностью не менее 275 км

Газопровод Газли-Сарымай (54км)
Перенос ВОЛС

Стадия	Лист	Листов
РД	2	2

Типовые чертежи

ООО "EAST-WEST Engineering"
г. Ташкент 2026г.

Взам. инв. №
Подпись и дата
Инв.№ подл.

Формат А3 / Format A3