СХЕМА 1

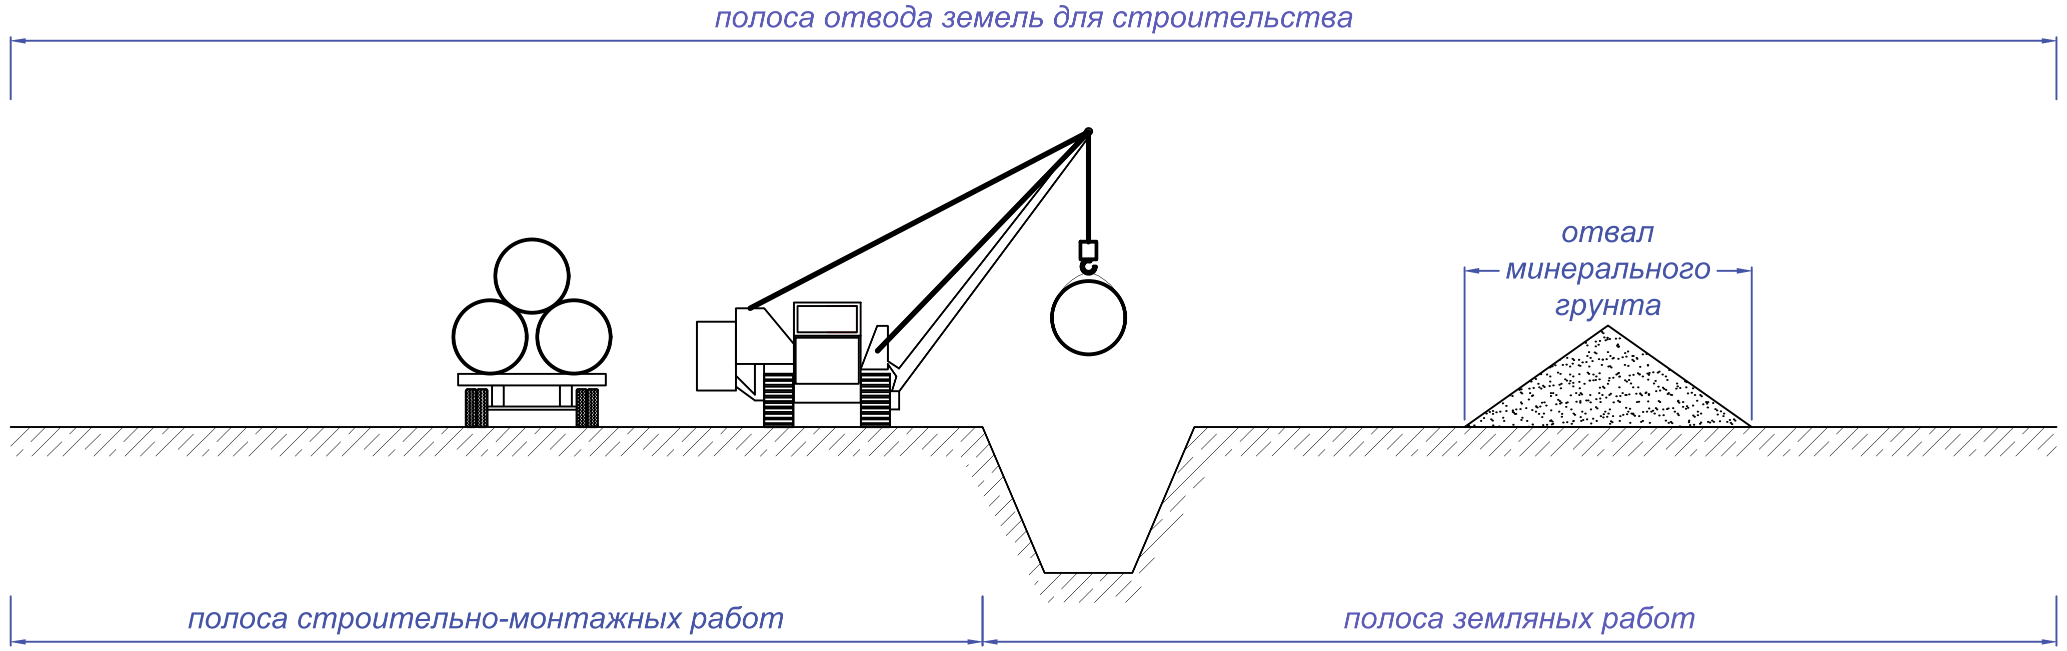
полоса отвода земель для строительства
отвал минерального грунта
полоса строительно-монтажных работ
полоса земляных работ

СХЕМА 2


полоса отвода земель для строительства
снятие плодородного слоя 3,5 м
отвал минерального грунта
отвал плодородной почвы
полоса строительно-монтажных работ
полоса земляных работ

Полоса строительно-монтажных работ	
Диаметр трубопровода, мм	Минимальная ширина, м
До 426 включительно	11
Более 426 до 720 включительно	12,5
Более 720 до 1020 включительно	12,7
Более 1020 до 1220 включительно	13,2
Более 1220 до 1420 включительно	13,4

Ширина полосы отвода земель для строительства одного подземного трубопровода, м		
Диаметр трубопровода, мм	земли несельскохозяйственного назначения, или непригодные для сельского хозяйства, земли государственного лесного фонда (схема 1)	земли сельскохозяйственного назначения при снятии и восстановлении плодлолдного слоя (схема 2)
До 426 включительно	20	28
Более 426 до 720 включительно	23	33
Более 720 до 1020 включительно	28	39
Более 1020 до 1220 включительно	30	42
Более 1220 до 1420 включительно	32	45

1. Настоящий чертеж разработан на основании требований и рекомендаций СН 452-73 "Нормы отвода земаль для магистральных трубопроводов" и ВСН 179-85 "Инструкция по рекультивации земель при строительстве трубопроводов".
2. Ширина полос, отводимых во временное пользование для капитального ремонта магистральных газопроводов, не должна превышать ширины, указанной в таблице.

Рев.	Дата	Назначение ревизии	Проверил	Утвердил
A1	09.10.2026	Выпущено для строительства		
R1	22.07.2026	Выпущено для рассмотрения		

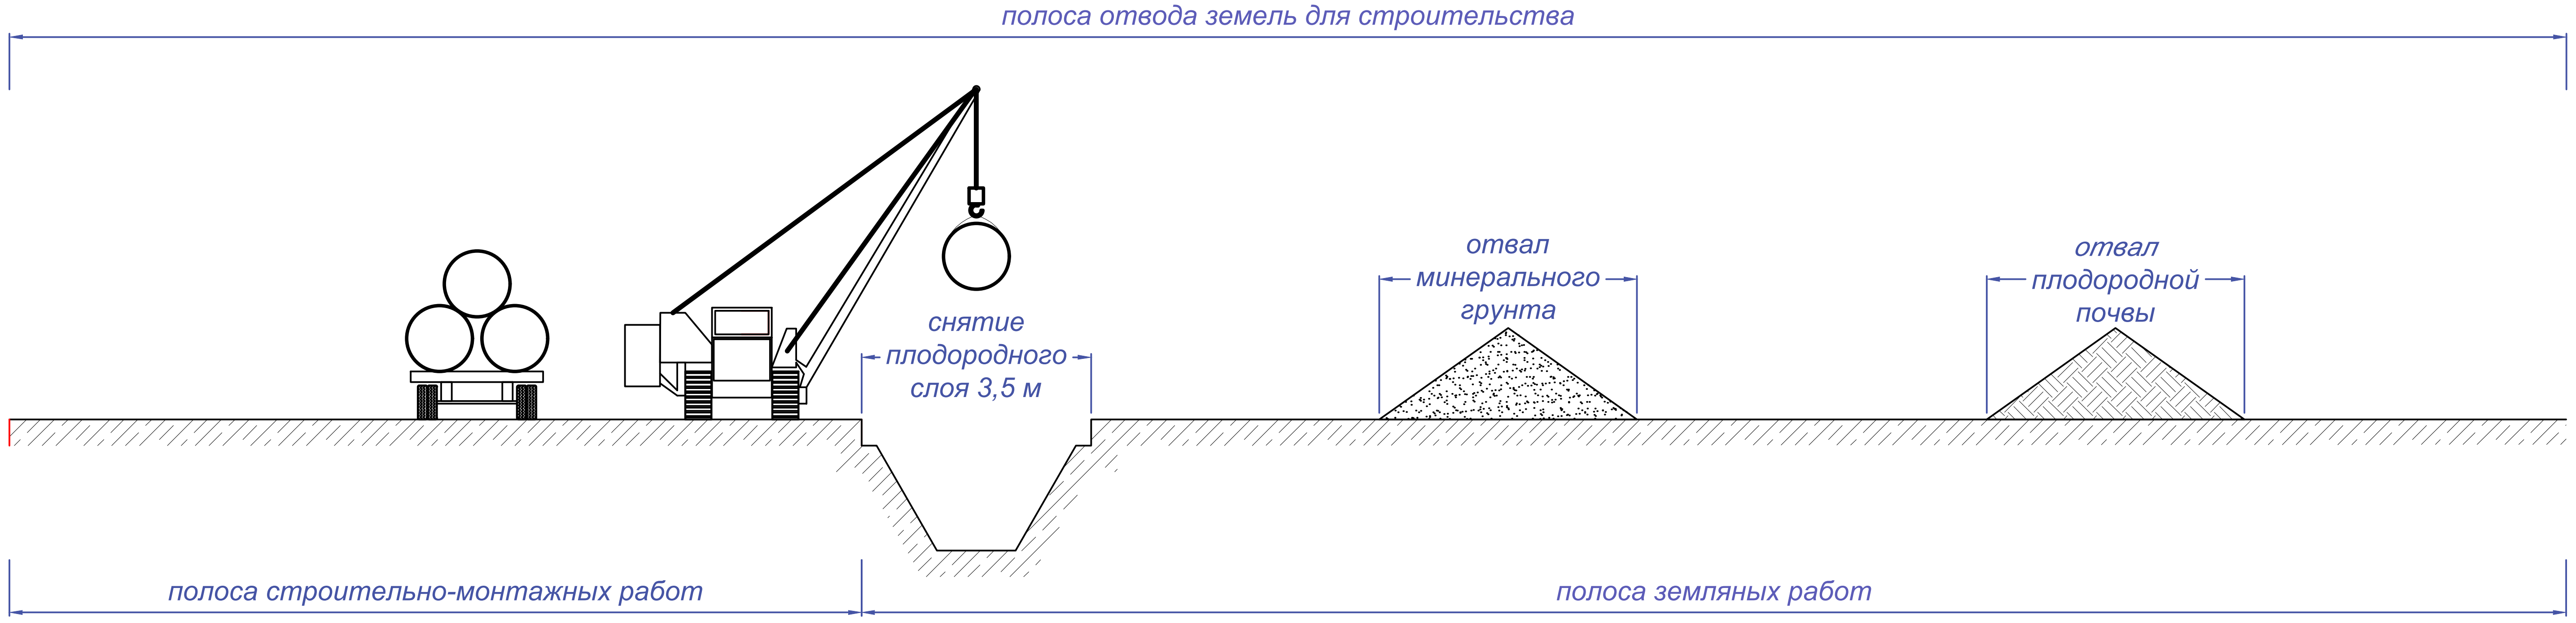ЗАКАЗЧИК: UTG UZTRANSGAZ

ГЕНЕРАЛЬНЫЙ ПОДРЯДЧИК: UET UZBEKENERGOTAMIR

ПОДРЯДЧИК: PBG Pro Build Generation

ГЕНЕРАЛЬНЫЙ ПРОЕКТИРОВЩИК: EAST WEST ENGINEERING

EWE0426-MGL1-PIL-000-DRW-810201-A1

«СТРОИТЕЛЬСТВО НОВЫХ НИТОК (УЧАСТКОВ) ГАЗОПРОВОДОВ «ГАЗЛИ - САРИМОЙ» И «АКЧАЛОК - ГАЗЛИ - НУКУС» ОБЩЕЙ ПРОТЯЖЕННОСТЬЮ НЕ МЕНЕЕ 275 КМ».

Изм.	Кол.уч.	Лист	№док.	Подпись	Дата
ГИП		Кирпичников С.			09.10.2026
Провер.		Кирпичников С.			09.10.2026
Исполн.		Шафиева О.			09.10.2026
Н.контр		Кирпичников С.			09.10.2026

Магистральные газопроводы с перемычками Ф1220, Ф1020

Стадия	Лист	Листов
РД	1	1

Ширина полосы отвода земель для строительства газопровода. Типовой чертеж

EAST WEST ENGINEERING
ООО "EAST-WEST Engineering"
г. Ташкент 2026г.

Формат A4x3

Взам. инв. №

Подпись и дата

Инв. № подл.