Схема границы охранной зоны магистрального газопровода

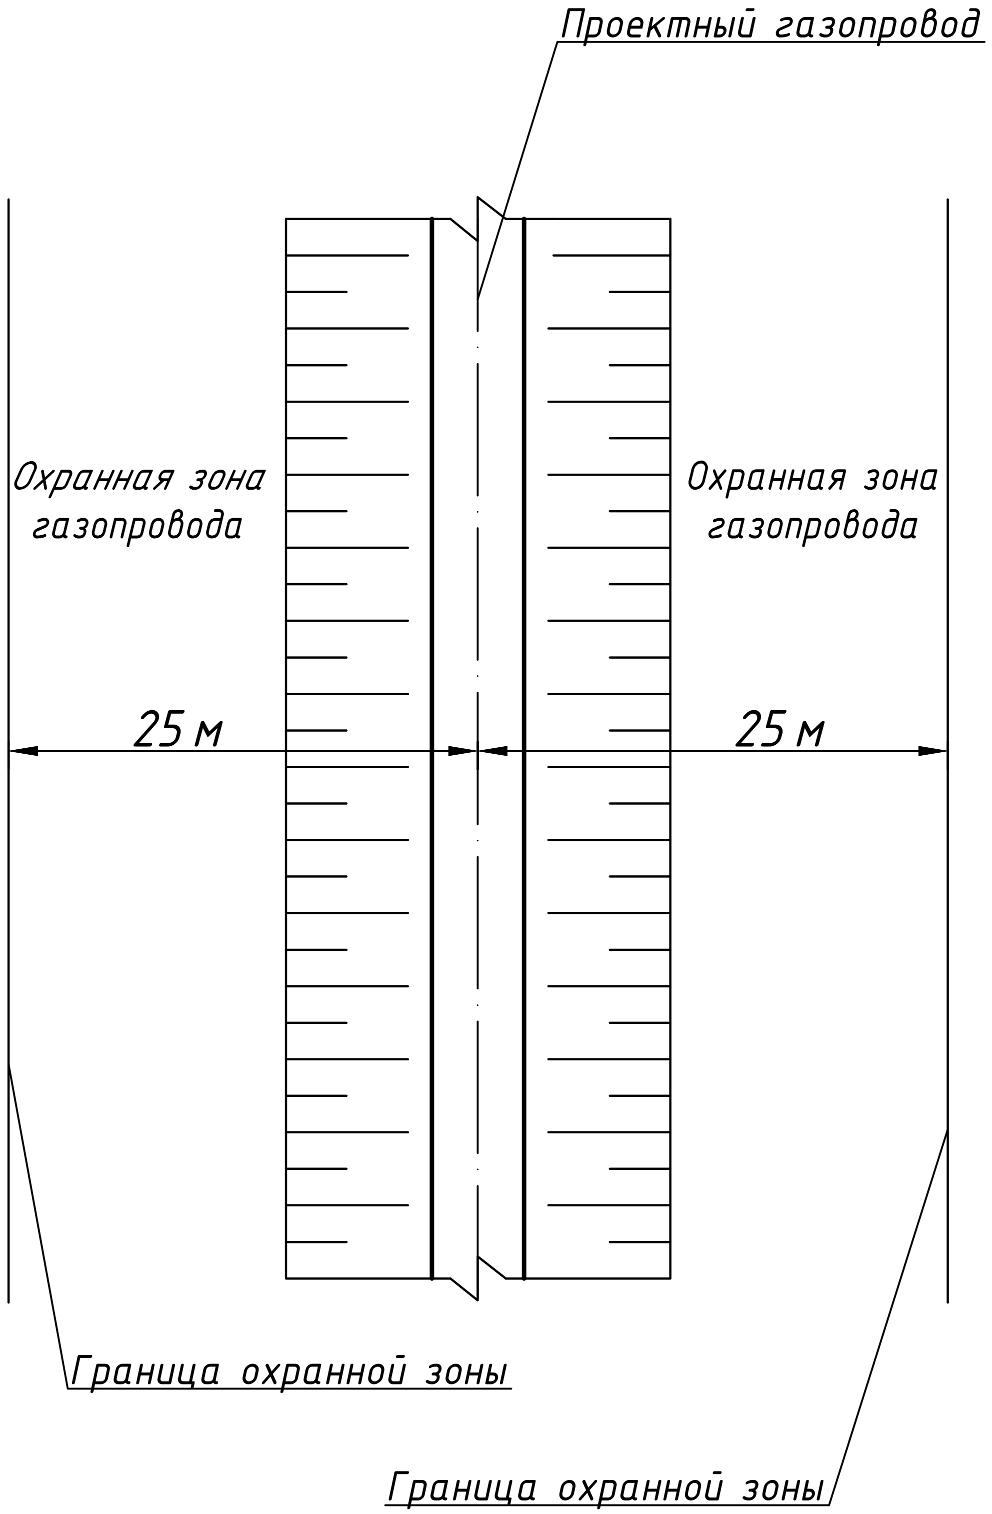

1 Производство работ по трассе проектного газопровода вести в строгом соответствии с "Инструкцией по производству строительных работ в охранных зонах магистральных трубопроводов Мингазпрома" ВСН 51-1-80.

2 Охранная зона — это участок земли, ограниченный условными линиями, проходящими в 25 метрах от оси магистральных газопроводов с каждой стороны.

3 В границах охранных зон запрещается:

- перемещать, демонтировать, засыпать, повреждать указатели трасс подземных газопроводов и мест расположения сетевых сооружений на них, контрольно-измерительные пункты;
- открывать самовольно люки газовых колодцев и коверов, станций защиты газопроводов от коррозии, открывать и закрывать краны и задвижки, отключать и включать средства энергоснабжения и телемеханики газопроводов;
- устраивать свалки, выливать агрессивные жидкости, в том числе растворы кислот, солей и щелочей;
- складировать материалы и оборудование (в том числе для временного хранения) вдоль трассы подземного газопровода в пределах 2 метров по обе стороны от оси, а также производить посадку деревьев и кустарников всех видов в пределах 1,5 метра по обе стороны от оси газопровода;
- разрушать сооружения и устройства, предохраняющие газопроводы и сооружения на них от повреждений;
- проходить с цепями, лотами, волокушами, проводить траление жёсткими и полужёсткими тралами;
- разводить огонь и размещать какие-либо открытые или закрытые источники огня;
- проводить любые мероприятия, связанные с большим скоплением людей, не занятых выполнением разрешённых в установленном порядке работ;
- осуществлять строительство зданий, строений и сооружений.

Рев.	Дата	Назначение ревизии	Проверил	Утвердил
A1	09.10.2026	Выпущено для строительства		
R1	22.07.2026	Выпущено для рассмотрения		

ЗАКАЗЧИК: UTG UZTRANSGAZ
ГЕНЕРАЛЬНЫЙ ПОДРЯДЧИК: UET UZBEKENERGOTAMIR
ПОДРЯДЧИК: PBG Pro Build Generation
ГЕНЕРАЛЬНЫЙ ПРОЕКТИРОВЩИК: EAST WEST ENGINEERING

EWE0426-MGL1-PIL-000-DRW-810202-A1

«СТРОИТЕЛЬСТВО НОВЫХ НИТОК (УЧАСТКОВ) ГАЗОПРОВОДОВ «ГАЗЛИ - САРИМОЙ» И «АКЧАЛОК - ГАЗЛИ - НУКУС» ОБЩЕЙ ПРОТЯЖЕННОСТЬЮ НЕ МЕНЕЕ 275 КМ».

Изм.	Кол.уч.	Лист	№док.	Подпись	Дата
ГИП		Кирпичников С.			09.10.2026
Провер.		Кирпичников С.			09.10.2026
Исполн.		Шафиева О.			09.10.2026
Н.контр		Кирпичников С.			09.10.2026

Магистральные газопроводы с перемычками Ф1220, Ф1020

Стадия	Лист	Листов
РД	1	1

Охранная зона магистрального газопровода.
Типовой чертеж

EAST WEST ENGINEERING
ООО "EAST-WEST Engineering"
г. Ташкент 2026г.

Формат А3

Инв. № подл.
Подпись и дата
Взам. инв. №