ЗАКАЗЧИК: **ГЕНЕРАЛЬНЫЙ ПОДРЯДЧИК:** **ПОДРЯДЧИК:** **ГЕНЕРАЛЬНЫЙ ПРОЕКТИРОВЩИК:**

ОБЪЕКТ: «СТРОИТЕЛЬСТВО МАГИСТРАЛЬНОГО ГАЗОПРОВОДА ОТ КОМПРЕССОРНОЙ СТАНЦИИ «АКЧАЛАК» ДО УЧАСТКА 175 КМ МАГИСТРАЛЬНОГО ГАЗОПРОВОДА «ГАЗЛИ-НУКУС» (ПРОТЯЖЕННОСТЬЮ 221 КМ)», «СТРОИТЕЛЬСТВО МАГИСТРАЛЬНОГО ГАЗОПРОВОДА «ГАЗЛИ-САРЫМАЙ» 105-159 КМ (ПРОТЯЖЕННОСТЬЮ 54 КМ)»

КОНТРАКТ №: EWEUZ-DW-26/04 от 16.04.2026г.

Ревизия документа: R1

Дата: 13.05.2026.

ООО “EAST-WEST ENGINEERING”

Критерии проектирования генерального плана

EWE0426-MGL1-ALL-000-REG-810301-R1

Согласовано

Гл.инженер	
Калугин	
04.26	

Взам. инв. №

Подпись и дата

Инв.№подл.

Изм.	Кол.уч.	Лист	№док.	Подпись	Дата	EWE0426-MGL1-ALL-000-REG-810301-R1		
ГИП		Схабицкий А.			05.26	Критерии проектирования генерального плана	Стадия	Лист	Листов
Нач.отд.		Нигманова Н.			05.26		РД	1	5
Исполн.		Нигманова Н.			05.26		ООО “EAST-WEST Engineering” г. Ташкент 2026г.		
Н.контр.		Схабицкий А.			05.26				

Лист регистрации изменений

Ревизия	Дата	Цель ревизии	Разработал	Проверил	Утвердил
R1	13.05.2026	Выпуск для проверки	Нигманова Н.	Нигманова Н.	Схабицкий А.

ОГЛАВЛЕНИЕ

1. Используемые нормативные документы 4
2. Решения и показатели по генеральному плану, внутриплощадочному и внешнему транспорту 4
3. Мероприятия по благоустройству 5
4. Организация охраны предприятия 5

1. Используемые нормативные документы

При проектировании необходимо руководствоваться действующими стандартами, нормативно-правовыми актами и руководящими документами Республики Узбекистан:

№	Номер стандарта, нормативного акта, руководящего документа	Наименование стандарта, нормативного акта, руководящего документа
1	Стандарты Республики Узбекистан	
2	ШНК 2.09.17-21	Проектирование генеральных планов промышленных предприятий
3	ШНК 2.05.02-23	Автомобильные дороги
4	СП-37.13330.2012	Промышленный транспорт
5	МСН 2.03-02-2002	Инженерная защита территории зданий и сооружений от опасных геологических процессов
6	КМК 2.07.03-97	Ограждение территории предприятий, зданий и сооружений
7	ОНТП 51-1-85	Общесоюзные нормы технологического проектирования. Магистральные трубопроводы
8	ВСН 51-3-85	Проектирование промысловых стальных трубопроводов

2. Решения и показатели по генеральному плану, внутриплощадочному и внешнему транспорту

Генеральные планы площадок узла запуска очистных устройств (УЗОУ), крановых узлов (КУП) и узла замера расхода газа (УЗРГ) разрабатываются на основе принятой технологической схемы с учетом следующих требований:

- применения планировочных решений, соответствующих международным стандартам;
- эффективного использования территории;
- рационального размещения технологического оборудования во взаимосвязи со вспомогательными зданиями и сооружениями;
- благоустройства территории;
- соблюдения экологических, санитарных и противопожарных норм, а также требований к автоматизации зданий и сооружений.

На территории площадки предусматриваются:

- въезды/выезды на площадки УЗОУ и УЗРГ с воротами шириной 4,5 м, подъездными автомобильными дорогами шириной 4,5 м и разворотными площадками размером 12×12 м;
- подъезды к крановым узлам, обеспечивающие доступ пожарной техники и обслуживающего транспорта.

В составе проектной документации должны быть приведены основные технико-экономические показатели площадок.

3. Мероприятия по благоустройству

На площадках УЗОУ предусматривается благоустройство территории с устройством покрытий подъездных автомобильных дорог, разворотных площадок, обочин и площадок в пределах ограждения. Конструкции покрытий принимаются из щебеночно- и гравийно-песчаных смесей, железобетонных плит с заполнением швов монолитным бетоном, а также щебеночных слоев по уплотненному грунтовому основанию с обеспечением нормативных коэффициентов уплотнения.

На площадке УЗРГ покрытия подъездных автодорог, проездов и площадки в пределах ограждения приняты аналогичными решениям, примененным на площадках УЗОУ.

Тротуарное покрытие на площадке УЗРГ предусматривается из бетонных плит по песчаному основанию с устройством подстилающего слоя и уплотненного грунта.

На площадках крановых узлов КУП покрытия подъездных автодорог и площадок в пределах ограждения приняты аналогичными решениям, предусмотренным для площадок УЗОУ и УЗРГ.

Отвод дождевых стоков должен быть предусмотрен самотеком по проектному рельефу с обеспечением нормативных уклонов и исключением размещения площадок в зонах подтопления.

4. Организация охраны предприятия

В состав охраны площадок узла запуска очистных устройств (УЗОУ), крановых узлов (КУП) и узла замера расхода газа (УЗРГ) входит периметральное ограждение.

Ограждение предусматривается типа «Махаон» высотой 2,25 м. Допускается применение других типов ограждений при условии обеспечения требуемых эксплуатационных и охранных характеристик.

В составе проектной документации представлено приложение, содержащее пример оформления чертежей площадок узла запуска очистных устройств (УЗОУ), крановых узлов (КУП) и узла замера расхода газа (УЗРГ).

Ведомость рабочих чертежей основного комплекта

Лист	Наименование	Примечание
1	Общие данные	
	XXXX-XX-XXX-XXX-XXX-XXX-XX	
2	Разбивочный план М 1:500	
	XXXX-XX-XXX-XXX-XXX-XXX-XX	
3	План организации рельефа М 1:500	
	XXXX-XX-XXX-XXX-XXX-XXX-XX	
4	План земляных масс М 1:500	
	XXXX-XX-XXX-XXX-XXX-XXX-XX	
5	Сводный план инженерных сетей М 1:500	
	XXXX-XX-XXX-XXX-XXX-XXX-XX	
6	План благоустройства территории М 1:500	
	XXXX-XX-XXX-XXX-XXX-XXX-XX	
7	Ведомость объемов работ	2 листа
	XXXX-XX-XXX-XXX-XXX-XXX-XX	

Ведомость основных комплектов рабочих чертежей

Обозначение	Наименование	Примечание
XXXX-XX-XXX-PLT	Генеральный план и транспорт	
XXXX-XX-XXX-PPL	Линейная часть	
XXXX-XX-XXX-OPN	Технологическая часть	
XXXX-XX-XXX-ELE	Электротехническая часть	
XXXX-XX-XXX-SST	Строительная часть	
XXXX-XX-XXX-SYS	Автоматизация технологии и производства	

Ведомость ссылочных и прилагаемых документов

Обозначение	Наименование	Примечание
ШНК 2.09.17-21	Проектирование генеральных планов промышленных предприятий	
ШНК 2.05.02-23	Автомобильные дороги	
СП-37.13330.2012	Промышленный транспорт	
МСН 2.03-02-2002	Инженерная защита территории зданий и	
	сооружений от опасных геологических процессов	
КМК 2.07.03-97	Ограждение территорий предприятий, зданий	
	и сооружений	
КМК 2.05.06-97	Магистральные трубопроводы	
ОНТП 51-1-85	Общесоюзные нормы технологического	
	проектирования. Магистральные трубопроводы.	
	Часть 1. Газопровод	

Общие указания


Генеральный план разработан на основании задания ГИПа и плана, выданного заказчиком.

Компоновка сооружений генплана решена с учетом положения существующих автодорог во взаимосвязи с технологическими процессами, а также с учетом зонального размещения объектов по назначению. Во избежание аварий до начала производства земляных работ необходимо определить фактическое положение подземных инженерных сетей и принять меры, по их защите.

Рабочие чертежи разработаны в соотвествии с действующими нормами, правилами и стандартами.

Изм.	Кол.уч	Лист	№док	Подп.	Дата				
ГИП						Крановый узел. Генеральный план и транспорт.	Стадия	Лист	Листов
Нач.отд.							РП	1	1
Исполн.									
						Общие данные			
Н.контр.									

Взам. инв.№ | Подпись и дата | Инв. №подл.

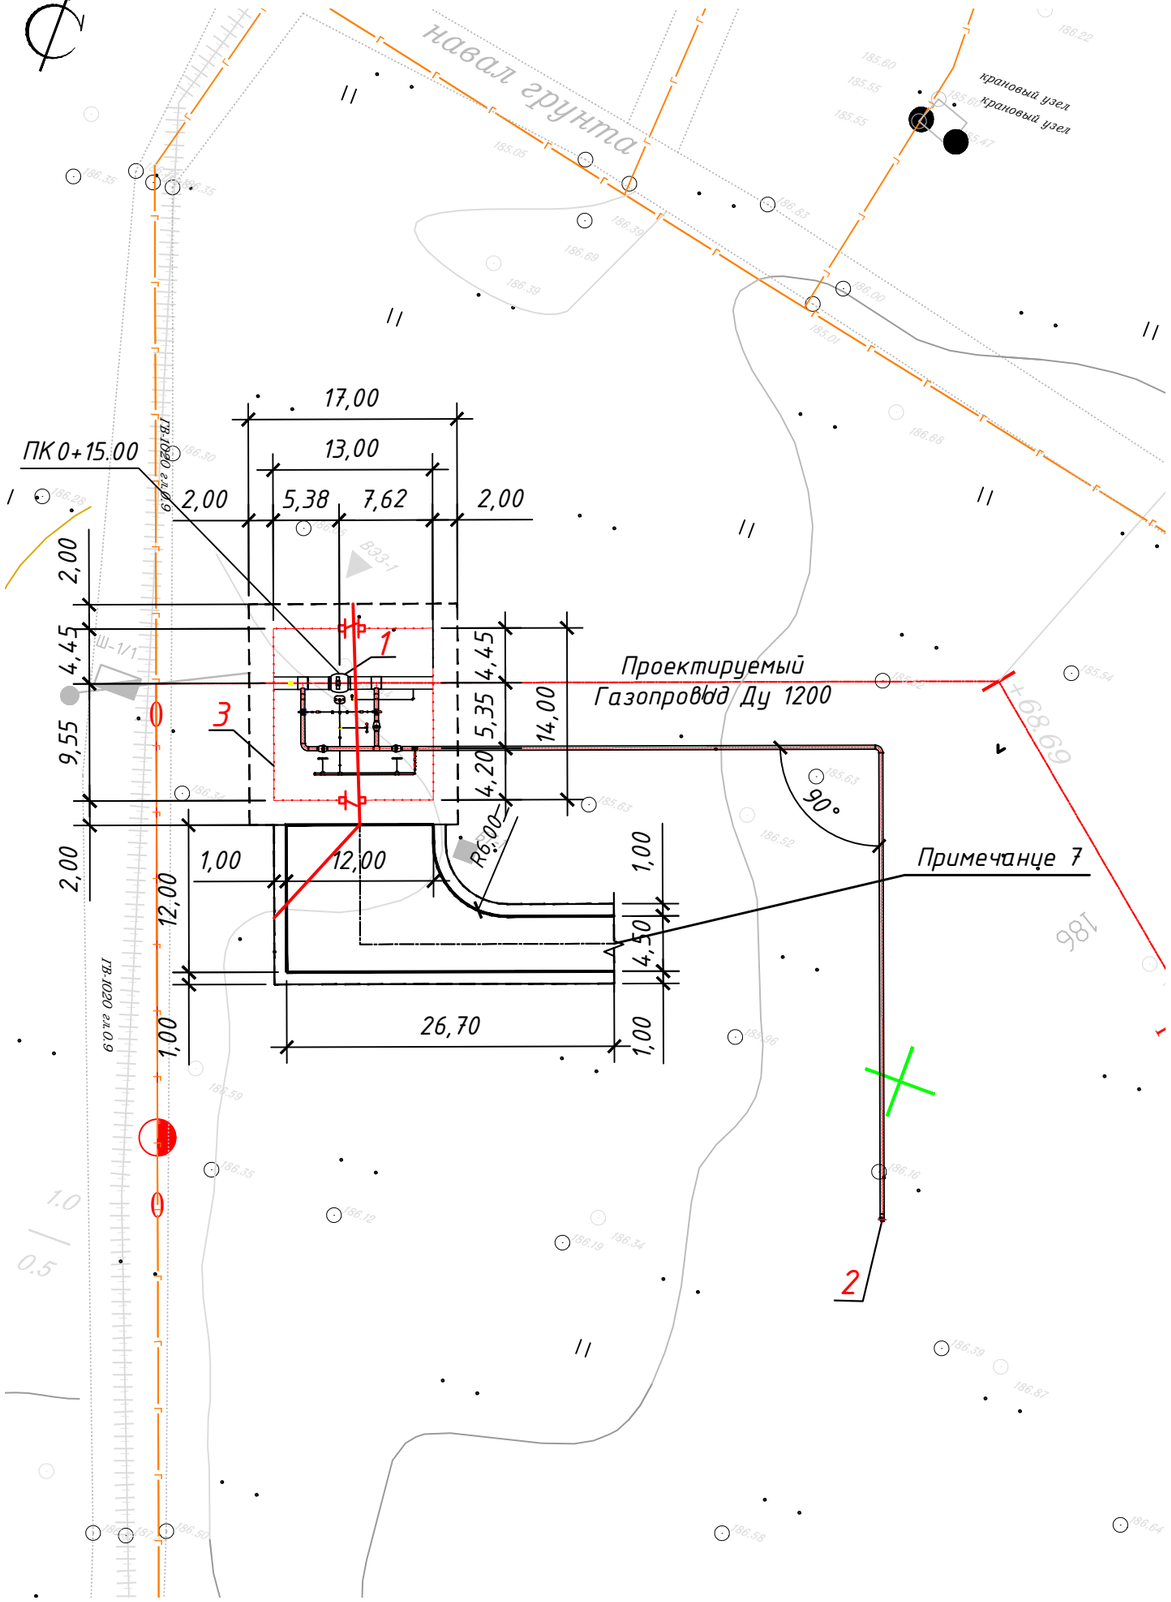

Экспликация зданий и сооружений

Номер на плане	Наименование	Примечание
1	Крановый узел Ду 1200	
2	Продувочная свеча	
3	Ограждение типа "Махаон"	

Условные обозначения

- Ограждение
- Калитка
- Граница планировки
- Существующий газопровод
- Проектируемый газопровод ДУ-1200


Примечание:

При составлении настоящего чертежа были использованы :
1. Материалы топографо-геодезической съемки, предоставлены "О"ZGASHKLITI"DUK.
2. Система координат СК 42. Высотные отметки даны в Балтийской системе.
3. Размеры даны в метрах.
4. Площадка кранового узла привязана линейно к пикету ПК 0+15.00.
5. Данный лист смотри совместно с листами ELE, INF, OPN.

Изм.	Кол.уч	Лист	N°док.	Подп.	Дата				
ГИП						Крановый узел. Генеральный план и транспорт.	Стадия	Лист	Листов
Нач.отд.							РП	1	1
Исполн.									
Проверил						Разбивочный план. М 1:500			
Н. контр.									

Взам. инв. N | Подпись и дата | Инв. N подл.

Формат А3

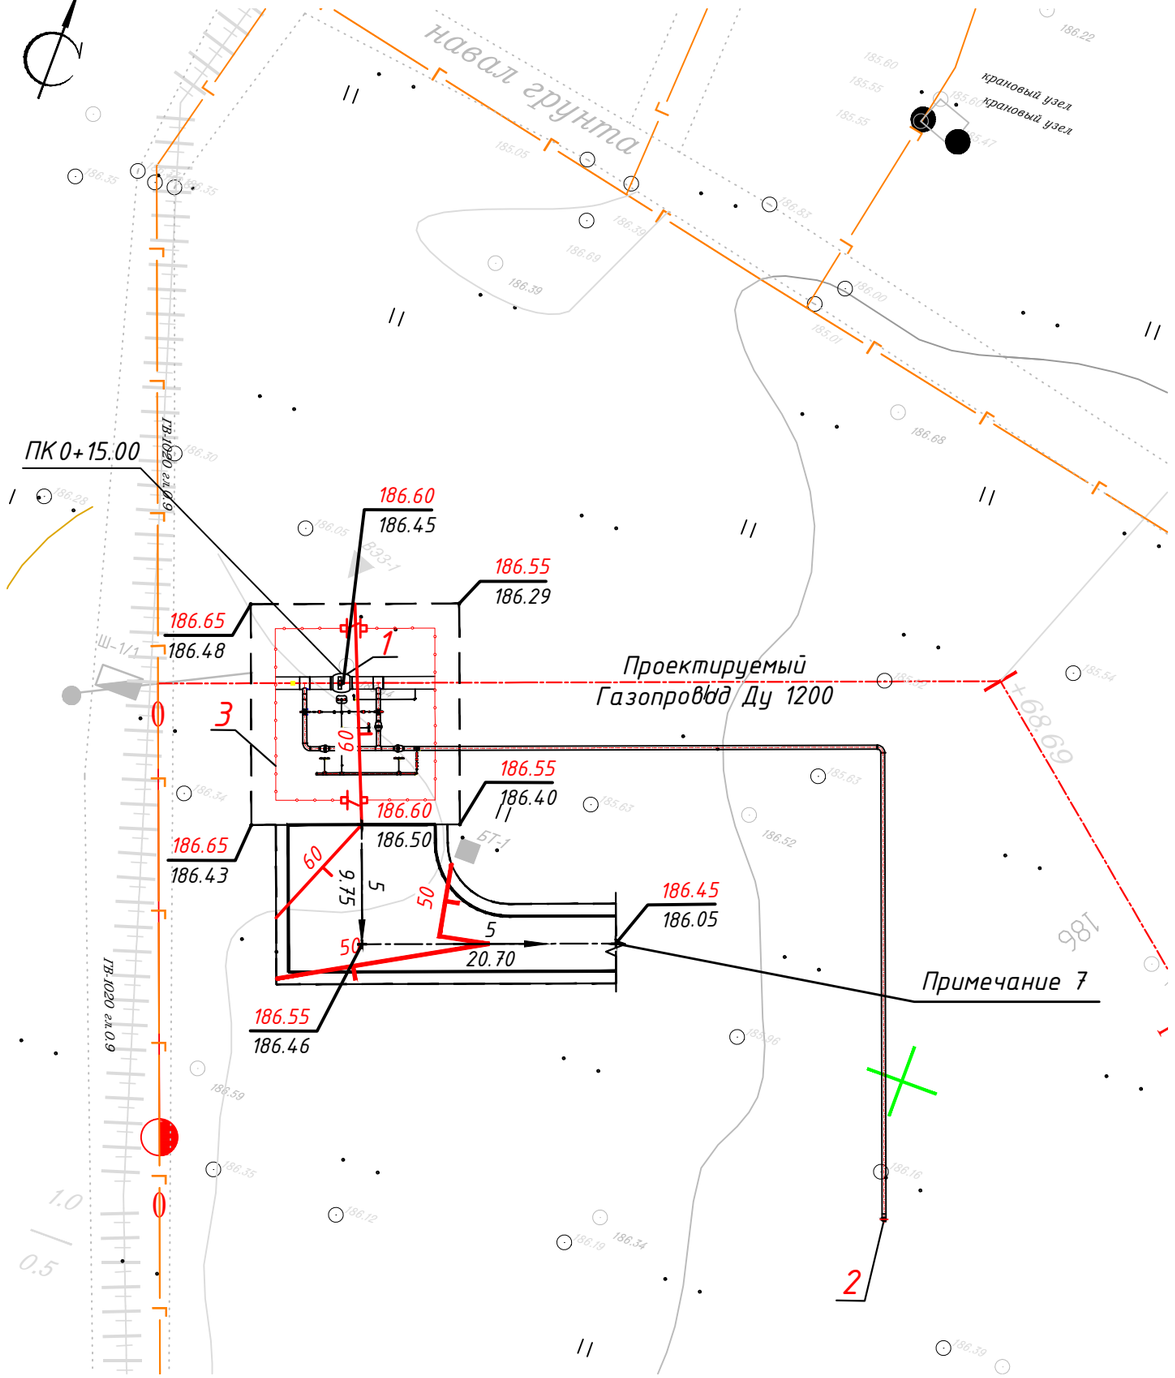

Экспликация зданий и сооружений

Номер на плане	Наименование	Примечание
1	Крановый узел Ду 1200	
2	Продувочная свеча	
3	Ограждение типа "Махаон"	

Условные обозначения

- Ограждение
- Калитка
- Граница планировки
- Существующий газопровод
- Проектируемый газопровод ДУ-1200
- 186.45 / 186.05 — Проектная отметка / Существующая отметка
- 60 — Проектные красные горизонтали

Примечание:


При составлении настоящего чертежа были использованы :

1. Материалы топографо-геодезической съемки, предоставлены "О"ZGASHKLITI"DUK.
2. Система координат СК 42. Высотные отметки даны в Балтийской системе.
3. Размеры даны в метрах.
4. Площадка кранового узла привязана линейно к пикету ПК 0+15.00.
5. Данный лист смотрите совместно с листами ELE, INF, OPN.

Изм.	Кол.уч	Лист	N°док.	Подп.	Дата				
ГИП						Крановый узел. Генеральный план и транспорт.	Стадия	Лист	Листов
Нач.отд.							РП	1	1
Исполн.						План организации рельефа. М1:500			
Проверил									
Н. контр.									

Взам. инв. N | Подпись и дата | Инв. N подл.

Формат А3

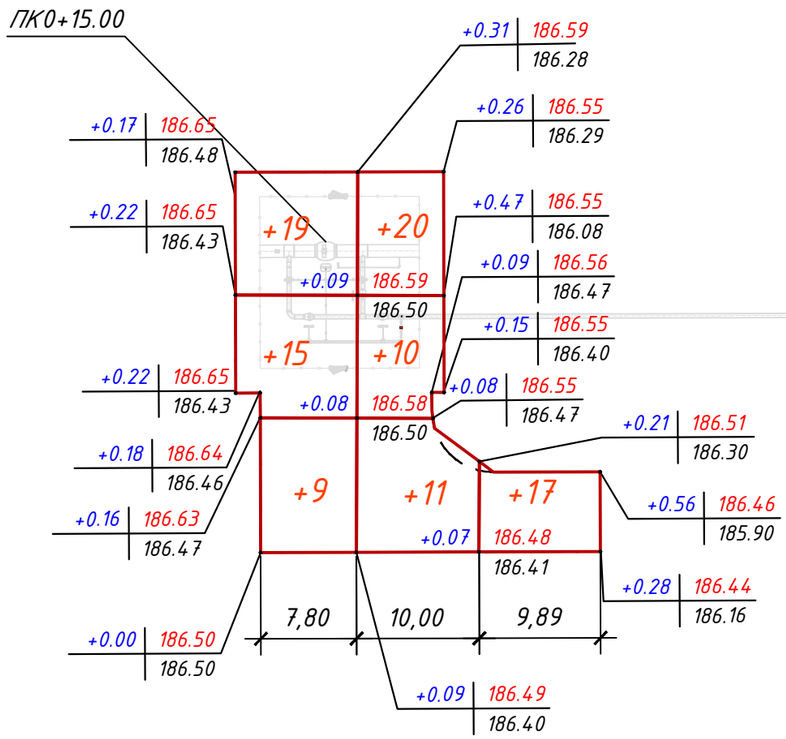

Итого,м3					Всего,м3	
	Насыпь (+)	+43	+41	+17		+101
	Выемка (-)	--	--	--		--

Общая площадь насыпи = 586 м2

Общая площадь выемки = 0 м2

Общая площадь 0-области = 1 м2

Общая площадь картограммы = 587 м2

Условные обозначения:

+10 — объем насыпи в м³

+0.09 | 186.49 / 186.40 — рабочая отм. | проектная отм. / отм.сущ.рельефа

Примечание:

При составлении настоящего чертежа были использованы :

1. Сетка картограммы привязана линейно к пикету ПК 0+15.00.
2. Сетка квадратов объёмы земляных масс разбита на ячейки размерами 10х10м.
3. Производство земляных работ вести в соответствии с требованиями ШНК 3.02.01-19.

Ведомость объемов земляных масс

Наименование грунта	Количество, м³		Примечание
	Насыпь (+)	Выемка (-)	
1. Грунт планировки территории	101	0	
2. Вытесненный грунт, в т.ч. при устройстве:			
а) автодорожных покрытий		83.1	
б) покрытий площадок		24.6	
в) плодородной почвы на участках насыпи		176	Для информации
г) плодородной почвы на участках выемки			
3. Замена растительного грунта на участках насыпи	176		
4. Поправка на уплотнение	27.7		
Всего пригодного грунта	304.7	107.7	
5. Недостаток пригодного грунта		197**	
6. Плодородный грунт, всего в т.ч.:		176	
а) Используемый для озеленения территории			
б) Избыток плодородного грунта	176		
(рекультивация земель)			
7. Итого перерабатываемого грунта	480.7	480.7	


* С учетом плодородного грунта.

** В карьере.

Изм.	Кол.уч.	Лист	N°док.	Подп.	Дата				
ГИП						Крановый узел. Генеральный план и транспорт.	Стадия	Лист	Листов
Нач.отд.							РП	1	1
Исполн.									
Проверил						План земляных масс. М1:500			
Н. контр.									

Взам. инв. N | Подпись и дата | Инв. N подл.

Формат А3

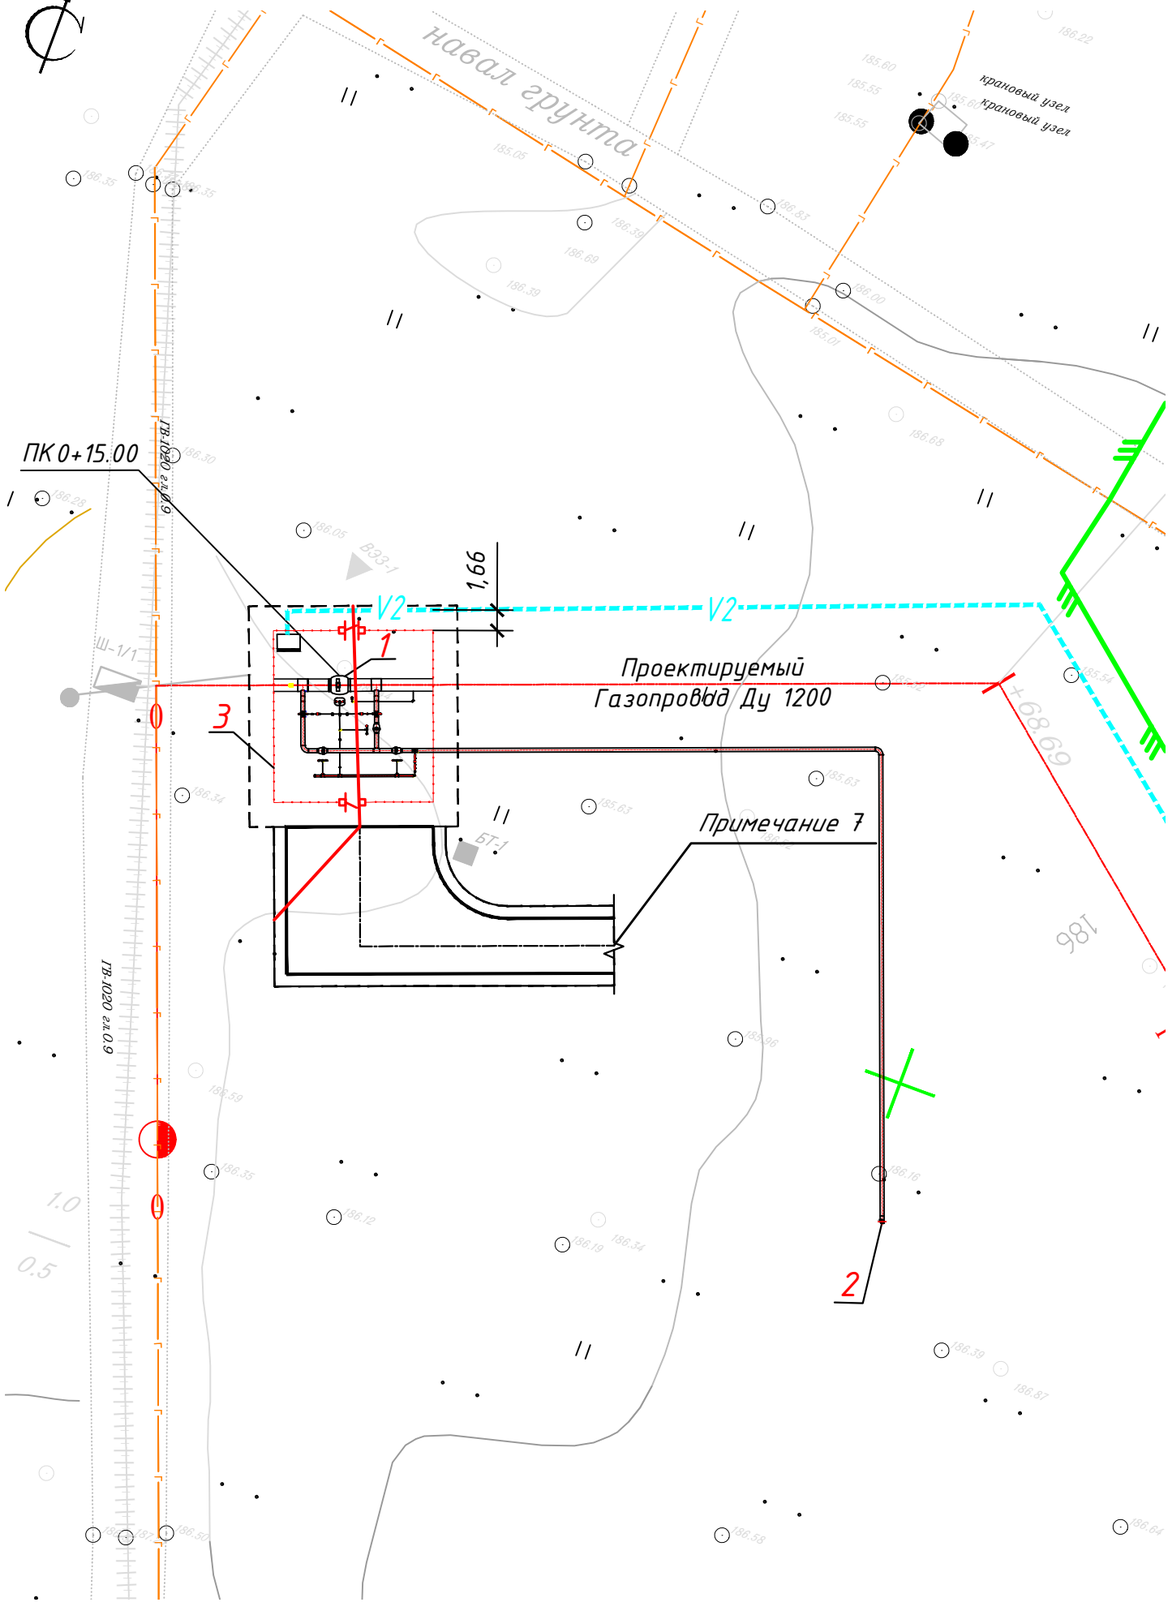

Экспликация зданий и сооружений

Номер на плане	Наименование	Примечание
1	Крановый узел Ду 1200	
2	Продувочная свеча	
3	Ограждение типа "Махаон"	

Условные обозначения

- Существующий газопровод
- Проектируемый газопровод ДУ-1200
- Линия ВОЛС
- Шкаф управления автоматики
- V2 — Сети автоматики (КИПиА)


Примечание:

1. Генеральный план разработан по материалам инженерно-геодезических изысканий выполненный "O'ZGASHKLITI"DUK.
2. Расстояние по горизонтали (в свету) от подземных инженерных сетей до зданий и сооружений следует принимать не менее указанных в табл.9 см. ШНК 2.09.17-21 "Проектирование генеральных планов промышленных предприятий".
3. Расстояние по горизонтали (в свету) между инженерными подземными сетями при их параллельном размещении следует принимать не менее указанных в табл.10 см. ШНК 2.09.17-21.
4. Расположение оборудования и прокладку кабелей уточнить по месту при монтаже.
5. Данный лист смотри совместно с листами разделов PPL, OPN, ELE, SST.


Изм.	Кол.уч.	Лист	N°док.	Подп.	Дата			
ГИП						Крановый узел. Генеральный план и транспорт.	Стадия: РП	Лист: 1 / Листов: 1
Нач.отд.								
Исполн.								
Проверил						Сводный план инженерных сетей. М 1:500		
Н. контр.								

Взам. инв. N | Подпись и дата | Инв. N подл.


Формат А3

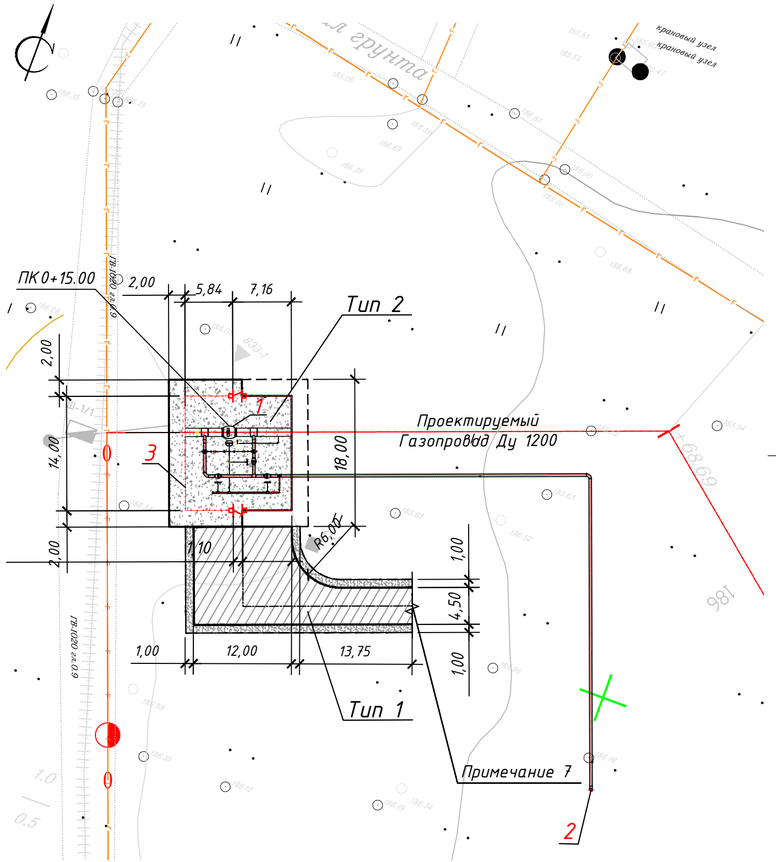

Тип 1

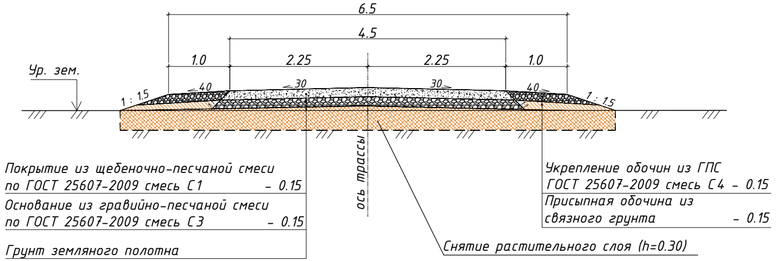

Тип 2

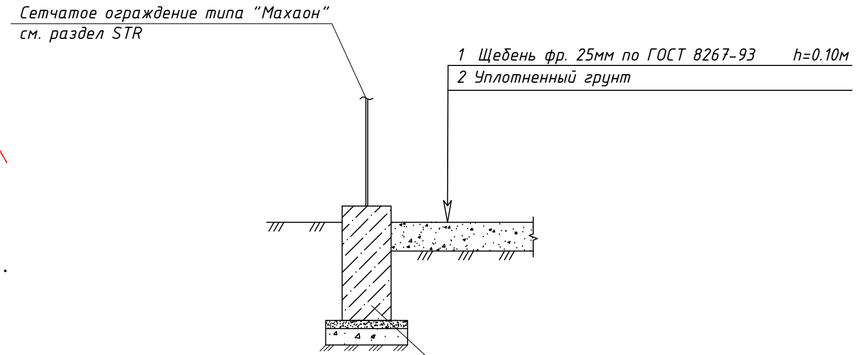

Экспликация зданий и сооружений

Номер на плане	Наименование	Примечание
1	Крановый узел Ду 1200	
2	Продувочная свеча	
3	Ограждение типа "Махаон"	

Ведомость тротуаров, дорожек и площадок

Тип	Обозначение	Наименование	Ед. изм.	Примечание
		Покрытие площадки		
1		Покрытие из щебня по ГОСТ 8267-93, h=0.10	м²	246
		Покрытие проездов		
2		Покрытие из щебеночно-песчаной смеси по ГОСТ 25607-2009 смесь С1 h=0,15м Основание из гравийно-песчаной смеси по ГОСТ 25607-2009 смесь С3 h=0,15м	м²	218.0
		Укрепление обочин из ГПС ГОСТ 25607-2009 смесь С4 h=0,15м	м²	59.0

Условные обозначения

- Ограждение
- Калитка
- Граница планировки
- Существующий газопровод
- Проектируемый газопровод ДУ-1200

Примечание:

При составлении настоящего чертежа были использованы :
1. Материалы топографо-геодезической съемки, предоставлены "О"ZGASHKLITI"DUK.
2. Система координат СК 42. Высотные отметки даны в Балтийской системе.
3. Размеры даны в метрах.
4. Площадка кранового узла привязана линейно к пикету ПК ПК 0+15.00.
5. Данный лист смотри совместно с листами ELE, INF, OPN.
6. Информация по указанию подготовки основания и применяемым грунтам см. раздел STR.
7. Выполнить примыкание к ближайшей дороге по месту.

Изм.	Кол.уч.	Лист	N°док.	Подп.	Дата			
ГИП						Крановый узел. Генеральный план и транспорт.	Стадия	Лист	Листов
Нач.отд.							РП	1	1
Исполн.									
Проверил						План благоустройства территории М1:500			
Н. контр.									

Взам. инв. N | Подпись и дата | Инв. N подл.

Формат А4х3

Позиция	Наименование работ	Единица измерения	Количество	Примечание
	Вертикальная планировка: Насыпь/Выемка	$м^3/м^3$	101/-	
	Земляные работы			
1	Снятие растительного грунта мощностью 0,3 м бульдозером 132 Квт (180 л.с) с погрузкой экскаватором на автосамосвалы 25 т. Вывоз до 5 км.	$м^3$	176	
2	Разработка грунта 1 группы в карьере экскаватором с погрузкой на автосамосвалы с транспортировкой в насыпь, расстояние до 5 км. (привоз).	$м^3$	197	С учетом грунта на уплотнение
3	Устройство корыта под дорожное покрытие (h=0.3 м)	$м^3$	83.1	
4	Устройство корыта под щебеночное покрытие (h=0.1 м)	$м^3$	24.6	
5	Разравнивание и послойное уплотнение насыпи самоходными катками на пневмоколесном ходу массой до 25 т за 8 проходов при толщине слоя до 0.25 м по одному следу с поливкой водой.	$м^3$	197	

Взамен инв.№

Подпись и дата

Инв.№ подл.

Изм.	Кол.уч	Лист	N°док.	Подп.	Дата

ГИП		Крановый узел. Генеральный план и транспорт.	Стадия: РП; Лист: 1; Листов: 2
Нач.отд.			
Исполн.			
Проверил		Ведомость объемов работ.	
Н. контр.			

Формат А4

Позиция	Наименование работ	Единица измерения	Количество	Примечание
	Устройство дорожной одежды	$м^2/м^2$	218 / 59	59-обочина
6	Покрытия из щебеночно-песчаной смеси С1 с К.упл.=1.1 по ГОСТ 25607-2009	$м^3$	36.0	(h=0.15м)
7	Основания из гравийно-песчаной смеси С3 с К.упл.=1.2 по ГОСТ 25607-2009 смесь	$м^3$	39.2	(h=0.15м)
8	Укрепление обочин из ГПС смесь С4 с К.упл.=1.2 по ГОСТ 25607-2009	$м^3$	10.62	(h=0.15м)
9	Присыпная обочина из связного грунта, с К.упл.=1.1	$м^3$	9.74	(h=0.15м)
	Уплотненный грунт К=0.95			
	Щебёночное покрытие площадки	$м^2$	246	
10	Покрытие из щебня по ГОСТ 8267-93	$м^3$	24.6	(h=0.10м)
	Уплотненный грунт К=0.95			

Взамен инв.№

Подпись и дата

Инв.№ подл.

Изм.	Кол.	Лист	№док.	Подпись	Дата

Ведомость рабочих чертежей основного комплекта

Лист	Наименование	Примечание
1	Общие данные	
	XXXX-XX-XXX-XXX-XXX-XXX-XX	
2	Разбивочный план М 1:500	
	XXXX-XX-XXX-XXX-XXX-XXX-XX	
3	План организации рельефа М 1:500	
	XXXX-XX-XXX-XXX-XXX-XXX-XX	
4	План земляных масс М 1:500	
	XXXX-XX-XXX-XXX-XXX-XXX-XX	
5	Сводный план инженерных сетей М 1:500	
	XXXX-XX-XXX-XXX-XXX-XXX-XX	
6	План благоустройства территории М 1:500	
	XXXX-XX-XXX-XXX-XXX-XXX-XX	
7	Ведомость объемов работ	3 листа
	XXXX-XX-XXX-XXX-XXX-XXX-XX	

Ведомость основных комплектов рабочих чертежей

Обозначение	Наименование	Примечание
XXXX-XX-XXX-PLT	Генеральный план и транспорт	
XXXX-XX-XXX-PPL	Линейная часть	
XXXX-XX-XXX-OPN	Технологическая часть	
XXXX-XX-XXX-ELE	Электротехническая часть	
XXXX-XX-XXX-SST	Строительная часть	
XXXX-XX-XXX-INF	ВОЛС	
XXXX-XX-XXX-SYS	Автоматизация технологии и производства	

Ведомость ссылочных и прилагаемых документов

Обозначение	Наименование	Примечание
ШНК 2.09.17-21	Проектирование генеральных планов промышленных предприятий	
ШНК 2.05.02-23	Автомобильные дороги	
СП-37.13330.2012	Промышленный транспорт	
МСН 2.03-02-2002	Инженерная защита территории зданий и	
	сооружений от опасных геологических процессов	
КМК 2.07.03-97	Ограждение территорий предприятий, зданий	
	и сооружений	
КМК 2.05.06-97	Магистральные трубопроводы	
ОНТП 51-1-85	Общесоюзные нормы технологического	
	проектирования. Магистральные трубопроводы	
	Часть 1. Газопровод	

Общие указания

Генеральный план разработан на основании задания ГИПа и плана, выданного заказчиком.

Компоновка сооружений генплана решена с учетом положения существующих автодорог во взаимосвязи с технологическими процессами, а также с учетом зонального размещения объектов по назначению. Во избежание аварий до начала производства земляных работ необходимо определить фактическое положение подземных инженерных сетей и принять меры, по их защите.

Рабочие чертежи разработаны в соотвествии с действующими нормами, правилами и стандартами.

Взам. инв.№


Подпись и дата

Инв. №подл.

Изм.	Кол.уч	Лист	№док	Подп.	Дата	
ГИП						Площадка УЗОУ Генеральный план и транспорт
Нач.отд.						
Исполн.						
						Общие данные
Н.контр.						

Стадия	Лист	Листов
РП	1	1

Формат А3

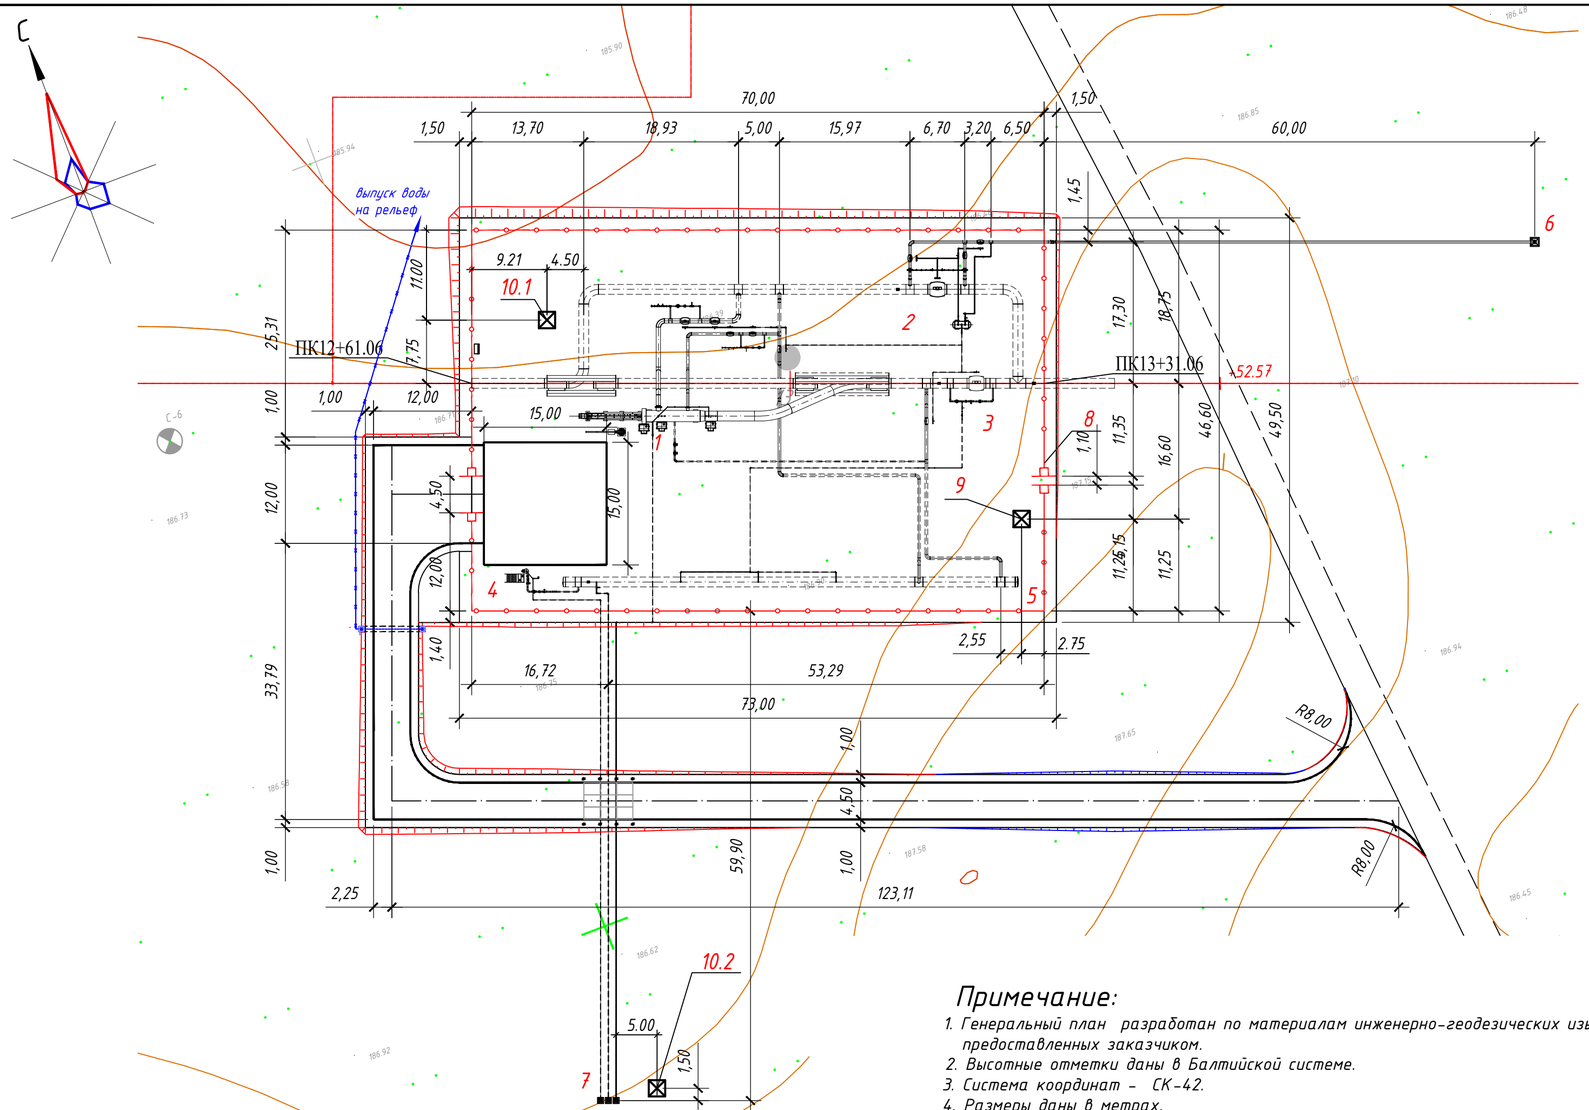

Экспликация зданий и сооружений

Номер на плане	Наименование	Примечание
1	Камера запуска/приема	
2	Крановый узел	
3	Крановый узел	
4	Разделитель	
5	Конденсатосборник	
6	Продувочная свеча	
7	Вытяжные свечи	
8	Сетчатое ограждение с воротами шир.4.5 м	
9	Прожекторная мачта ПМЖ-22.8 (серия 3.407.9-172)	
10.1,10.2	Молниеотвод МЖ-30.6 (серия 3.407.9-172)	

Условные обозначения

- Проектные автодороги, подъезды
- Проектируемые ворота распашные
- Проектируемое ограждение
- Проектируемый газопровод
- Ирригационный лоток ЛИ-5
- Проектный откос


Примечание:

1. Генеральный план разработан по материалам инженерно-геодезических изысканий предоставленных заказчиком.
2. Высотные отметки даны в Балтийской системе.
3. Система координат - СК-42.
4. Размеры даны в метрах.
5. Площадка УЗОУ привязана линейно к пикетажу газопровода.
6. Данный лист смотри совместно с листами разделов PPL, OPN, ELE, SST, INF, SYS.

Изм.	Кол.уч.	Лист	№док.	Подп.	Дата			
ГИП						Площадка УЗОУ Генеральный план и транспорт	Стадия	Лист	Листов
Нач.отдела							РП	1	1
Исполн.									
						Разбивочный план М 1:500			
Н. контр.									

Взам. инв.№ | Подпись и дата | Инв.№подл.

Формат А4х3

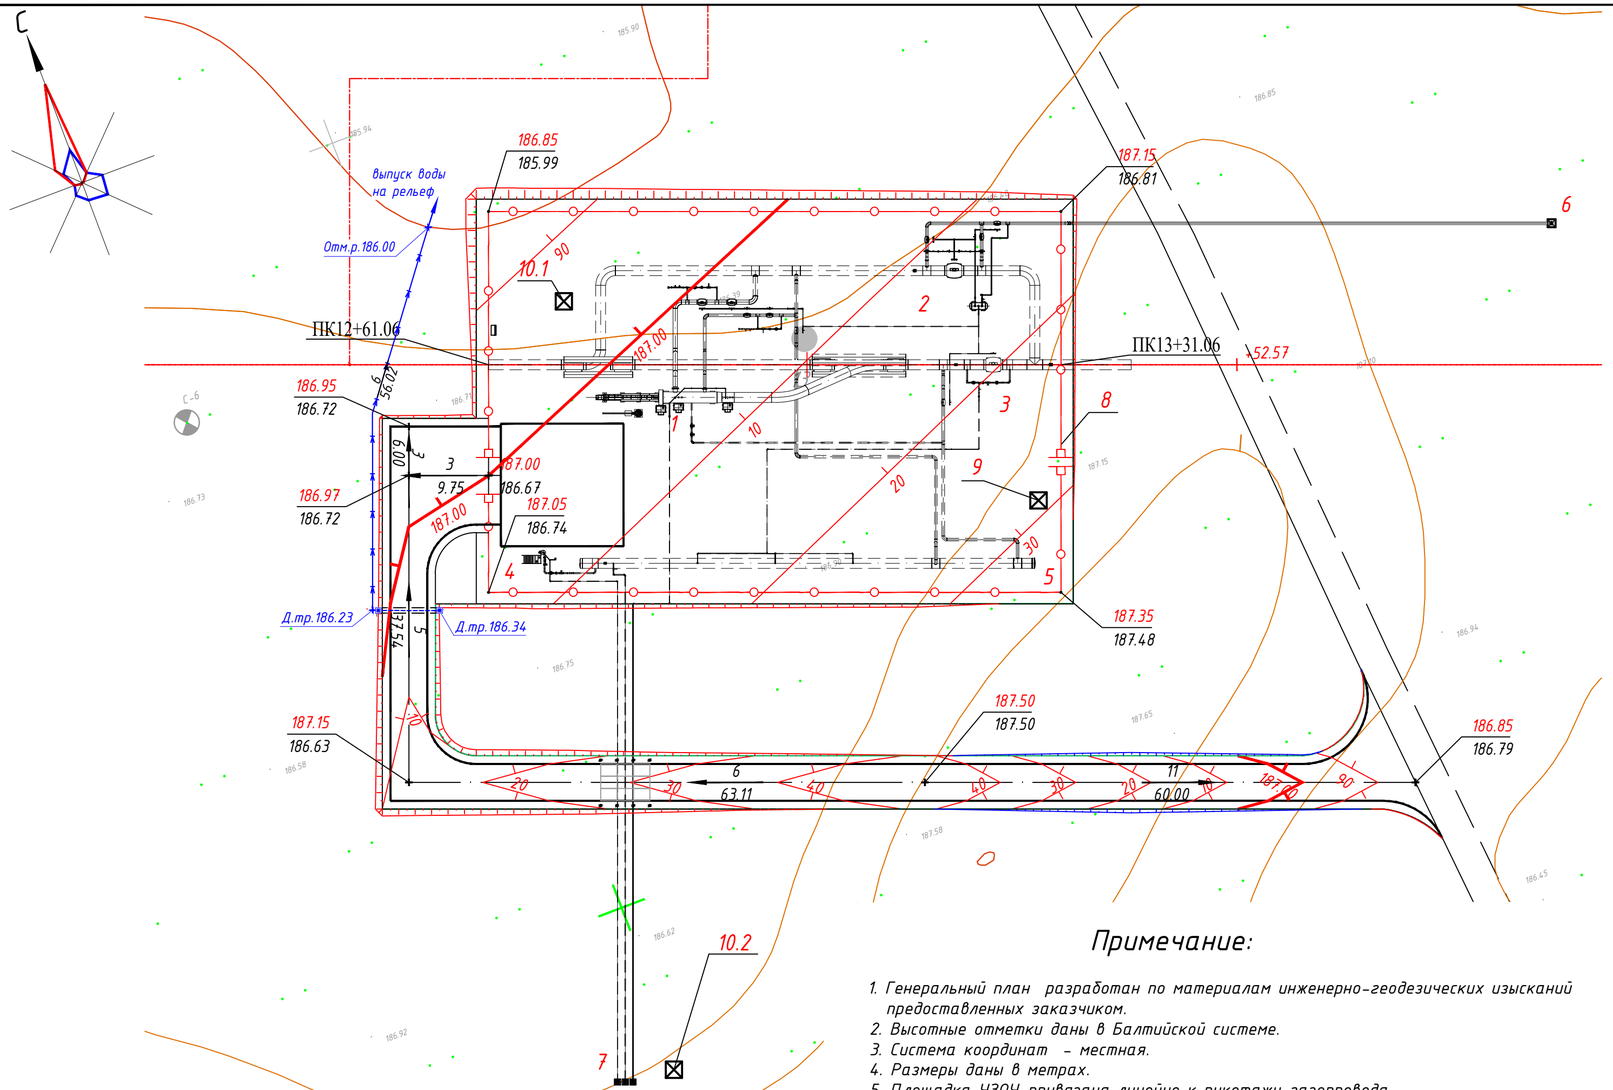

Примечание:

1. Генеральный план разработан по материалам инженерно-геодезических изысканий предоставленных заказчиком.
2. Высотные отметки даны в Балтийской системе.
3. Система координат – местная.
4. Размеры даны в метрах.
5. Площадка УЗОУ привязана линейно к пикетажу газопровода.
6. Планировочные отметки даны по верху покрытия площадок, дорог, земли.
7. Данный лист смотри совместно с листами разделов PPL, OPN, ELE, SST, INF, SYS.

Экспликация зданий и сооружений

Номер на плане	Наименование	Примечание
1	Камера запуска/приема	
2	Крановый узел	
3	Крановый узел	
4	Разделитель	
5	Конденсатосборник	
6	Продувочная свеча	
7	Вытяжные свечи	
8	Сетчатое ограждение с воротами шир.4.5 м	
9	Прожекторная мачта ПМЖ-22.8 (серия 3.407.9-172)	
10.1,10.2	Молниеотвод МЖ-30.6 (серия 3.407.9-172)	


Условные обозначения

	Проектируемые ворота распашные
	Проектируемое ограждение
	Проектируемый газопровод
187.05 / 186.74	Проектная отметка земли / Существующая отметка земли
30	Проектные красные горизонтали
11 / 60.00	Уклон в ‰ / Расстояние в метрах
	Труба, d=0.325м, L=7.3м
	Ирригационный лоток ЛИ-5
Д.тр.186.34	Отметка низа трубы

Изм.	Кол.уч.	Лист	№док.	Подп.	Дата			
ГИП						Площадка УЗОУ Генеральный план и транспорт	Стадия	Лист	Листов
Нач.отдела							РП	1	1
Исполн.									
						План организации рельефа М1:500			
Н. контр.									

Взам. инв.№ | Подпись и дата | Инв. №подл.

Формат А4х3

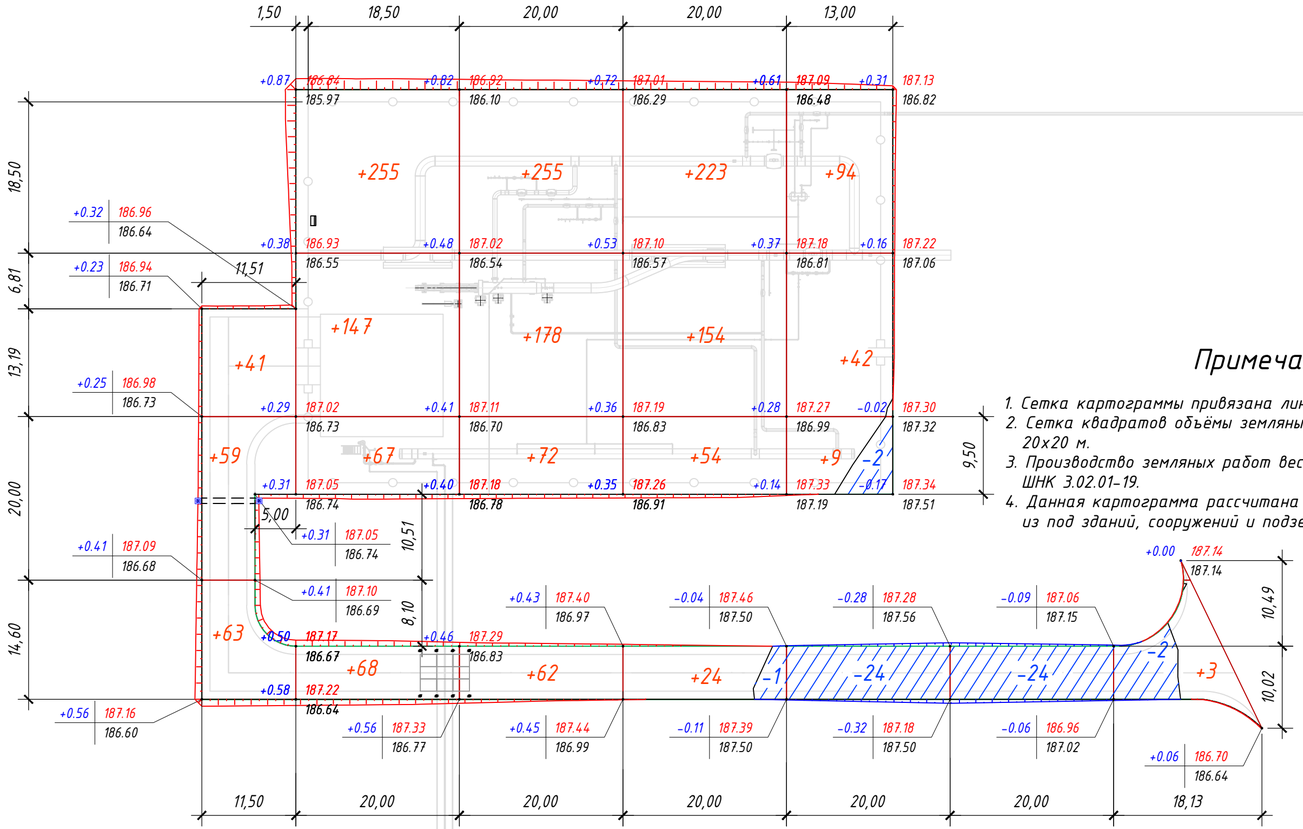

Условные обозначения:

+255 — Объем насыпи в м³

Линия нулевых работ

+0.16 | 187.22 (рабочая отм.) / 187.06 (проектная отм. отм.сущ.рельефа)

Примечание:

1. Сетка картограммы привязана линейно к ограждению площадки.
2. Сетка квадратов объёмы земляных масс разбита на ячейки размерами 20х20 м.
3. Производство земляных работ вести в соответствии с требованиями ШНК 3.02.01-19.
4. Данная картограмма рассчитана без учёта объёмов вытесненного грунта из под зданий, сооружений и подземных инженерных сетей.

Итого,м³	Насыпь (+)	+163	+537	+567	+455	+145	--	+3	Всего,м³ +1870
	Выемка (-)	--	--	--	-1	-26	-24	-2	-53

Общая площадь насыпи = 4487 м2
Общая площадь выемки = 377 м2
Общая площадь 0-области = 2 м2

Общая площадь откосов насыпи = 239 м2
Общая площадь откосов выемки = 24 м2
Общая площадь картограммы = 5129 м2

Ведомость объемов земляных масс

Наименование грунта	Количество, м³				Примечание
	Насыпь (+)	Выемка (-)	Насыпь (+)	Выемка (-)	
1. Грунт планировки территории	1870	53*			
2. Вытесненный грунт, в т.ч. при устройстве:					
а) автодорожных покрытий (покрытий площадки)		802			
б) вытесненный грунт из под устройства лотков		10			
в) плодородной почвы на участках насыпи		1419			для инф.
ж) плодородной почвы на участках выемки		120			
3. Замена растительного грунта					
на участках насыпи	1419				
4. Грунт для устройства откосов насыпи	81				
5. Грунт для устройства откосов выемки		1			
6. Поправка на уплотнение	337				
Всего пригодного грунта	3707	986			
7. Недостаток пригодного грунта		2721**			
8. Плодородный грунт, всего, в т.ч.:		1539			
б) избыток плодородного грунта (рекультивация земель)	1539				
9. Итого перерабатываемого грунта	5246	5246			

* С учетом плодородного грунта.
** В карьере.

Изм.	Кол.уч.	Лист	№док.	Подп.	Дата
ГИП					
Нач.отдела					
Исполн.					
Н. контр.					


Площадка УЗОУ
Генеральный план и транспорт

Стадия	Лист	Листов
РП	1	1

План земляных масс
М 1:500

Взам. инв.№ | Подпись и дата | Инв. №подл.

Формат А4х3

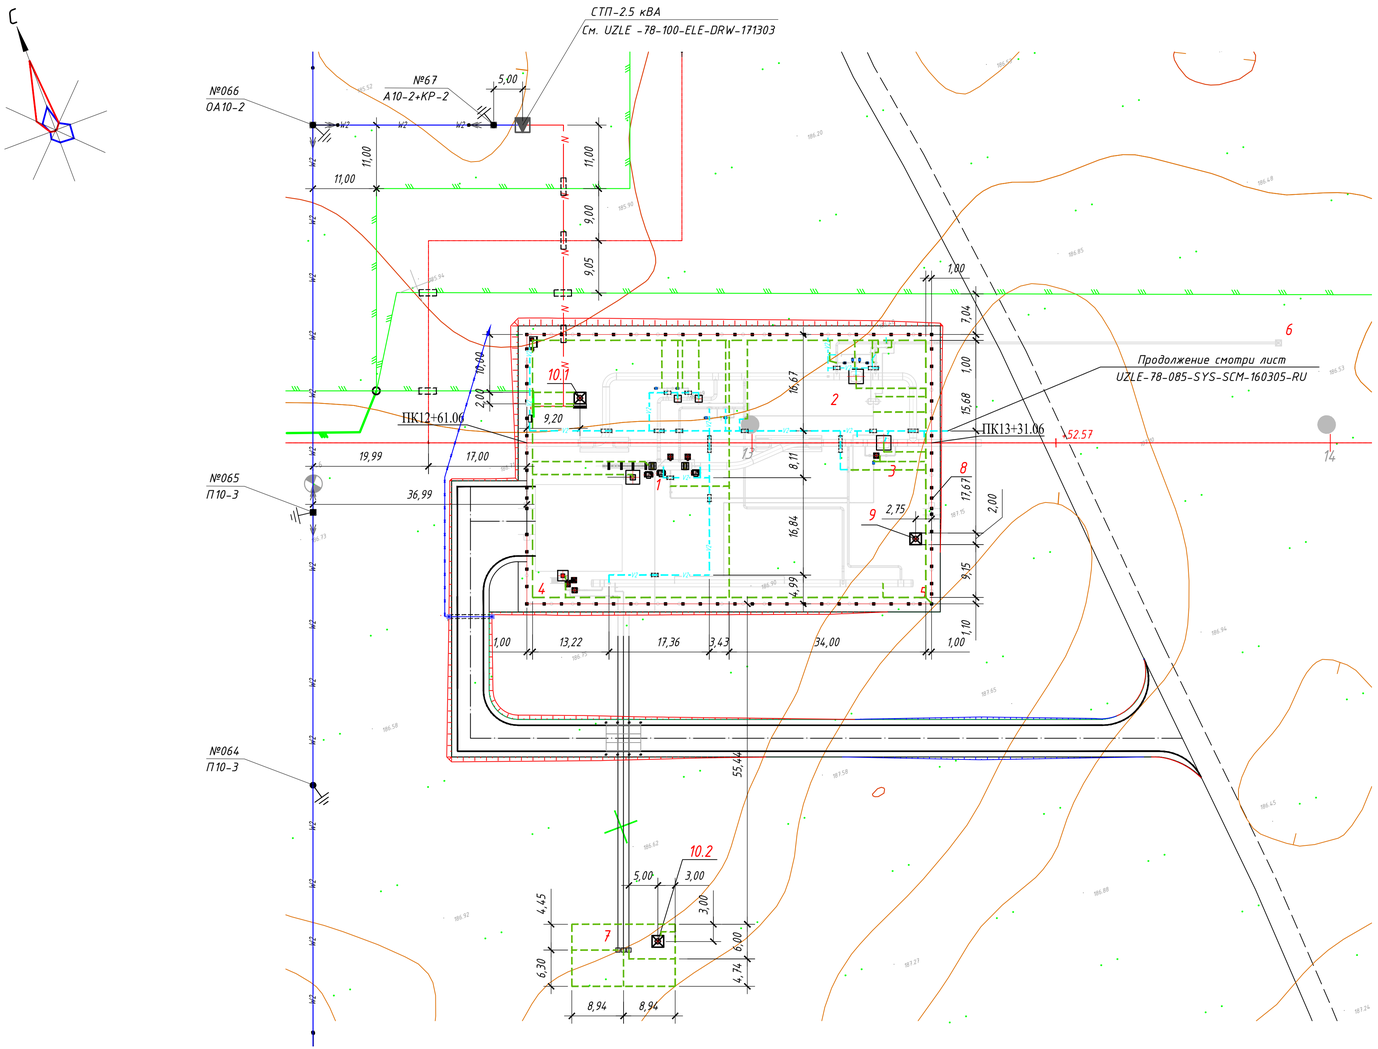

Экспликация зданий и сооружений

Номер на плане	Наименование	Примечание
1	Камера запуска/приема	
2	Крановый узел	
3	Крановый узел	
4	Разделитель	
5	Конденсатосборник	
6	Продувочная свеча	
7	Вытяжные свечи	
8	Сетчатое ограждение с воротами шир.4.5 м	
9	Прожекторная мачта ПМЖ-22.8 (серия 3.407.9-172)	
10.1,10.2	Молниеотвод МЖ-30.6 (серия 3.407.9-172)	

Условные обозначения

- Проектируемое ограждение
- Проектируемый газопровод
- Ирригационный лоток ЛИ-5
- N – Кабель силовой 0,23 кВ в траншее
- N – Кабель силовой 0,23 кВ в ПНД трубе в траншее
- W2 – Проектируемая линия 10 кВ (провод марки АС-95/16)
- Проектируемая опора ВЛ-10 кВ
- СТП столбовая подстанция
- УЗОУ-С-РДВ
- ШТМ-УЗОУ-С шкаф телемеханики
- Горизонтальный заземлитель -полоса стальная сечением 5х40 мм
- Вертикальный заземлитель - круг 16 длиной 3м
- Проектируемый волоконно-оптический кабель связи, прокладываемый в грунте
- Проектируемый волоконно-оптический кабель связи, прокладываемый в БНТ трубе
- Волоконно-оптическая муфта
- V2 – Кабельная трасса КИПиА в траншее
- Кабельная трасса КИПиА в ПНД трубе

Примечание:


1. Генеральный план разработан по материалам инженерно-геодезических изысканий предоставленных заказчиком.
2. Высотные отметки даны в Балтийской системе.
3. Система координат - местная.
4. Расстояние по горизонтали (в свету) от подземных инженерных сетей до зданий и сооружений следует принимать не менее указанных в табл.9 см. ШНК 2.09.17-21 "Проектирование генеральных планов промышленных предприятий".
5. Расстояние по горизонтали (в свету) между инженерными подземными сетями при их параллельном размещении следует принимать не менее указанных в табл.10 см. ШНК 2.09.17-21.
6. Площадка УЗОУ привязана линейно к пикетажу газопровода.
7. Данный лист смотри совместно с листами разделов PPL, OPN, ELE, SST, INF, SYS.

Изм.	Кол.уч.	Лист	№док.	Подп.	Дата			
ГИП						Площадка УЗОУ Генеральный план и транспорт	Стадия	Лист	Листов
Нач.отдела							РП	1	1
Исполн.									
Н. контр.						Сводный план инженерных сетей М 1:500			

Взам. инв.№ | Подпись и дата | Инв. №подл.


Формат А3х3

Тип 1

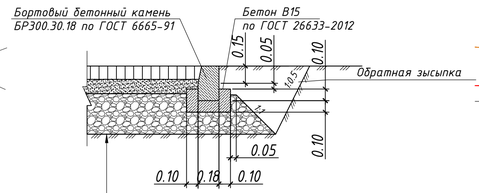


1	Ж/б плита ПДН (6х2х0.14)	h=0.14м
2	Щебень фр. 25мм по ГОСТ 8267-93	h=0.10м
3	ГПС (гравийно-песчанная смесь), С4 ГОСТ 25607-2009	h=0.30м
4	Уплотненный грунт (К=0,98)	

Тип 2

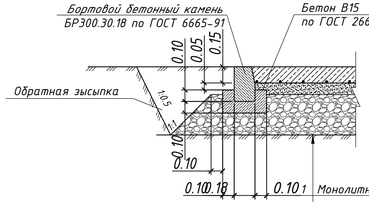

1	Монолитный бетон кл.В30, ГОСТ 26633-2012	h=0.14м
2	Арматура Ф8AIII/Ф8AIII яч. 200х200 мм	
3	Техническая полиэтиленовая пленка 120мкм	
4	Щебень фр. 25мм по ГОСТ 8267-93	h=0.10м
5	ГПС (гравийно-песчанная смесь), С4 ГОСТ 25607-2009	h=0.30м
6	Уплотненный грунт (К=0,98)	


Тип 5

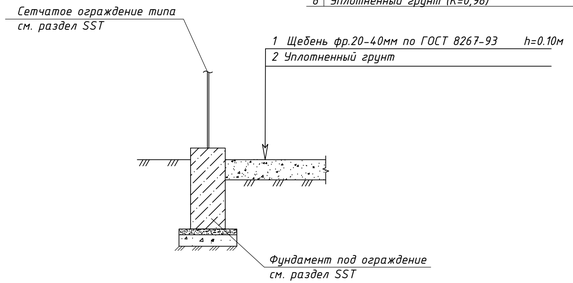


1	Щебень фр.20-40мм по ГОСТ 8267-93	h=0.10м
2	Уплотненный грунт	


Примечание:

1. Генеральный план разработан по материалам инженерно-геодезических изысканий предоставленных заказчиком.
2. Размеры даны в метрах.
3. Бетонные поверхности блоков, соприкасающиеся с землей, и их торцы смазываются горячим битумом за 2 раза.
4. Конструкцию ограждения рассматривать совместно со строительными чертежами

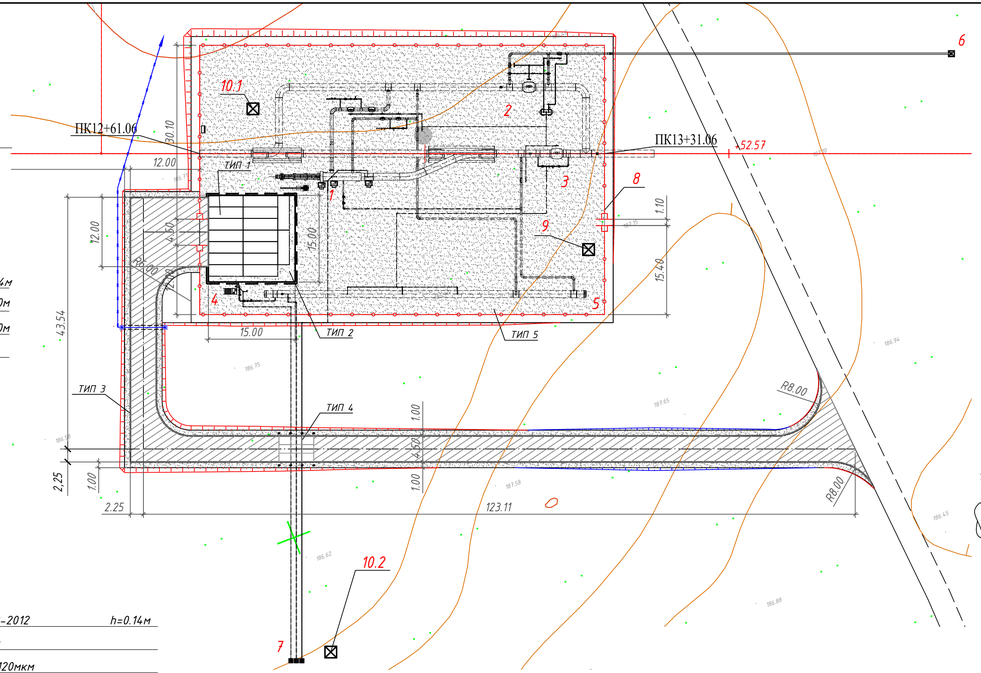

Ж/б монолитный колодец на ливнеотводящей сети размером 0,7х0,7х0,7м

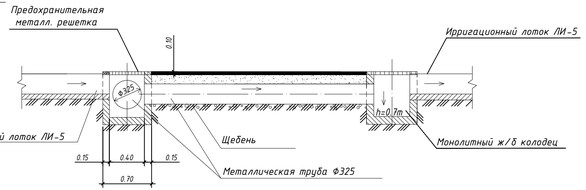

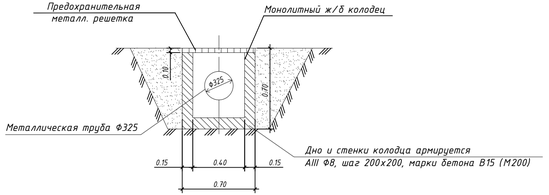


Условные обозначения

- Проектные автодороги, подъезды
- Проектируемые ворота распашные
- Проектируемое ограждение
- Проектируемый газопровод
- Ирригационный лоток ЛИ-5
- Проектный откос


Тип 4

Покрытие из бетонных плит на переезде через газопровод

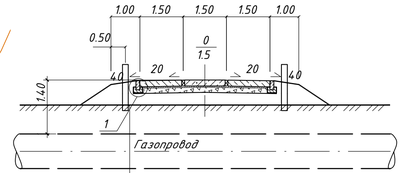

Железобетонные плиты ПД 20.15-17	h=0.21м
Песок по ГОСТ 8736-93	h=0.05м
Щебень или гравий по ГОСТ 8267-93	h=0.18м

Тип 3

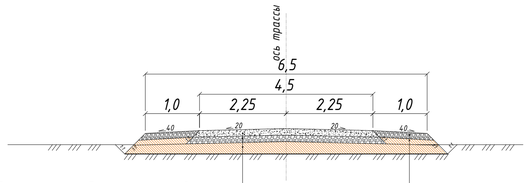

Покрытия из щебеночно-песчаной смеси по ГОСТ 25607-2009 смесь С1 -	0,15
Основания из гравийно-песчаной смеси по ГОСТ 25607-2009 смесь С3 -	0,15
Грунт земляного полотна	

Укрепление обочины из ГПС ГОСТ 25607-2009 смесь С4 -	0,15
Присыпная обочина из связного грунта	-0,15

Ведомость водоотводных сооружений

Вид сооружения	Координата оси или номер сооружения	Координата (пикетаж) Beginning/ Начало	Координата (пикетаж) Ending/ Конца	Длина п/м	Тип укрепления или конструкция	Примечание
	Лоток ЛИ-5			50	Железобетонный	
	Водоприем.колодец				Железобетонный	2шт
	Труба			8	Металлическая	d=0.325 м

Экспликация зданий и сооружений

Номер на плане	Наименование	Примечание
1	Камера запуска/приема	
2	Крановый узел	
3	Крановый узел	
4	Разделитель	
5	Конденсатосборник	
6	Продувочная свеча	
7	Вытяжные свечи	
8	Сетчатое ограждение с воротами шир.4.5 м	
9	Прожекторная мачта ПМЖ-22.8 (серия 3.407.9-172)	
10.1,10.2	Молниеотвод МЖ-30.6 (серия 3.407.9-172)	

Ведомость тротуаров, дорожек и площадок

Поз	Обозначение	Наименование	Тип	Площадь покрытия, м²	Примечание
1		Покрытие из бетонных плит марки ПДН (6х2х0.14)	1	192	16 шт
2		Армированный монолитный бетон кл. В30 по ГОСТ 26633-2012	2	33	
3		Щебеночно-песчаная смесь С1 по ГОСТ 25607-2009 Гравийно-песчаная смесь С3 по ГОСТ 25607-2009 Укрепление обочины из ГПС смесь С4 по ГОСТ 25607-2009	3	888 335	
4		Покрытие из бетонных плит ПД20.15-17 на переезде через газопровод	4	27	9 шт
5		Покрытие свободной площади из щебня по ГОСТ 8267-93	5	3018	
6		Бетонный бордюрный камень БР300.30.18 бетон В30 (М-400) ГОСТ 6665-91*		51	п.м
7	•	Сигнальные столбики			8 шт

Изм.	Кол.уч.	Лист	№док.	Подп.	Дата			
ГИП						Площадка УЗОУ Генеральный план и транспорт	Стадия	Лист	Листов
Нач.отдела							РП	1	1
Исполн.									
						План благоустройства территории М 1:500			
Н. контр.									

Инв. №подл. | Подпись и дата | Взам. инв.№

Формат А3х3

Позиция	Наименование работ	Единица измерения	Количество	Примечание
	Вертикальная планировка: Насыпь/Выемка	$м^3/м^3$	1870/53	
	Земляные работы			
1	Разработка растительного грунта мощностью 0,2 м с погрузкой экскаватором на автосамосвалы 25 т и вывоз до 5 км	$м^3$	1419	
2	Разработка в карьере грунта 1гр. экскаватором с погрузкой на автосамосвалы (привоз) с перемещением в насыпь бульдозером 10 м	$м^3$	2721	
3	Уплотнение насыпи катками массой 25 тонн за 6-8 проходов по одному следу при толщине слоя до 0.20 м с поливкой водой.	$м^3$	2721	
4	Планировка территории площадки после земляных работ: планировка корыта под автодороги -//-//- под площадки	$м^2$	1475 3018	
5	Устройство корыта под дорожную одежду	$м^3$	802	
6	Планировка откосов механизированным способом	$м^2$	263	

Взамен инв.№

Подпись и дата

Инв.№ подл.

Изм.	Кол.уч	Лист	№док	Подп.	Дата

ГИП	Площадка УЗОУ Генеральный план и транспорт	Стадия	Лист	Листов
Нач.отд.		РП	1	3
Исполн.				
Н.контр.	Ведомость объёмов работ			

Формат А4

Позиция	Наименование работ	Единица измерения	Количество	Примечание
	Покрытие разворотной площадки плитами ПДН	$м^2$	192 / 33	33-монолит
7	Ж/б плита ПДН 6/2/0.14	шт	16	(h=0.14м)
8	Щебень фр. 20-40 мм по ГОСТ 8267-93 К.упл.=1,1	$м^3$	19.2	(h=0.10м)
9	ГПС (гравийно-песчанная смесь), С4 ГОСТ 25607-2009 К.упл.=1,2	$м^3$	57.6	(h=0.30м)
10	Бортовой бетонный камень БР300.30.18 по ГОСТ 6665-91	пм	52	
	Подготовка под бордюрный камень, бетон В15 по ГОСТ 26633-2012	$м^3$	3.1	
11	Монолитный бетон кл. В30, ГОСТ 26633-2012	$м^3$	4,6	(h=0.14м)
	Арматура Ф8AIII/Ф8AIII яч. 200х200 мм	кг	130.4	$1м^2$=3.95кг 3.95х33=130.4
12	Техническая полиэтиленовая пленка 120 мкм	$м^2$	35	
13	Щебень фр. 20-40 мм по ГОСТ 8267-93 К.упл.=1,1	$м^3$	3.3	(h=0.10м)
14	ГПС (гравийно-песчанная смесь), С4 ГОСТ 25607-2009 К.упл.=1,2	$м^3$	9.9	(h=0.30м)
	Уплотнённый грунт (К=0,98)			
	Подъездная дорога	$м^2/м^2$	888 / 335	335-обочина
15	Покрытие из ЩПС по ГОСТ 25607-2009 смесь С1 К.упл.=1,1	$м^3$	146.5	(h=0.15м)
16	Основание из ГПС по ГОСТ 25607-2009 смесь С3 К.упл.=1,2	$м^3$	159.8	(h=0.15м)
17	Укрепление обочин из ГПС по ГОСТ 25607-2009 смесь С4 К.упл.=1,2	$м^3$	60.3	(h=0.15м)
18	Присыпная обочина из связного грунта К.упл.=1,1	$м^3$	55.3	(h=0.15м)
	Уплотнённый грунт (К=0,98)			
	Устройство переезда через газопровод ж/б плитами	$м^2$	27 / 9	9-монолит
19	Ж/б плита ПД 20.15-17	шт/$м^3$	9/27	(h=0.21м)
20	Устройство выравнивающего слоя из песка по ГОСТ 8736-93 К.упл.=1.1	$м^3$	1.35	(h=0.05м)
21	Устройство основания из щедня или (гравия)по ГОСТ 8267-93 Купл.=1.1	$м^3$	4.86	(h=0.18м)
22	Омоноличивание стыков цементным раствором	$м^3$	0.61	

Взамен инв.№

Подпись и дата

Инв.№ подл.

Изм.	Кол.уч.	Лист	№док.	Подп.	Дата

Формат А4

Позиция	Наименование работ	Единица измерения	Количество	Примечание
23	Установка сигнальных столбиков	шт	8	
	– бетон класса В 30	$м^3$	0.32	
	– арматура класса AI	т	0.023	
	Ирригация			
24	ж/б лоток ли-5	пм. шт	50/ 5	
	Подготовка под ж/б лоток из щебня по ГОСТ 8267-93	$м^3$	3.0	0.6x0.1x50= 3.0 (h=0.10м)
25	Металлическая труба d=0.325м	пм.	10	
	Подготовка под металл. трубу из щебня по ГОСТ 8267-93	$м^3$	0.44	0.55x0.1x8.0= 0.44(h=0.10м)
	Гидроизоляция стальных труб обмазочным битумом	кг	20.4	1.02x8.0=8.16$м^2$ ($1м^2$=2кг)
	Железобетонный монолитный колодец (Спецификация элементов на 1 шт.)	шт	2	
26	Арматура Ф8AIII, ячейка 200x200 мм L=2430мм	шт	8	1шт.=0.96kg/кг 8x0.96=7.7rg/кг
27	Арматура Ф8AIII, ячейка 200x200 мм L=830мм	шт	18	1шт.=0.33kg/кг 18x0.33=5.9rg/кг
28	Бетон класса В15 (М200)	$м^3$	0.3	
29	Гравийно-песчаная смесь	$м^3$	0.1	
	Щебёночное покрытие площадки	$м^2$	3018	
30	Покрытие из щебня по ГОСТ 8267-93	$м^3$	301.8	(h=0.10м)
	Уплотнённый грунт (К=0,95)			

Взамен инв.№

Подпись и дата

Инв.№ подл.

Изм.	Кол.уч.	Лист	№док.	Подп.	Дата	UZLE-78-010-PLT-SCH-140107-RU-A2	Лист 3

Формат А4

Ведомость рабочих чертежей основного комплекта

Лист	Наименование	Примечание
1	XXXX-XX-XXX-XXX-XXX-XXX-XX	
	Общие данные	
2	XXXX-XX-XXX-XXX-XXX-XXX-XX	
	Разбивочный план. М 1:500	
3	XXXX-XX-XXX-XXX-XXX-XXX-XX	
	План организации рельефа. М 1:500	
4	XXXX-XX-XXX-XXX-XXX-XXX-XX	
	План земляных масс. М 1:500	
5	XXXX-XX-XXX-XXX-XXX-XXX-XX	
	Сводный план инженерных сетей. М 1:500	
6	XXXX-XX-XXX-XXX-XXX-XXX-XX	
	План благоустройства территории. М 1:500	
7	XXXX-XX-XXX-XXX-XXX-XXX-XX	
	Ведомость объемов работ	

Ведомость основных комплектов рабочих чертежей

Обозначение	Наименование	Примечание
XXXX-XX-XXX-PLT	Генеральный план и транспорт	
XXXX-XX-XXX-PPL	Линейная часть	
XXXX-XX-XXX-OPN	Технологическая часть	
XXXX-XX-XXX-ELE	Электротехническая часть	
XXXX-XX-XXX-SST	Строительная часть	

Ведомость ссылочных и прилагаемых документов

Обозначение	Наименование	Примечание
ШНК 2.09.17-21	Проектирование генеральных планов промышленных предприятий	
ШНК 2.05.02-23	Автомобильные дороги	
СП-37.13330.2012	Промышленный транспорт	
МСН 2.03-02-2002	Инженерная защита территории зданий и	
	сооружений от опасных геологических процессов	
КМК 2.07.03-97	Ограждение территорий предприятий, зданий	
	и сооружений	
КМК 2.05.06-97	Магистральные трубопроводы	
ОНТП 51-1-85	Общесоюзные нормы технологического	
	проектирования. Магистральные трубопроводы	
	Часть 1. Газопровод	

Общие указания:

ГенеральныЙ план разработан на основании задания ГИПа и плана, выданного заказчиком.

Основой для разработки рабочей документации послужила материалы инженерных изысканий предоставленные заказчиком.

Компоновка сооружений генплана решена с учетом положения существующих автодорог во взаимосвязи с технологическими процессами, а также с учетом зонального размещения объектов по назначению. Во избежание аварий до начала производства земляных работ необходимо определить фактическое положение подземных инженерных сетей и принять меры, по их защите.

Рабочие чертежи разработаны в соотвествии с действующими нормами, правилами и стандартами.


Взаим.инв.N

Подпись и дата

Инв.N подл.

Изм.	Кол.уч	Лист	№док	Подп.	Дата			
ГИП						Площадка УЗРГ Генеральный план и транспорт	Стадия: РП	Лист: 1 / Листов: 1
Нач.отд.								
Исполн.						Общие данные		
Н.контр.								

Формат А3

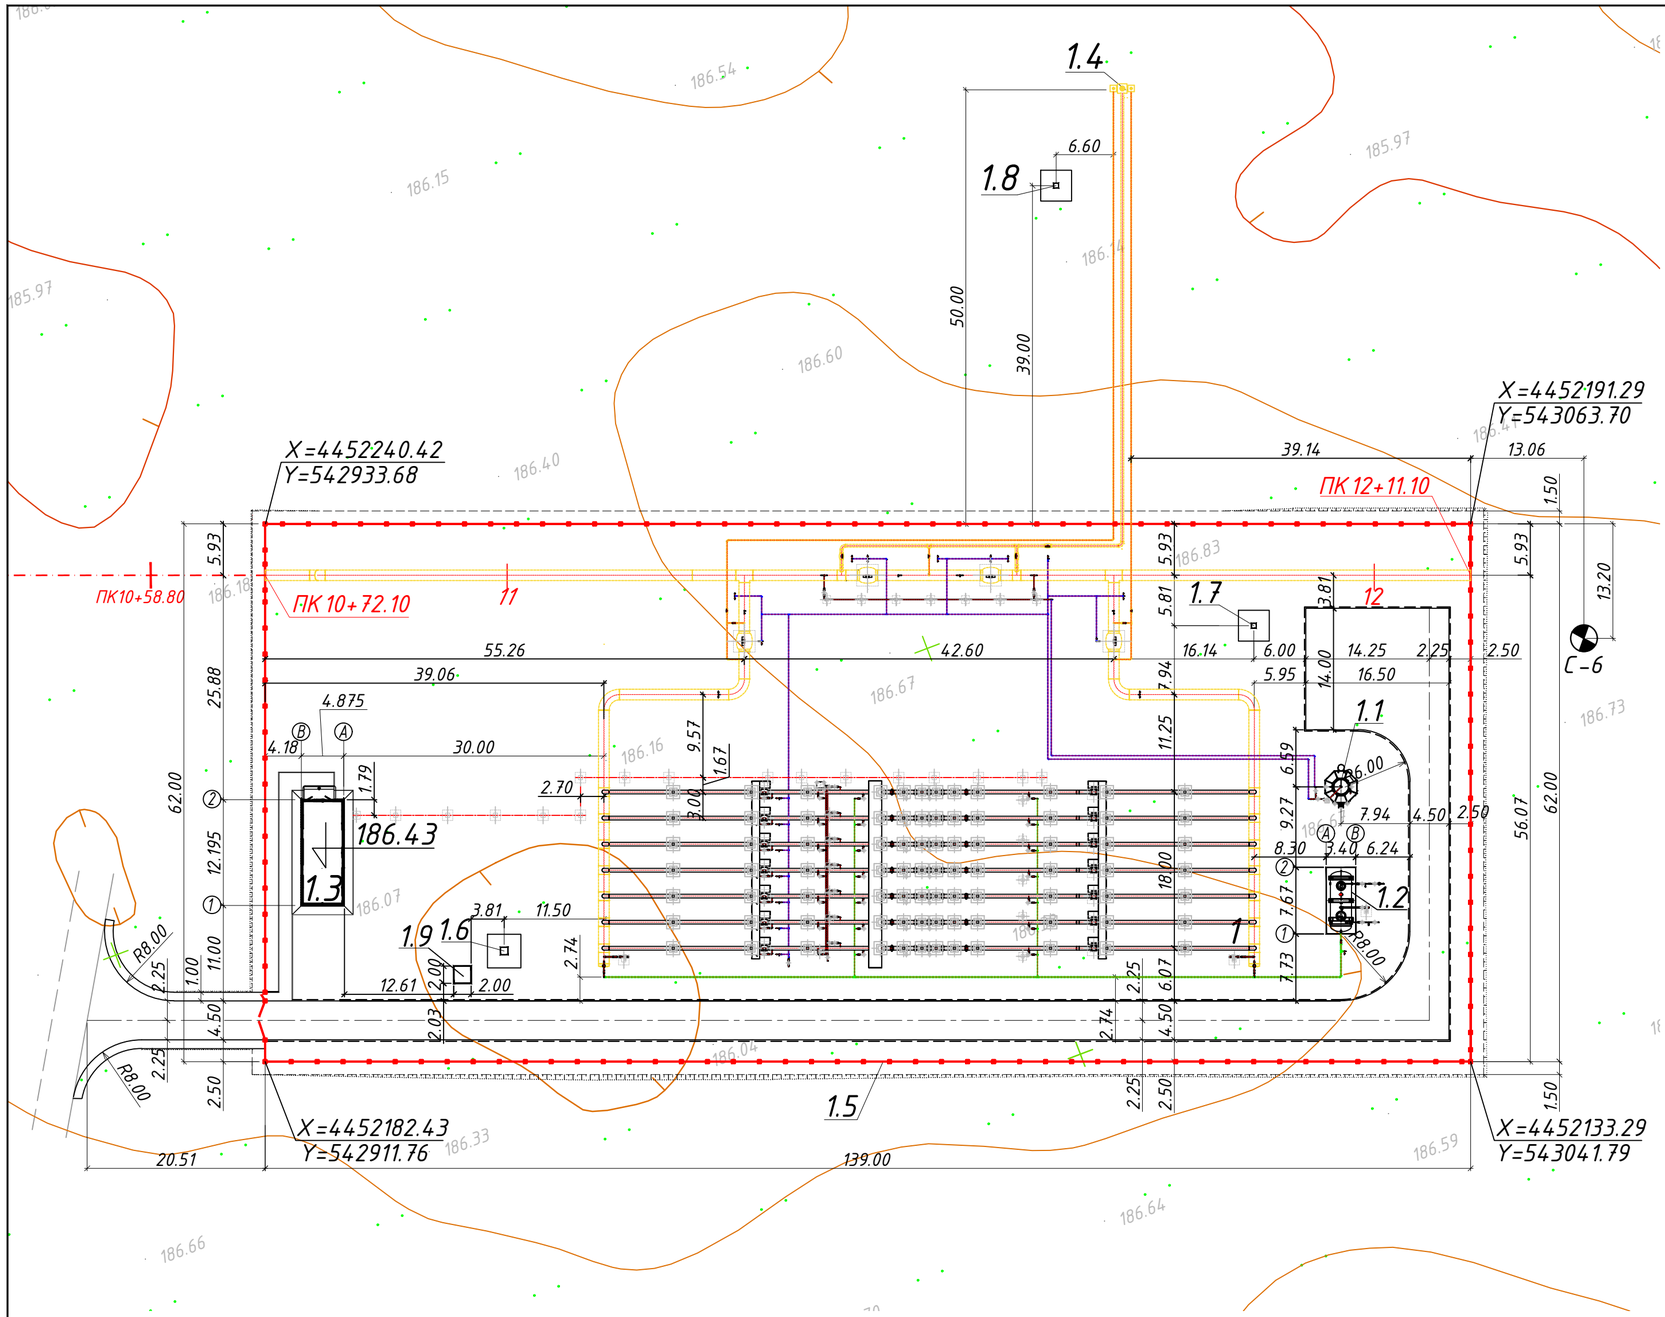

Экспликация зданий и сооружений

Номер на плане	Наименование	Примечание
1	Площадка УЗРГ	
1.1	Ресивер воздуха	
1.2	Площадка дренажной емкости V=25м3	
1.3	Операторная	
1.4	Продувочные свечи	
1.5	Сетчатое ограждение с воротами шир.4.5 м	
1.6	Прожекторная мачта ПМЖ-22.8 (ПМ1)	
1.7	Прожекторная мачта ПМЖ-30.6 (ПМ2)	
1.8	Молниеотвод МЖ-30.6	
1.9	Выгреб	

Условные обозначения:

- Проектируемые ворота распашные
- Проектируемое ограждение
- Проектируемый газопровод (ПК 10+72.10)
- Граница планировки
- Кабельная эстакада

Примечания:


1. При составлении настоящего чертежа были использованы: материалы топографической съемки в масштабе М 1:500, предоставленные заказчиком.
2. Система координат СК-42, система высот - Балтийская.
3. Размеры даны в метрах.
4. Площадка УЗРГ привязана к пикетам газопровода ПК 10+72.10, ПК 12+11.10.

Изм.	Кол.уч	Лист	№док	Подп.	Дата	
ГИП						Площадка УЗРГ Генеральный план и транспорт
Нач.отд.						
Исполн.						
						Разбивочный план М1:500
Н.контр.						

Стадия	Лист	Листов
РП	1	1

Взам. инв.№ | Подпись и дата | Инв. №подл.

Формат А2

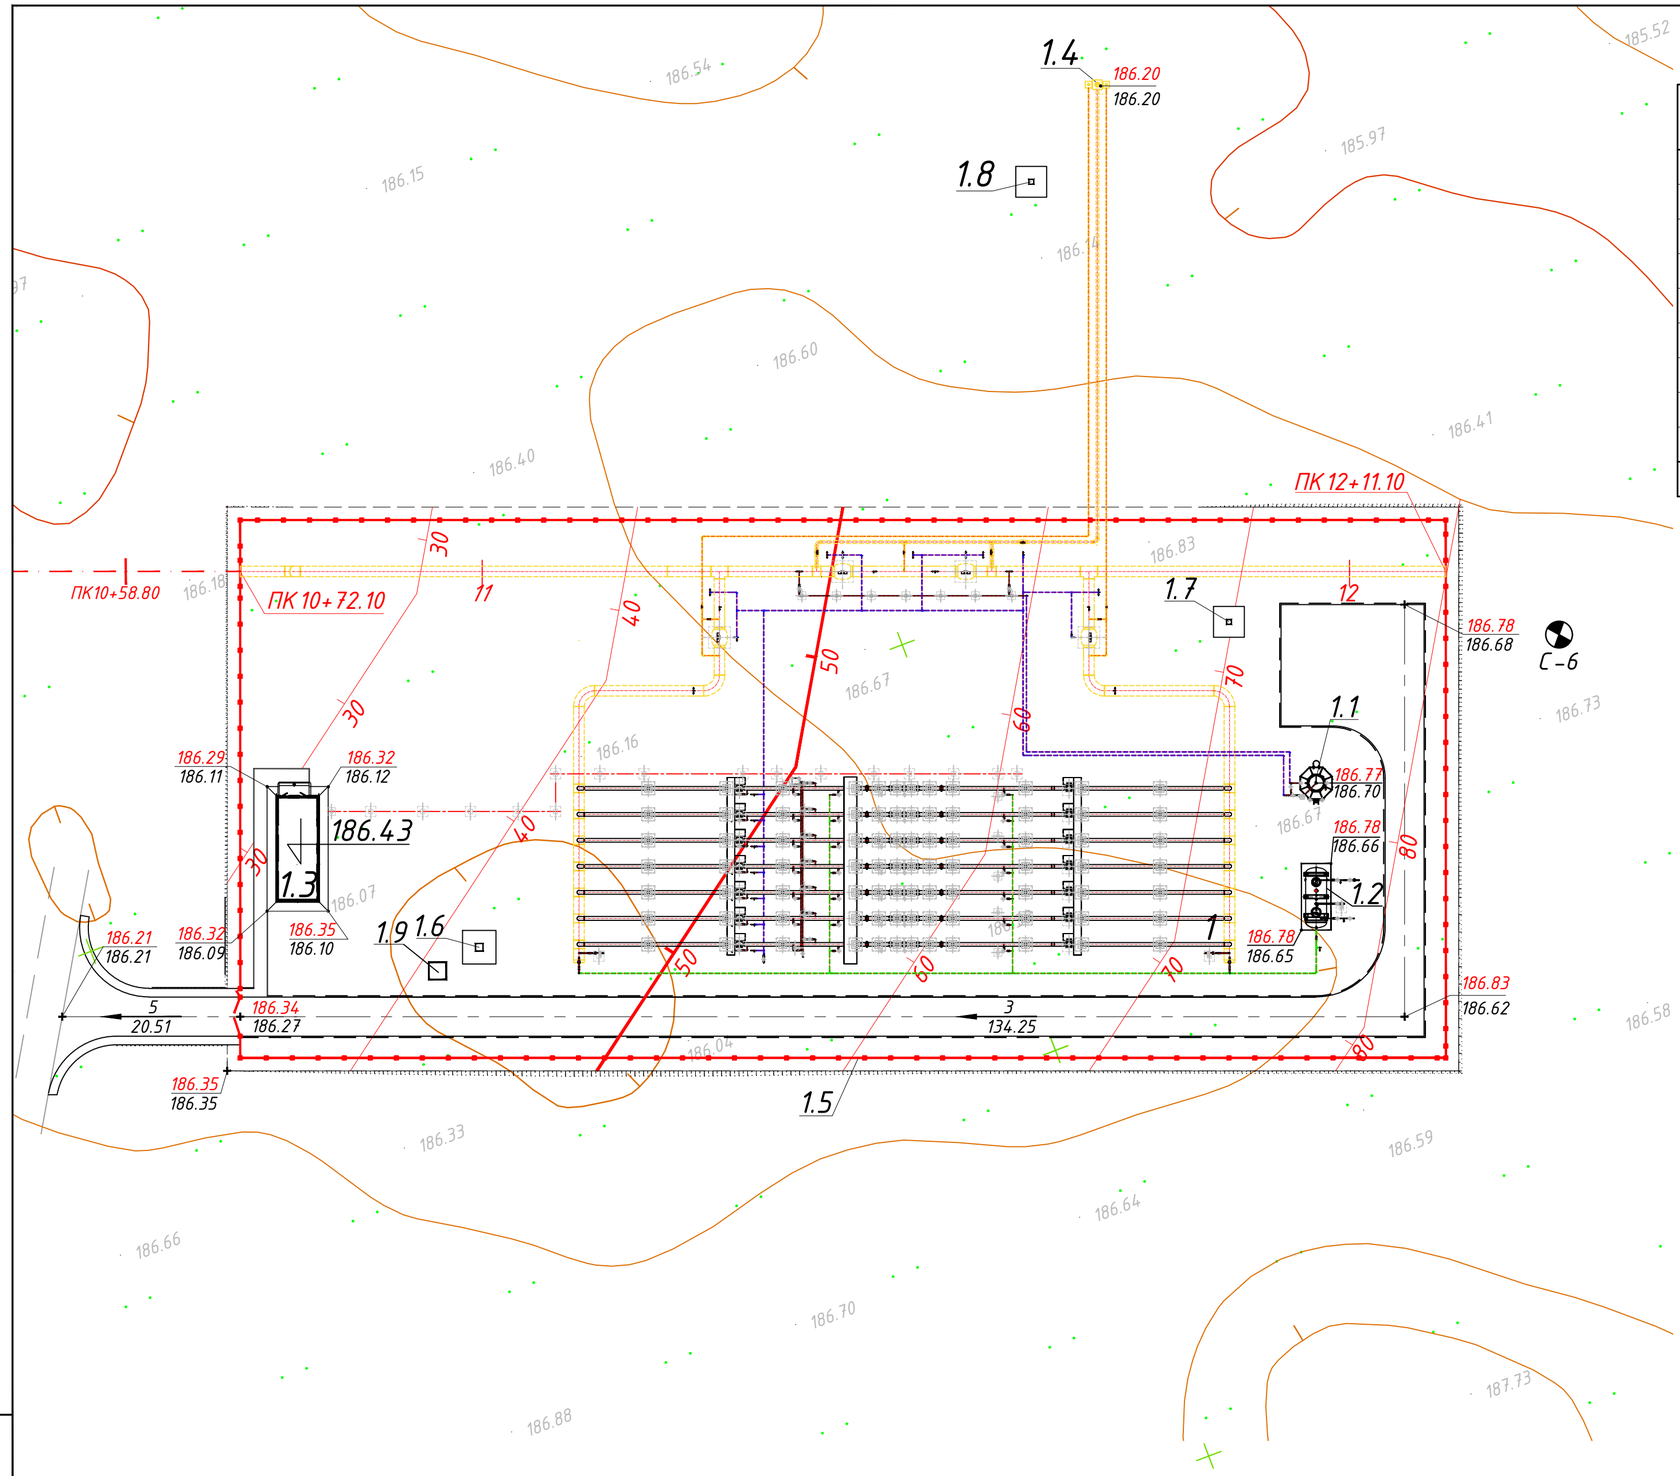

Экспликация зданий и сооружений

Номер на плане	Наименование	Примечание
1	Площадка УЗРГ	
1.1	Ресивер воздуха	
1.2	Площадка дренажной емкости V=25м3	
1.3	Операторная	
1.4	Продувочные свечи	
1.5	Сетчатое ограждение с воротами шир.4.5 м	
1.6	Прожекторная мачта ПМЖ-22.8 (ПМ1)	
1.7	Прожекторная мачта ПМЖ-30.6 (ПМ2)	
1.8	Молниеотвод МЖ-30.6	
1.9	Выгреб	

Условные обозначения:

- Проектируемые ворота распашные
- Проектируемое ограждение
- Проектируемая кабельная эстакада

186.80 / 186.50 — Проектная отметка земли / Существующая отметка земли

80 — Проектные красные горизонтали

3 / 134.25 — Уклон в ‰ / Расстояние в метрах

186.43 — Отметка нуля

— — — — Граница планировки

Примечания:


1. При составлении настоящего чертежа были использованы: материалы топографической съемки в масштабе М 1:500, предоставленные заказчиком.
2. Система координат СК-42, система высот - Балтийская.
3. Размеры даны в метрах.
4. Площадка УЗРГ привязана к пикетам газопровода ПК10+72.10, ПК12+11.10.

Изм.	Кол.уч.	Лист	№док	Подп.	Дата	
ГИП						Площадка УЗРГ Генеральный план и транспорт
Нач.отд.						
Исполн.						
						План организации рельефа М1:500
Н.контр.						

Стадия	Лист	Листов
РП	1	1

Инв. №подл. | Подпись и дата | Взам. инв.№

Формат А2

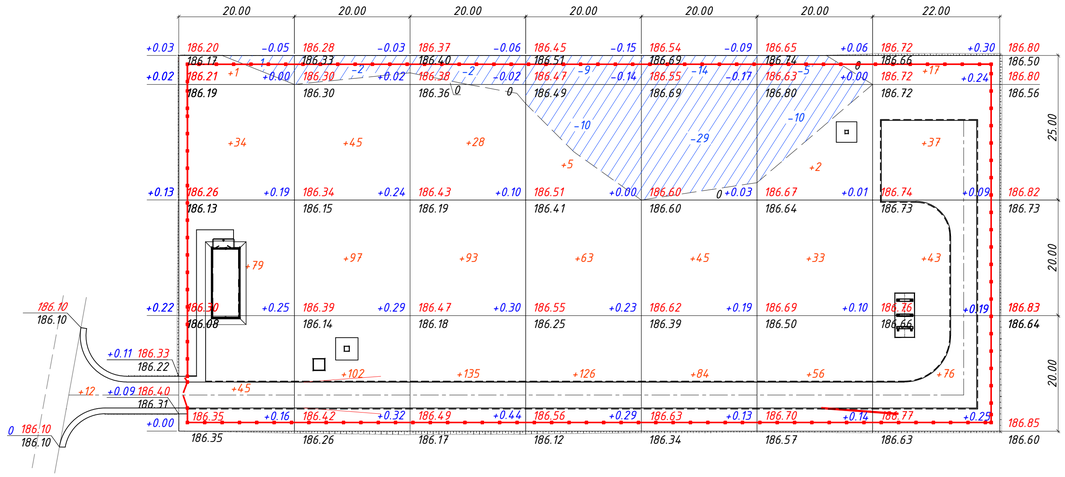

Итого,м3									Всего,м3	
	Насыпь (+)	+12	+159	+244	+256	+194	+129	+91	+173		+1258
	Выемка (-)	--	-1	-2	-2	-19	-43	-15	--		-82

Общая площадь насыпи = 8027 м2
Общая площадь выемки = 1268 м2
Общая площадь 0-области = 106 м2
Общая площадь картограммы = 9401 м2

Ведомость объемов земляных масс

Наименование грунта	Количество, м³				Примечание
	Насыпь (+)	Выемка (-)	Насыпь (+)	Выемка (-)	
1. Грунт планировки территории	1258	82			
2. Вытесненный грунт, в т.ч. при устройстве:					
а) покрытия площадки из щебня толщ. 0.10м		709			
б) автодорожных покрытий		303			
в) растительный слой почвы на участках насыпи толщ. 0.20м		1606			
г) растительный слой почвы на участках выемки толщ. 0.20м		254			
3. Замена растительного грунта					
на участках насыпи толщ. 0.20м	1606				
4. Грунт для устройства откосов насыпи	87				
5. Грунт для устройства откосов выемки		-			
6. Поправка на уплотнение грунта (К=1.1)	295				
Всего пригодного грунта	3246	1094**			
7. Недостаток пригодного грунта		2152			
8. Плодородный грунт, всего, в т.ч.:		1860			
а) избыток плодородного грунта (рекультивация земель)	1860				
9. Итого перерабатываемого грунта	5106	5106			

* С учетом плодородного грунта.
** В карьере.

Условные обозначения:

+43 — объем насыпи в м³


+0.19 | 186.83 / 186.64 — рабочая отм. | проектная отм. / отм. сущ. рельефа

Примечание:

1. Сетка картограммы привязана линейно к ограждению площадки.
2. Сетка квадратов объема земляных масс разбита на ячейки размерами 20х20 м.
3. Производство земляных работ вести в соответствии с требованиями КМК 3.02.01-97.
4. Данная картограмма рассчитана без учёта объёмов вытесненного грунта из под зданий, сооружений и подземных инженерных сетей.

Инв. №подл. | Подпись и дата | Взам. инв.№

Формат А3х3

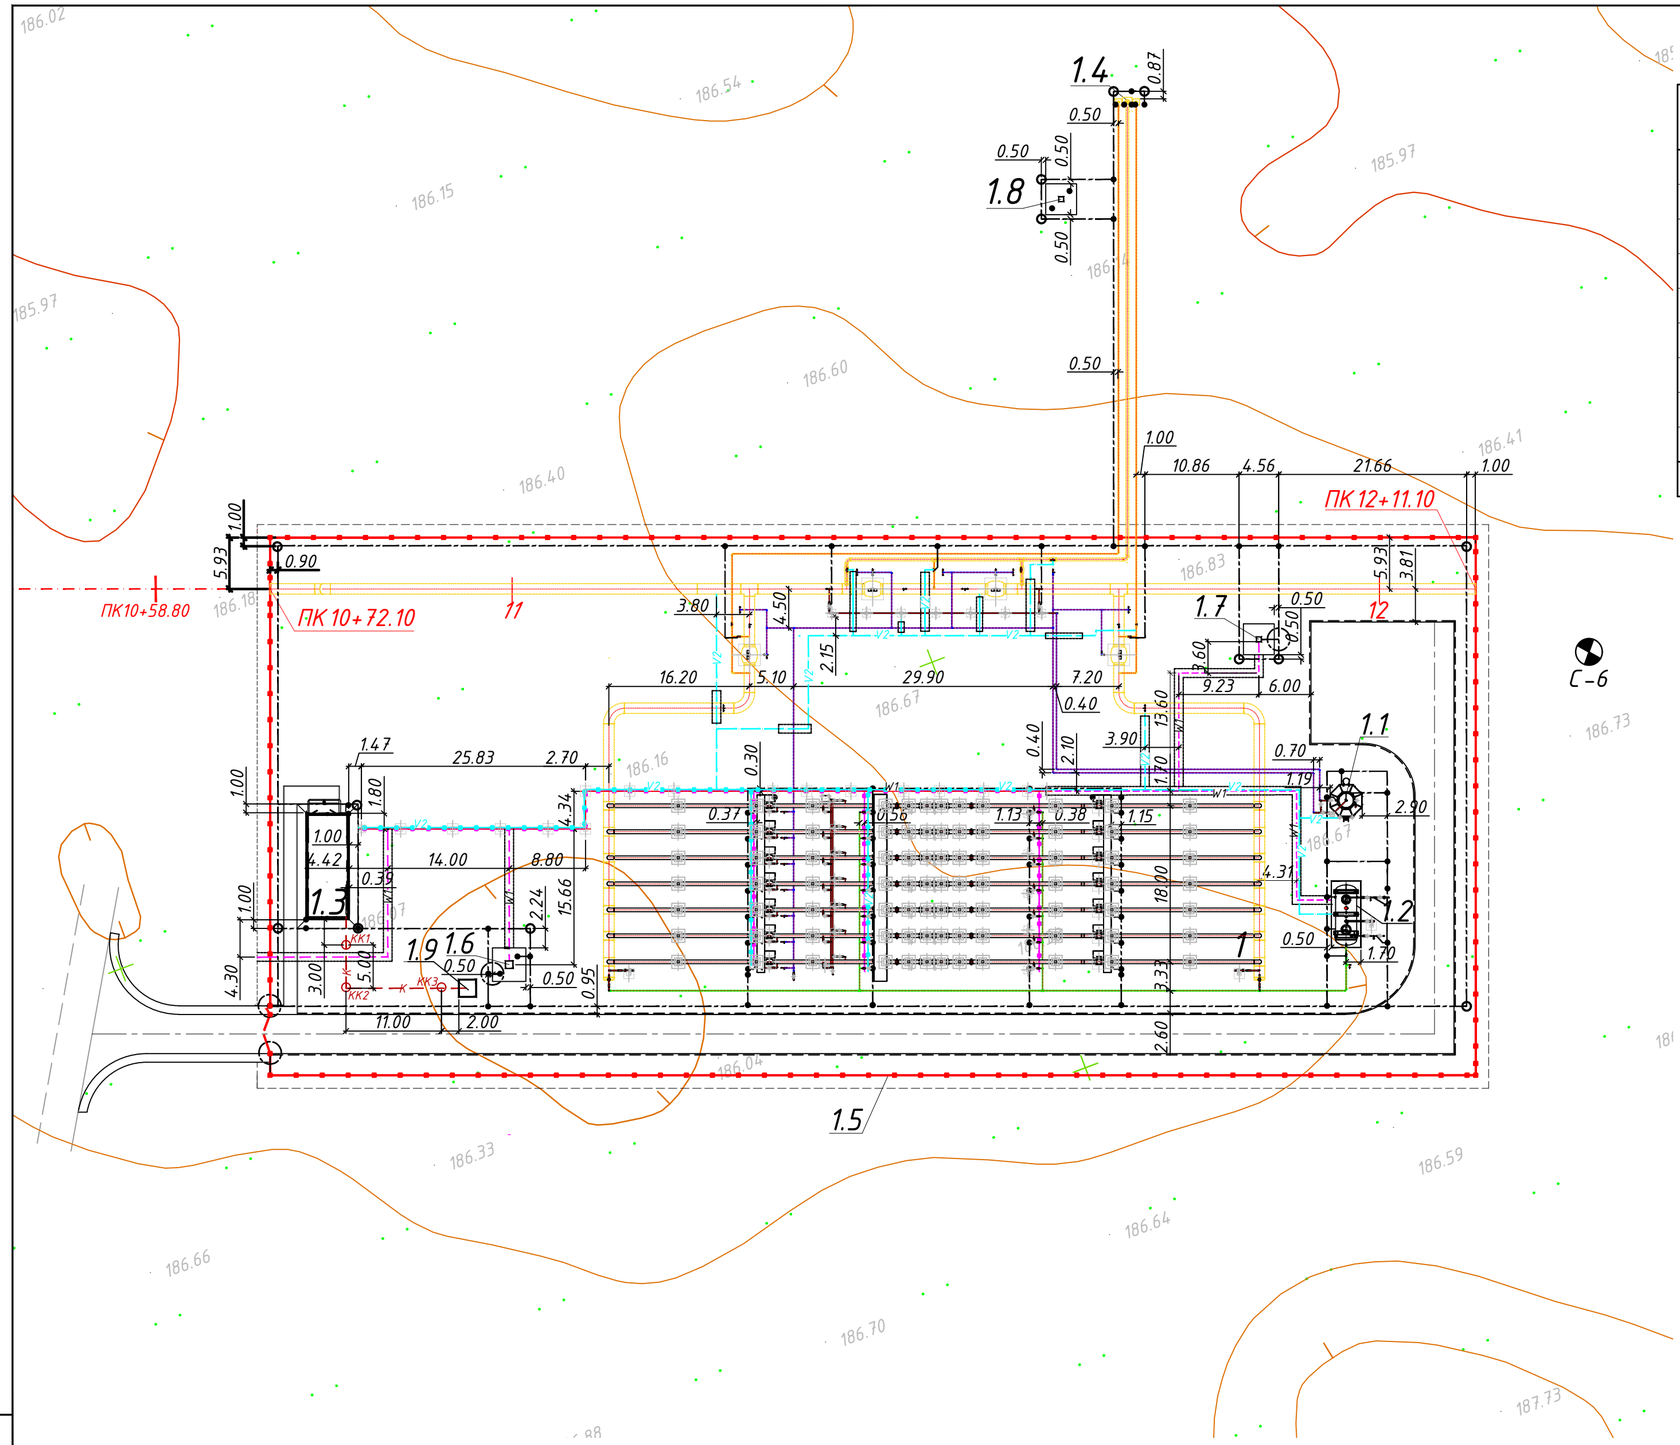

Экспликация зданий и сооружений

Номер на плане	Наименование	Примечание
1	Площадка УЗРГ	
1.1	Ресивер воздуха	
1.2	Площадка дренажной емкости V=25м3	
1.3	Операторная	
1.4	Продувочные свечи	
1.5	Сетчатое ограждение с воротами шир.4.5 м	
1.6	Прожекторная мачта ПМЖ-22.8 (ПМ1)	
1.7	Прожекторная мачта ПМЖ-30.6 (ПМ2)	
1.8	Молниеотвод МЖ-30.6	
1.9	Выгреб	

Условные обозначения:

- Проектируемые ворота распашные
- Проектируемое ограждение
- ПК 10+72.10 – Проектируемый газопровод
- Граница планировки
- Электрические кабели по кабельной эстакаде
- Электрические кабели напряжением до 1 кВ в траншее
- Горизонтальный заземлитель – полоса 4х40,прокладываемая горизонтально на глубине 0.5м
- Вертикальный заземлитель – круг 16 длиной 3м
- Места присоединения полосы заземления при помощи сварки
- V2 – Кабели КИПиА по проектируемой эстакаде
- V2 – Кабели КИП в траншее
- V2 – Кабели КИП в траншее, в защитном трубопроводе
- К – Хозяйственно-бытовая канализация
- КК2 – Канализационный колодец

Примечания:


1. При составлении настоящего чертежа были использованы: материалы топографической съемки в масштабе М 1:500, предоставленные заказчиком.
2. Система координат СК-42, система высот – Балтийская.
3. Размеры даны в метрах.
4. Площадка УЗРГ привязана к пикету газопровода ПК 10+72.10, ПК 12+11.10.

Изм.	Кол.уч	Лист	№док	Подп.	Дата	
ГИП						Площадка УЗРГ Генеральный план и транспорт
Нач.отд.						
Исполн.						
						Сводный план инженерных сетей М1:500
Н.контр.						

Стадия	Лист	Листов
РП	1	1

Взам. инв.№ | Подпись и дата | Инв. №подл.

Формат А2

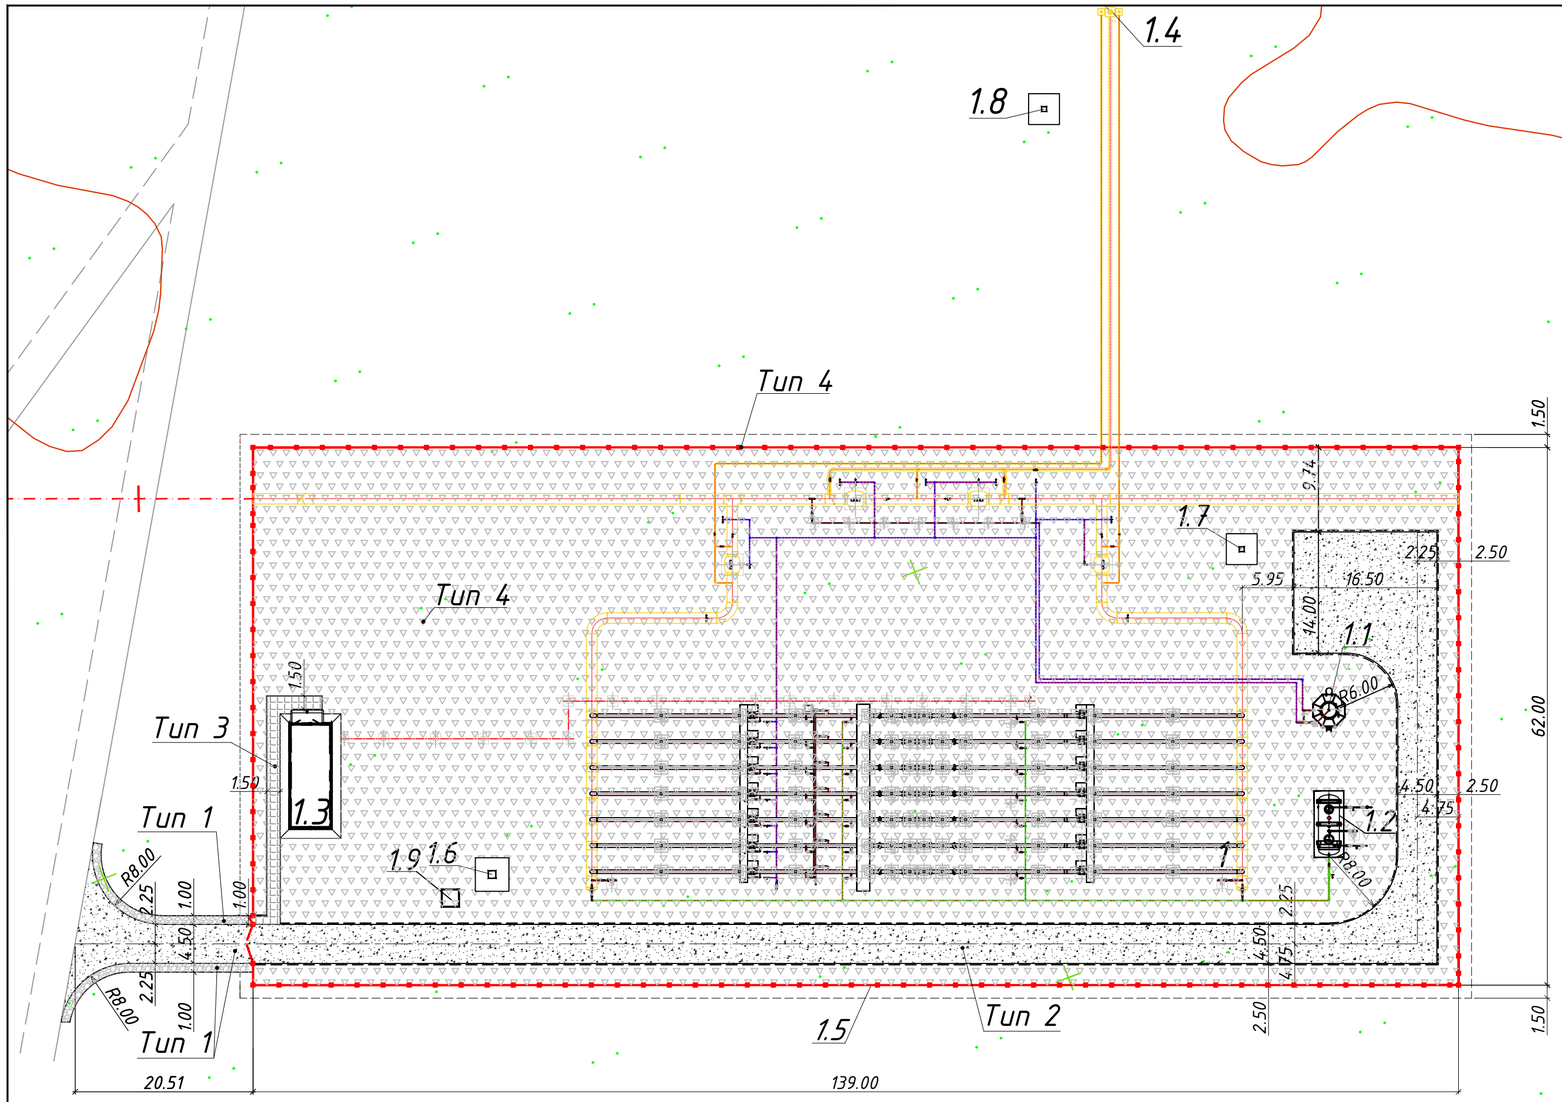

Экспликация зданий и сооружений

Номер на плане	Наименование	Примечание
1	Площадка УЗРГ	
1.1	Ресивер воздуха	
1.2	Площадка дренажной емкости V=25м3	
1.3	Операторная	
1.4	Продувочные свечи	
1.5	Сетчатое ограждение с воротами шир.4.5 м	
1.6	Прожекторная мачта ПМЖ-22.8 (ПМ1)	
1.7	Прожекторная мачта ПМЖ-30.6 (ПМ2)	
1.8	Молниеотвод МЖ-30.6	
1.9	Выгреб	

Ведомость тротуаров, дорожек и площадок

Поз	Обозначение	Наименование	Тип	Площадь покрытия, м²	Примечание
1		Покрытие из щебеночно-песчаной смеси толщ. 0.15м по ГОСТ 25607-2009	1	333.5	Подъездная автодорога
2		Покрытие из щебеночно-песчаной смеси толщ. 0.15м по ГОСТ 25607-2009	2	1008	Внутриплощ. дороги
3		Укрепление обочины из ГПС толщ. 0.15м смесь С4 по ГОСТ 25607-2009	1	47.6	Подъездная автодорога
4		Покрытие из квадратных тротуарных плит марки А.6К.7 ГОСТ 17608-2017 h-0.07м	3	49	
5		Покрытие верха площадки из щебня фр. 20-40мм толщ. 0.10м по ГОСТ 8267-93	4	74.30	
6	------	Бетонный бордюрный камень БР300.30.18 бетон В30 (М-400) ГОСТ 6665-91*		383	п.м
7	------	Бетонный бордюрный камень БР100.20.8 бетон В15 (М-400) ГОСТ 6665-91*		45	п.м

Условные обозначения:


- Проектируемые ворота распашные
- Проектируемое ограждение
- Проектируемый газопровод

ПК 10+72.10


Примечания:

1. При составлении настоящего чертежа были использованы: материалы топографической съемки в масштабе М 1:500, предоставленные заказчиком.
2. Система координат СК-42, система высот - Балтийская.
3. Размеры даны в метрах.
4. Площадка УЗРГ привязана к пикету газопровода ПК 10+72.10, ПК 12+11.10.

Тип 1

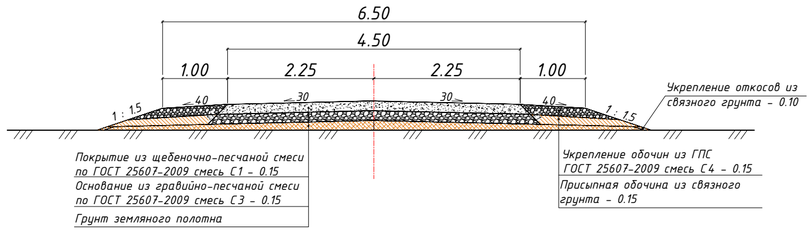


Тип 3

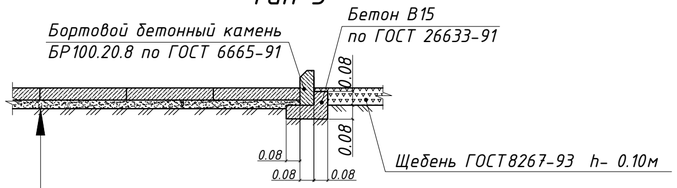


	Квадратная плита, марка А.6К.7	
1	0.5х0.5м ГОСТ 17608-2017	h-0.07м
2	Среднезернистый песок по ГОСТ 8736-93	h-0.15м
3	Уплотненный грунт с К. упл. не <0.98	

Тип 2

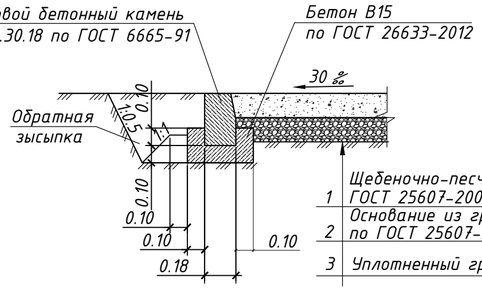

1	Щебеночно-песчаная смесь по ГОСТ 25607-2009, смесь С-1	h=0.15м
2	Основание из гравийно-песчаной смеси по ГОСТ 25607-2009 смесь С3	h=0.15м
3	Уплотненный грунт	

Тип 4

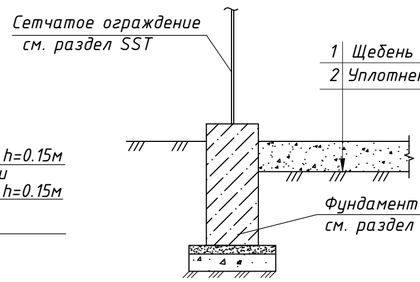

1	Щебень фр.20-40мм по ГОСТ 8267-93	h=0.10м
2	Уплотненный грунт с К. упл. не <0.98	

Изм.	Кол.уч.	Лист	№док.	Подп.	Дата			
ГИП						Площадка УЗРГ Генеральный план и транспорт	Стадия	Лист	Листов
Нач.отд.							РП	1	1
Исполн.						План благоустройства территории М1:500			
Н.контр.									

Взам. инв.№ | Подпись и дата | Инв. №подл.

Формат А2

Позиция	Наименование работ	Единица измерения	Количество	Примечание
	Вертикальная планировка: Насыпь/Выемка	$м^3/м^3$	1258/82	
	Земляные работы			
1	Разработка растительного грунта бульдозером с погрузкой экскаватором на автосамосвалы и вывоз до 5 км	$м^3$	1860	1606+254 =1860
2	Разработка грунта 1группы в карьере экскаватором с погрузкой в автосамосвалы и транспортировкой в насыпь на расстояние до 5 км	$м^3$	2152	
3	Уплотнение насыпи катками на пневмоколесном ходу за 6-8 проходов по одному следу при толщине слоя до 0.20м с поливкой водой.	$м^3$	2152	
4	Разработка грунта 1 группы бульдозером под покрытие дорог и площадки бульдозером с перемещением в насыпь	$м^3$	1045.4	
5	Планировка территории площадки после земляных работ: планировка насыпи под автодорогу -//-//- под площадки	$м^2$ $м^2$	1008 7430	
6	Планировка откосов насыпи механизированным способом	$м^2$	87	
7	Укрепление откосов дороги из связного грунта	$м^2$	23	(h=0.10м)

Взамен инв.№

Подпись и дата

Инв.№ подл.

Изм.	Кол.уч	Лист	№док	Подп.	Дата
ГИП					
Нач.отд.					
Исполн.					
Н.контр.					

Площадка УЗРГ
Генеральный план и транспорт

Стадия	Лист	Листов
РП	1	2

Ведомость объемов работ

Формат А4

Позиция	Наименование работ	Единица измерения	Количество	Примечание
	Устройство дорожной одежды	$м^2$	1341.5/47.6	47.6-обочина
8	Щебеночно-песчаная смесь С1 К.упл.=1.1 по ГОСТ 25607-2009	$м^3$	221.4	(h=0.15м)
9	Гравийно-песчаная смесь С3 с К.упл.=1.2 по ГОСТ 25607-2009	$м^3$	241.5	(h=0.15м)
10	Укрепление обочины из ГПС, смесьС4, с К.упл.=1.2 по ГОСТ 25607-2009	$м^3$	9	(h=0.15м)
11	Присыпная обочина из связного грунта, с К.упл.=1.1	$м^3$	2	(h=0.15м)
12	Бетонный бордюрный камень БР300.30.18 бетон В30 (М-400) по ГОСТ 6665-91	пм	383	
13	Подготовка под бордюрный камень, бетон В15 по ГОСТ 26633-2012	$м^3$	22.3	
	Тротуарное покрытие из квадратных плит			
14	Квадратная плита, марка А.6К.7 ГОСТ 17608-91	$м^2$	49	(h=0.07м)
15	Подстилающий слой из песка по ГОСТ 17608-93 с К.упл.=1.15	$м^3$	8.5	(h=0.15м)
16	Бетонный бордюрный камень БР100.20.8 бетон В15 (М-400) по ГОСТ 6665-91	пм	45	
17	Подготовка под бордюрный камень, бетон В15 по ГОСТ 26633-2012	$м^3$	1.5	
18	Покрытие площадки из щебня фр. 20-40мм по ГОСТ 8267-93	$м^2/м^3$	7430/743	(h=0.10м)

Взамен инв.№

Подпись и дата

Инв.№ подл.

Изм.	Кол.уч.	Лист	№док.	Подп.	Дата