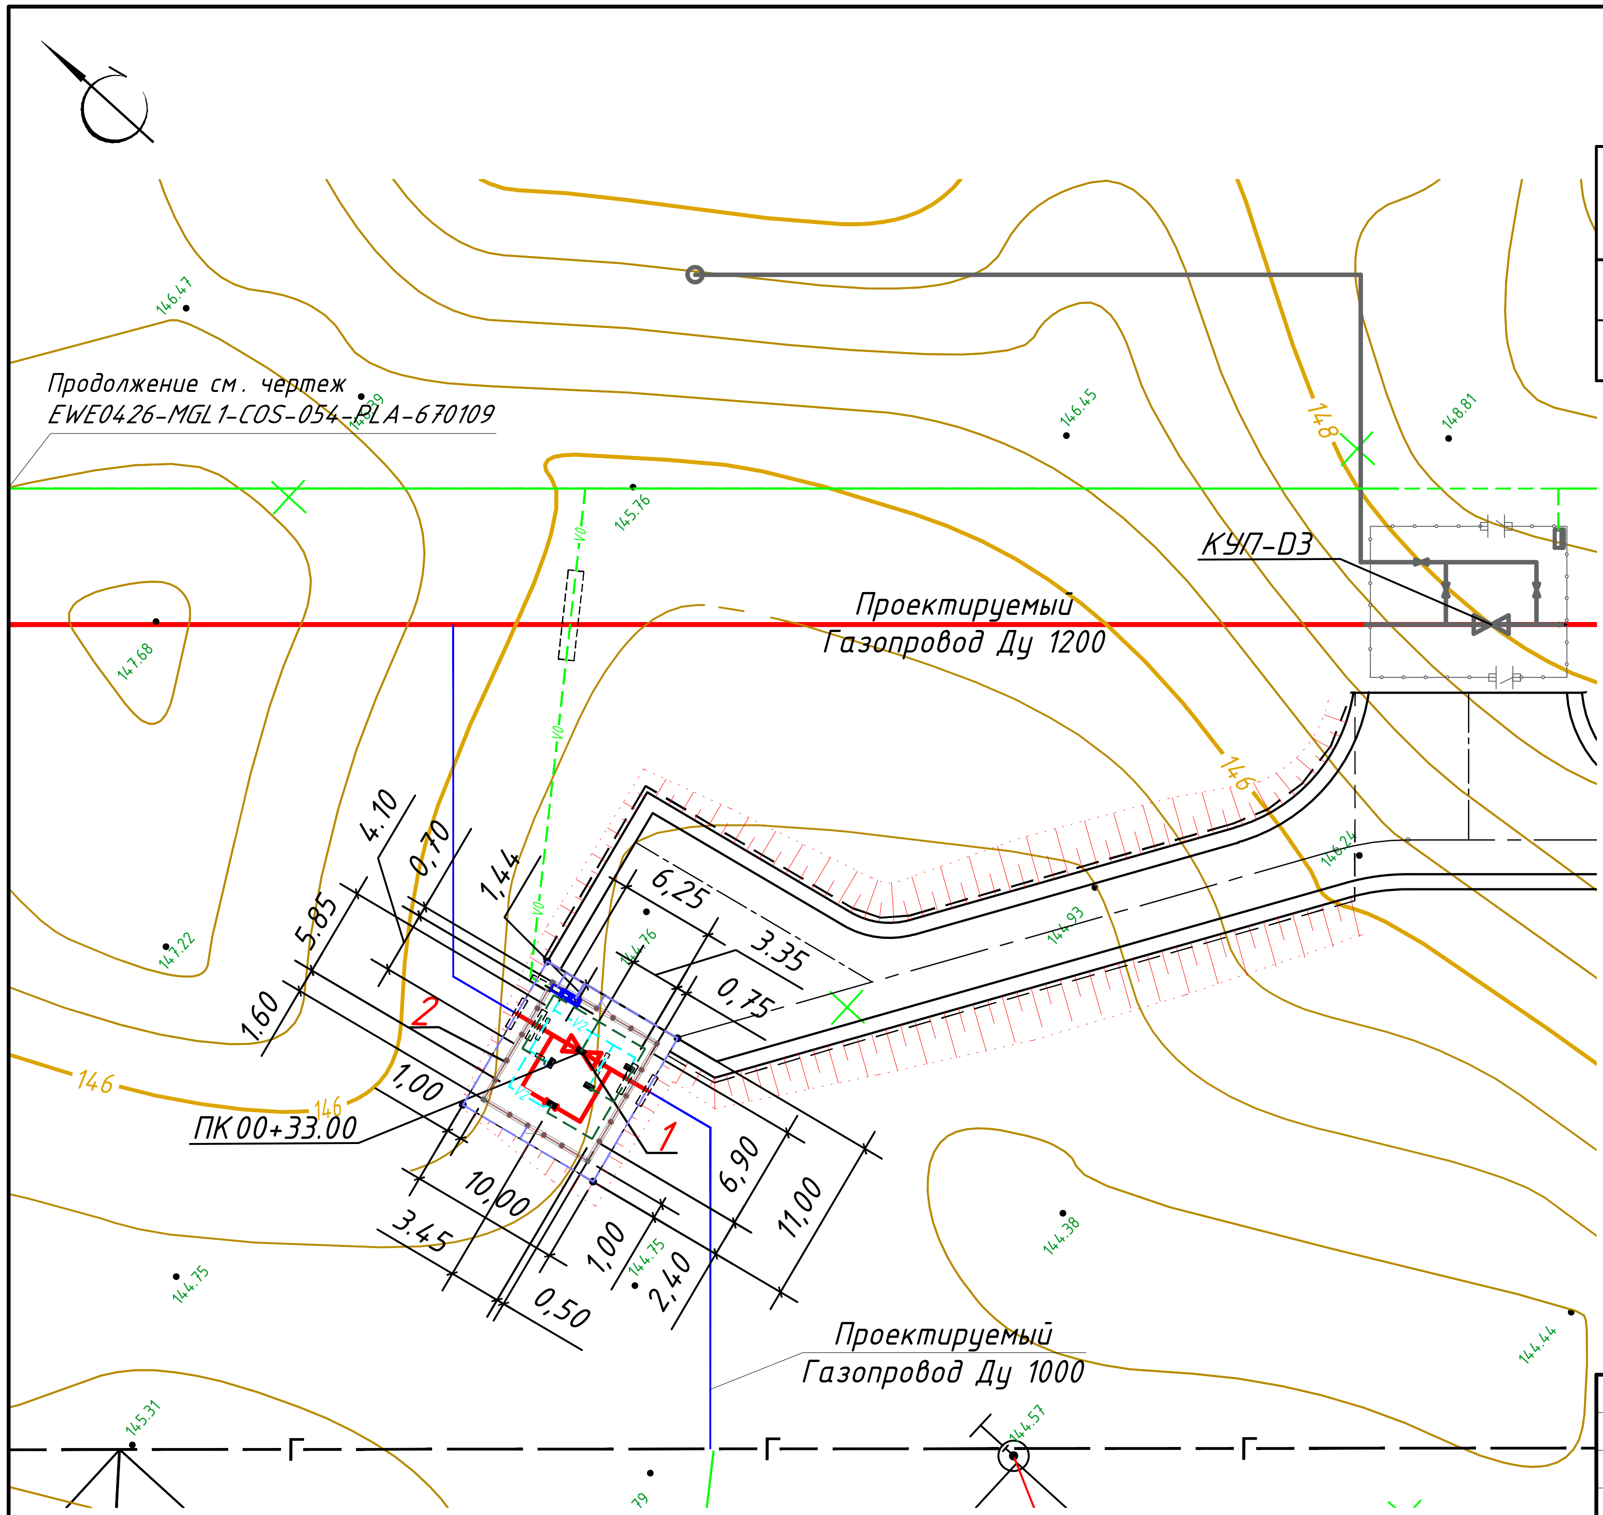

Экспликация зданий и сооружений

Номер на плане	Наименование	Примечание
1	Крановый узел Ду 1000	
2	Ограждение сетчатое	

Условные обозначения

—г——г—	Существующий газопровод
🟥	Проектируемый газопровод ДУ-1200
🟦	Проектируемый газопровод ДУ-1000
●	Вертикальный заземлитель Ф16
- - - -	Полоса заземления 4х40
— — —	Гибкий провод
⌐ ─ ─ ┐	Стальная труба
▭	Шкаф телемеханики (ШТМ)
▬	Датчики давления
---V2---	Проектный кабель КИПиА в траншее
-[-V2-]-	Проектный кабель КИПиА в ПНД трубе
---V0---	Проектируемый волоконно-оптический кабель в траншее
-[-V0-]-	Проектируемый волоконно-оптический кабель в трубе

Примечания:

При составлении настоящего чертежа были использованы :

1. Материалы топографо-геодезической съемки, предоставлены АО "O'ZLITINEFTGAZ".
2. Площадка кранового узла КУП-D5 привязана линейно к пикету ПК 0+33.00
3. Расстояние по горизонтали (в свету) от подземных инженерных сетей до зданий и сооружений следует принимать не менее указанных в табл.9 см. ШНК 2.09.17-21 "Проектирование генеральных планов промышленных предприятий".
4. Расположение оборудования и прокладку кабелей уточнить по месту при монтаже.
5. Данный лист смотри совместно с листами разделов PIL, PRE, ELE, STR, SYS.
6. Детальный план кранового узла см. EWE0426-MGL1-PRE-054-DRW-740203.
7. Детальный план сетей КИПиА см. EWE0426-MGL1-SYS-054-PLA-740306.
8. Детальный план сетей заземления см. EWE0426-MGL1-ELE-054-DRW-740402.
9. Детальный план ограждения см. EWE0426-MGL1-STR-054-DRW-740507.
6. Сводный план инженерных сетей кранового узла КУП-D3 см. EWE0426-MGL1-GLT-054-DRW-720103.

Взам. инв.№
Подпись и дата
Инв. № подл

Рев.	Дата	Назначение ревизии	Проверил	Утвердил
A1	23.09.2026	Выпущено для строительства		
R1	07.08.2026	Выпущено для рассмотрения		

ЗАКАЗЧИК: UTG UZTRANSGAZ
ГЕНЕРАЛЬНЫЙ ПОДРЯДЧИК: UET UZBEKENERGOTAMIR
ПОДРЯДЧИК: PBG Pro Build Generation
ГЕНЕРАЛЬНЫЙ ПРОЕКТИРОВЩИК: EAST WEST ENGINEERING

EWE0426-MGL1-GLT-054-DRW-740105-A1

«СТРОИТЕЛЬСТВО НОВЫХ НИТОК (УЧАСТКОВ) ГАЗОПРОВОДОВ «ГАЗЛИ - САРИМОЙ» И «АКЧАЛОК - ГАЗЛИ - НУКУС» ОБЩЕЙ ПРОТЯЖЕННОСТЬЮ НЕ МЕНЕЕ 275 км».

Изм.	Кол.уч.	Лист	№ док.	Подпись	Дата
ГИП		Схабицкий А.			09.2026
Нач.отд.		Нигманова Н.			09.2026
Исполн.		Горлова О.			09.2026
Н.контр		Схабицкий А.			09.2026

ГАЗОПРОВОД «ГАЗЛИ-САРИМОЙ» (54 км)
Генеральный план и транспорт.

Стадия	Лист	Листов
РД	1	1

КУП-D5.
Сводный план инженерных сетей.
М 1:500

EAST WEST ENGINEERING
ООО "EAST-WEST Engineering"
г. Ташкент 2026 г.

Формат / Format A3