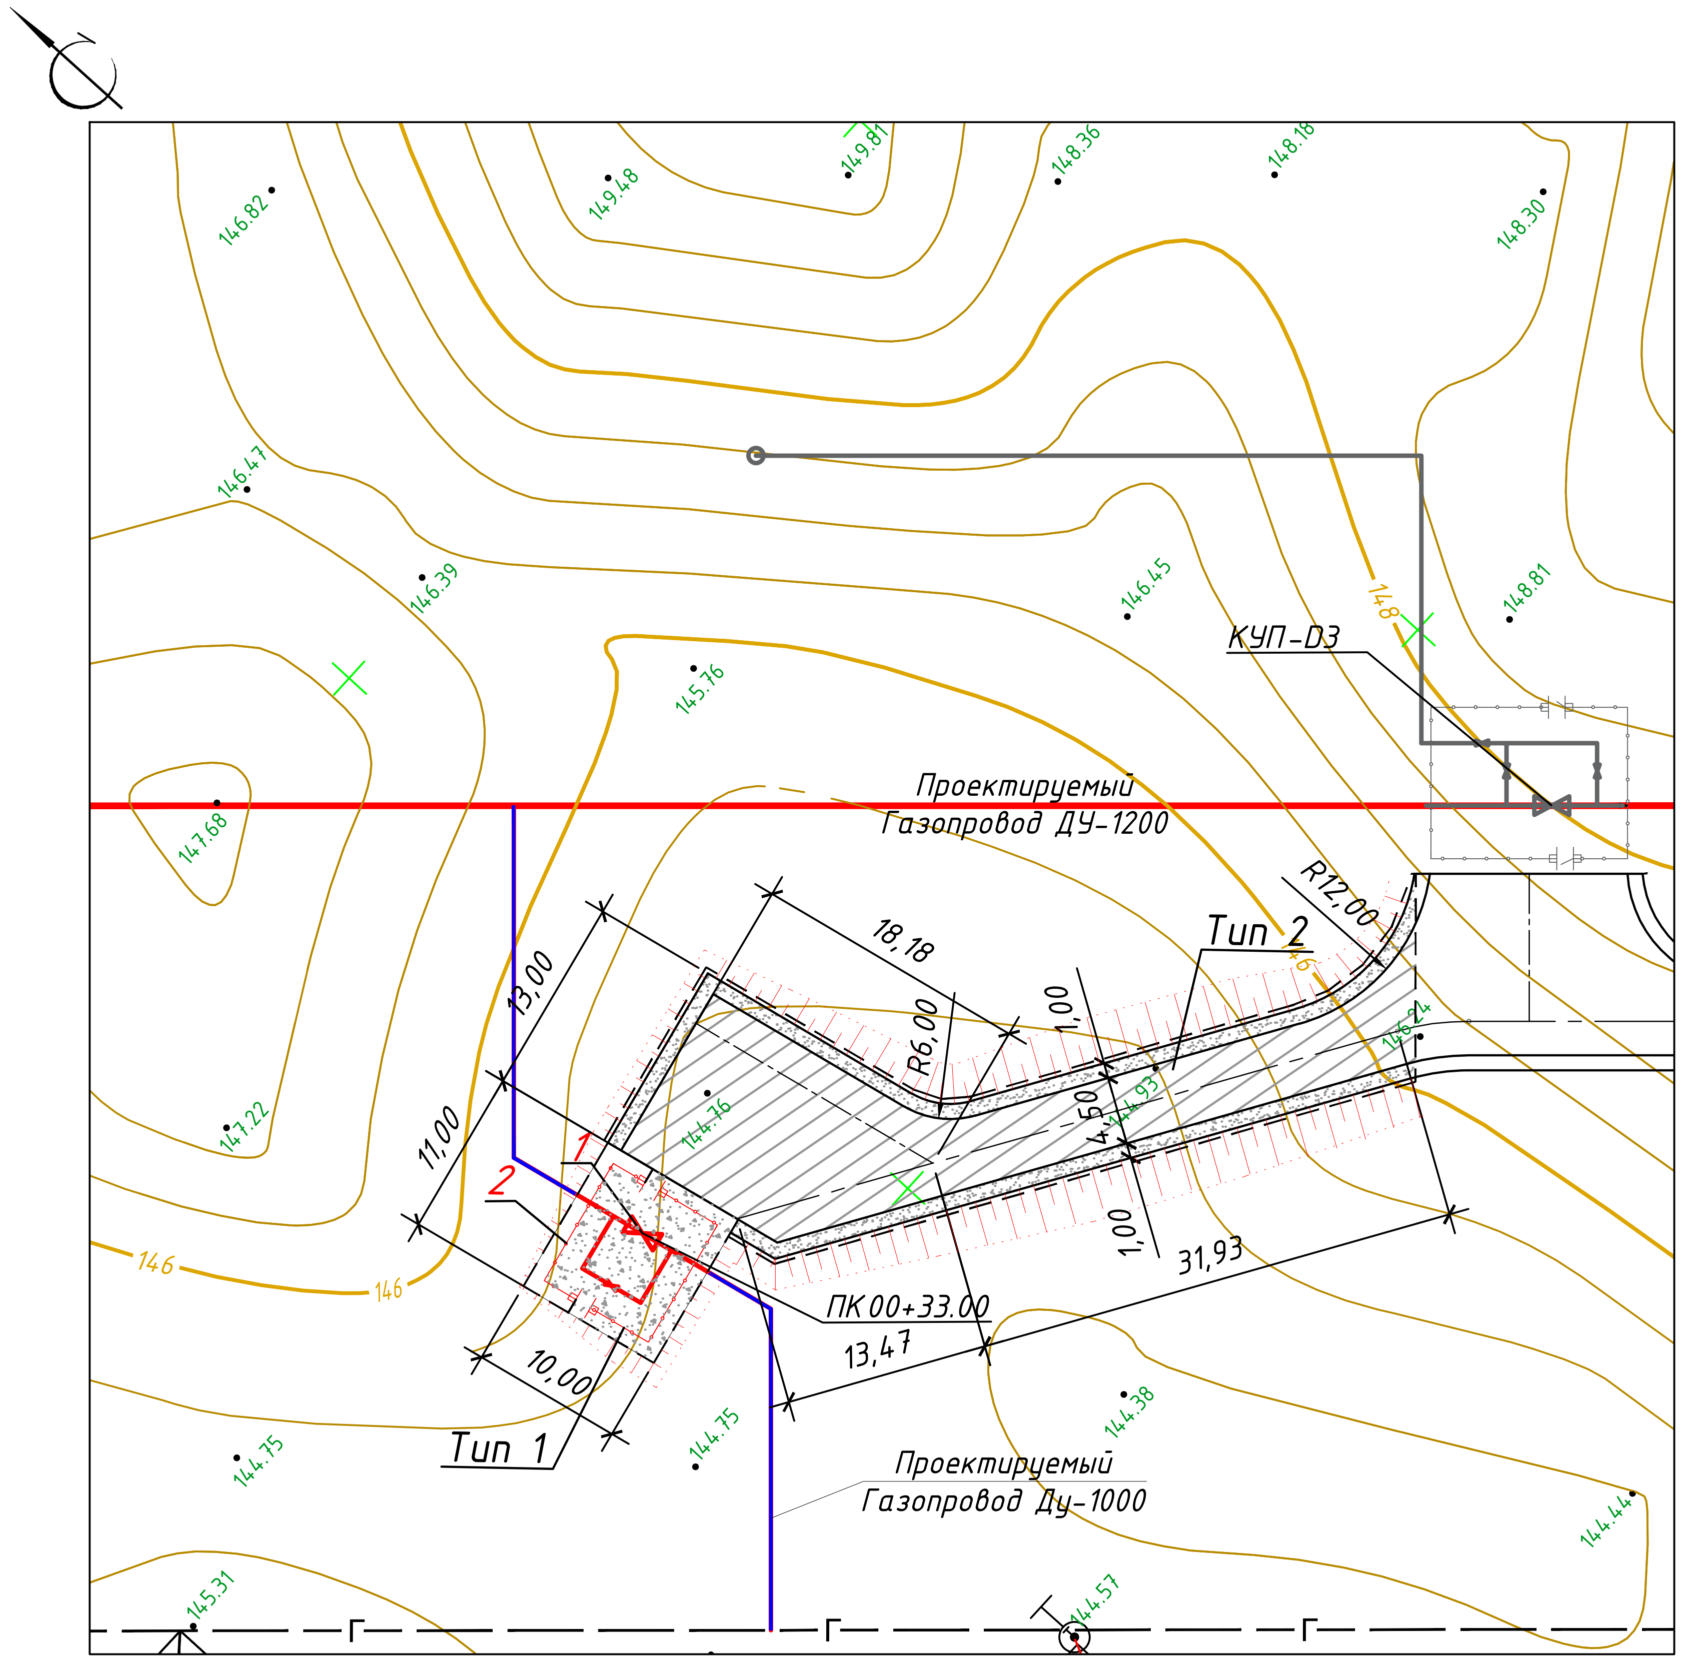

## Тип 2

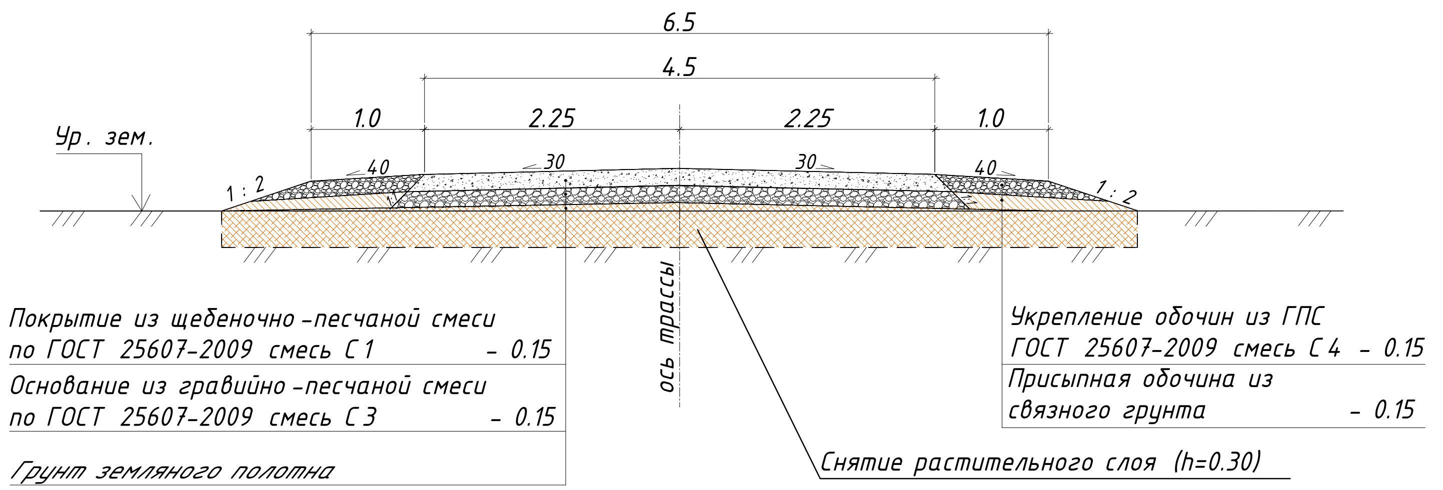
6.5
4.5
1.0
2.25
2.25
1.0
Ур. зем.
40
30
30
40
1 : 2
1 : 2
Покрытие из щебеночно-песчаной смеси по ГОСТ 25607-2009 смесь С1 - 0.15
Основание из гравийно-песчаной смеси по ГОСТ 25607-2009 смесь С3 - 0.15
Грунт земляного полотна
ось трассы
Укрепление обочин из ГПС ГОСТ 25607-2009 смесь С4 - 0.15
Присыпная обочина из связного грунта - 0.15
Снятие растительного слоя (h=0.30)

## Тип 1

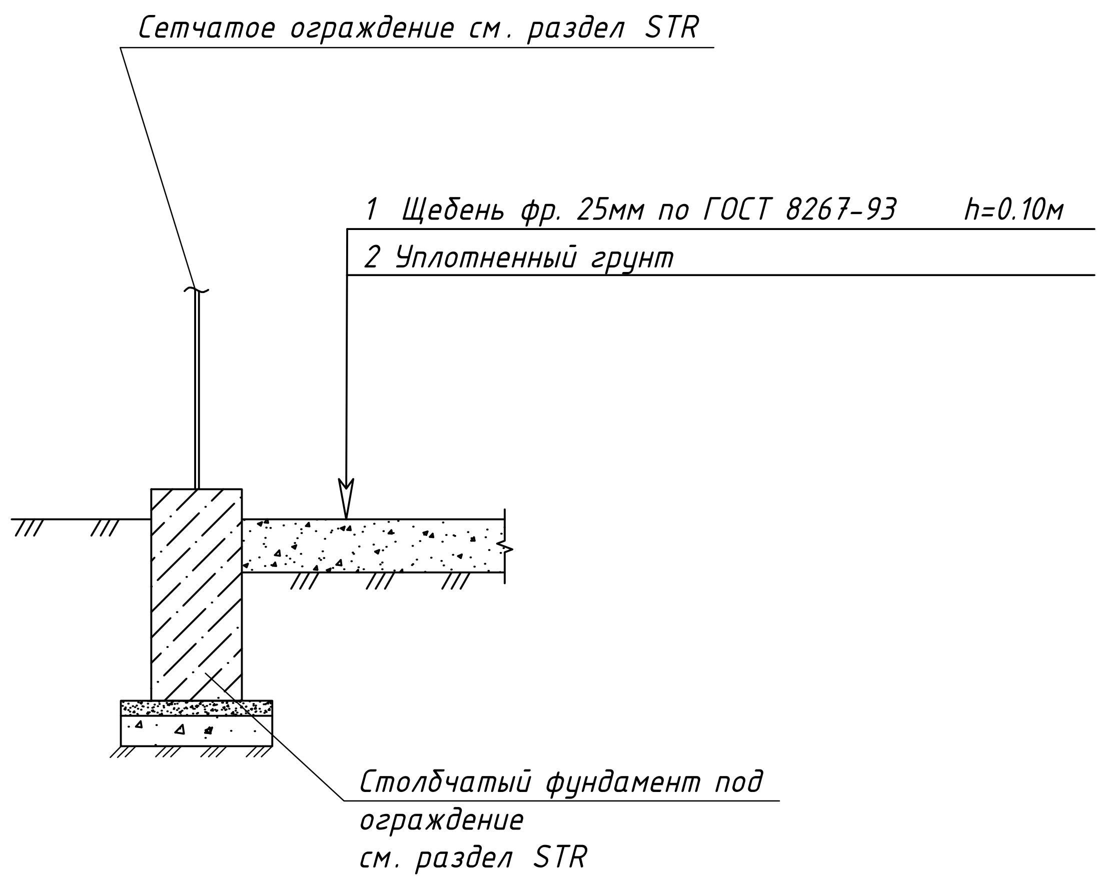
Сетчатое ограждение см. раздел STR
1 Щебень фр. 25мм по ГОСТ 8267-93 h=0.10м
2 Уплотненный грунт
Столбчатый фундамент под ограждение см. раздел STR

## Экспликация зданий и сооружений

| Номер на плане | Наименование | Примечание |
|---|---|---|
| 1 | Крановый узел Ду 1000 | |
| 2 | Продувочная свеча | |
| 3 | Ограждение сетчатое | |

## Ведомость тротуаров, дорожек и площадок

| Тип | Обозначение | Наименование | Ед. изм. | Примечание |
|---|---|---|---|---|
| Покрытие площадки | | | | |
| 1 | ⬚ | Покрытие из щебня по ГОСТ 8267-93, h=0.10 | $м^2$ | 95 |
| Покрытие проездов | | | | |
| 2 | ▨ | Покрытие из щебеночно-песчаной смеси по ГОСТ 25607-2009 смесь С1 h=0,15 м<br>Основание из гравийно-песчаной смеси по ГОСТ 25607-2009 смесь С3 h=0,15 м | $м^2$ | 360.0 |
| | | Укрепление обочин из ГПС ГОСТ 25607-2009 смесь С4 h=0,15 м | $м^2$ | 115.0 |

### Примечания:

При составлении настоящего чертежа были использованы :

1. Материалы топографо-геодезической съемки, предоставлены АО "O'ZLITINEFTGAZ".
2. Система координат местная. Высотные отметки даны в Балтийской системе.
3. Размеры даны в метрах.
4. Площадка кранового узла КУП-D5 привязана линейно к пикету ПК 00+33.00.
5. Данный лист смотри совместно с листами разделов PIL, PRE, ELE, STR, SYS.
6. Детальный план кранового узла см. EWE0426-MGL1-PRE-054-DRW-740203.
7. План благоустройства территории кранового узла КУП-D3 см. EWE0426-MGL1-GLT-054-DRW-720106.

Взам. инв. №
Подпись и дата
Инв.№ подл.

| Рев. | Дата | Назначение ревизии | Проверил | Утвердил |
|---|---|---|---|---|
| A2 | 06.10.2026 | Выпущено для строительства | | |
| A1 | 26.08.2026 | Выпущено для строительства | | |
| R1 | 21.07.2026 | Выпущено для рассмотрения | | |

ЗАКАЗЧИК: UTG UZTRANSGAZ
ГЕНЕРАЛЬНЫЙ ПОДРЯДЧИК: UET UZBEKENERGOTAMIR
ПОДРЯДЧИК: PBG Pro Build Generation
ГЕНЕРАЛЬНЫЙ ПРОЕКТИРОВЩИК: EAST WEST ENGINEERING

**EWE0426-MGL1-GLT-054-DRW-740106-A2**

«СТРОИТЕЛЬСТВО НОВЫХ НИТОК (УЧАСТКОВ) ГАЗОПРОВОДОВ «ГАЗЛИ - САРИМОЙ» И «АКЧАЛОК - ГАЗЛИ - НУКУС» ОБЩЕЙ ПРОТЯЖЕННОСТЬЮ НЕ МЕНЕЕ 275 км».

| Изм. | Кол.уч. | Лист | № док. | Подпись | Дата |
|---|---|---|---|---|---|
| ГИП | | Кирпичников С. | | | 10.2026 |
| Нач.отд. | | Нигманова Н. | | | 10.2026 |
| Исполн. | | Нигманова Н. | | | 10.2026 |
| Н.контр | | Кирпичников С. | | | 10.2026 |

ГАЗОПРОВОД «ГАЗЛИ-САРИМОЙ» (54 км)
Генеральный план и транспорт.

| Стадия | Лист | Листов |
|---|---|---|
| РД | 1 | 1 |

КУП-D5.
План благоустройства территории
М 1:500

EAST WEST ENGINEERING
ООО "EAST-WEST Engineering"
г. Ташкент 2026 г.

Формат / Format A4x3