
N
СЕВЕР

ПЕРЕЧЕНЬ СВАРНЫХ ШВОВ		
№	DN	ТИП
1	1000	INSTRUMENT
2	1000	BUTTWELD
3	1000	BUTTWELD
4	1000	BUTTWELD
5	1000	BUTTWELD
6	1000	BUTTWELD
7	1000	BUTTWELD
8	300	BUTTWELD
9	300	BUTTWELD

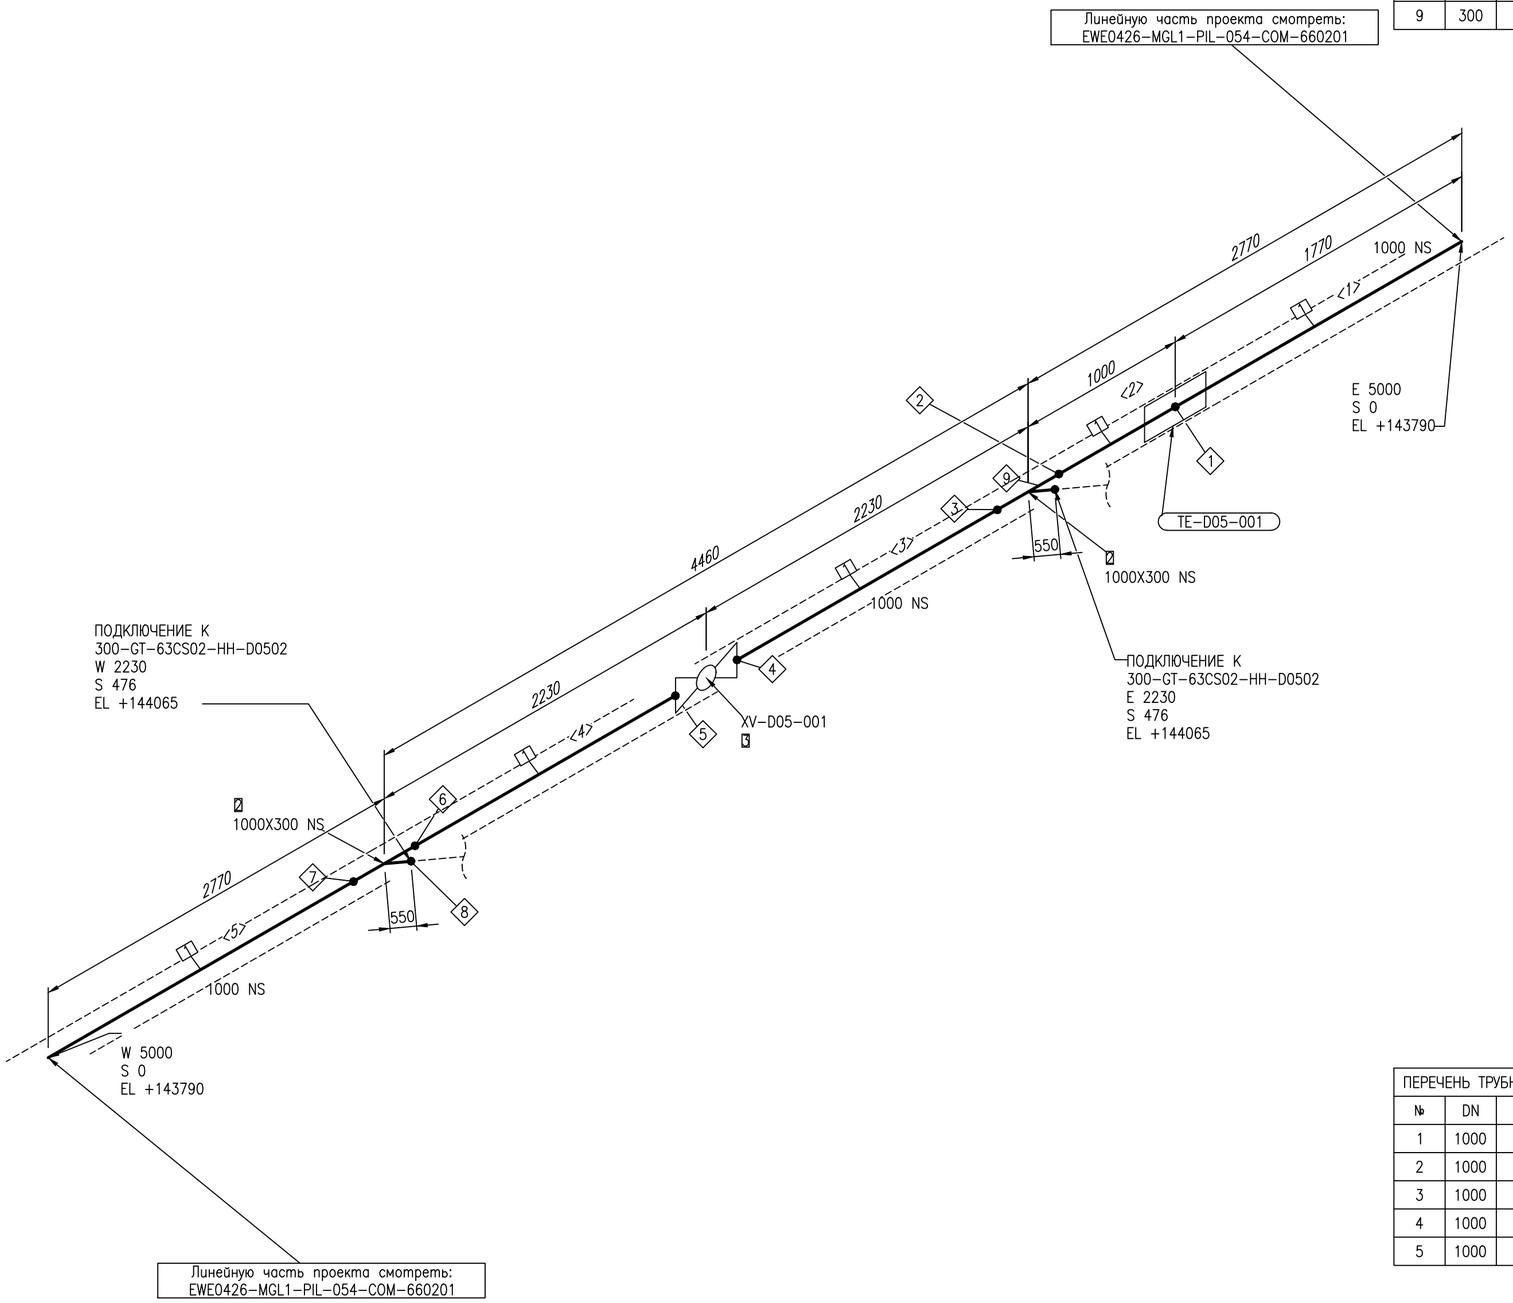

ПЕРЕЧЕНЬ ТРУБНЫХ КАТУШЕК		
№	DN	ДЛИНА
1	1000	1770ММ
2	1000	590ММ
3	1000	859ММ
4	1000	859ММ
5	1000	2360ММ

СПЕЦИФИКАЦИЯ ИЗДЕЛИЙ И МАТЕРИАЛОВ

ПОЗ.	НАИМЕНОВАНИЕ	СТАНДАРТ	КОЛ.	ПРИМЕЧАНИЕ
1	Трубы стальные сварные прямошовные, типа 3, К60, 1020Х10	ГОСТ 31447-2012	6.5М	ТРУБА УЧТЕНА В ЛИНЕЙНОЙ ЧАСТИ ПРОЕКТА
2	Тройник Т I 1020(11К60)-325(10К48)-5,5(6,9)-0,75-30, сталь К60	ТУ 1469-017-38948552-2015	2	
3	Кран шаровой DN1000 PN-6,3 МПа с пневмогидроприводом, приварной, подземный	EWE0426-MGL1-PRE-054-DSH-610124	1	

Трубопровод	ДАННЫЕ ПО ТРУБОПРОВОДУ		
1000-GT-63CS00-HH-D0501	Расчетные параметры	Температура	-26,9...+85 °C
		Давление	6,3 MPa
	Рабочие параметры	Температура	-20...+40 °C
		Давление	5,5 MPa
Ссылочные чертежи No	Параметры испытания	Тип	Гидравлическое
		Давление	6,9 MPa
EWE0426-MGL1-PRE-054-SCM-610107	Изоляция	Тип	HH
		Толщина	mm
	Катодная защита	Да или Нет	Да

Рев.	Дата	Назначение ревизии	Проверил	Утвердил
A1	07.09.2026	Утверждено для строительства		
R1	22.06.2026	Выпущено для рассмотрения		

ЗАКАЗЧИК: UTG ЦЕНТРАЛЬНАЯ АЗИЯ
ГЕНЕРАЛЬНЫЙ ПОДРЯДЧИК: UET
ПОДРЯДЧИК: PBG Pre Build Generation
ГЕНЕРАЛЬНЫЙ ПРОЕКТИРОВЩИК: EAST WEST ENGINEERING

EWE0426-MGL1-PRE-054-ISO-740602-A1

«СТРОИТЕЛЬСТВО НОВЫХ НИТОК (УЧАСТКОВ) ГАЗОПРОВОДОВ «ГАЗЛИ - САРИМОЙ» И «АКЧАЛОК - ГАЗЛИ - НУКУС» ОБЩЕЙ ПРОТЯЖЕННОСТЬЮ НЕ МЕНЕЕ 275 КМ».

Изм.	Кол.уч.	Лист	№док.	Подпись	Дата
ГИП		Кирпичников С.			09.2026
Нач.отд.		Рябинин А.			09.2026
Исполн.		Таштимуров Р.			09.2026
Н.контр		Кирпичников С.			09.2026

ГАЗОПРОВОД «ГАЗЛИ-САРИМОЙ» (54 КМ)
Линейный крановый узел DN1000 КУП-D5

Стадия	Лист	Листов
РД	1	1

Изометрический чертеж трубопровода
1000-GT-63CS00-HH-D0501

ООО "EAST-WEST Engineering"
г. Ташкент 2026г.

Взам. инв. №
Подпись и дата
Инв.№ подл.

Формат А2 594х420