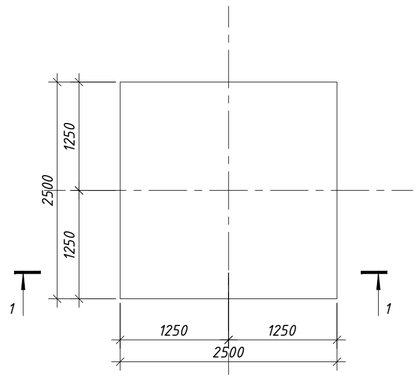
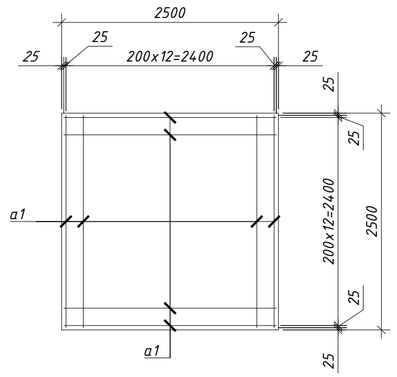
## Фундамент ФОМ1



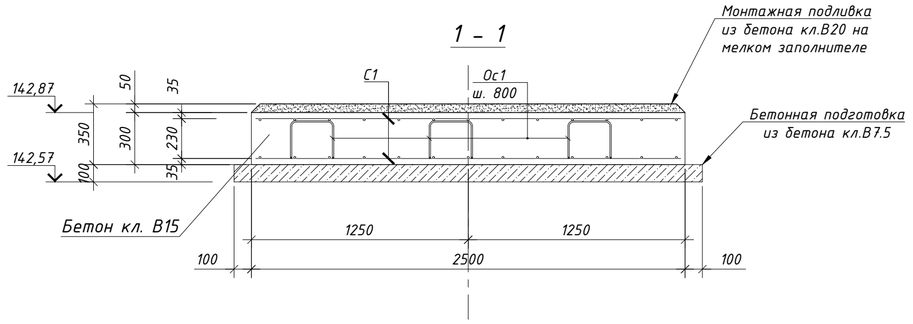

## Сетка С1



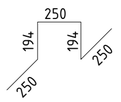

## Спецификация элементов

| Марка Поз. | Обозначение | Наименование | Кол.шт | Масса ед., кг | Прим. |
|---|---|---|---|---|---|
| | | *Фундамент ФОМ1* | | | |
| | | *Сборные единицы* | | | |
| *С1* | *См. данный лист* | *Сетка С1* | *2* | | *113.05* |
| | | *Детали* | | | |
| *Ос1* | *ГОСТ 34028-2016* | *Ф8 А240 L=1138 мм* | *9* | *0.45* | *4.04* |
| | | *Сетка С1* | | | |
| *а1* | *ГОСТ 34028-2016* | *Ф12 А500 L=2450 мм* | *26* | *2.17* | *56.53* |
| | | *Материалы* | | | |
| | *на подливку* | *Бетон кл. В25, W6, F50* | | | *0.32 м³* |
| | | *Бетон кл. В20, W6, F50* | | | *1.88 м³* |
| | *на подготовку* | *Бетон кл. В7.5* | | | *0.73* |
| | | | | | |

## 1 – 1




## Ведомость деталей

| Поз. | Эскиз |
|---|---|
| Ос1 |  |



*Гидроизоляция фундамента из двух слоев полимерного покрытия на основе лака ХП-734 по ГОСТ 52165-2003 толщиной 25 мкм.*

*Примечания:*

1. *Объединение арматурных стержней в плоские сетки или пространственные каркасы выполнять вязальной стальной отожженной проволокой d=0.8-1.0мм. Применение ручной электродуговой сварки не допускается.*
2. *Подливку выполнить из бетона кл. В25 на мелком заполнителе.*
3. *Фундамент ФОМ1 разработан под шаровой кран. Бетонирование выполнять после получения оборудования и сверки с паспортными данными.*
4. *Фиксаторы для крепления двух сеток марки Ос-1 устанавливать в шахматном порядке.*

## Ведомость расхода стали, кг

| Марка элемента | Изделия арматурные | | | | | Общий расход |
|---|---|---|---|---|---|---|
| | Арматура класса | | | | Всего | |
| | А240 | | А500 | | | |
| | ГОСТ 34028-2016 | | ГОСТ 34028-2016 | | | |
| | Ф8 | Итого | Ф12 | Итого | | |
| Фундамент ФОМ1 | 4.19 | 4.19 | 113.05 | 113.05 | 117.24 | 117.24 |

| | | | | |
|---|---|---|---|---|
| *А1* | *09.09.2026* | *Выпущено для строительства* | | |
| *R1* | *24.07.2026* | *Выпущено для рассмотрения* | | |
| *Рев* | *Дата* | *Назначение ревизии* | *Проверил* | *Утвердил* |

ЗАКАЗЧИК: UTG UZTRANSGAZ | ГЕНЕРАЛЬНЫЙ ПОДРЯДЧИК: UET UZBEKENERGOTAMIR | ПОДРЯДЧИК: PBG Pro Build Generation | ГЕНЕРАЛЬНЫЙ ПРОЕКТИРОВЩИК: EAST WEST ENGINEERING

*EWE0426-MGL1-STR-054-DRW-740504-A1*

*«СТРОИТЕЛЬСТВО НОВЫХ НИТОК (УЧАСТКОВ) ГАЗОПРОВОДОВ «ГАЗЛИ – САРИМОЙ» И «АКЧАЛОК – ГАЗЛИ – НУКУС» ОБЩЕЙ ПРОТЯЖЕННОСТЬЮ НЕ МЕНЕЕ 275 КМ».*

| Изм. | Кол.уч. | Лист | № док. | Подпись | Дата |
|---|---|---|---|---|---|
| ГИП | | Кирпичников С. | | | 09.09.26 |
| Нач.отд. | | Каршиев А. | | | 09.09.26 |
| Исполн. | | Юлдашев Ж. | | | 09.09.26 |
| Н.контр | | Кирпичников С. | | | 09.09.26 |

*ГАЗОПРОВОД "ГАЗЛИ-САРИМОЙ" (54 КМ)*
*Линейный крановый узел DN1000 КУП-D5*

| Стадия | Лист | Листов |
|---|---|---|
| РП | 1 | 1 |

*Фундамент ФОМ1*

ООО "EAST-WEST Engineering"
г. Ташкент 2026г.

Взам. инв. №

Подпись и дата

Инв.№ подл.

*Формат / Format A2*