Стойка ограждения Ст1

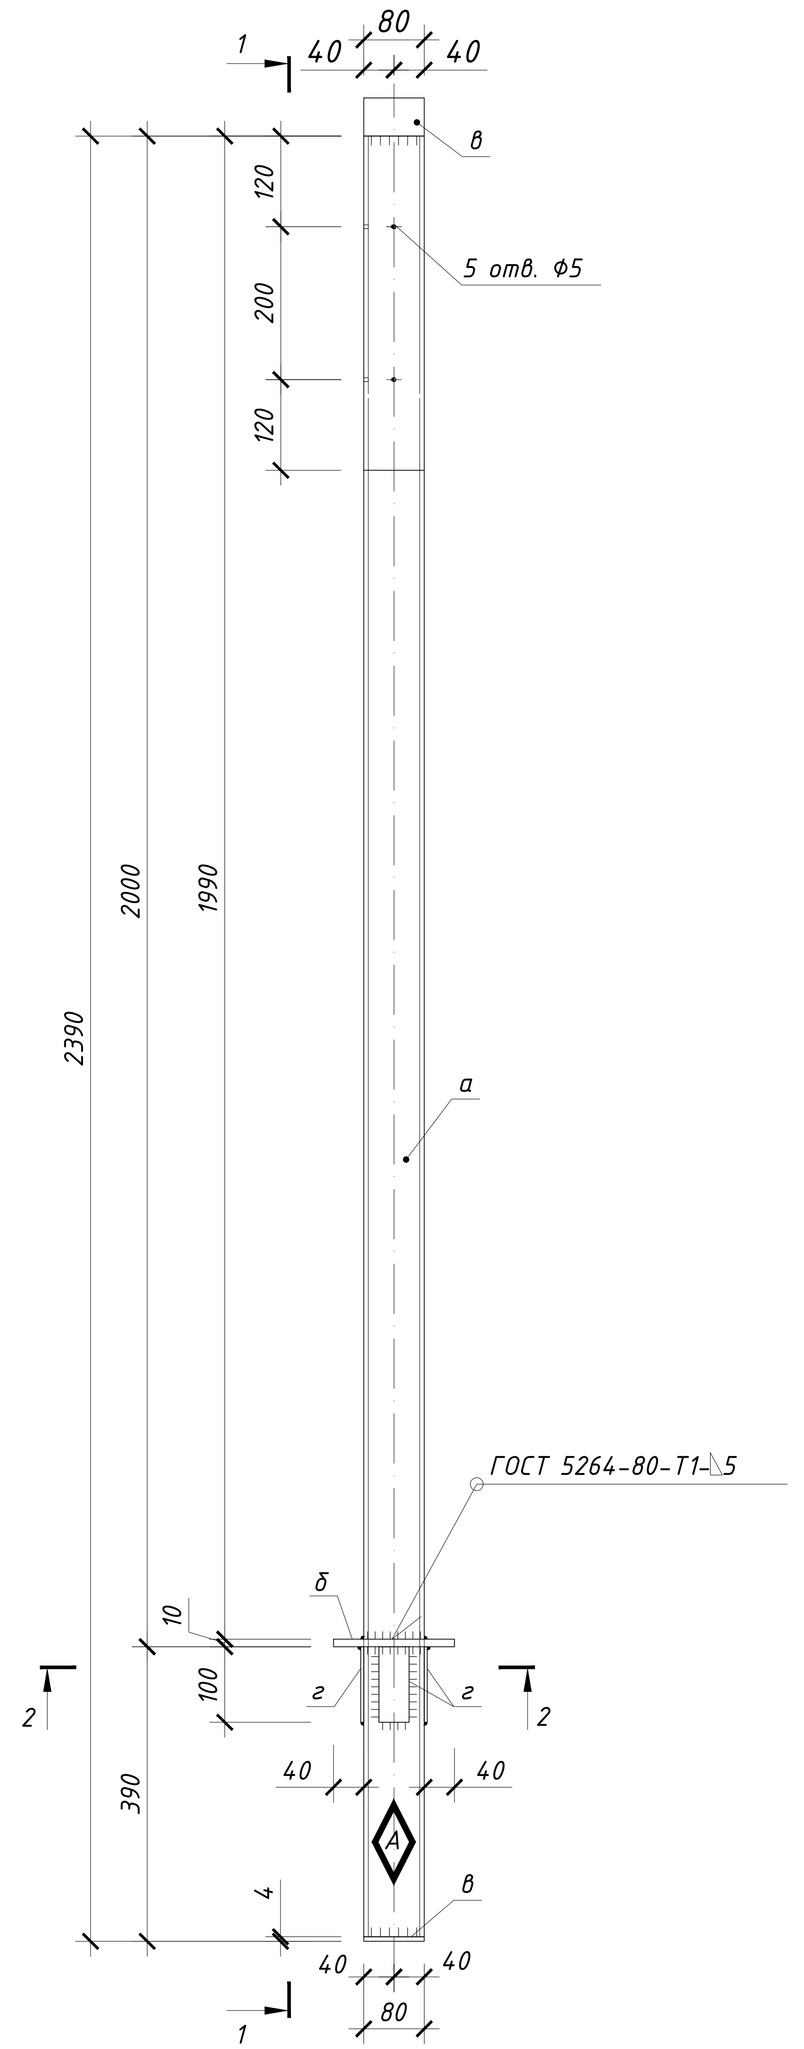

1-1 м 1:10.

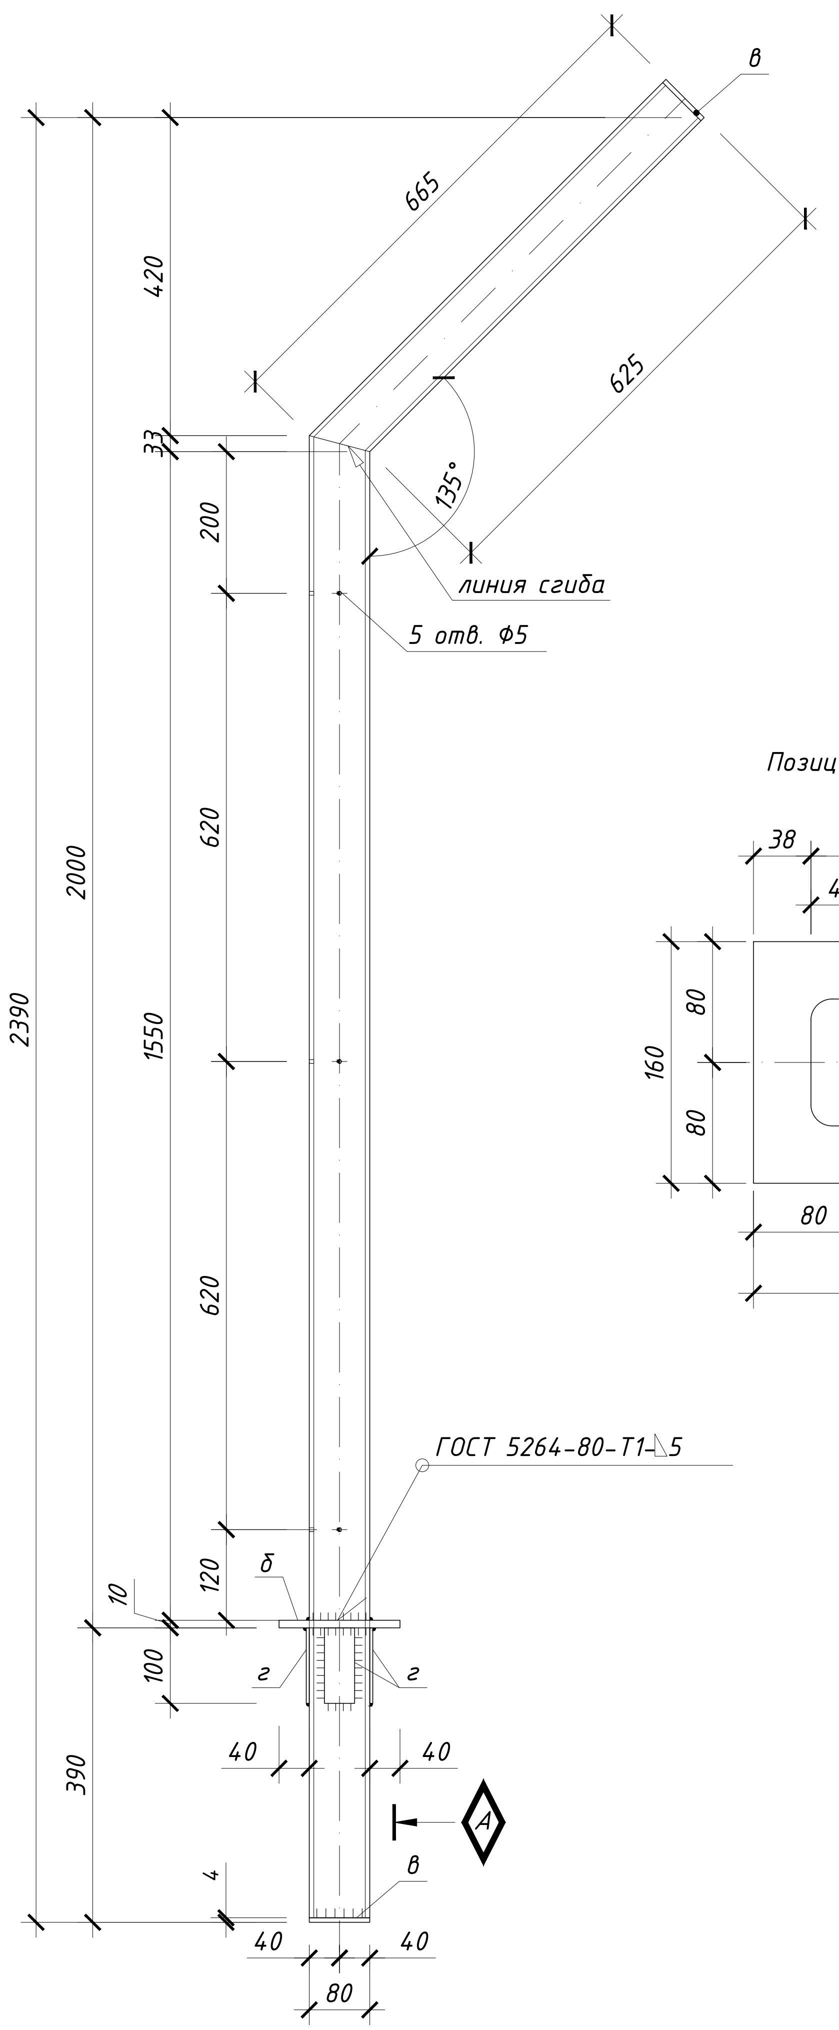

2-2

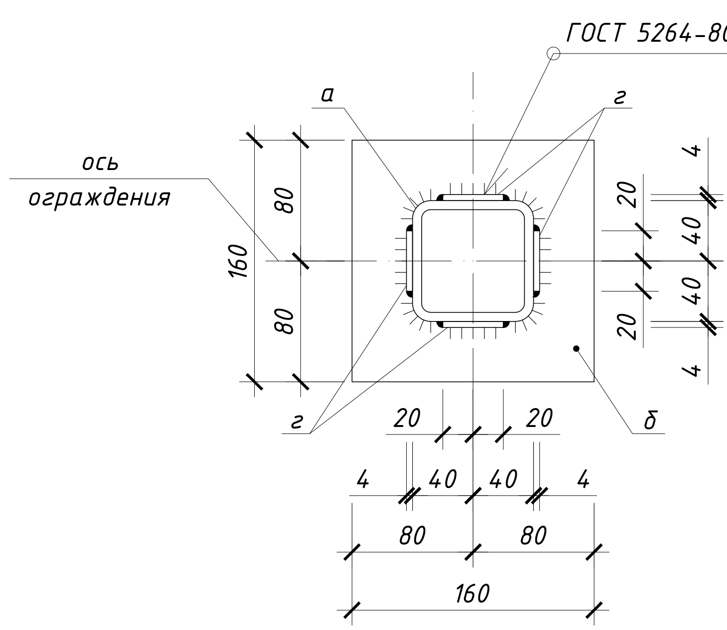

Позиция "б".

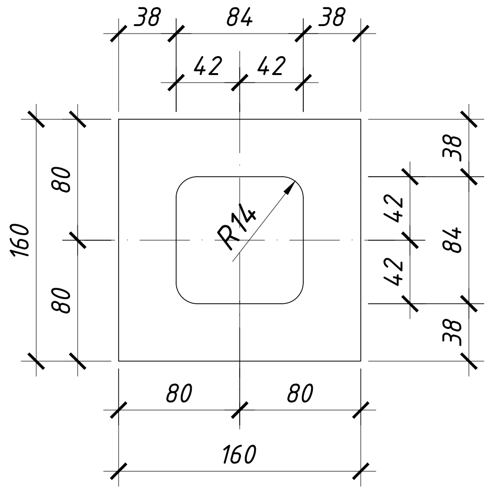

Деталь срезки стойки Ст-1. (поз. а)

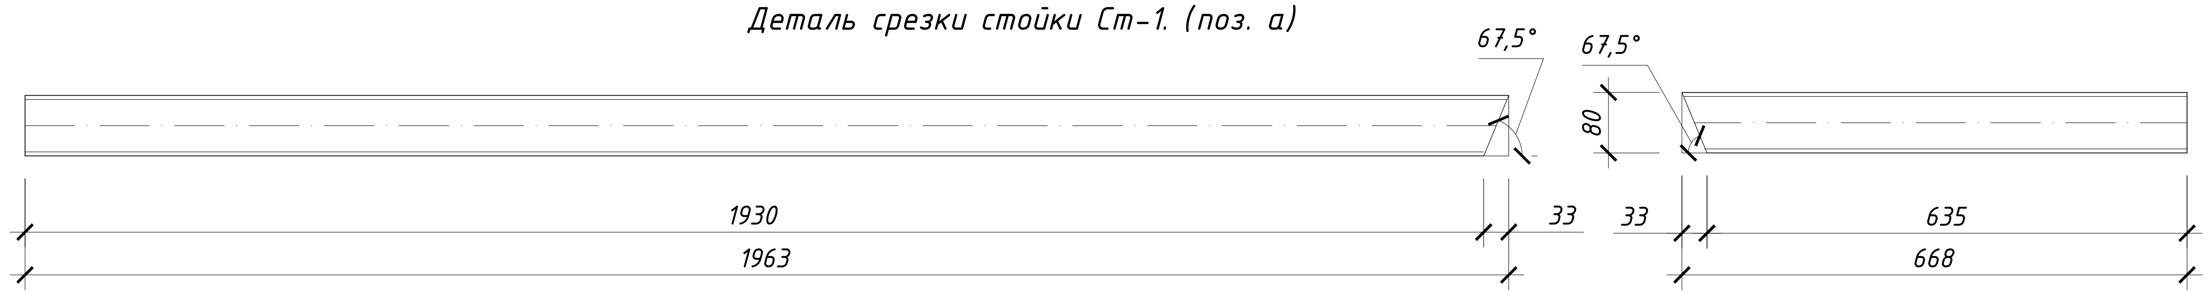

Спецификация элементов на одну марку

Марка поз.	Обозначение	Наименование	Кол. шт.	Масса ед.кг	Примечание
Ст1		Стойка ограждения Ст1		27,6	вес на 1 стойку
а		Гн.пр 80х80х4 ГОСТ 30245-2003 / С255-ГК ГОСТ 27772-2015 L=2631мм	1	24,55	24,55
б		Лист Б-ПН-10х160х160 ГОСТ 19903-2015 / С245-ГК ГОСТ 27772-2015	1	2,01	2,01
в		Лист Б-ПН-4х80х80 ГОСТ 19903-2015 / С245-ГК ГОСТ 27772-2015	2	0,20	0,4
г		Лист Б-ПН-4х40х124 ГОСТ 19903-2015 / С245-ГК ГОСТ 27772-2015	4	0,16	0,64
		Материалы:			
		Окраска металлоконструкций масляной краской за 2 раза			0.95м²

Гн.пр - Гнутые профили

А - Знак ориентации. Нанести несмываемой краской!

Примечания:
1. Сварку вести электродами Э42А ГОСТ 9467-75.
2. Конструкция должна быть покрыта масляной краской за 2 раза по грунтовке.
3. Элемент "г" следует приварить к "а" в первую очередь.
4. Крепления стойки смотри чертёж Фундамента ФМЛ1. (-DRW-740506)

●	Отверстие для болта
◇	Болт постоянный, нормальной точности
◆	Болт временный, нормальной точности
┴┴┴┴┴	Сварной шов заводской
×××××	Сварной шов монтажный

Рев	Дата	Назначение ревизии	Проверил	Утвердил
A1	09.09.2026	Выпущено для строительство		
R1	24.07.2026	Выпущено для рассмотрения		

ЗАКАЗЧИК: UTG UZTRANSGAZ «TRANSGAZINJINIRING»
ГЕНЕРАЛЬНЫЙ ПОДРЯДЧИК: UET UZBEKENERGOTAMIR
ПОДРЯДЧИК: PBG Pro Build Generation
ГЕНЕРАЛЬНЫЙ ПРОЕКТИРОВЩИК: EAST WEST ENGINEERING

EWE0426-MGL1-STR-054-DRW-740508-A1

«СТРОИТЕЛЬСТВО НОВЫХ НИТОК (УЧАСТКОВ) ГАЗОПРОВОДОВ «ГАЗЛИ - САРИМОЙ» И «АКЧАЛОК - ГАЗЛИ - НУКУС» ОБЩЕЙ ПРОТЯЖЕННОСТЬЮ НЕ МЕНЕЕ 275 КМ».

Изм.	Кол.уч.	Лист	№ док.	Подпись	Дата
ГИП		Кирпичников С.			09.09.26
Нач.отд.		Каршиев А.			09.09.26
Исполн.		Юлдашев Ж.			09.09.26
Н.контр		Кирпичников С.			09.09.26

ГАЗОПРОВОД "ГАЗЛИ-САРИМОЙ" (54 КМ)
Линейный крановый узел DN1000 КУП-D5

Стадия	Лист	Листов
РП	1	1

Стойка ограждения Ст1

ООО "EAST-WEST Engineering"
г. Ташкент 2026г.

Формат / Format A4X3

Взам. инв. №
Подпись и дата
Инв.№ подл.