Стойка ограждения Ст2

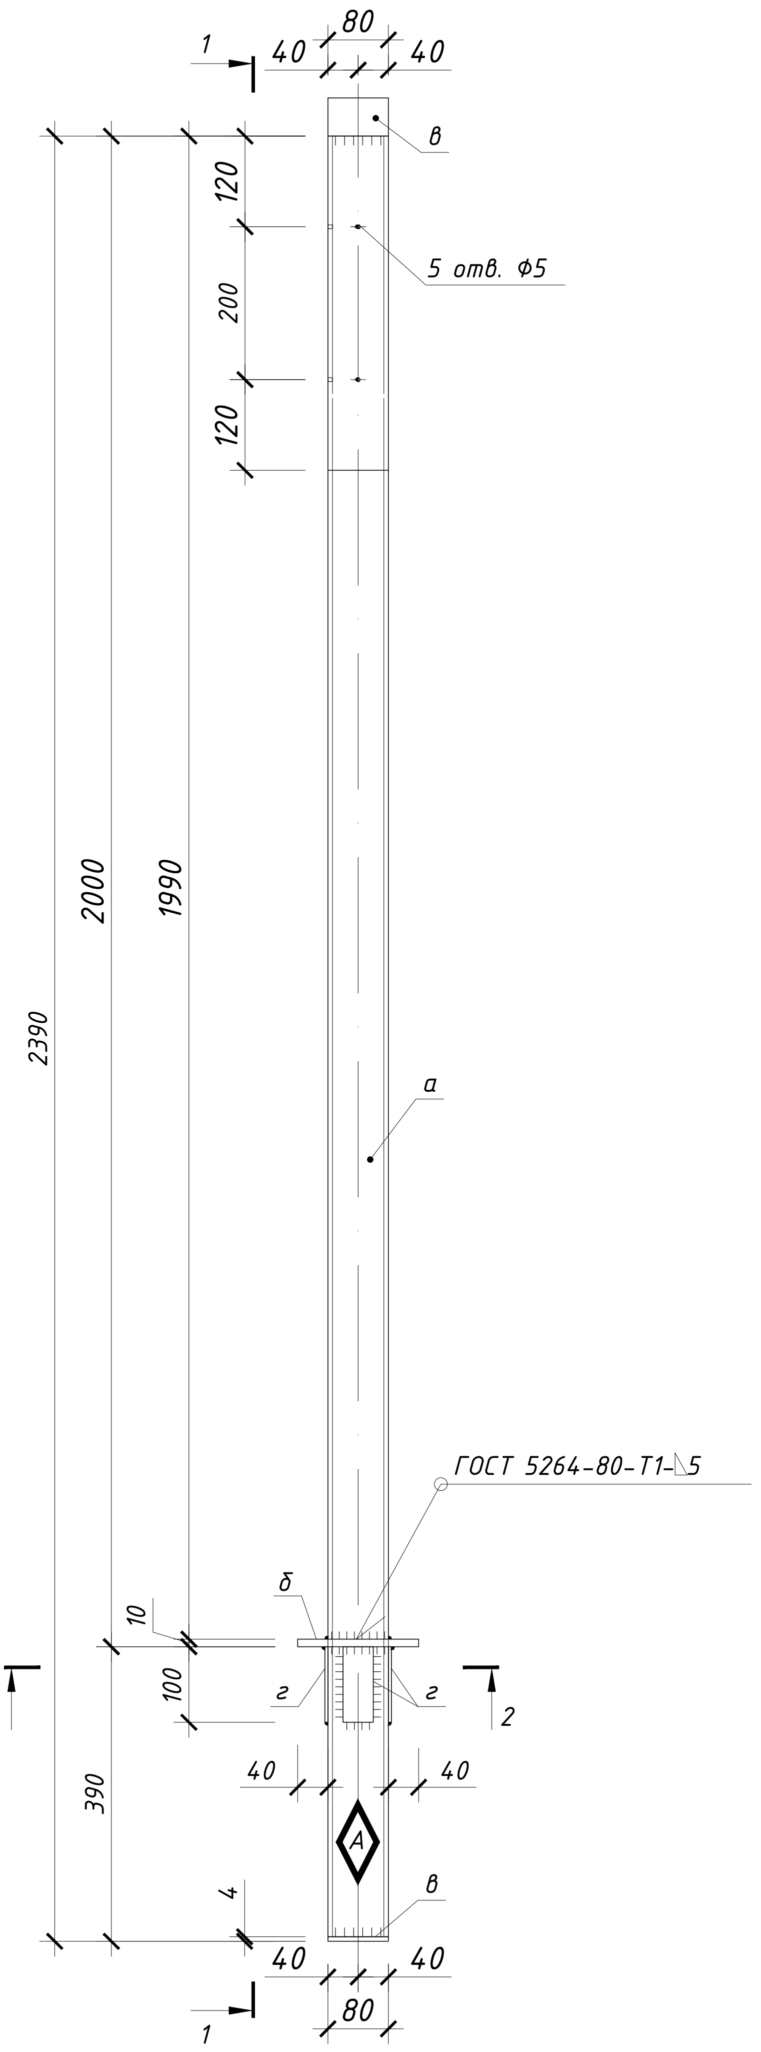

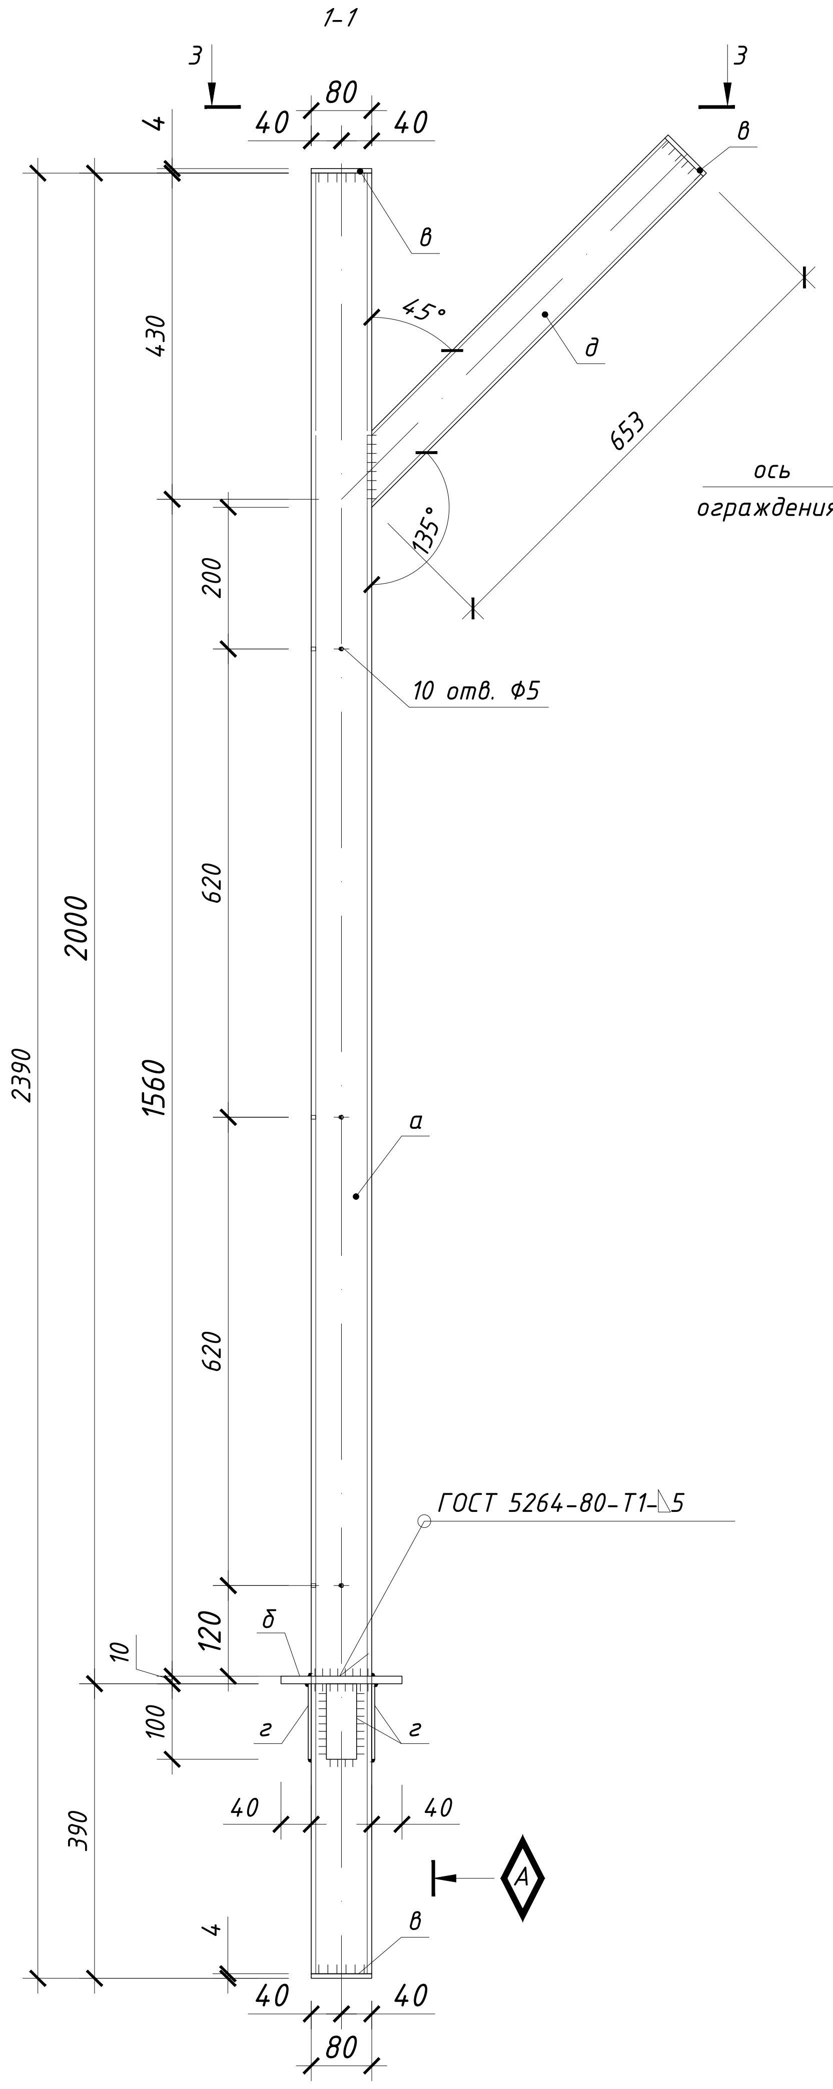

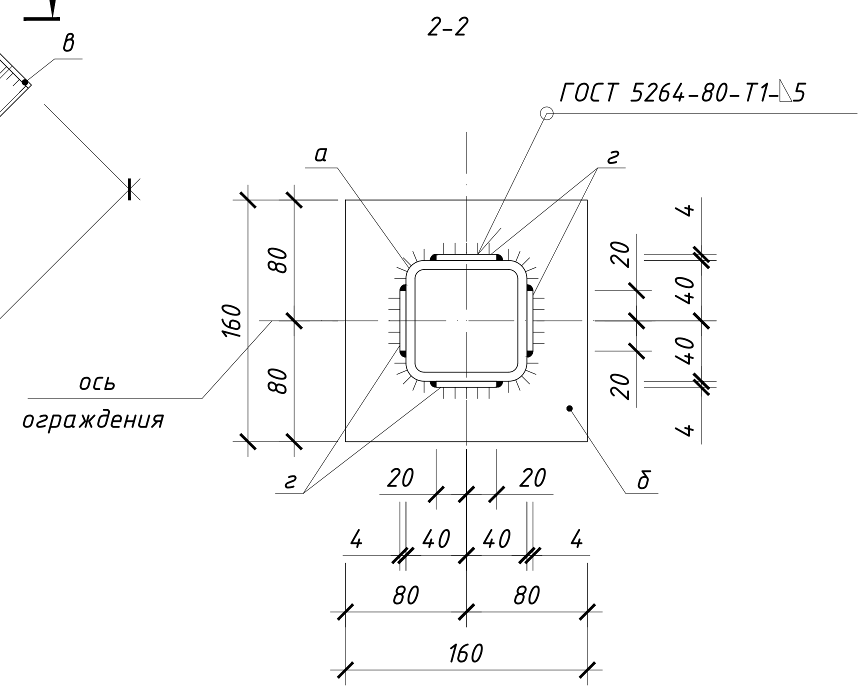

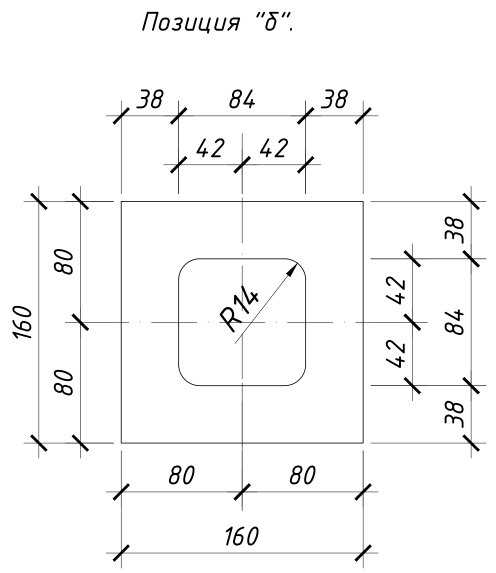

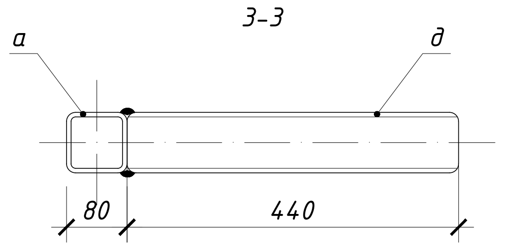

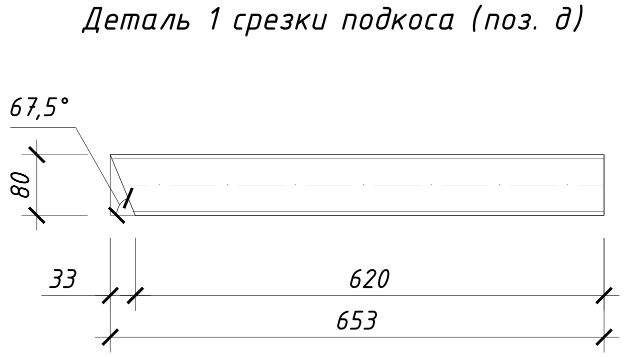

●	Отверстие для болта
⌖	Болт постоянный, нормальной точности
◆	Болт временный, нормальной точности
⁞⁞⁞⁞⁞⁞	Сварной шов заводской
xxxxx	Сварной шов монтажный

Спецификация элементов на одну марку

Марка поз.	Обозначение	Наименование	Кол. шт.	Масса ед.кг	Примечание
Ст2		Стойка ограждения Ст2		31.65	вес на 1 стойку
а*		Гн.пр 80x80x4 ГОСТ 30245-2003 / С255-ГК ГОСТ 27772-2015 L=2390мм	1	22.30	22.30
б		Лист Б-ПН-10x160x160 ГОСТ 19903-2015 / С245-ГК ГОСТ 27772-2015	1	2,01	2,01
в		Лист Б-ПН-4x80x80 ГОСТ 19903-2015 / С245-ГК ГОСТ 27772-2015	3	0,20	0,6
г		Лист Б-ПН-4x40x124 ГОСТ 19903-2015 / С245-ГК ГОСТ 27772-2015	4	0,16	0,64
д*		Гн.пр 80x80x4 ГОСТ 30245-2003 / С255-ГК ГОСТ 27772-2015 L=653мм	1	6.10	6.10
		Материалы:			
		Окраска металлоконструкций масляной краской за 2 раза			1,09м²

*- Гн.пр - Гнутые профили

Примечания:
1. Сварку вести электродами Э42А ГОСТ 9467-75.
2. Конструкция должна быть покрыта масляной краской за 2 раза по грунтовке.
3. Элемент "г" следует приварить к "а" в первую очередь.
4. Деталь-1 - деталь срезки подкоса. (поз. д)
5. Крепления стойки смотри Фундамента ФМЛ1. (-DRW-740506)

◆А - Знак ориентации. Нанести несмываемой краской!

Рев	Дата	Назначение ревизии	Проверил	Утвердил
A1	09.09.2026	Выпущено для строительство		
R1	24.07.2026	Выпущено для рассмотрения		

ЗАКАЗЧИК: UTG UZTRANSGAZ «TRANSGAZINJINIRING»
ГЕНЕРАЛЬНЫЙ ПОДРЯДЧИК: UET UZBEKENERGOTAMIR
ПОДРЯДЧИК: PBG Pro Build Generation
ГЕНЕРАЛЬНЫЙ ПРОЕКТИРОВЩИК: EAST WEST ENGINEERING

EWE0426-MGL1-STR-054-DRW-740509-A1

«СТРОИТЕЛЬСТВО НОВЫХ НИТОК (УЧАСТКОВ) ГАЗОПРОВОДОВ «ГАЗЛИ - САРИМОЙ» И «АКЧАЛОК - ГАЗЛИ - НУКУС» ОБЩЕЙ ПРОТЯЖЕННОСТЬЮ НЕ МЕНЕЕ 275 КМ».

Изм.	Кол.уч.	Лист	№ док.	Подпись	Дата
ГИП		Кирпичников С.			09.09.26
Нач.отд.		Каршиев А.			09.09.26
Исполн.		Юлдашев Ж.			09.09.26
Н.контр		Кирпичников С.			09.09.26

ГАЗОПРОВОД "ГАЗЛИ-САРИМОЙ" (54 КМ)
Линейный крановый узел DN1000 КУП-D5

Стадия	Лист	Листов
РП	1	1

Стойка ограждения Ст2

ООО "EAST-WEST Engineering"
г. Ташкент 2026г.

Формат / Format A4X3

Взам. инв. №
Подпись и дата
Инв.№ подл.