Стойка ограждения Ст3

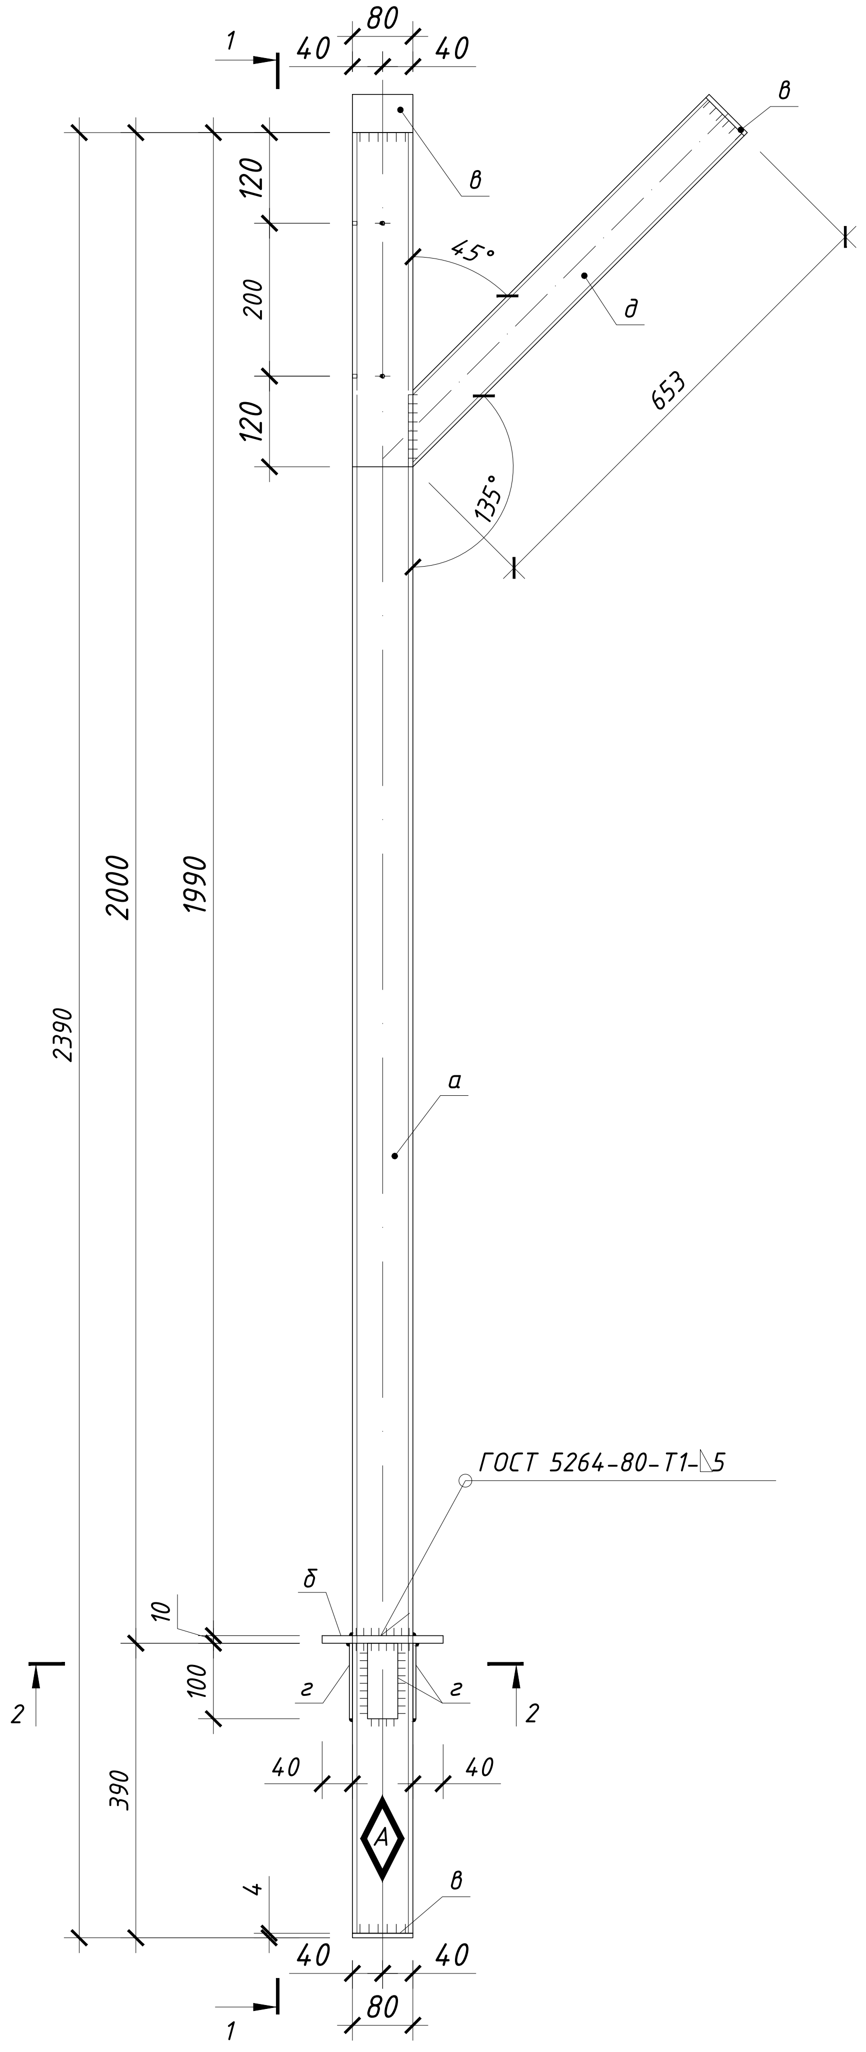

1-1

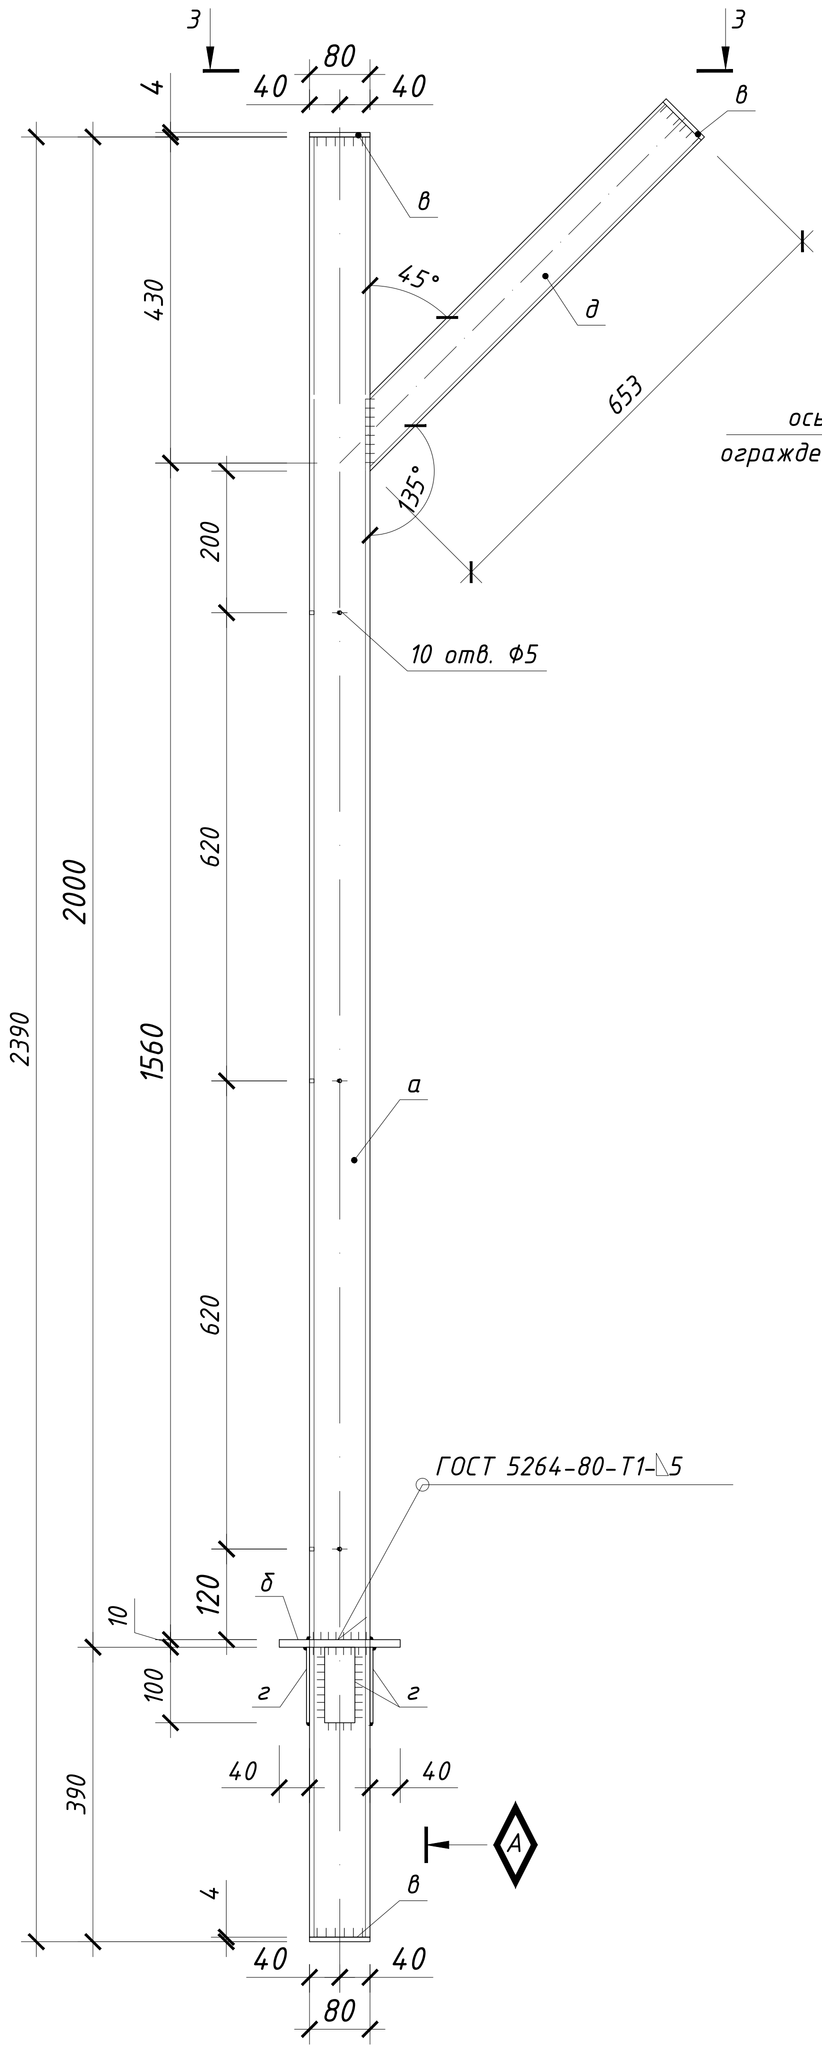

2-2

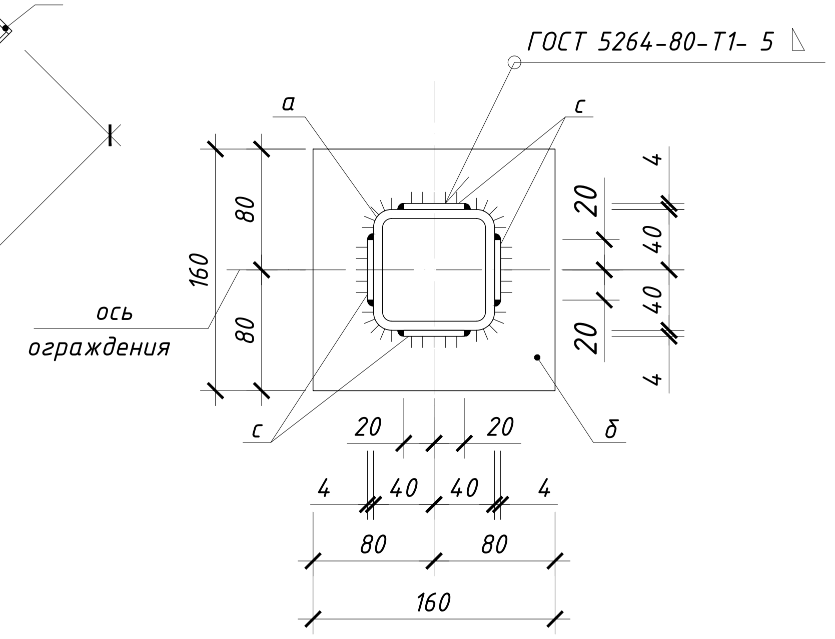

Позиция "б"

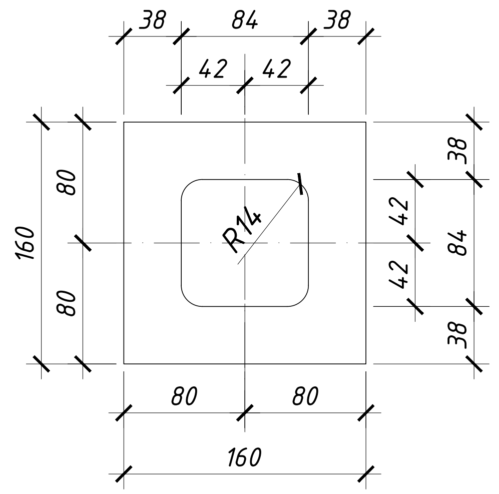

3-3

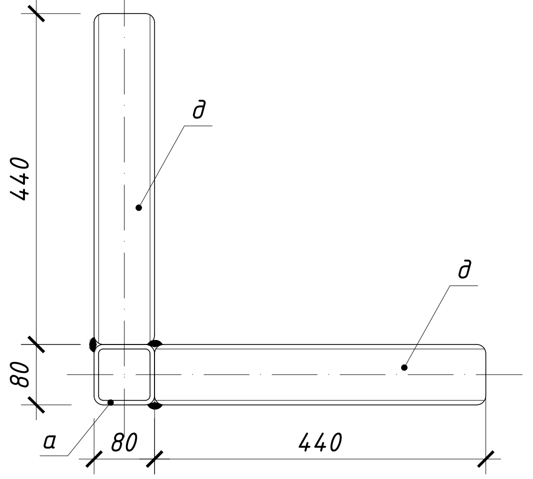

Деталь-1 срезки подкоса (поз. д)

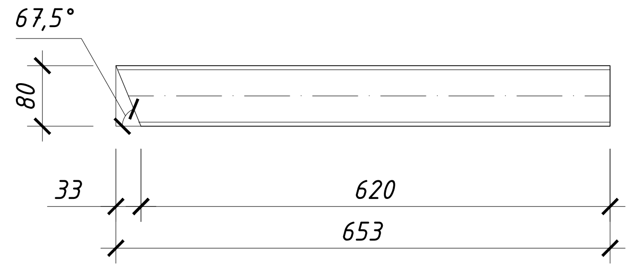

Спецификация элементов на одну марку

Марка поз.	Обозначение	Наименование	Кол. шт.	Масса ед.кг	Примечание
Ст3		Стойка ограждения Ст-3		37.95	вес на 1 стойку
а		Гн.пр $\frac{\text{80x80x4 ГОСТ 30245-2003}}{\text{С255-ГК ГОСТ 27772-2015}}$ L=2390мм	1	22.3	22.3
б		Лист $\frac{\text{Б-ПН-10x160x160 ГОСТ 19903-2015}}{\text{С245-ГК ГОСТ 27772-2015}}$	1	2,01	2,01
в		Лист $\frac{\text{Б-ПН-4x80x80 ГОСТ 19903-2015}}{\text{С245-ГК ГОСТ 27772-2015}}$	4	0,20	0,8
г		Лист $\frac{\text{Б-ПН-4x40x124 ГОСТ 19903-2015}}{\text{С245-ГК ГОСТ 27772-2015}}$	4	0,16	0,64
д		Гн.пр $\frac{\text{80x80x4 ГОСТ 30245-2003}}{\text{С255-ГК ГОСТ 27772-2015}}$ L=653мм	2	6.10	12.20
		Материалы:			
		Окраска металлоконструкций масляной краской за 2 раза			1,31м²

*- Гн.пр - Гнутые профили

Примечания:
1. Сварку вести электродами Э42А ГОСТ 9467-75.
2. Конструкция должна быть покрыта масляной краской за 2 раза по грунтовке.
3. Элемент "г" следует приварить к "а" в первую очередь.
4. Деталь-1 - деталь срезки подкоса (поз. д)
5. Крепления стойки смотри лист Фундамента ФМЛ1. (-DRW-740506)

◊A - Знак ориентации. Нанести несмываемой краской!

● Отверстие для болта
⊕ Болт постоянный, нормальной точности
♦ Болт временный, нормальной точности
┴┴┴┴┴ Сварной шов заводской
xxxxx Сварной шов монтажный

Рев	Дата	Назначение ревизии	Проверил	Утвердил
A1	09.09.2026	Выпущено для строительство		
R1	24.07.2026	Выпущено для рассмотрения		

ЗАКАЗЧИК: UTG UZTRANSGAZ «TRANSGAZINJINIRING»
ГЕНЕРАЛЬНЫЙ ПОДРЯДЧИК: UET UZBEKENERGOTAMIR
ПОДРЯДЧИК: PBG Pro Build Generation
ГЕНЕРАЛЬНЫЙ ПРОЕКТИРОВЩИК: EAST WEST ENGINEERING

EWE0426-MGL1-STR-054-DRW-740510-A1

«СТРОИТЕЛЬСТВО НОВЫХ НИТОК (УЧАСТКОВ) ГАЗОПРОВОДОВ «ГАЗЛИ - САРИМОЙ» И «АКЧАЛОК - ГАЗЛИ - НУКУС» ОБЩЕЙ ПРОТЯЖЕННОСТЬЮ НЕ МЕНЕЕ 275 КМ».

Изм.	Кол.уч.	Лист	№ док.	Подпись	Дата
ГИП		Кирпичников С.			09.09.26
Нач.отд.		Каршиев А.			09.09.26
Исполн.		Юлдашев Ж.			09.09.26
Н.контр		Кирпичников С.			09.09.26

ГАЗОПРОВОД "ГАЗЛИ-САРИМОЙ" (54 КМ)
Линейный крановый узел DN1000 КУП-D5

Стадия	Лист	Листов
РП	1	1

Стойка ограждения Ст3.

ООО "EAST-WEST Engineering"
г. Ташкент 2026г.

Взам. инв. №
Подпись и дата
Инв.№ подл.

Формат / Format A4X3