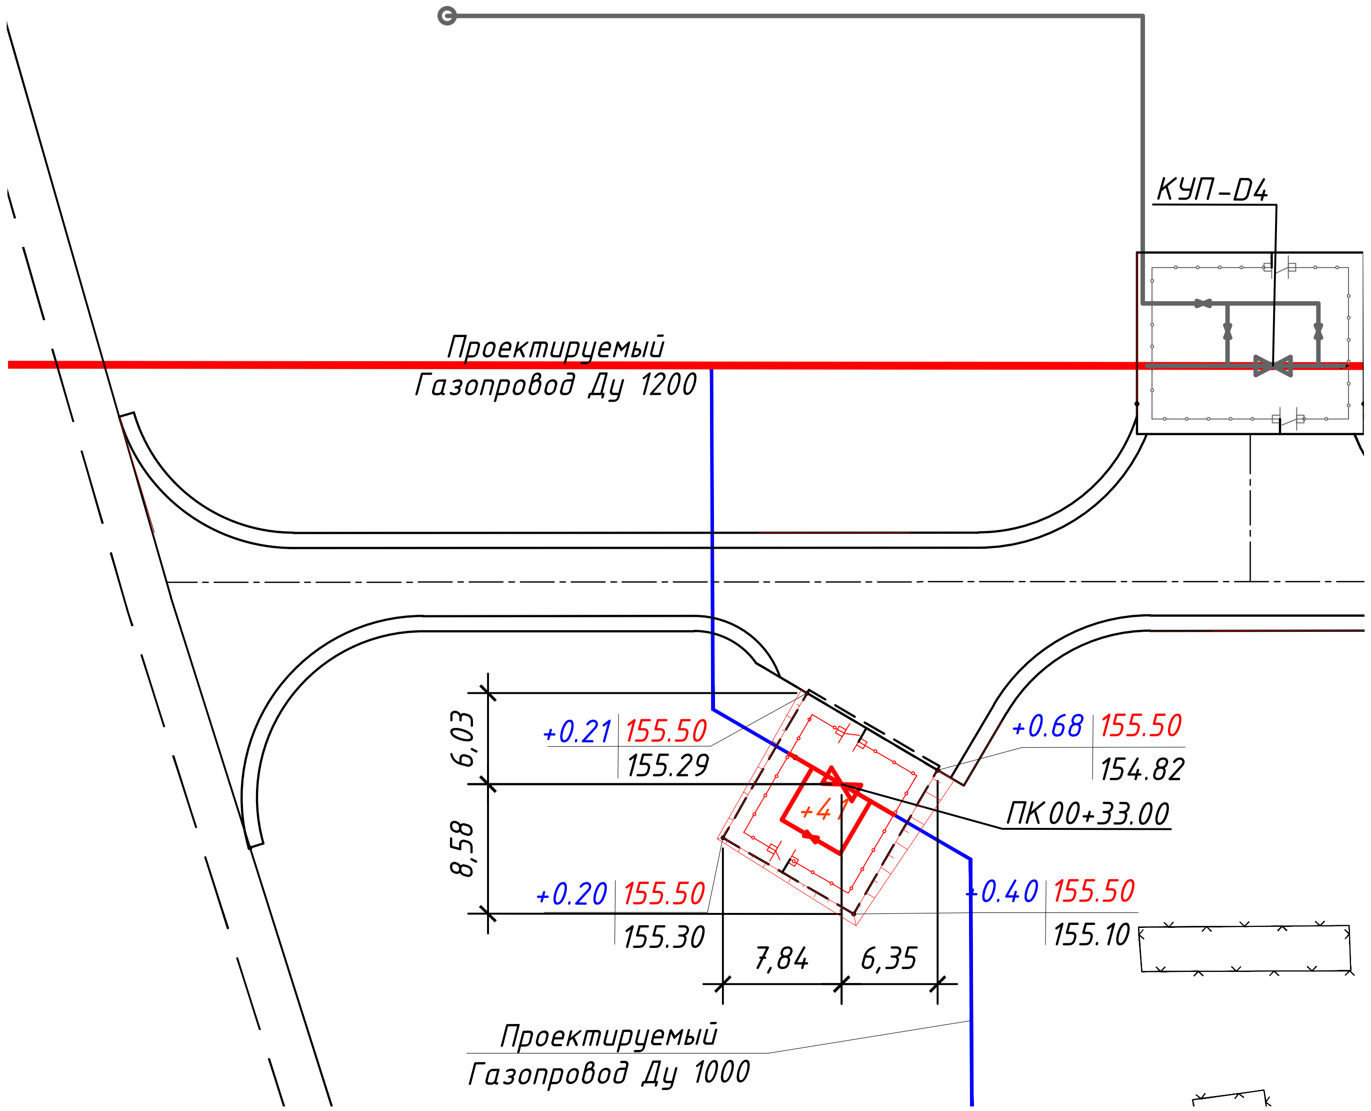

Итого,м3			Всего,м3	
	Насыпь (+)	+41		+41
	Выемка (-)	--		--

Примечания:

При составлении настоящего чертежа были использованы :

1. Сетка картограммы привязана линейно к пикету ПК 00+33.00.
2. Сетка квадратов объёмы земляных масс разбита на ячейки размерами 10х10м.
3. Производство земляных работ вести в соответствии с требованиями ҚР 02.01.
4. План земляных масс кранового узла КУП-Д4 и подъездной дороги см. EWE0426-MGL1-GLT-054-DRW-730104.

Условные обозначения:

+41	объем насыпи в м^3
+0.20 | 155.50 155.30	рабочая отм. | проектная отм. отм.сущ.рельефа
┴┴┴┴┴┴┴┴	откосы насыпи

Ведомость объемов земляных масс

Наименование грунта	Количество, м^3		Примечание
	Насыпь (+)	Выемка (-)	
1. Грунт планировки территории	41	--	
2. Вытесненный грунт, в т.ч. при устройстве:			
а) автодорожных покрытий			
б) покрытий площадок		9	
в) плодородной почвы на участках насыпи			
г) плодородной почвы на участках выемки			
3. Замена растительного грунта на участках насыпи			
4. Грунт для устройства откосов насыпи	5		
5. Грунт для устройства откосов выемки			
6. Поправка на уплотнение	4.6		
Всего пригодного грунта	50.6	9	
7. Недостаток пригодного грунта		41.6	
8. Плодородный грунт, всего в т.ч.:		33	
а) Используемый для озеленения территории			
б) Избыток плодородного грунта	33		
(рекультивация земель)			
9. Итого перерабатываемого грунта	83.6	83.6	

* С учетом плодородного грунта.

** В карьере. Общая площадь картограммы = 110 м2

Рев.	Дата	Назначение ревизии	Проверил	Утвердил
A1	08.09.2026	Выпущено для строительства		
R1	28.07.2026	Выпущено для рассмотрения		

ЗАКАЗЧИК: UTG UZTRANSGAZ
ГЕНЕРАЛЬНЫЙ ПОДРЯДЧИК: UET UZBEKENERGOTAMIR
ПОДРЯДЧИК: PBG Pro Build Generation
ГЕНЕРАЛЬНЫЙ ПРОЕКТИРОВЩИК: EAST WEST ENGINEERING

EWE0426-MGL1-GLT-054-DRW-760104-A1

«СТРОИТЕЛЬСТВО НОВЫХ НИТОК (УЧАСТКОВ) ГАЗОПРОВОДОВ «ГАЗЛИ - САРИМОЙ» И «АКЧАЛОК - ГАЗЛИ - НУКУС» ОБЩЕЙ ПРОТЯЖЕННОСТЬЮ НЕ МЕНЕЕ 275 км».

Изм.	Кол.уч.	Лист	№ док.	Подпись	Дата
ГИП		Схабицкий А.			09.2026
Нач.отд.		Нигманова Н.			09.2026
Исполн.		Нигманова Н.			09.2026
Н.контр		Схабицкий А.			09.2026

ГАЗОПРОВОД «ГАЗЛИ-САРИМОЙ» (54 км)
Генеральный план и транспорт.

Стадия	Лист	Листов
РД	1	1

КУП-Д7.
План земляных масс М 1:500

ООО "EAST-WEST Engineering"
г. Ташкент 2026г.

Взам. инв. №
Подпись и дата
Инв. № подл

Формат / Format A3