## СПЕЦИФИКАЦИЯ ИЗДЕЛИЙ И МАТЕРИАЛОВ

| ПОЗ. | НАИМЕНОВАНИЕ | СТАНДАРТ | КОЛ. | ПРИМЕЧАНИЕ |
|---|---|---|---|---|
| 1 | Трубы стальные бесшовные горячедеформированные 09Г2С, 325Х10 | ТУ 14-3-1128-2000 | 7.8М | |
| 2 | Отвод ОК I 30-325(10К48)-5,5(6,9)-0,75-1,5DN-30, сталь 09Г2С | ТУ 1469-017-38948552-2015 | 2 | |
| 3 | Отвод ОК I 90-325(10К48)-5,5(6,9)-0,75-1,5DN-30, сталь 09Г2С | ТУ 1469-017-38948552-2015 | 2 | |
| 4 | Тройник Т I 325(10К48)-114(5К48)-5,5(6,9)-0,75-30, сталь 09Г2С | ТУ 1469-017-38948552-2015 | 2 | |
| 5 | Кран шаровой DN300 PN-6,3 МПа с пневмогидроприводом, приварной, подземный | EWE0426-MGL1-PRE-054-DSH -610124 | 1 | |

## ПЕРЕЧЕНЬ СВАРНЫХ ШВОВ

| № | DN | ТИП |
|---|---|---|
| 1 | 100 | BUTTWELD |
| 2 | 300 | BUTTWELD |
| 3 | 300 | BUTTWELD |
| 4 | 300 | BUTTWELD |
| 5 | 300 | BUTTWELD |
| 6 | 300 | BUTTWELD |
| 7 | 300 | BUTTWELD |
| 8 | 300 | BUTTWELD |
| 9 | 300 | BUTTWELD |
| 10 | 300 | BUTTWELD |
| 11 | 300 | BUTTWELD |
| 12 | 300 | BUTTWELD |
| 13 | 300 | BUTTWELD |
| 14 | 300 | BUTTWELD |
| 15 | 300 | BUTTWELD |

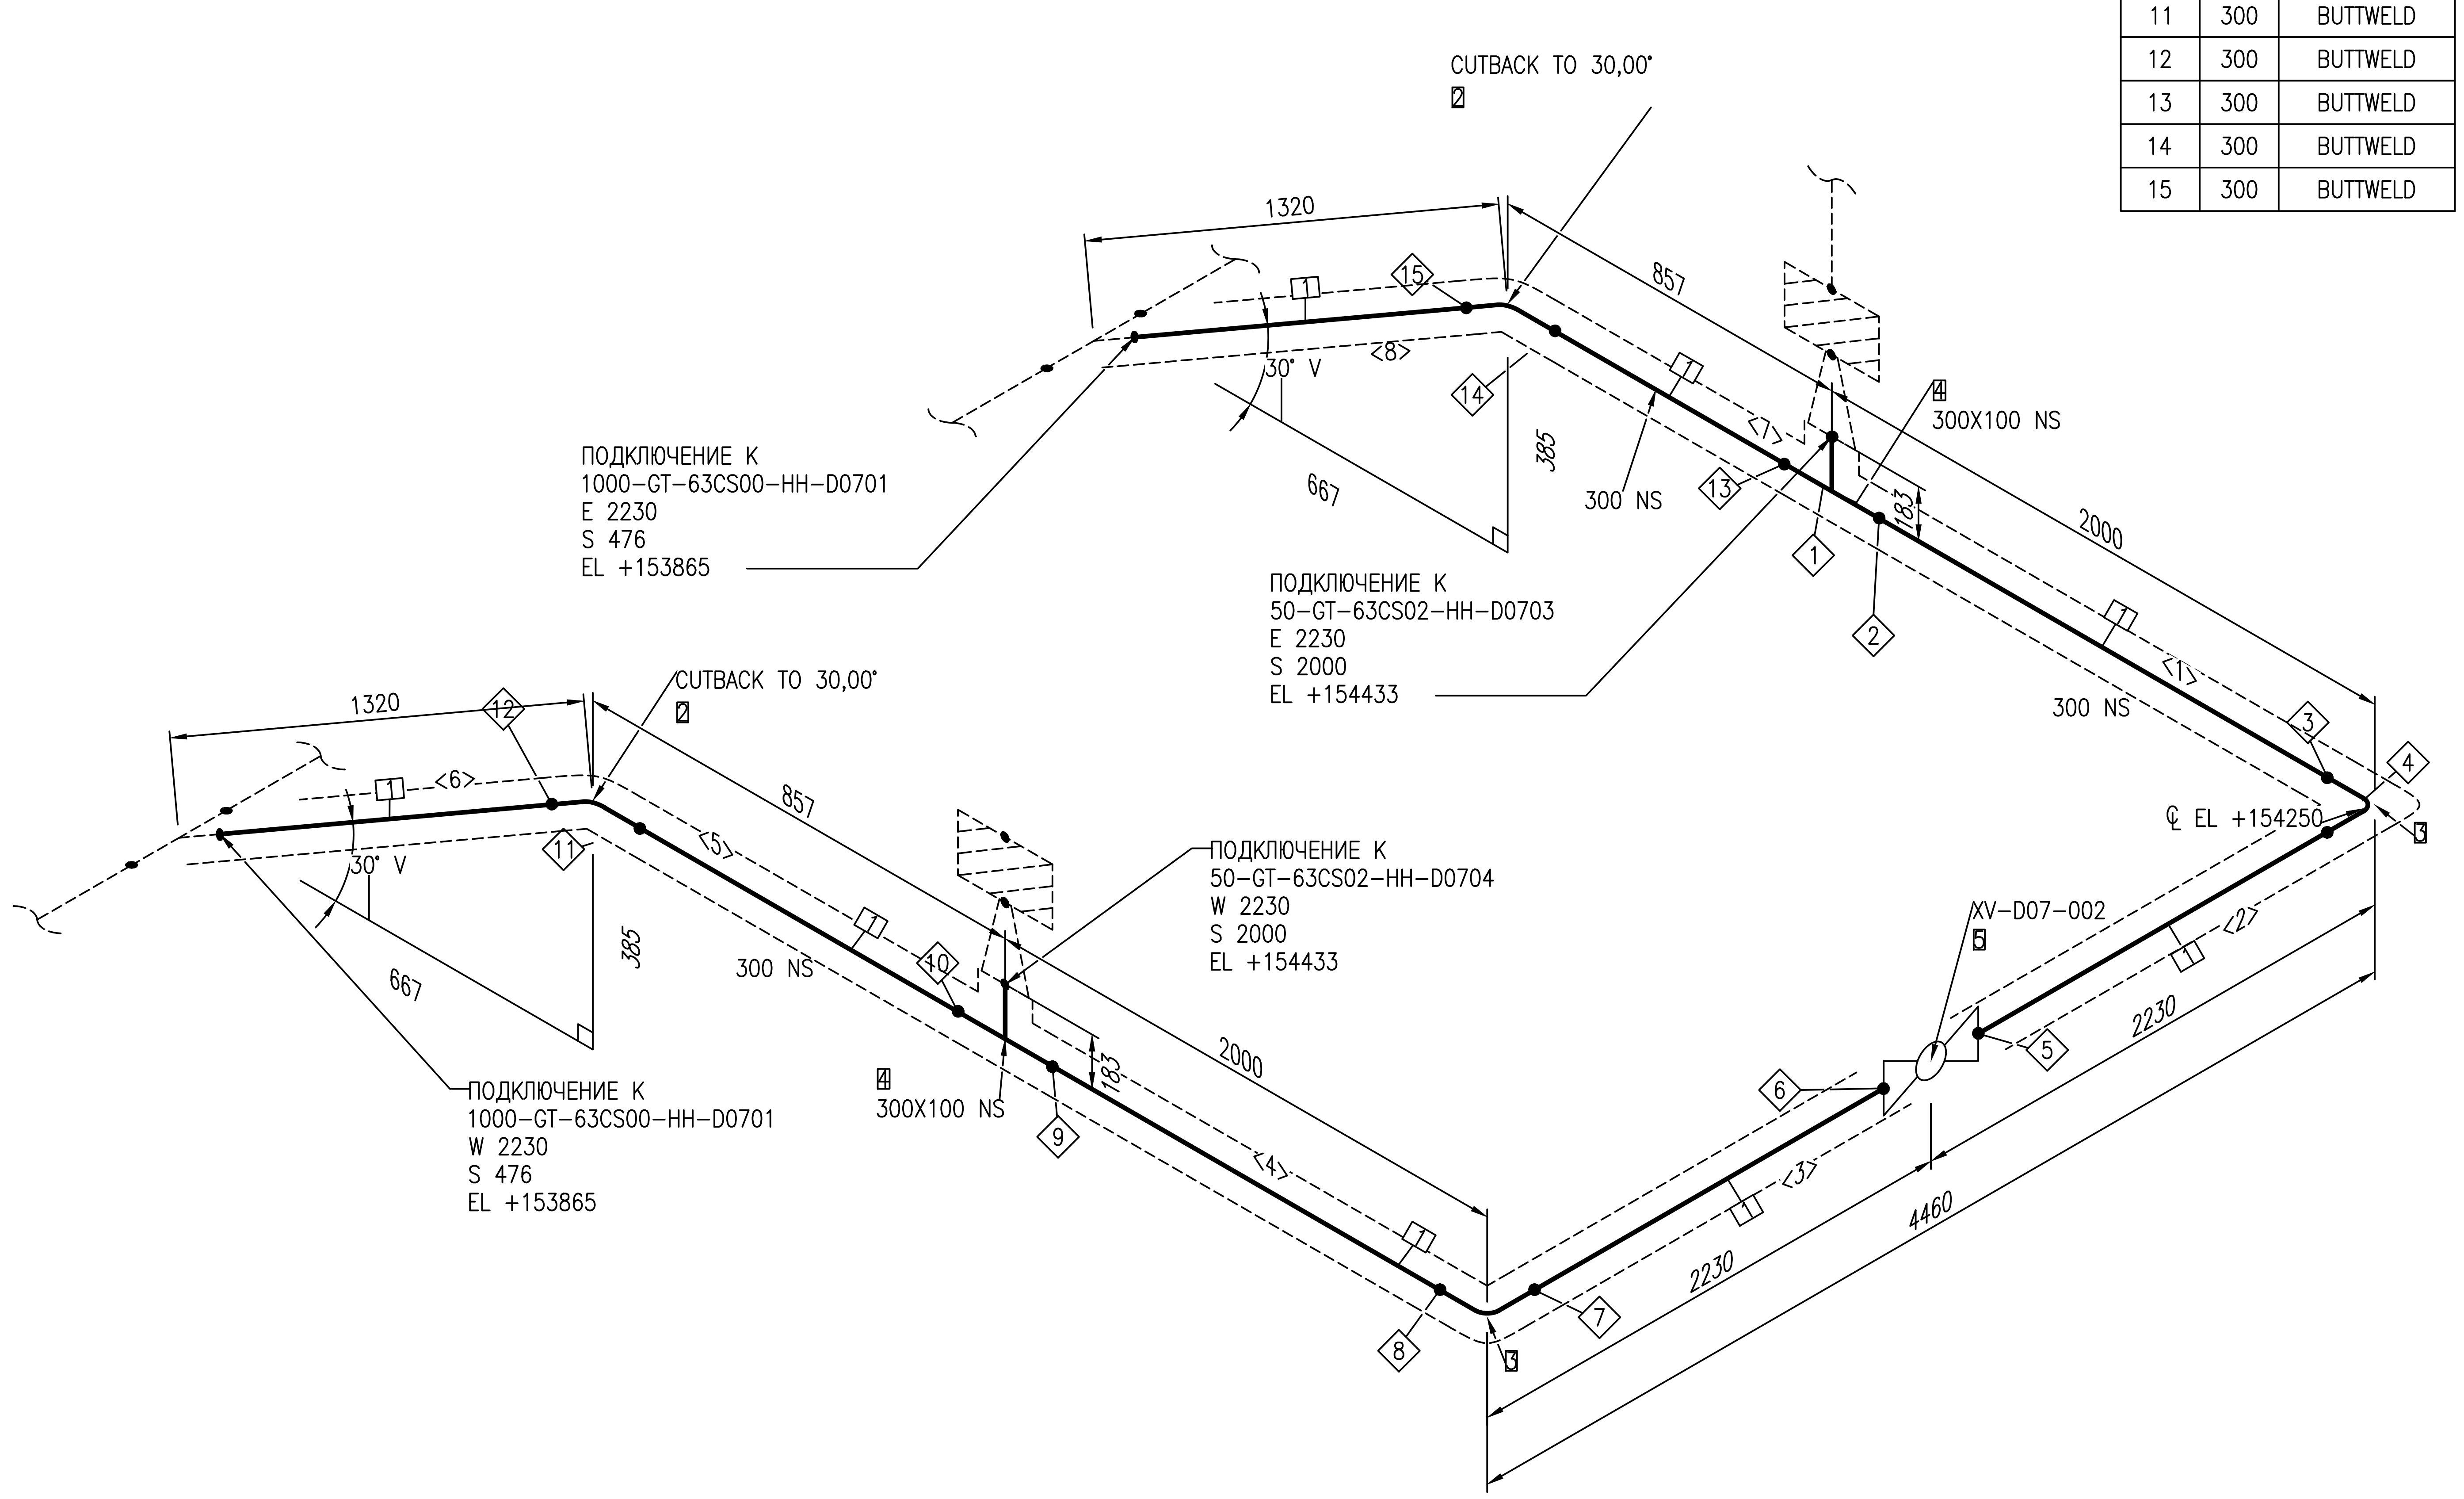
CUTBACK TO 30,00°
2
1320
857
15
1
<8>
30° V
14
385
667
300 NS
13
<7>
4
300X100 NS
183
1
2
2000
<1>
300 NS
3
4
3
℄ EL +154250
ПОДКЛЮЧЕНИЕ К
1000-GT-63CS00-HH-D0701
E 2230
S 476
EL +153865
ПОДКЛЮЧЕНИЕ К
50-GT-63CS02-HH-D0703
E 2230
S 2000
EL +154433
CUTBACK TO 30,00°
2
1320
12
1
<6>
11
30° V
385
667
857
<5>
300 NS
10
ПОДКЛЮЧЕНИЕ К
50-GT-63CS02-HH-D0704
W 2230
S 2000
EL +154433
4
300X100 NS
183
9
2000
<4>
8
3
7
ПОДКЛЮЧЕНИЕ К
1000-GT-63CS00-HH-D0701
W 2230
S 476
EL +153865
XV-D07-002
5
6
5
<3>
<2>
2230
2230
4460

## ПЕРЕЧЕНЬ ТРУБНЫХ КАТУШЕК

| № | DN | ДЛИНА |
|---|---|---|
| 1 | 300 | 1330ММ |
| 2 | 300 | 1362ММ |
| 3 | 300 | 1362ММ |
| 4 | 300 | 1330ММ |
| 5 | 300 | 517ММ |
| 6 | 300 | 650ММ |
| 7 | 300 | 517ММ |
| 8 | 300 | 650ММ |

| Трубопровод | ДАННЫЕ ПО ТРУБОПРОВОДУ | | |
|---|---|---|---|
| 300-GT-63CS02-HH-D0702 | Расчетные параметры | Температура | -26,9...+85 °C |
| | | Давление | 6,3 MPa |
| | Рабочие параметры | Температура | -20...+40 °C |
| | | Давление | 5,5 MPa |
| | Параметры испытания | Тип | Гидравлическое |
| Ссылочные чертежи No | | Давление | 6,9 MPa |
| EWE0426-MGL1-PRE-054-SCM-610109 | Изоляция | Тип | HH |
| | | Толщина | mm |
| | Катодная защита | Да или Нет | Да |

| Рев. | Дата | Назначение ревизии | Проверил | Утвердил |
|---|---|---|---|---|
| A1 | 07.09.2026 | Утверждено для строительства | | |
| R1 | 22.06.2026 | Выпущено для рассмотрения | | |

ЗАКАЗЧИК: UTG UZTRANSGAZ

ГЕНЕРАЛЬНЫЙ ПОДРЯДЧИК: UET UZBEKENERGOTAMIR

ПОДРЯДЧИК: PBG Pre Build Generation

ГЕНЕРАЛЬНЫЙ ПРОЕКТИРОВЩИК: EAST WEST ENGINEERING

# EWE0426-MGL1-PRE-054-ISO-760603-A1

«СТРОИТЕЛЬСТВО НОВЫХ НИТОК (УЧАСТКОВ) ГАЗОПРОВОДОВ «ГАЗЛИ - САРИМОЙ» И «АКЧАЛОК - ГАЗЛИ - НУКУС» ОБЩЕЙ ПРОТЯЖЕННОСТЬЮ НЕ МЕНЕЕ 275 КМ».

| Изм. | Кол.уч. | Лист | №док. | Подпись | Дата |
|---|---|---|---|---|---|
| ГИП | | Кирпичников С. | | | 09.2026 |
| Нач.отд. | | Рябинин А. | | | 09.2026 |
| Исполн. | | Таштимуров Р. | | | 09.2026 |
| Н.контр | | Кирпичников С. | | | 09.2026 |

ГАЗОПРОВОД «ГАЗЛИ-САРИМОЙ» (54 КМ)
Линейный крановый узел DN1000 КУП-D7

| Стадия | Лист | Листов |
|---|---|---|
| РД | 1 | 1 |

Изометрический чертеж трубопровода
300-GT-63CS02-HH-D0702

ООО "EAST-WEST Engineering"
г. Ташкент 2026г.

Формат А2 594х420

Взам. инв. №

Подпись и дата

Инв.№ подл.