

План / Plan
M (1:50)

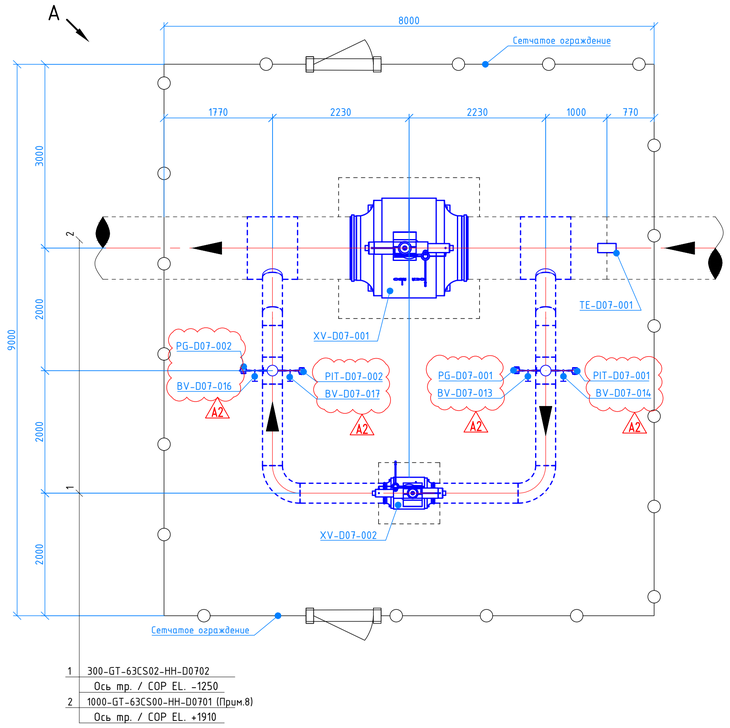


1 300-GT-63CS02-HH-D0702
Ось тр. / COP EL. -1250
2 1000-GT-63CS00-HH-D0701 (Прим.8)
Ось тр. / COP EL. +1910


Изометрический вид "A"
M (1:50)

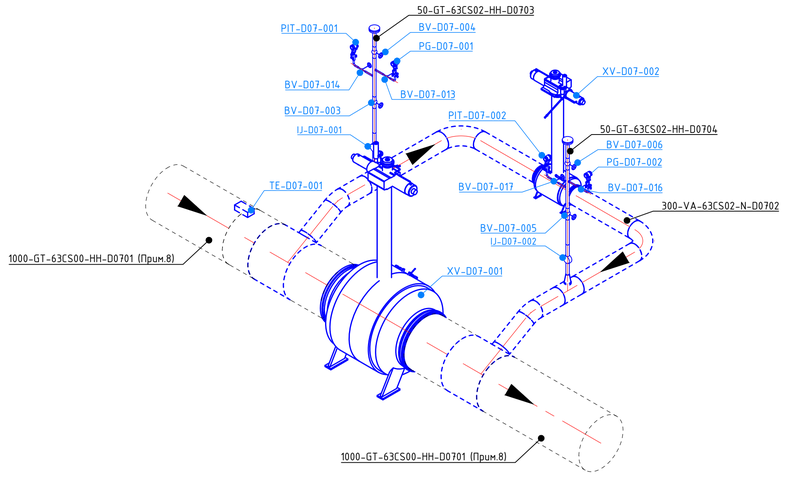

Разрез / Section 1-1
M (1:50)

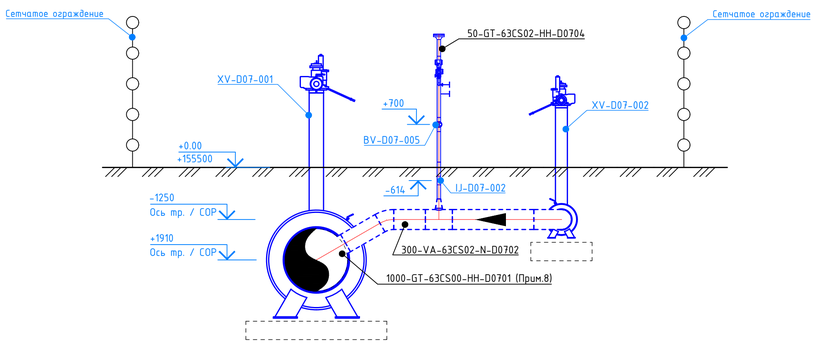

Разрез / Section 2-2
M (1:50)

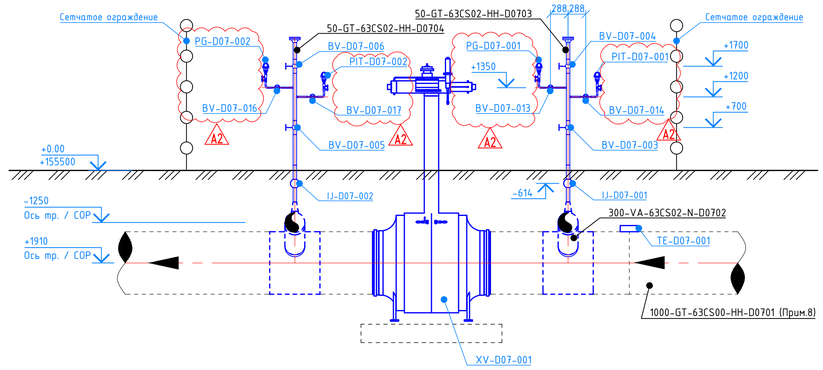

Условные обозначения:

N - нет изоляции
HH - гидроизоляция от почвенной коррозии

ПРИМЕЧАНИЯ

1. Общие данные см. EWE0426-MGL1-PRE-054-COM-760201;
2. * - Размеры для справок;
3. ** - Размеры уточнить по месту;
4. Кран XV-D07-001 расположен на пикете ПК 0+33 перемычки №4 Ду1000;
5. Размеры фитингов - по ГОСТ. Все размеры указаны в миллиметрах;
6. Высотные отметки уточнить по месту;
7. Данный чертеж составлен на основе EWE0426-MGL1-PIL-054-COM-660201;
8. Труба учтена в линейной части проекта;
9. Привязка к пикетажу указана в EWE0426-MGL1-PRE-054-PLA-760202;
10. Фундаменты под опоры, шаровой кран XV-D07-001, продувочную свечу см. EWE0426-MGL1-STR-054-COM-760501;
11. Детальную информацию по трубопроводам см. изометрические чертежи;
12. На схеме указано основное направление потока газа, согласно схеме PFD, см. EWE0426-MGL1-PRE-054-PFD-610101. В процессе эксплуатации поток может быть направлен в обратном направлении.

Рев	Дата	Назначение ревизии	Проверил	Утвердил
A2	28.08.2026	Утверждено для строительства		
A1	24.07.2026	Утверждено для строительства		
R1	19.06.2026	Выпущено для рассмотрения		

ЗАКАЗЧИК: UTG ГЕНЕРАЛЬНЫЙ ПОДРЯДЧИК: UET ПОДРЯДЧИК: PBG ГЕНЕРАЛЬНЫЙ ПРОЕКТИРОВЩИК: EAST WEST ENGINEERING

Изм.	Кол.уч.	Лист	№док.	Подпись	Дата
ГИП		Скабицкий А.			08.2026
Нач.отд.		Рябинин А.			08.2026
Исполн.		Таштимуров Р.			08.2026
Н.контр		Скабицкий А.			08.2026

EWE0426-MGL1-PRE-054-DRW-760203-A2

«СТРОИТЕЛЬСТВО НОВЫХ НИТОК (УЧАСТКОВ) ГАЗОПРОВОДОВ «ГАЗЛИ - САРИМОЙ» И «АКЧАЛОК - ГАЗЛИ - НУКУС» ОБЩЕЙ ПРОТЯЖЕННОСТЬЮ НЕ МЕНЕЕ 275 КМ».

ГАЗОПРОВОД «ГАЗЛИ-САРИМОЙ» (54 КМ).
Линейный крановый узел DN1000 КУП-D7.

Стадия	Лист	Листов
РП	1	1

КУП-D7. План. Разрезы. Виды.
M 1:50

ООО "EAST-WEST Engineering"
г. Ташкент 2026г.

Взам. инв. №
Подпись и дата
Инв.№ подл.

Формат / Format A1