Схема расположения кранового узла КУП-D7

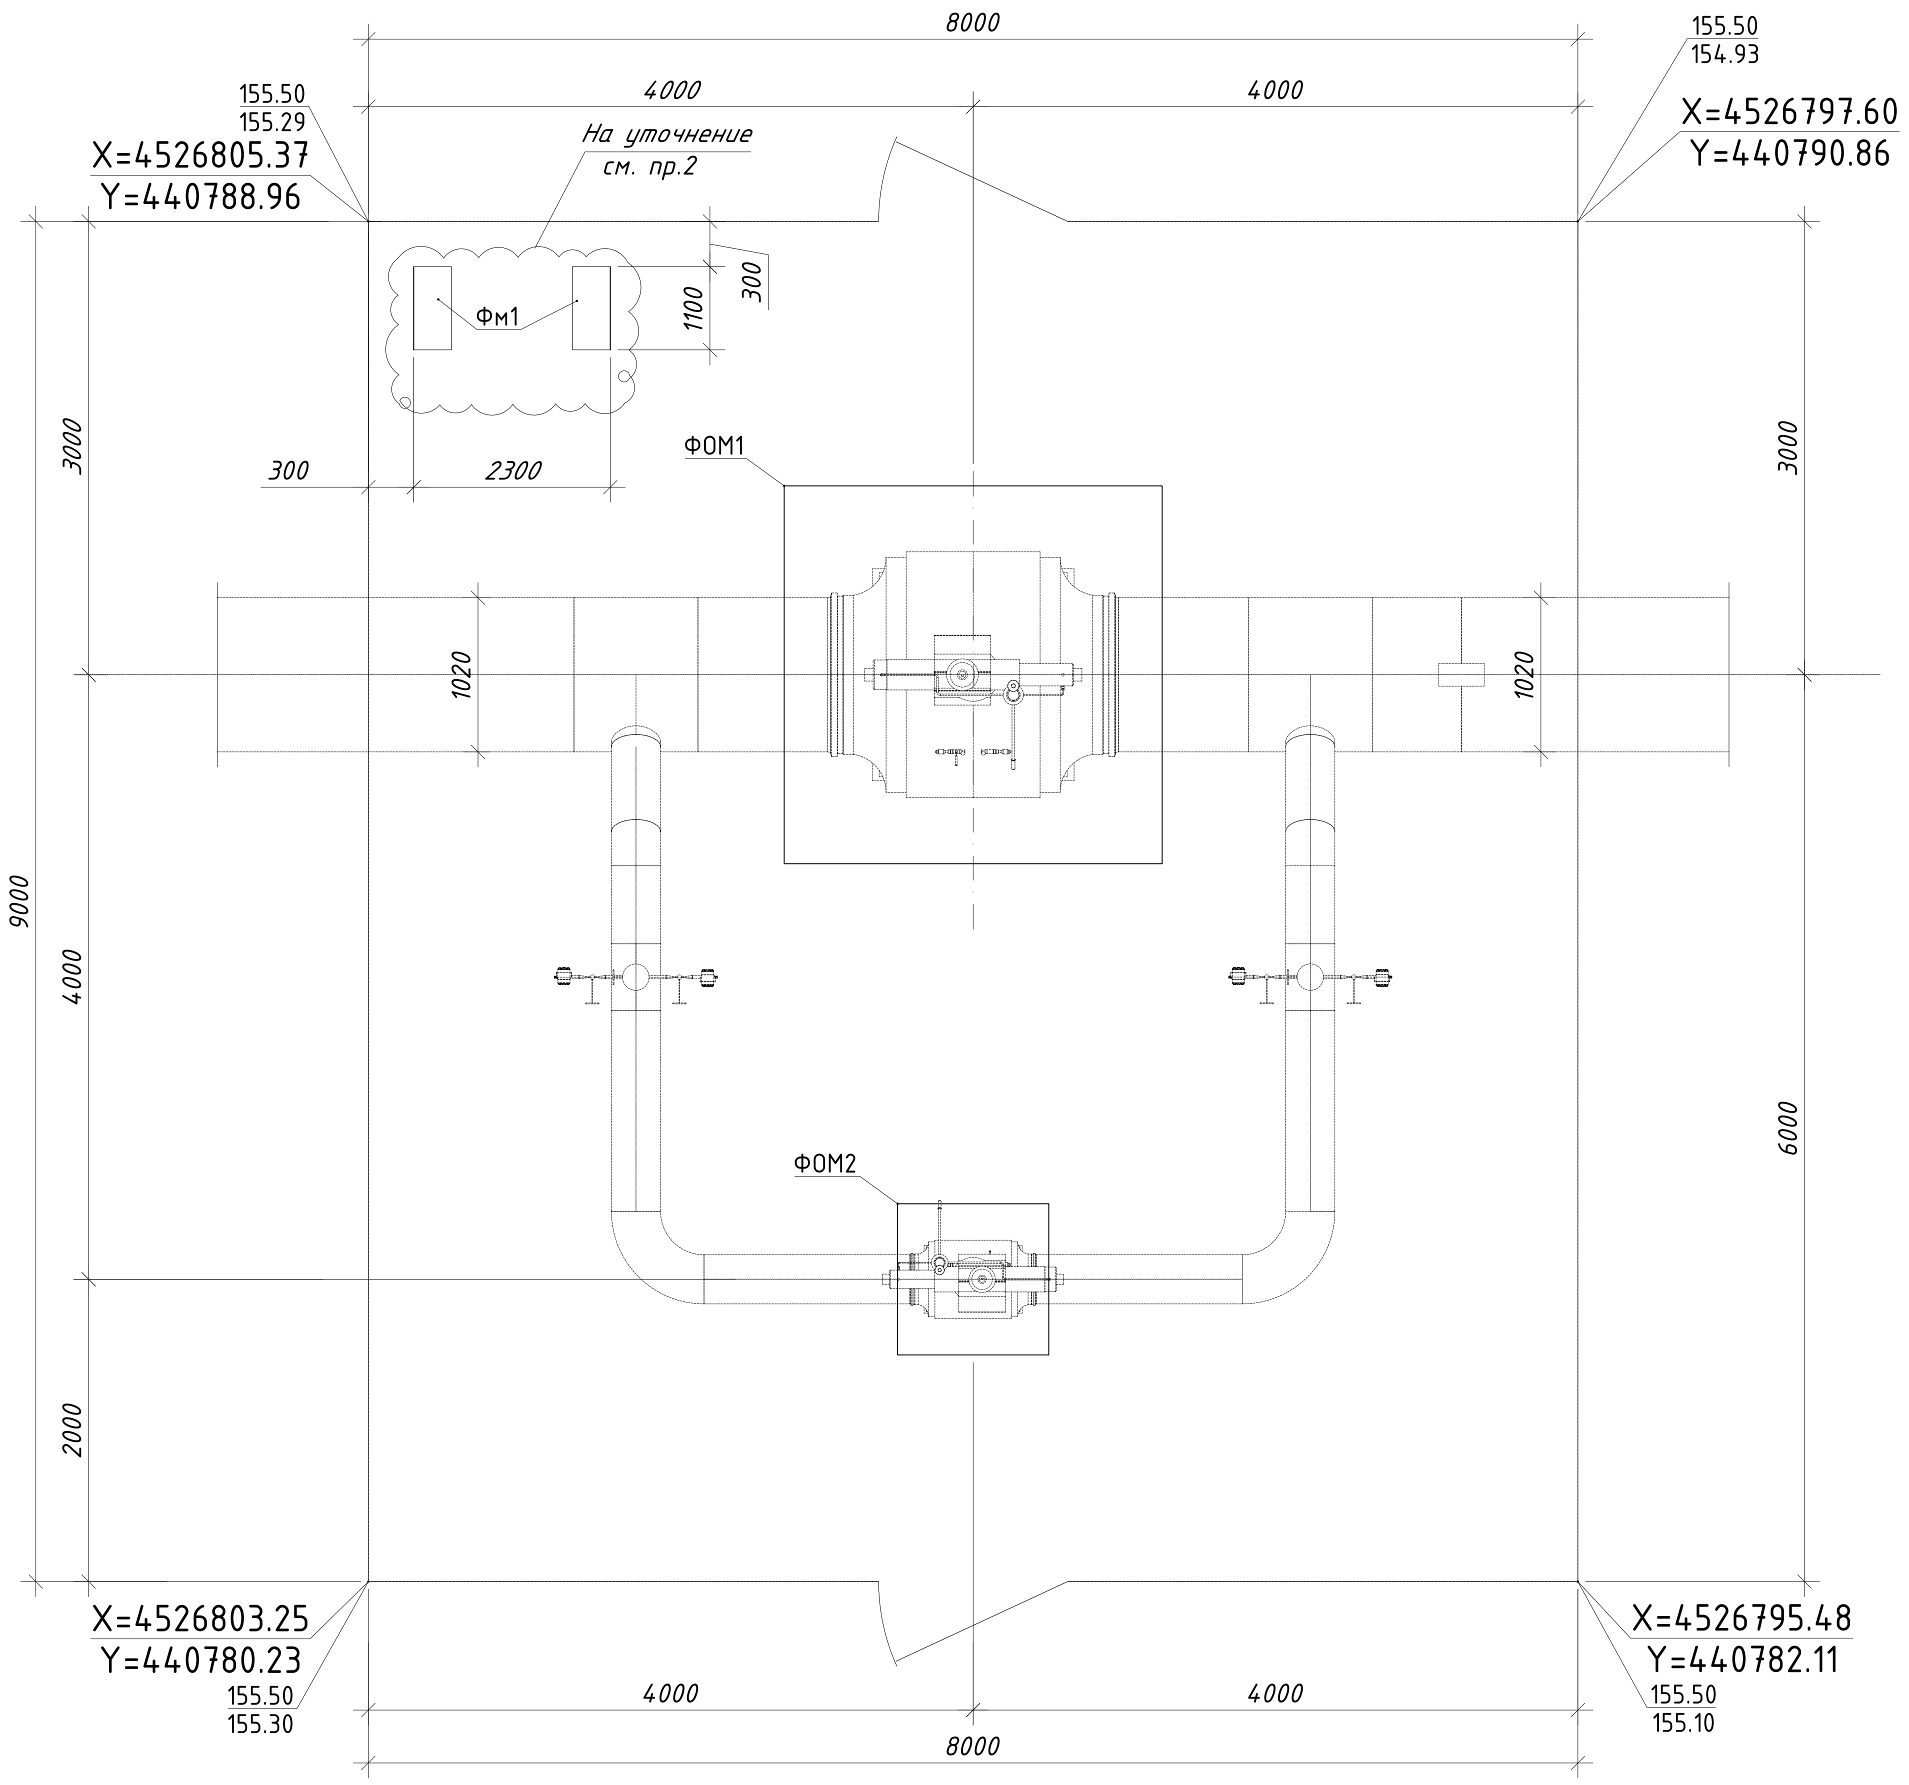
8000
4000
4000
155.50
155.29
X=4526805.37
Y=440788.96
155.50
154.93
X=4526797.60
Y=440790.86
На уточнение
см. пр.2
Фм1
1100
300
300
2300
3000
3000
9000
4000
6000
2000
ФОМ1
1020
1020
ФОМ2
X=4526803.25
Y=440780.23
155.50
155.30
X=4526795.48
Y=440782.11
155.50
155.10
4000
4000
8000

Спецификация элементов

Марка Поз.	Обозначение	Наименование	Кол. шт.	Масса ед.кг	Примеч.
		Крановый узел КУП-D7			
ФОМ1	EWE0426-MGL1-STR-054-DRW-760504	Фундамент оборудования, монолитный ФОМ1	1		
ФОМ2	EWE0426-MGL1-STR-054-DRW-760505	Фундамент оборудования, монолитный ФОМ2	1		
Фм1	см. лист 2	Фундамент Фм1	2		

Примечание:

1. Установка кранового узла КУП-D7 (DN1000) расположена на ПК0+33 трассы проектного газопровода.
2. Размеры установки навеса для КИПиА должны быть уточнены после получения КД на шкаф со стороны заказчика.
3. Данный лист см. совместно с листами: 2

Условные обозначения:

155.50 – Отметка спланированной поверхности земли

154.93 – Отметка существующей поверхности земли

Рев	Дата	Назначение ревизии	Проверил	Утвердил
A1	09.09.2026	Выпущено для строительства		
R1	27.07.2026	Выпущено для рассмотрения		

ЗАКАЗЧИК: UZTRANSGAZ «TRANSGAZINJINIRING»

ГЕНЕРАЛЬНЫЙ ПОДРЯДЧИК: UZBEKENERGOTAMIR

ПОДРЯДЧИК: PBG Pro Build Generation

ГЕНЕРАЛЬНЫЙ ПРОЕКТИРОВЩИК: EAST WEST ENGINEERING

EWE0426-MGL1-STR-054-DRW-760502-A1

«СТРОИТЕЛЬСТВО НОВЫХ НИТОК (УЧАСТКОВ) ГАЗОПРОВОДОВ «ГАЗЛИ - САРИМОЙ» И «АКЧАЛОК - ГАЗЛИ - НУКУС» ОБЩЕЙ ПРОТЯЖЕННОСТЬЮ НЕ МЕНЕЕ 275 КМ».

Изм.	Кол.уч.	Лист	№ док.	Подпись	Дата
ГИП		Кирпичников С.			09.09.26
Нач.отд.		Каршиев А.			09.09.26
Исполн.		Юлдашев Ж.			09.09.26
Н.контр		Кирпичников С.			09.09.26

ГАЗОПРОВОД "ГАЗЛИ-САРИМОЙ" (54 КМ)
Линейный крановый узел DN1000 КУП-D7

Стадия	Лист	Листов
РП	1	2

Схема расположения
кранового узла КУП-D7

EAST WEST ENGINEERING
ООО "EAST-WEST Engineering"
г. Ташкент 2026г.

Формат / Format A2

Взам. инв. №

Подпись и дата

Инв.№ подл.

Навес для электрического шкафа и шкафа телемеханики Н-1

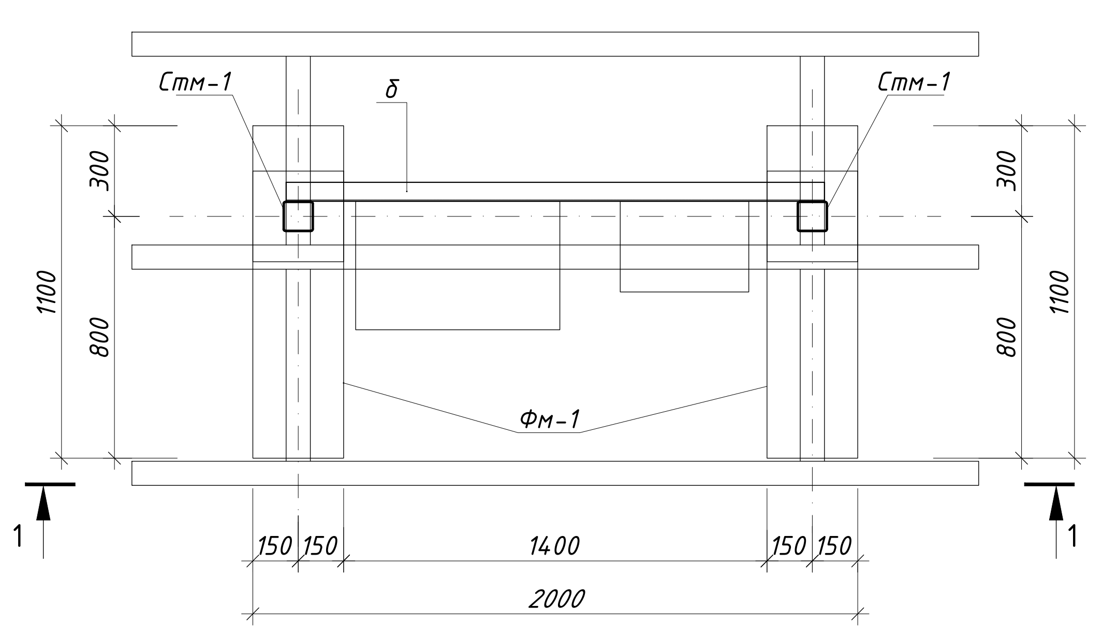
Стм-1
Стм-1
б
300
300
1100
800
800
1100
Фм-1
1
1
150 150
1400
150 150
2000

1 - 1

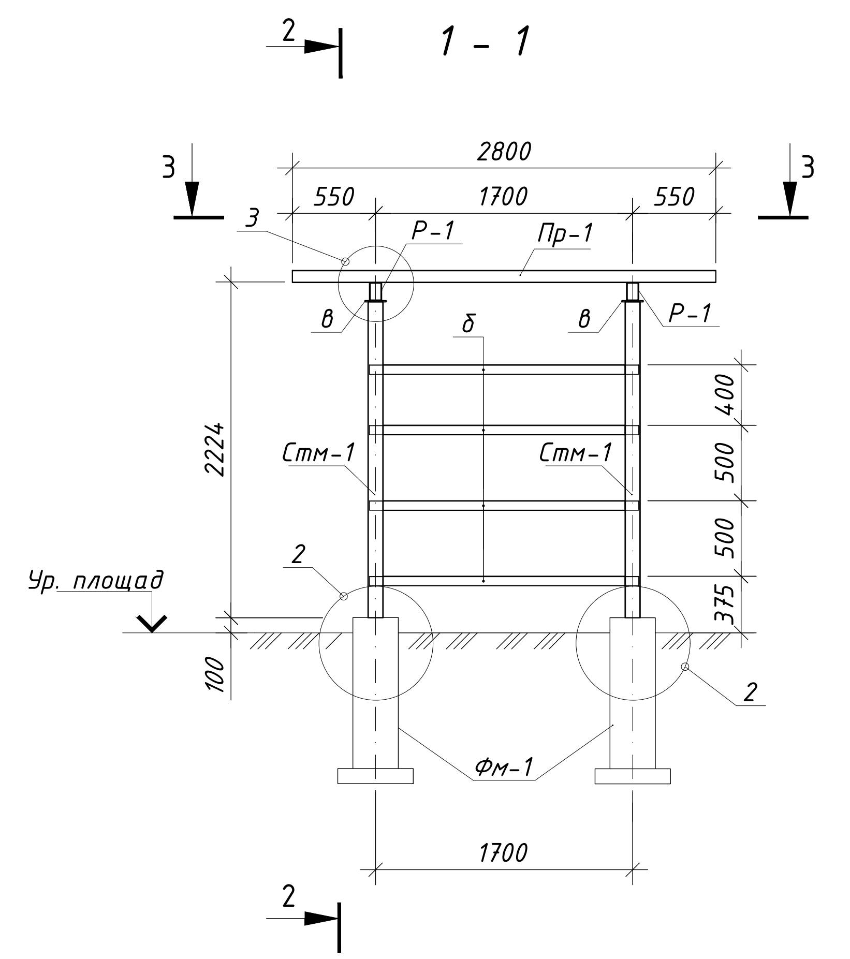
2
3
3
2800
550
1700
550
3
Р-1
Пр-1
в
б
в
Р-1
Стм-1
Стм-1
2224
400
500
500
375
Ур. площад
100
2
2
Фм-1
1700
2

2 - 2

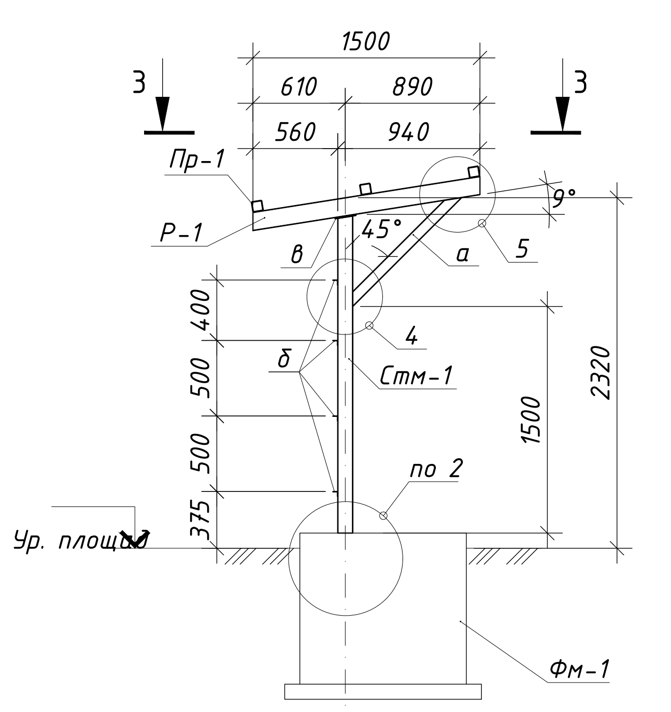
3
3
1500
610
890
560
940
Пр-1
Р-1
45°
9°
а
5
в
б
4
Стм-1
400
500
500
375
1500
2320
по 2
Ур. площад
Фм-1

3 - 3

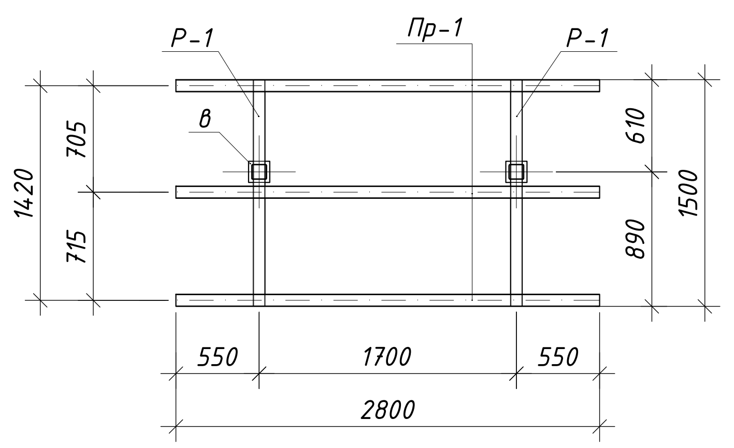
Р-1
Пр-1
Р-1
в
705
715
1420
610
890
1500
550
1700
550
2800

Ведомость деталей	
Поз.	Эскиз
ш1	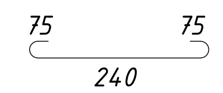 75 75 240

Спецификация элементов на данном листе

Марка Поз.	Обозначение	Наименование	Кол. шт	Масса ед., кг	Прим.
		Навес Н-1	1		
Стм-1	ГОСТ 30245-2003 С245	□100х100х4 L=2092 мм	2	22,70	45.40
Р-1	ГОСТ 30245-2003 С245	□120х80х4 L=1540 мм	2	18,00	36.00
Пр-1	ГОСТ 30245-2003 С245	□80х80х4 L=2800 мм	3	25,80	77.40
П-1	ГОСТ 24045-2016	Профнастил НС35-1000-0.6	5.1м²	6,40	32.64
а	ГОСТ 30245-2003 С245	□80х80х4 L=1020 мм	2	9,40	18.80
б	ГОСТ 8509-93 С245	∟ 63х4 L=1780 мм	4	6,94	27.76
в	ГОСТ 19903-2015 Лист	Б-ПН-8х150х150 ГОСТ 19903-2015 С245-ГК ГОСТ 27772-2015	2	1,41	2.82
г	ГОСТ 19903-2015 Лист	Б-ПН-8х100х200 ГОСТ 19903-2015 С245-ГК ГОСТ 27772-2015	8	1,25	10.00
		Фундамент Фм-1	2		Общие расх.
МН126-3	Серия 1.400-15	Изделие закладное МН126-3	2	6,70	13.40
С-1	См. данный лист	Сетка С-1	4	6,53	26.12
ш1	ГОСТ 34028-2016	Ф6 А240 L=390мм	30	0,20	5.93
		Материалы			
		Бетон класса В15, W6 F50			0.63м³
	на подготовку	Бетон кл. В7.5			0.13м³
С-1		Сетка С-1	1	6.53	6.53
1	ГОСТ 34028-2016	Ф10 А500 L=890мм	6	0,55	3.29
2	ГОСТ 34028-2016	Ф10 А500 L=1050мм	5	0,65	3.24

③

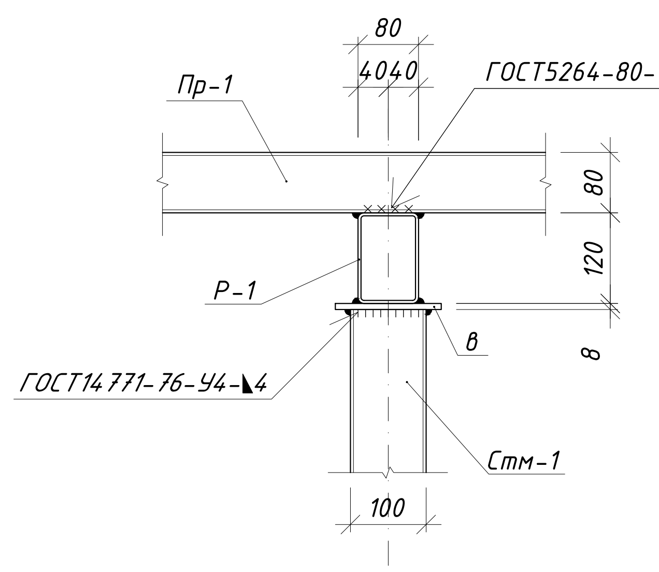
80
40 40
ГОСТ5264-80-Т3-◺4
Пр-1
80
120
Р-1
8
ГОСТ14771-76-У4-◺4
в
Стм-1
100

④

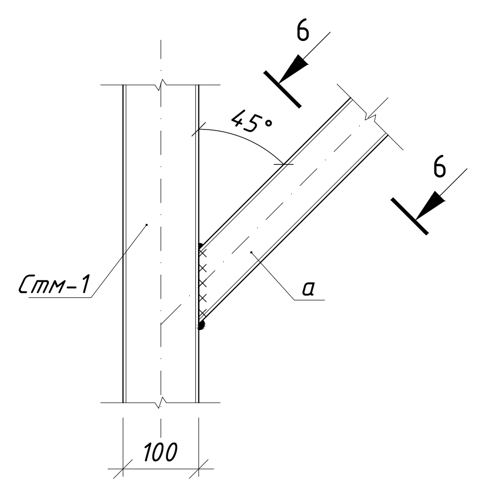
6
45°
6
Стм-1
а
100

Фундамент Фм-1

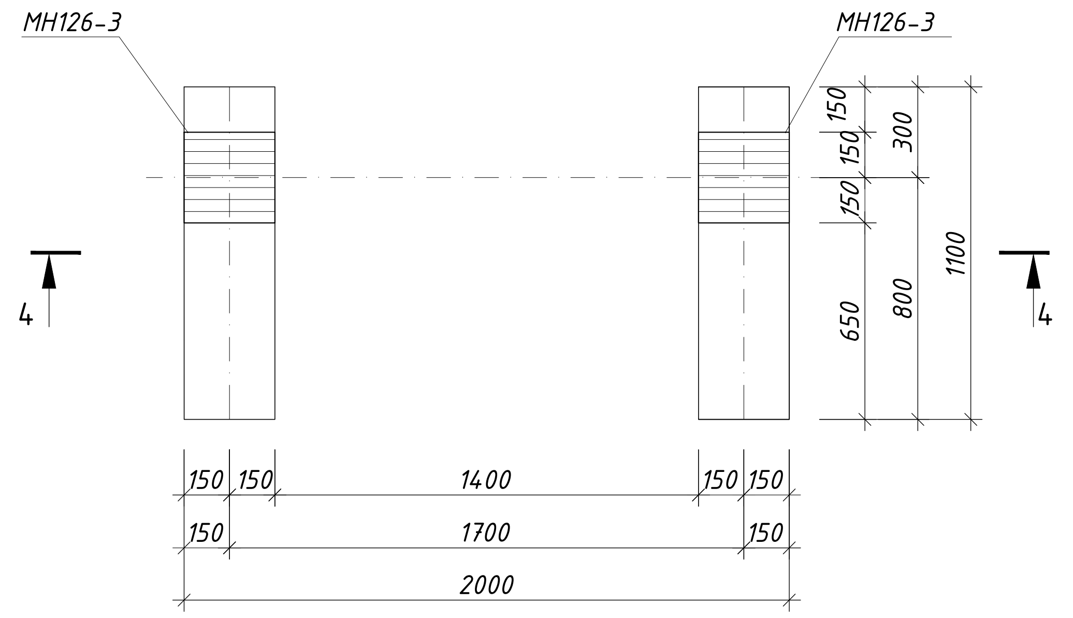
МН126-3
МН126-3
4
4
150
150
300
800
1100
650
150 150
1400
150 150
150
1700
150
2000

①

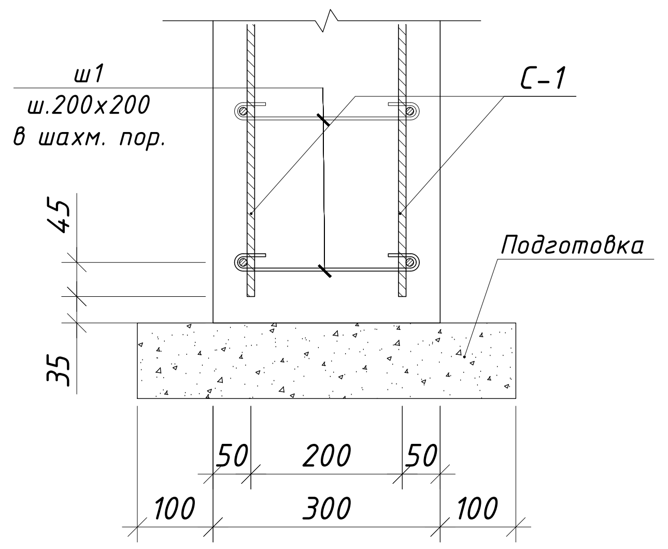
ш1
ш.200х200
в шахм. пор.
С-1
45
Подготовка
35
50
200
50
100
300
100

⑤

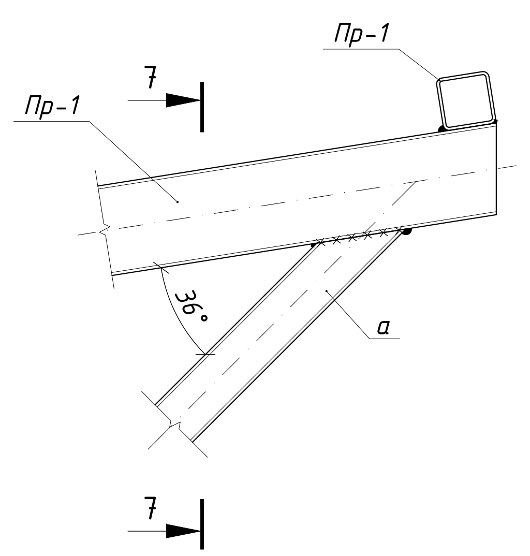
Пр-1
7
Пр-1
36°
а
7

6 - 6

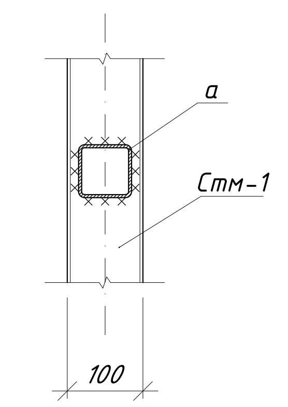

7 - 7

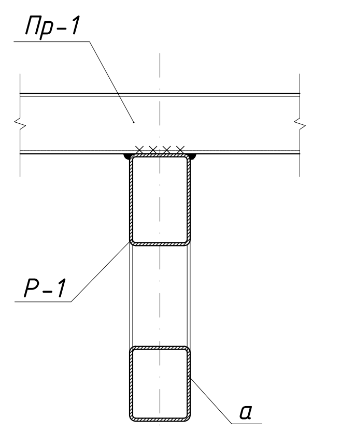

3D навеса

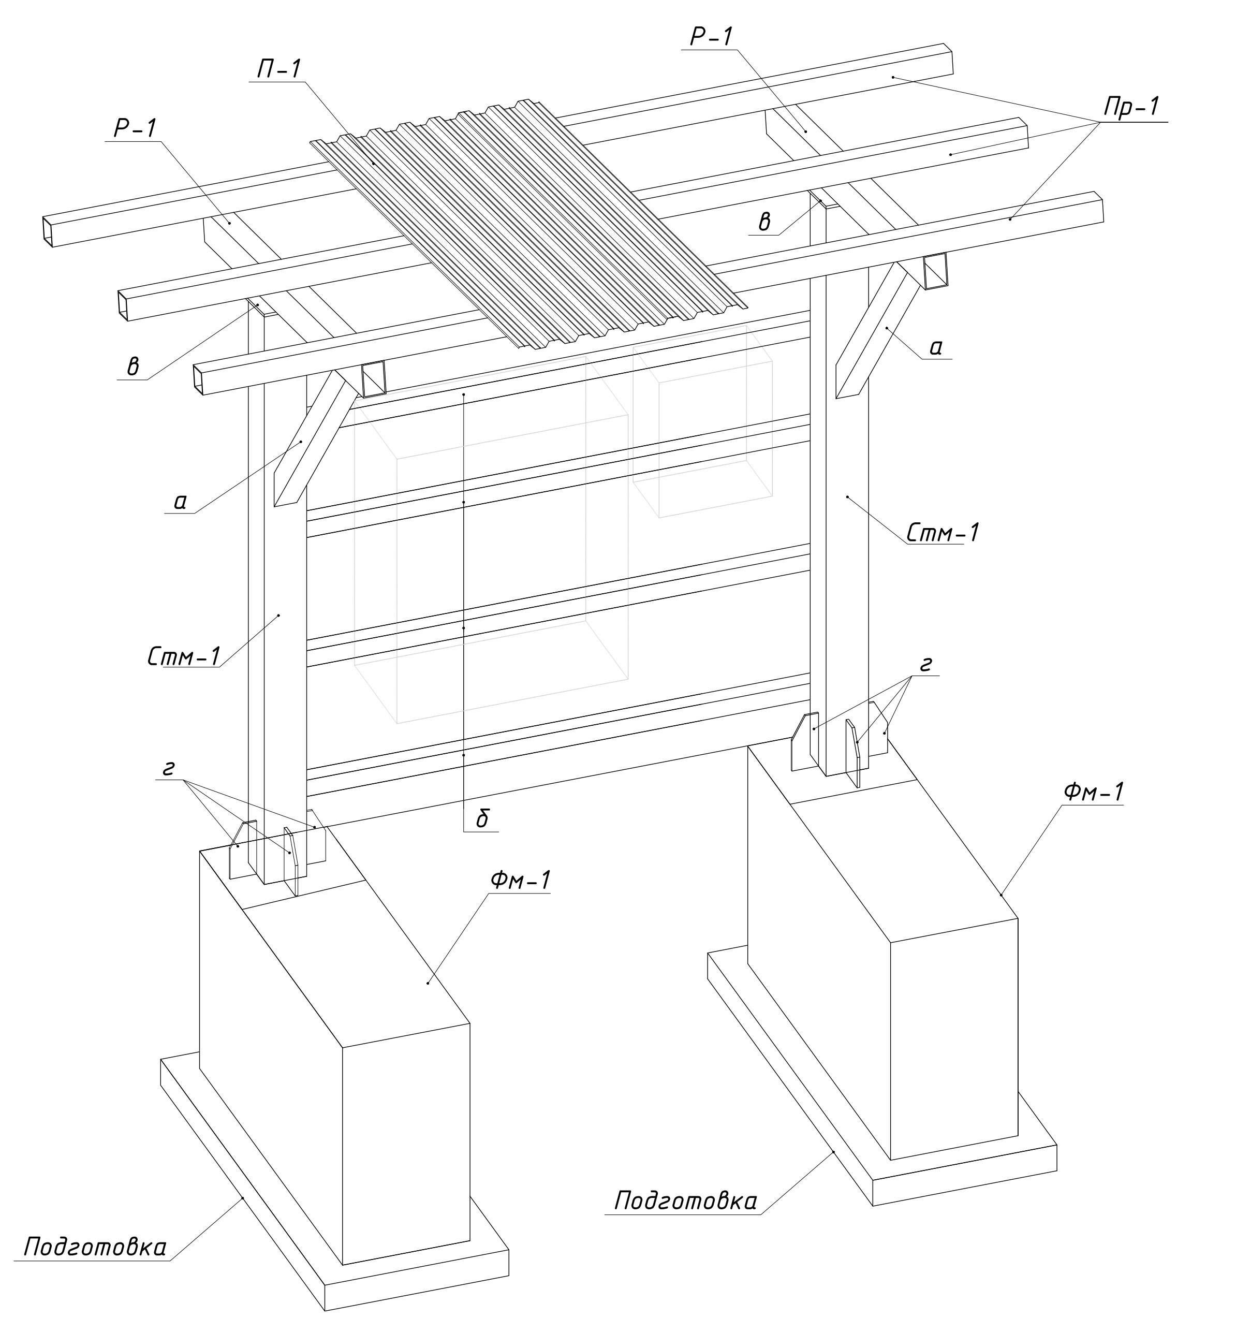
Р-1
П-1
Р-1
Пр-1
в
в
а
а
Стм-1
Стм-1
г
г
б
Фм-1
Фм-1
Подготовка
Подготовка

1. Общие указания см. лист EWE0426-MGL1-STR-054-COM-760501
2. Данный лист см. совместно с листами: 1
3. Монолитные конструкции выполнить согласно ШНК 2.03.01-24 "Бетонные и железобетонные конструкции", КМК 3.03.01-98 "Несущие и ограждающие конструкции".
4. Подготовку из бетона кл. В7.5, толщиной 100 мм и с уширением на 100 мм в каждую сторону. Бетон для фундаментов применять на сульфатостойком портландцементе.
5. Все соединения арматурных стержней выполнять вязаными стальной отожженной проволокой d=0.8-1.0 мм
6. Сварку арматуры производить по РСтУз 865-98 электродами типа Э42А по ГОСТ 9467-75.
7. Размеры установки навеса для КИПиА должны быть уточнены после получения КД на шкаф со стороны заказчика.
8. Профнастил крепить к прогону Пр1 самонарезающими болтами комплект БС6-25НМ по ОСТ 34-13-016-88 с уплотнительными шайбами в каждой волне.
9. Соединение листов между собой по продольным сторонам выполнять комбинированными заклепками ЗК-4,8х10 по ОСТ 34-13-017-88 с шагом 300 мм. После монтажа места установки болтов и заклепок окрасить краской БТ-177 за 2 раза.
10. До монтажа профнастила металлические конструкции и сварные швы подготовить и окрасить эмалью ПФ-115 по ГОСТ 6465-95 в два слоя по одному слою грунтовки ГФ-021 по ГОСТ 25129-2020

4 - 4

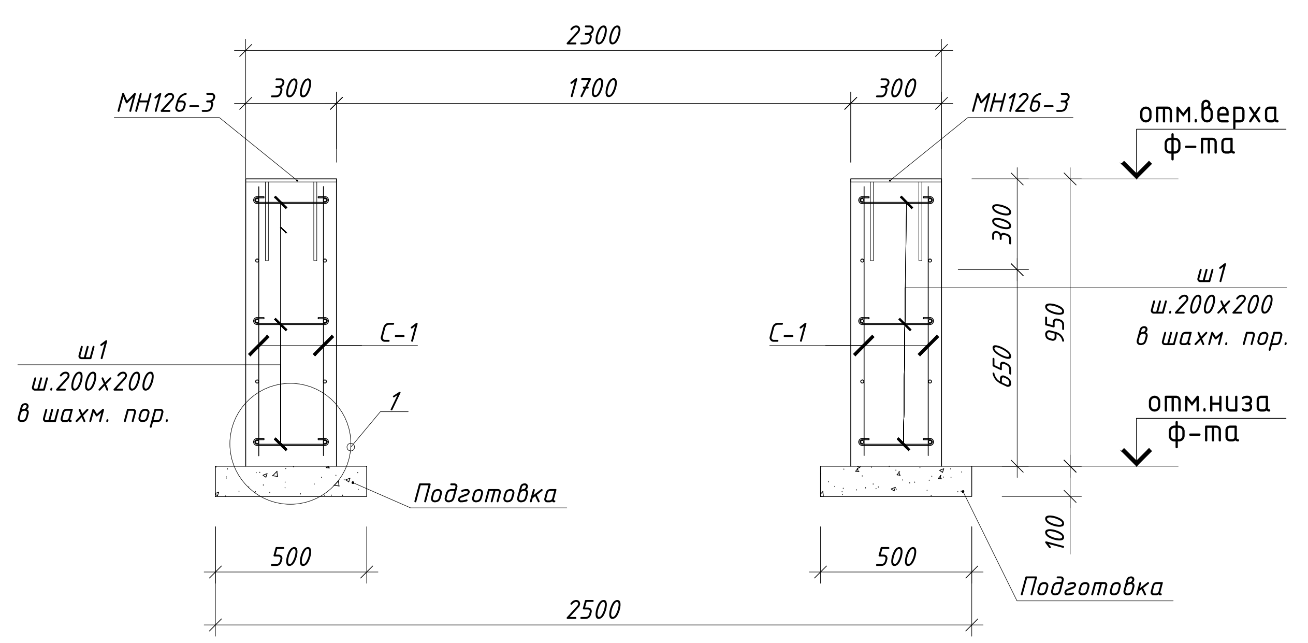
2300
300
1700
300
МН126-3
МН126-3
отм.верха ф-та
300
950
650
ш1
ш.200х200
в шахм. пор.
отм.низа ф-та
ш1
ш.200х200
в шахм. пор.
С-1
С-1
1
Подготовка
Подготовка
500
500
100
2500

Сетка С-1

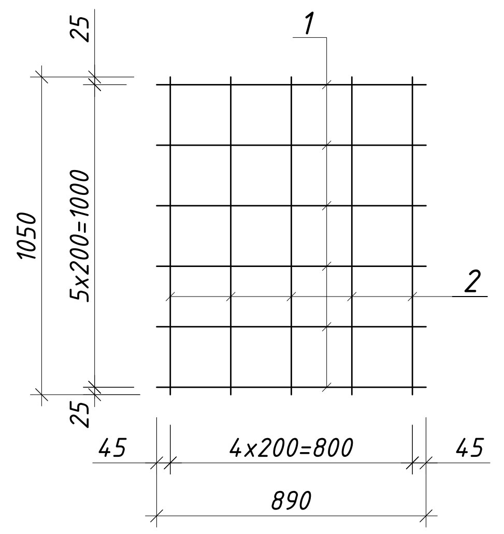
1
25
1050
5х200=1000
25
2
45
4х200=800
45
890

②

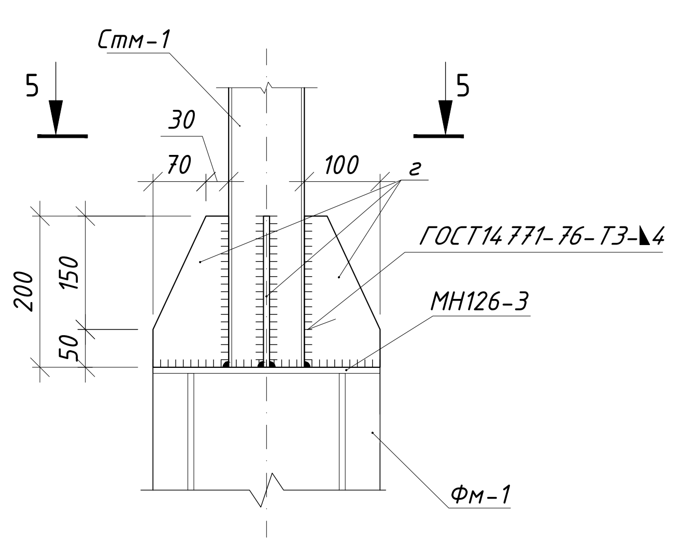
Стм-1
5
5
30
70
100
г
ГОСТ14771-76-Т3-◺4
МН126-3
200
150
50
Фм-1

5 - 5

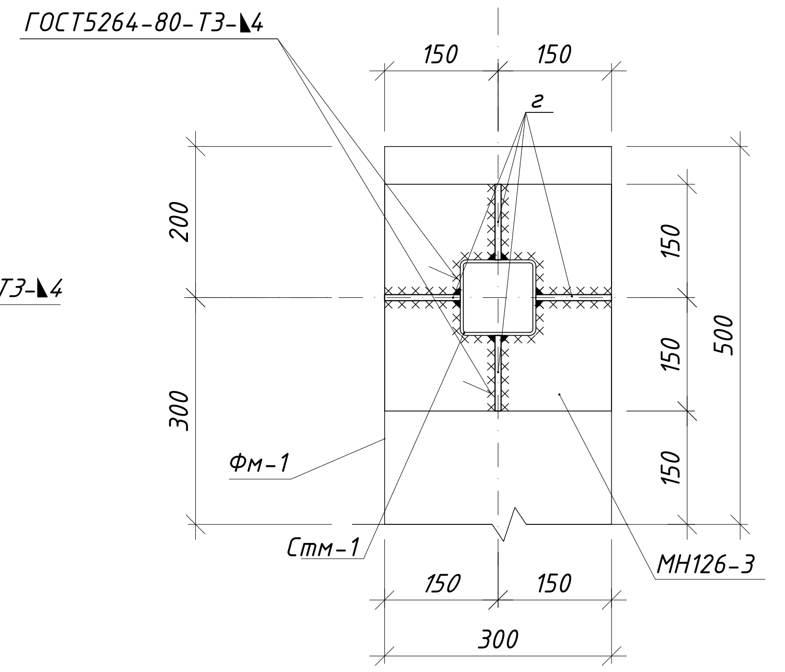
ГОСТ5264-80-Т3-◺4
150
150
г
200
300
150
150
500
150
Фм-1
Стм-1
МН126-3
150
150
300

Рев	Дата	Назначение ревизии	Проверил	Утвердил
А1	09.09.2026	Выпущено для строительство		
R1	27.07.2026	Выпущено для рассмотрения		

ЗАКАЗЧИК: UZTRANSGAZ «TRANSGAZINJINIRING»
ГЕНЕРАЛЬНЫЙ ПОДРЯДЧИК: UZBEKENERGOTAMIR
ПОДРЯДЧИК: Pro Build Generation
ГЕНЕРАЛЬНЫЙ ПРОЕКТИРОВЩИК: EAST WEST ENGINEERING

EWE0426-MGL1-STR-054-DRW-760502-A1

«СТРОИТЕЛЬСТВО НОВЫХ НИТОК (УЧАСТКОВ) ГАЗОПРОВОДОВ «ГАЗЛИ - САРИМОЙ» И «АКЧАЛОК - ГАЗЛИ - НУКУС» ОБЩЕЙ ПРОТЯЖЕННОСТЬЮ НЕ МЕНЕЕ 275 КМ».

Изм.	Кол.уч.	Лист	№ док.	Подпись	Дата
ГИП		Кирпичников С.			09.09.26
Нач.отд.		Каршиев А.			09.09.26
Исполн.		Юлдашев Ж.			09.09.26
Н.контр		Кирпичников С.			09.09.26

ГАЗОПРОВОД "ГАЗЛИ-САРИМОЙ" (54 КМ)
Линейный крановый узел DN1000 КУП-D7

Стадия	Лист	Листов
РП	2	2

Схема расположения кранового узла КУП-D7

EAST WEST ENGINEERING
ООО "EAST-WEST Engineering"
г. Ташкент 2026г.

Формат / Format A3X3

Взам. инв. №
Подпись и дата
Инв.№ подл.