

Фундамент ФОМ1

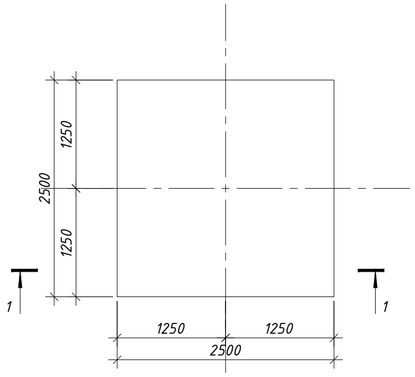


Сетка С1

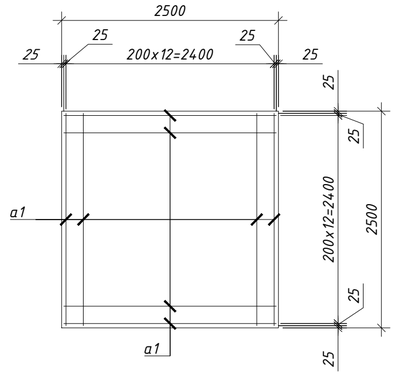


Спецификация элементов

Марка Поз.	Обозначение	Наименование	Кол.шт	Масса ед., кг	Прим.
		Фундамент ФОМ1			
		Сборные единицы			
С1	*См. данный лист*	*Сетка С1*	*2*		*113.05*
		Детали			
Ос1	*ГОСТ 34028-2016*	*Ф8 А240 L=1138 мм*	*9*	*0.45*	*4.04*
		Сетка С1			
а1	*ГОСТ 34028-2016*	*Ф12 А500 L=2450 мм*	*26*	*2.17*	*56.53*
		Материалы			
	на подливку	*Бетон кл. В25, W6, F50*			*0.32 м³*
		Бетон кл. В20, W6, F50			*1.88 м³*
	на подготовку	*Бетон кл. В7.5*			*0.73*

1 – 1

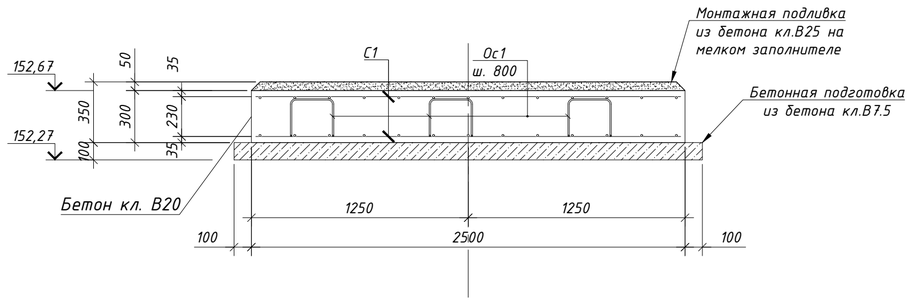

Ведомость деталей

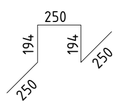Поз.	Эскиз
Ос1	

Гидроизоляция фундамента из двух слоев полимерного покрытия на основе лака ХП-734 по ГОСТ 52165-2003 толщиной 25 мкм.

Примечания:

1. *Объединение арматурных стержней в плоские сетки или пространственные каркасы выполнять вязальной стальной отожженной проволокой d=0.8-1.0мм. Применение ручной электродуговой сварки не допускается.*
2. *Подливку выполнить из бетона кл. В25 на мелком заполнителе.*
3. *Фундамент ФОМ1 разработан под шаровой кран. Бетонирование выполнять после получения оборудования и сверки с паспортными данными.*
4. *Фиксаторы для крепления двух сеток марки Ос-1 устанавливать в шахматном порядке.*

Ведомость расхода стали, кг

Марка элемента	Изделия арматурные				Всего	Общий расход
	Арматура класса					
	А240		А500			
	ГОСТ 34028-2016		ГОСТ 34028-2016			
	Ф8	Итого	Ф12	Итого		
Фундамент ФОМ1	4.04	4.04	113.05	113.05	117.09	117.09

Рев	Дата	Назначение ревизии	Проверил	Утвердил
А1	*09.09.2026*	*Выпущено для строительства*		
R1	*27.07.2026*	*Выпущено для рассмотрения*		

ЗАКАЗЧИК: UTG UZTRANSGAZ | ГЕНЕРАЛЬНЫЙ ПОДРЯДЧИК: UET UZBEKENERGOTAMIR | ПОДРЯДЧИК: PBG Pro Build Generation | ГЕНЕРАЛЬНЫЙ ПРОЕКТИРОВЩИК: EAST WEST ENGINEERING

EWE0426-MGL1-STR-054-DRW-760504-A1

«СТРОИТЕЛЬСТВО НОВЫХ НИТОК (УЧАСТКОВ) ГАЗОПРОВОДОВ «ГАЗЛИ – САРИМОЙ» И «АКЧАЛОК – ГАЗЛИ – НУКУС» ОБЩЕЙ ПРОТЯЖЕННОСТЬЮ НЕ МЕНЕЕ 275 КМ».

Изм.	Кол.уч.	Лист	№ док.	Подпись	Дата			
ГИП		Кирпичников С.			09.09.26	*ГАЗОПРОВОД "ГАЗЛИ-САРИМОЙ" (54 КМ) Линейный крановый узел DN1000 КУП-D7*	Стадия	Лист	Листов
Нач.отд.		Каршиев А.			09.09.26		РП	1	1
Исполн.		Юлдашев Ж.			09.09.26				
Н.контр		Кирпичников С.			09.09.26	*Фундамент ФОМ1*	EAST WEST ENGINEERING	ООО "EAST-WEST Engineering" г. Ташкент 2026г.	

Взам. инв. №

Подпись и дата

Инв.№ подл.