
Схема расположения сетчатого ограждения

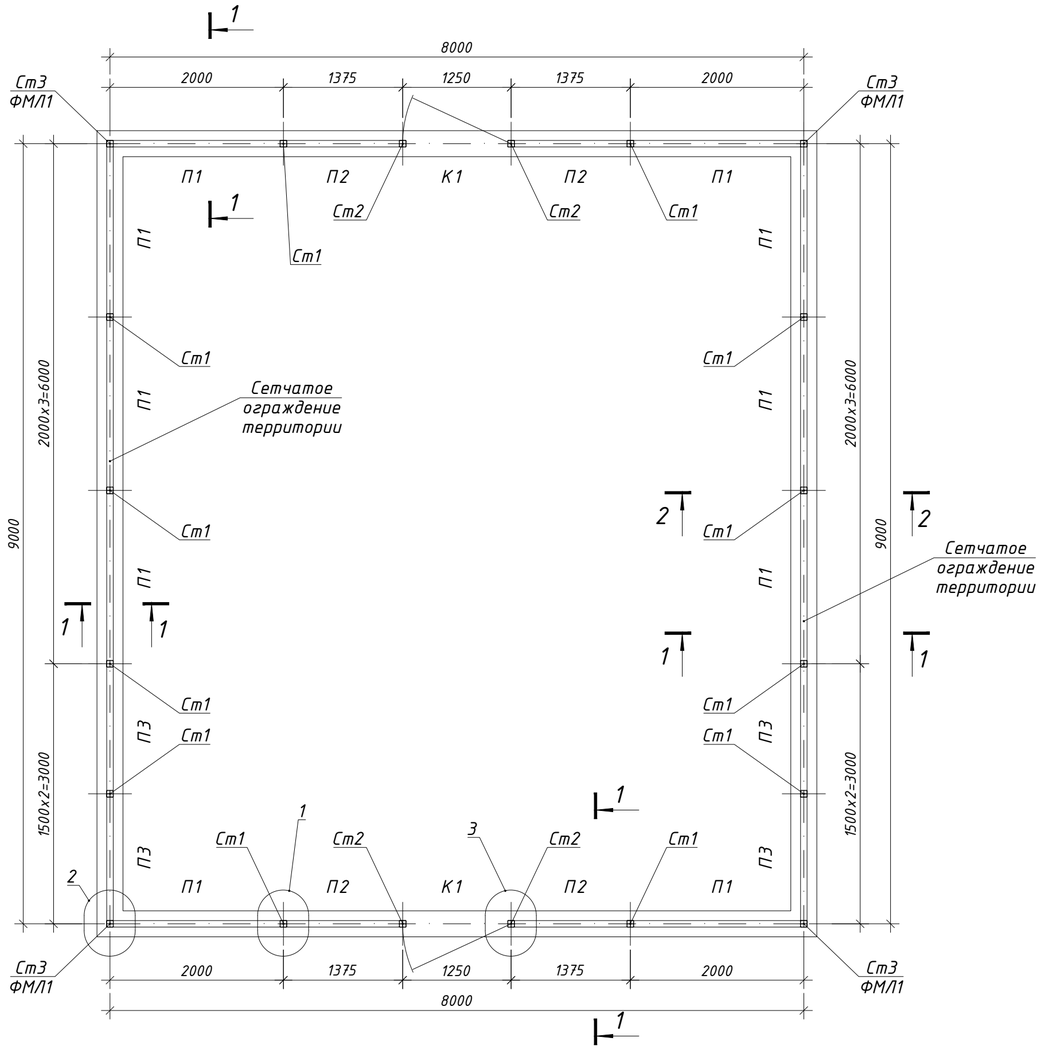


Спецификация элементов

Марка Поз.	Обозначение	Наименование	Кол. шт.	Масса ед.кг	Примеч.
		Линейный крановый узел КУП- D7			
ФМЛ1	EWE0426-MGL1-STR-054-DRW-760507	Фундамент ленточный, монолитный ФМЛ1			
Ст1	EWE0426-MGL1-STR-054-DRW-760508	Стойка ограждения Ст1	12		
Ст2	EWE0426-MGL1-STR-054-DRW-760509	Стойка ограждения Ст2	4		
Ст3	EWE0426-MGL1-STR-054-DRW-760510	Стойка ограждения Ст3	4		
П1	EWE0426-MGL1-STR-054-DRW-760511	Панель ограждения П1	10		
П2	EWE0426-MGL1-STR-054-DRW-760512	Панель ограждения П2	4		
П3	EWE0426-MGL1-STR-054-DRW-760513	Панель ограждения П3	4		
К1	EWE0426-MGL1-STR-054-DRW-760514	Калитка К1	2		
КД1	EWE0426-MGL1-STR-054-DRW-760515	Крепежная деталь КД1	24		
КД2	EWE0426-MGL1-STR-054-DRW-760515	Крепежная деталь КД2	24		


Примечания:

1. Данный чертёж читать совместно с ленточным фундаментом ФМЛ1.
2. Изготовить общее количество узлов:
   - узел 1 – 12 шт.
   - узел 2 – 4 шт.
   - узел 3 – 4 шт.
3. Сечения 1 – 1, 2 – 2 смотреть на л. -DRW-760507


Узел 1

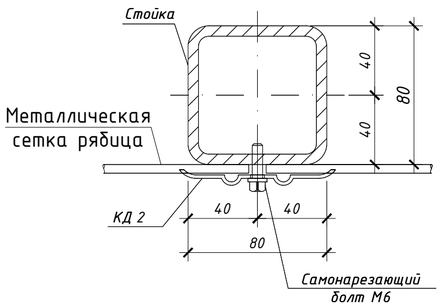

Узел 2

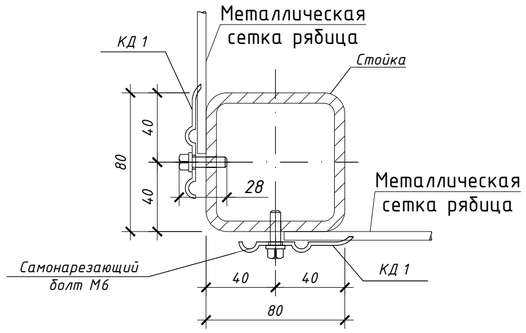

Узел 3

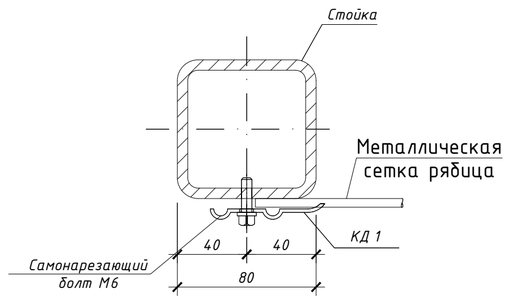

А1	09.09.2026	Выпущено для строительства			
R1	27.07.2026	Выпущено для рассмотрения			
Рев	Дата	Назначение ревизии		Проверил	Утвердил

ЗАКАЗЧИК: UTG UZTRANSGAZ | ГЕНЕРАЛЬНЫЙ ПОДРЯДЧИК: UET UZBEKENERGOTAMIR | ПОДРЯДЧИК: PBG Pro Build Generation | ГЕНЕРАЛЬНЫЙ ПРОЕКТИРОВЩИК: EAST WEST ENGINEERING

EWE0426-MGL1-STR-054-DRW-760506-A1

«СТРОИТЕЛЬСТВО НОВЫХ НИТОК (УЧАСТКОВ) ГАЗОПРОВОДОВ «ГАЗЛИ - САРИМОЙ» И «АКЧАЛОК - ГАЗЛИ - НУКУС» ОБЩЕЙ ПРОТЯЖЕННОСТЬЮ НЕ МЕНЕЕ 275 КМ».

Изм.	Кол.уч.	Лист	№ док.	Подпись	Дата
ГИП		Кирпичников С.			09.09.26
Нач.отд.		Каршиев А.			09.09.26
Исполн.		Юлдашев Ж.			09.09.26
Н.контр		Кирпичников С.			09.09.26

ГАЗОПРОВОД "ГАЗЛИ-САРИМОЙ" (54 КМ)
Линейный крановый узел DN1000 КУП-D7

Стадия	Лист	Листов
РП	1	1

Схема расположения сетчатого ограждения

ООО "EAST-WEST Engineering"
г. Ташкент 2026г.

Взам. инв. №

Подпись и дата

Инв.№ подл.

Формат / Format A2