Стойка ограждения Ст2

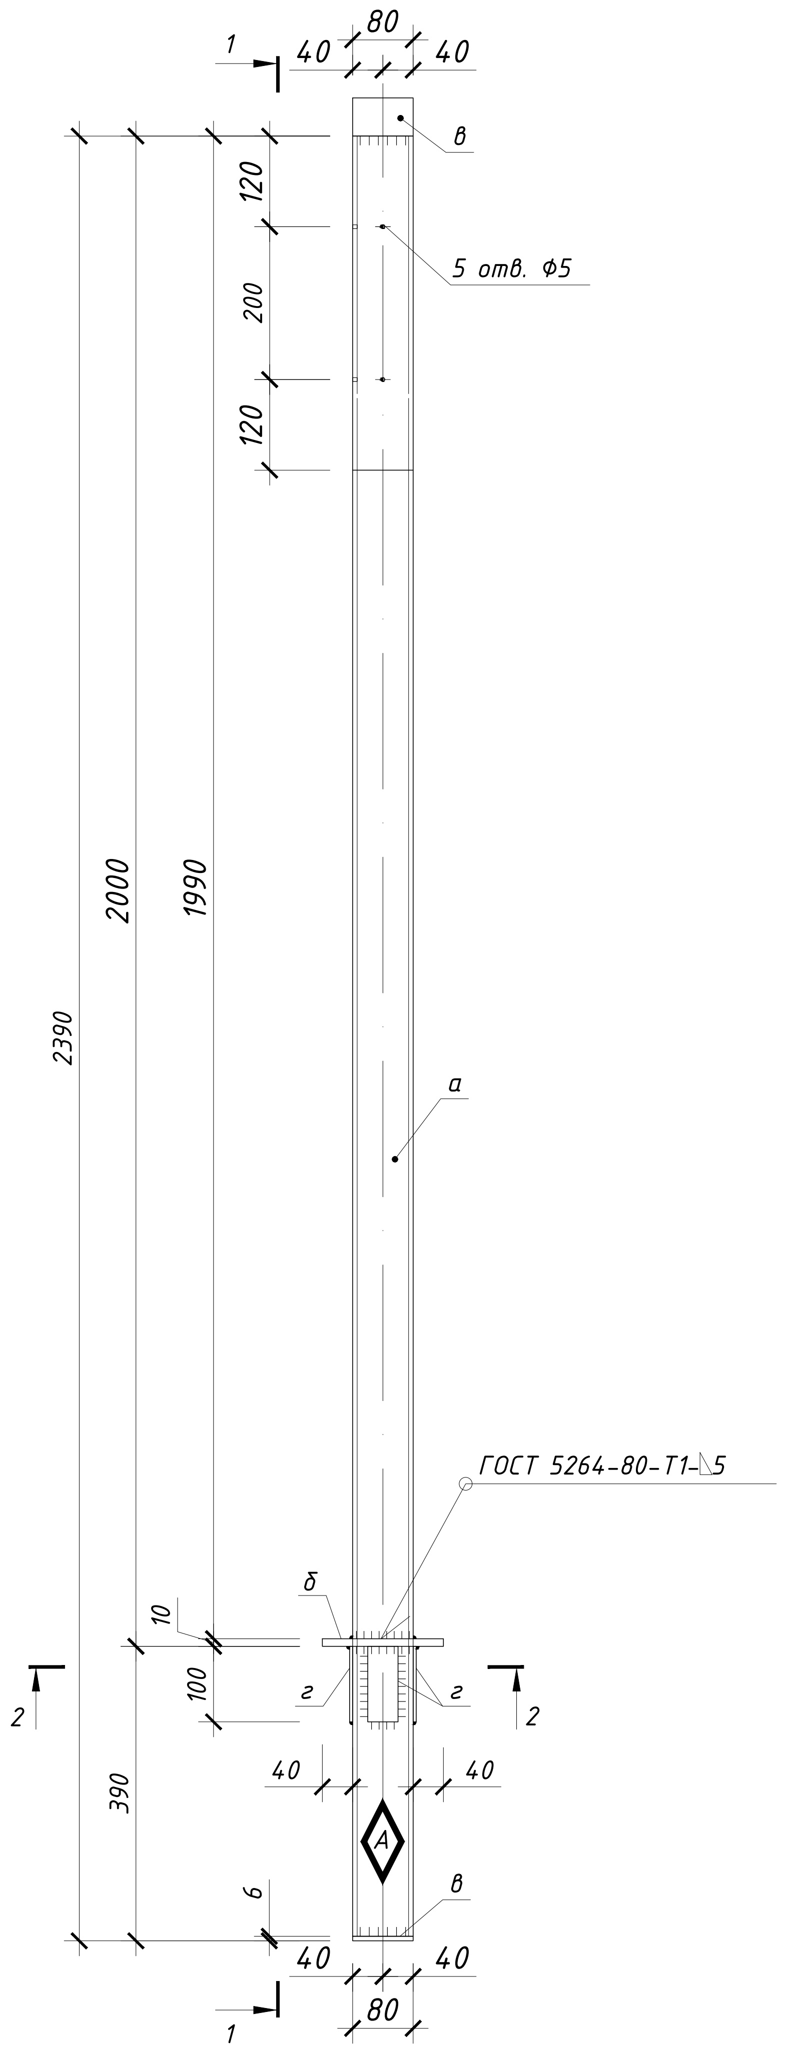

1-1

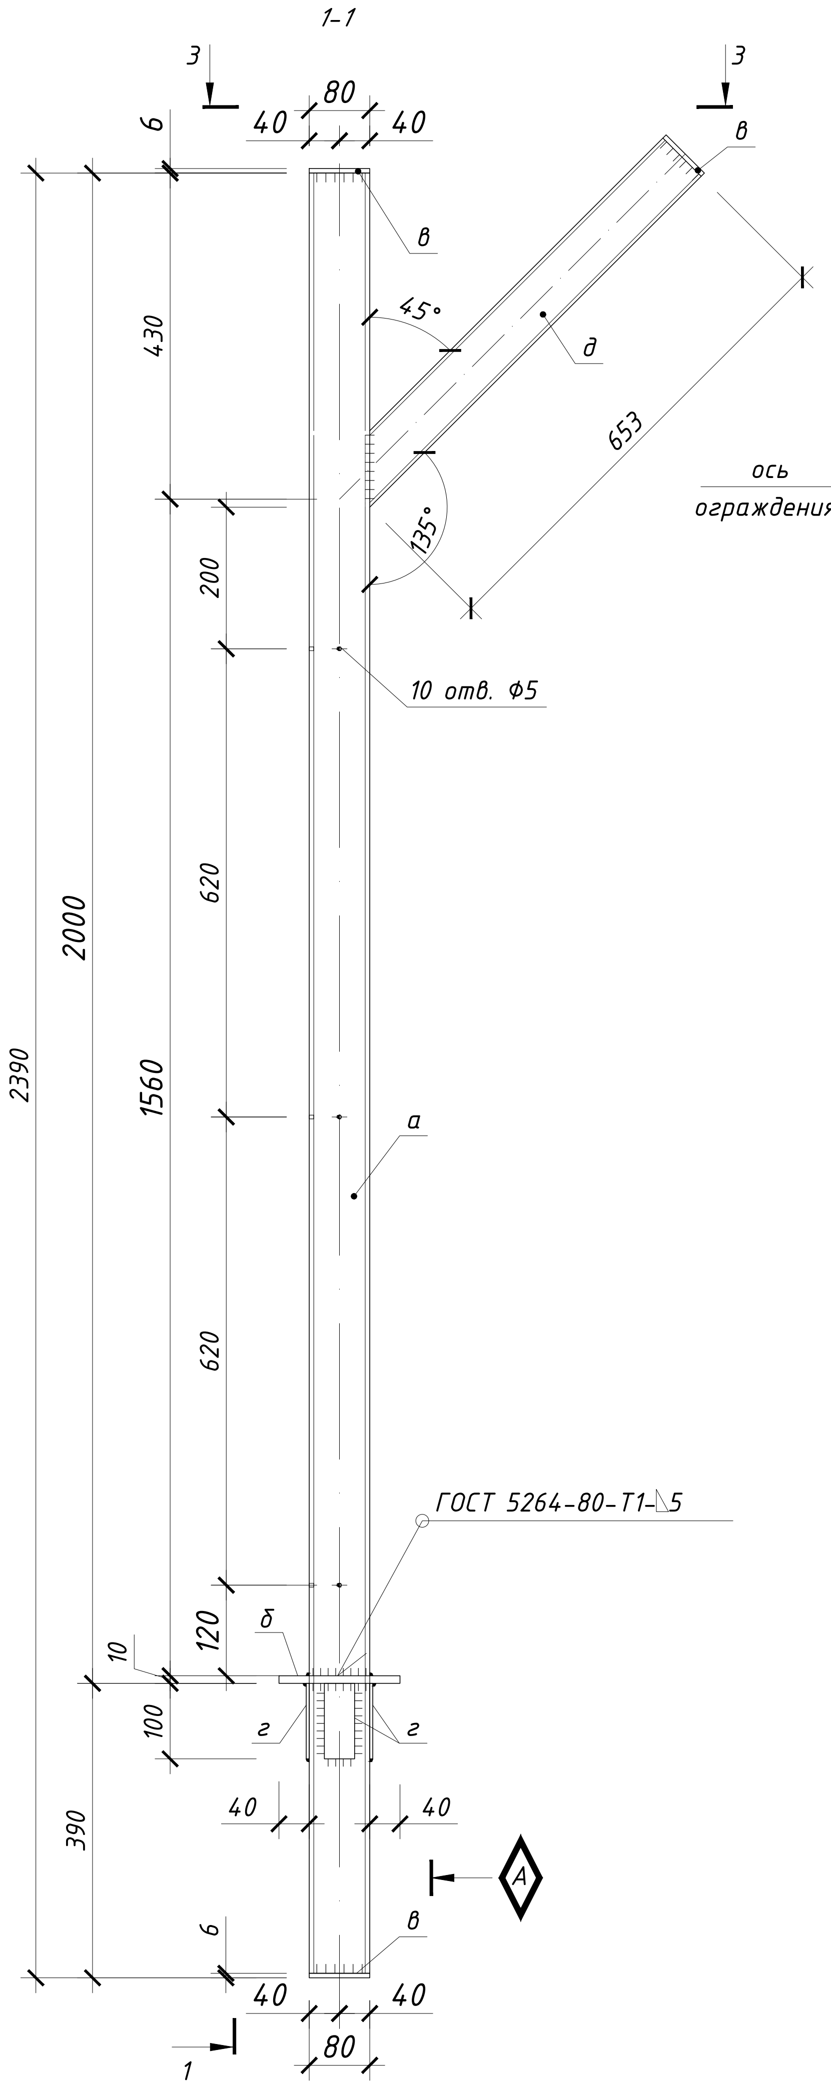

2-2

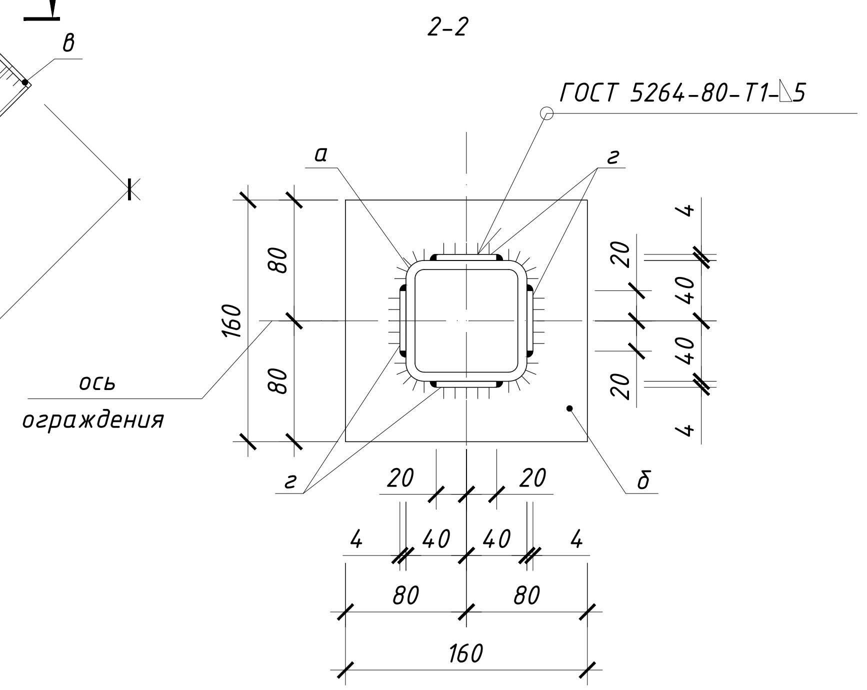

Позиция "б".

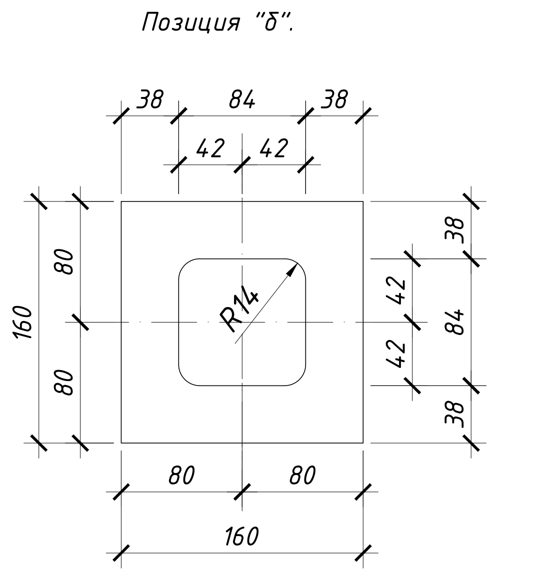

3-3

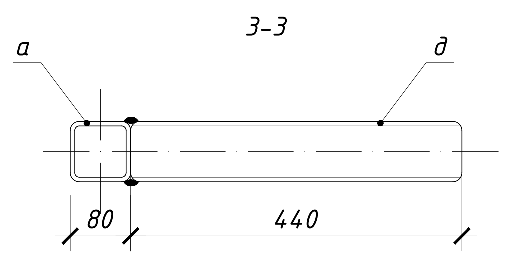

Деталь 1 срезки подкоса (поз. д)

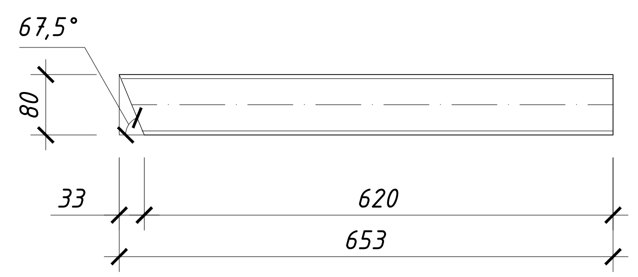

Спецификация элементов на одну марку

Марка поз.	Обозначение	Наименование	Кол. шт.	Масса ед.кг	Примечание
Ст2		Стойка ограждения Ст2		31.65	вес на 1 стойку
а		Гн.пр $\frac{\text{80x80x4 ГОСТ 30245-2003}}{\text{С255-ГК ГОСТ 27772-2015}}$ L=2390мм	1	22.30	22.30
б		Лист $\frac{\text{Б-ПН-10x160x160 ГОСТ 19903-2015}}{\text{С245-ГК ГОСТ 27772-2015}}$	1	2,01	2,01
в		Лист $\frac{\text{Б-ПН-4x80x80 ГОСТ 19903-2015}}{\text{С245-ГК ГОСТ 27772-2015}}$	3	0,20	0,6
г		Лист $\frac{\text{Б-ПН-4x40x124 ГОСТ 19903-2015}}{\text{С245-ГК ГОСТ 27772-2015}}$	4	0,16	0,64
д		Гн.пр $\frac{\text{80x80x4 ГОСТ 30245-2003}}{\text{С255-ГК ГОСТ 27772-2015}}$ L=653мм	1	6.10	6.10
		Материалы:			
		Окраска металлоконструкций масляной краской за 2 раза			1,09м²

*- Гн.пр - Гнутые профили

Примечания:
1. Сварку вести электродами Э42А ГОСТ 9467-75.
2. Конструкция должна быть покрыта масляной краской за 2 раза по грунтовке.
3. Элемент "г" следует приварить к "а" в первую очередь.
4. Деталь-1 - деталь срезки подкоса. (поз. д)
5. Крепления стойки смотри Фундамента ФМЛ1.

◇А - Знак ориентации. Нанести несмываемой краской!

● Отверстие для болта
◈ Болт постоянный, нормальной точности
♦ Болт временный, нормальной точности
┆┆┆┆┆ Сварной шов заводской
xxxxx Сварной шов монтажный

Рев	Дата	Назначение ревизии	Проверил	Утвердил
А1	09.09.2026	Выпущено для строительства		
R1	27.07.2026	Выпущено для рассмотрения		

ЗАКАЗЧИК: UTG UZTRANSGAZ «TRANSGAZINJINIRING»
ГЕНЕРАЛЬНЫЙ ПОДРЯДЧИК: UET UZBEKENERGOTAMIR
ПОДРЯДЧИК: PBG Pro Build Generation
ГЕНЕРАЛЬНЫЙ ПРОЕКТИРОВЩИК: EAST WEST ENGINEERING

EWE0426-MGL1-STR-054-DRW-760509-A1

«СТРОИТЕЛЬСТВО НОВЫХ НИТОК (УЧАСТКОВ) ГАЗОПРОВОДОВ «ГАЗЛИ - САРИМОЙ» И «АКЧАЛОК - ГАЗЛИ - НУКУС» ОБЩЕЙ ПРОТЯЖЕННОСТЬЮ НЕ МЕНЕЕ 275 КМ».

Изм.	Кол.уч.	Лист	№ док.	Подпись	Дата
ГИП		Кирпичников С.			09.09.26
Нач.отд.		Каршиев А.			09.09.26
Исполн.		Юлдашев Ж.			09.09.26
Н.контр		Кирпичников С.			09.09.26

ГАЗОПРОВОД "ГАЗЛИ-САРИМОЙ" (54 КМ)
Линейный крановый узел DN1000 КУП-D7

Стадия	Лист	Листов
РП	1	1

Стойка ограждения Ст2

EAST WEST ENGINEERING
ООО "EAST-WEST Engineering"
г. Ташкент 2026г.

Взам. инв. №
Подпись и дата
Инв.№ подл.

Формат / Format A4X3