Стойка ограждения Ст3

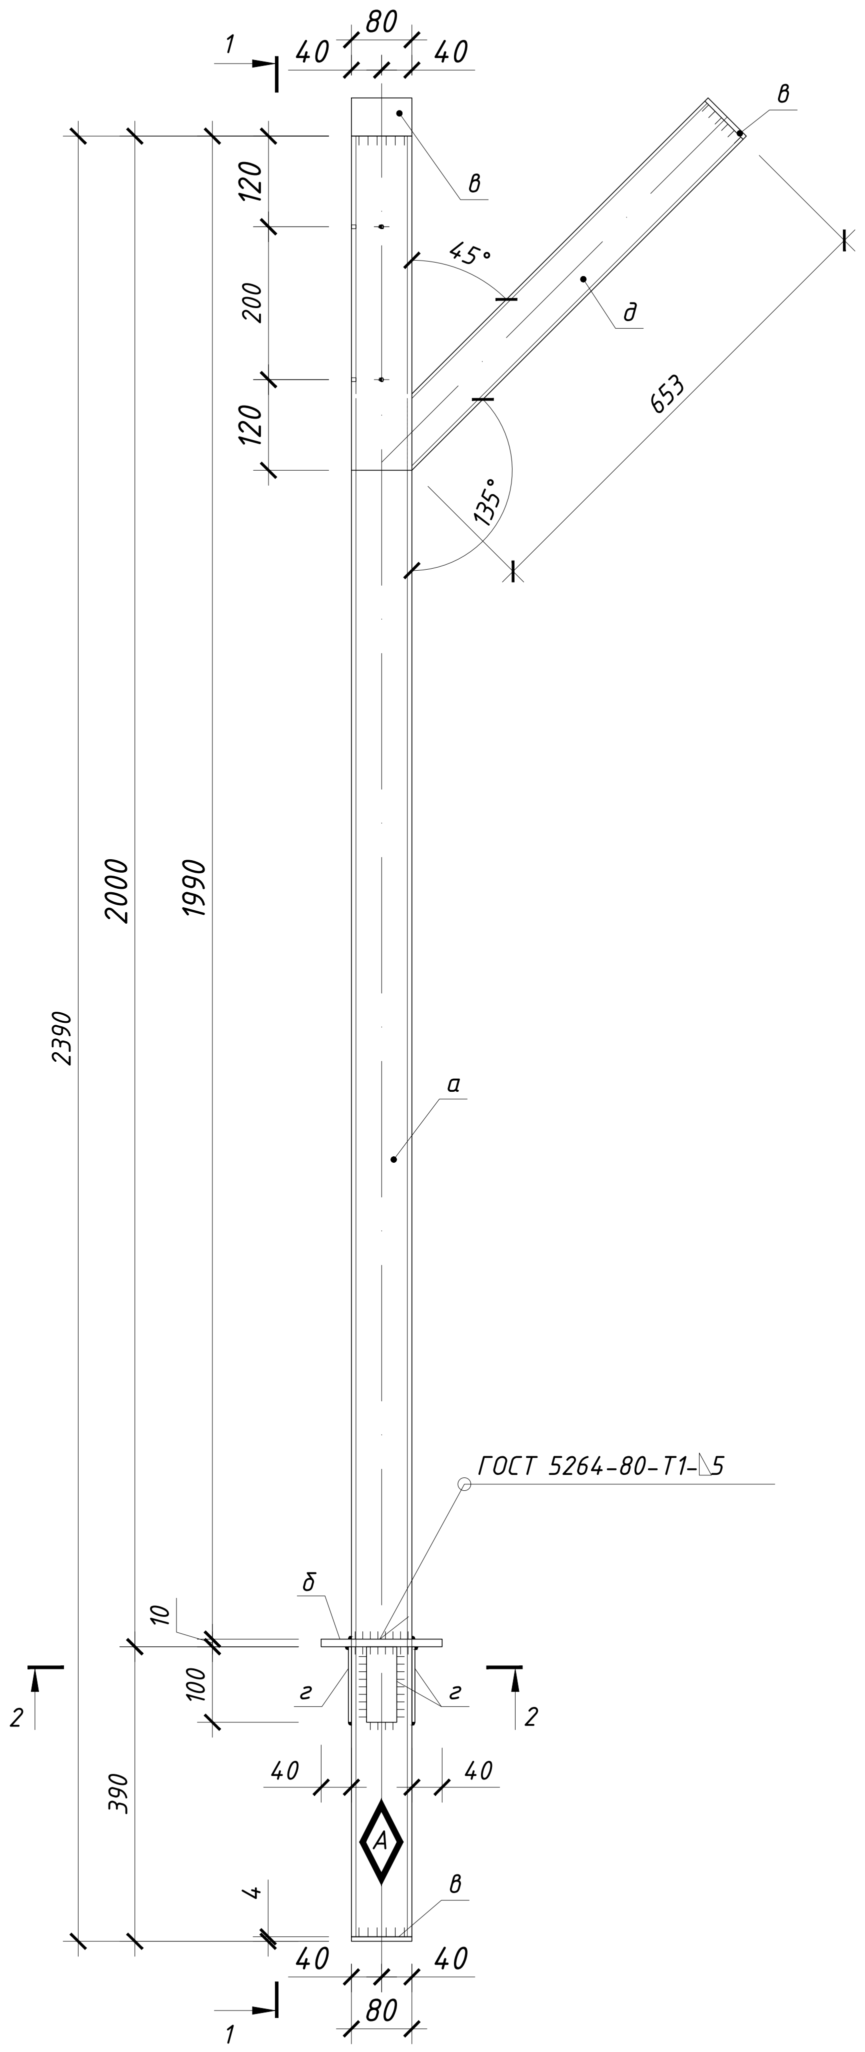

1-1

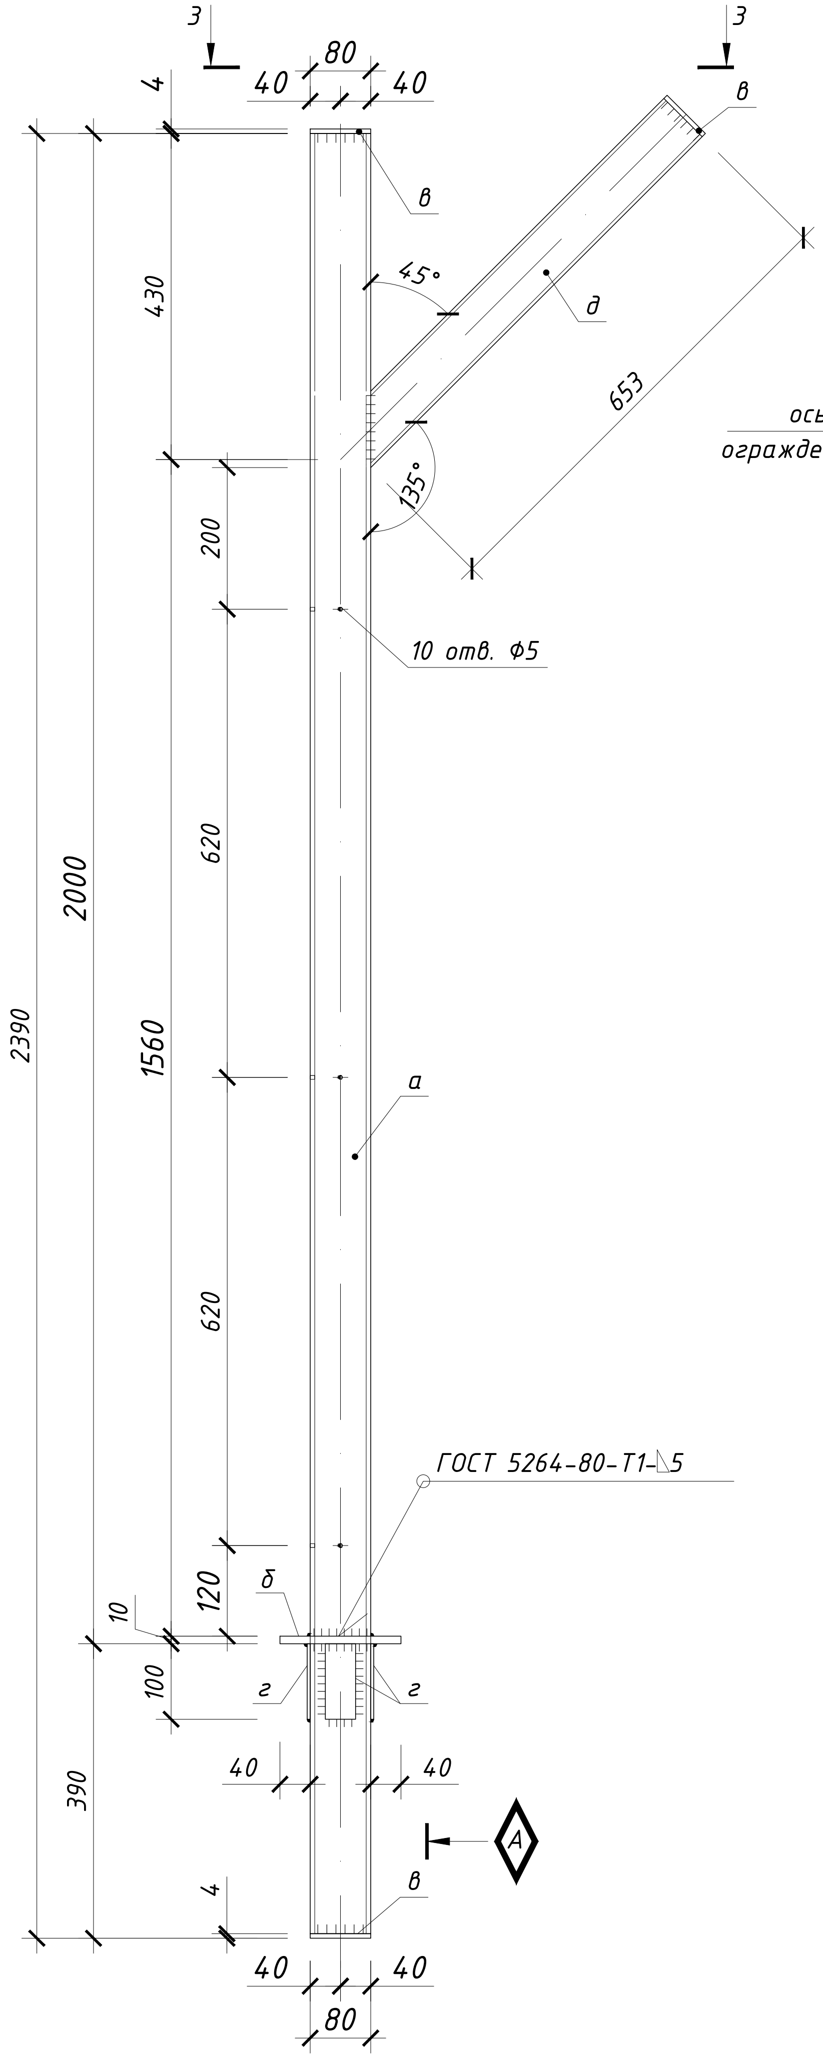

2-2

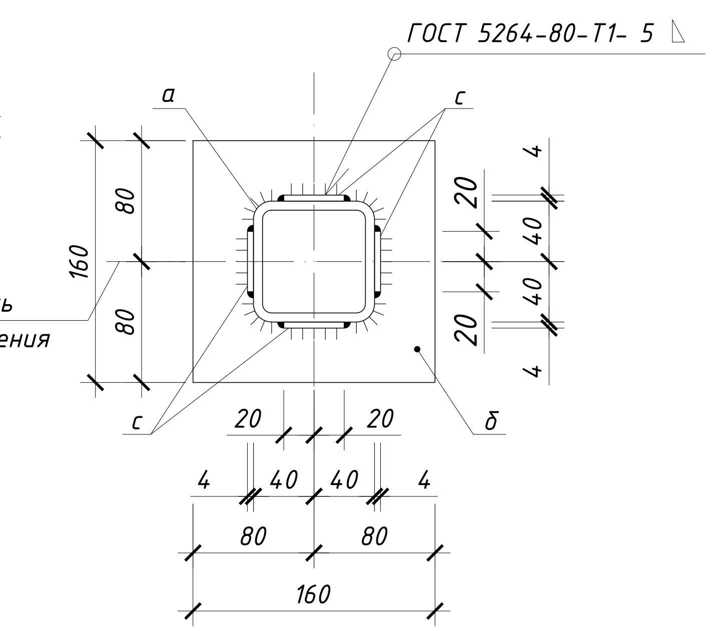

ось ограждения

Позиция "б"

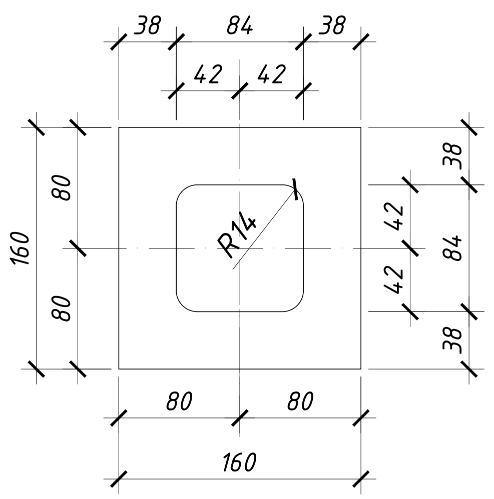

3-3

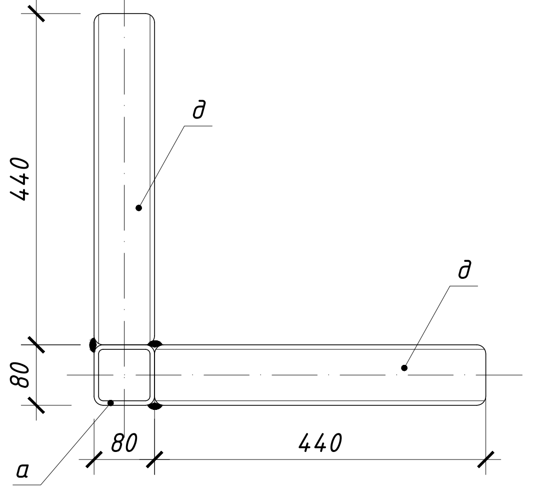

Деталь-1 срезки подкоса (поз. д)

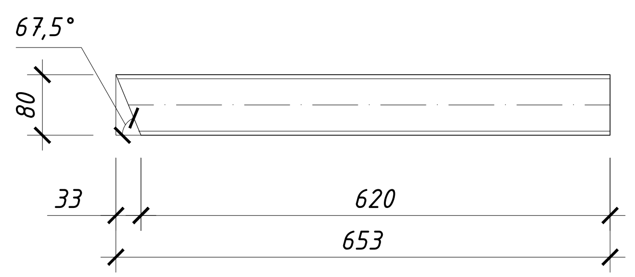

Спецификация элементов на одну марку

Марка поз.	Обозначение	Наименование	Кол. шт.	Масса ед.кг	Примечание
Ст3		Стойка ограждения Ст-3		37.95	вес на 1 стойку
а		Гн.пр 80х80х4 ГОСТ 30245-2003 / С255-ГК ГОСТ 27772-2015 L=2390мм	1	22.3	22.3
б		Лист Б-ПН-10х160х160 ГОСТ 19903-2015 / С245-ГК ГОСТ 27772-2015	1	2,01	2,01
в		Лист Б-ПН-4х80х80 ГОСТ 19903-2015 / С245-ГК ГОСТ 27772-2015	4	0,20	0,8
г		Лист Б-ПН-4х40х124 ГОСТ 19903-2015 / С245-ГК ГОСТ 27772-2015	4	0,16	0,64
д		Гн.пр 80х80х4 ГОСТ 30245-2003 / С255-ГК ГОСТ 27772-2015 L=653мм	2	6.10	12.20
		Материалы:			
		Окраска металлоконструкций масляной краской за 2 раза			1,31м²

Примечания:
1. Сварку вести электродами Э42А ГОСТ 9467-75.
2. Конструкция должна быть покрыта масляной краской за 2 раза по грунтовке.
3. Элемент "г" следует приварить к "а" в первую очередь.
4. Деталь-1 - деталь срезки подкоса (поз. д)
5. Крепления стойки смотри лист Фундамента ФМЛ1.

◇A - Знак ориентации. Нанести несмываемой краской!

● Отверстие для болта
⊕ Болт постоянный, нормальной точности
◆ Болт временный, нормальной точности
Сварной шов заводской
Сварной шов монтажный

Рев	Дата	Назначение ревизии	Проверил	Утвердил
A1	09.09.2026	Выпущено для строительства		
R1	27.07.2026	Выпущено для рассмотрения		

ЗАКАЗЧИК: UTG UZTRANSGAZ «TRANSGAZINJINIRING»
ГЕНЕРАЛЬНЫЙ ПОДРЯДЧИК: UET UZBEKENERGOTAMIR
ПОДРЯДЧИК: PBG Pro Build Generation
ГЕНЕРАЛЬНЫЙ ПРОЕКТИРОВЩИК: EAST WEST ENGINEERING

EWE0426-MGL1-STR-054-DRW-760510-A1

«СТРОИТЕЛЬСТВО НОВЫХ НИТОК (УЧАСТКОВ) ГАЗОПРОВОДОВ «ГАЗЛИ - САРИМОЙ» И «АКЧАЛОК - ГАЗЛИ - НУКУС» ОБЩЕЙ ПРОТЯЖЕННОСТЬЮ НЕ МЕНЕЕ 275 КМ».

Изм.	Кол.уч.	Лист	№ док.	Подпись	Дата
ГИП		Кирпичников С.			09.09.26
Нач.отд.		Каршиев А.			09.09.26
Исполн.		Юлдашев Ж.			09.09.26
Н.контр		Кирпичников С.			09.09.26

ГАЗОПРОВОД "ГАЗЛИ-САРИМОЙ" (54 КМ)
Линейный крановый узел DN1000 КУП-D7

Стадия	Лист	Листов
РП	1	1

Стойка ограждения Ст3.

EAST WEST ENGINEERING
ООО "EAST-WEST Engineering"
г. Ташкент 2026г.

Формат / Format A4X3

Взам. инв. №
Подпись и дата
Инв.№ подл.