Панель ограждения П1 м 1:25.

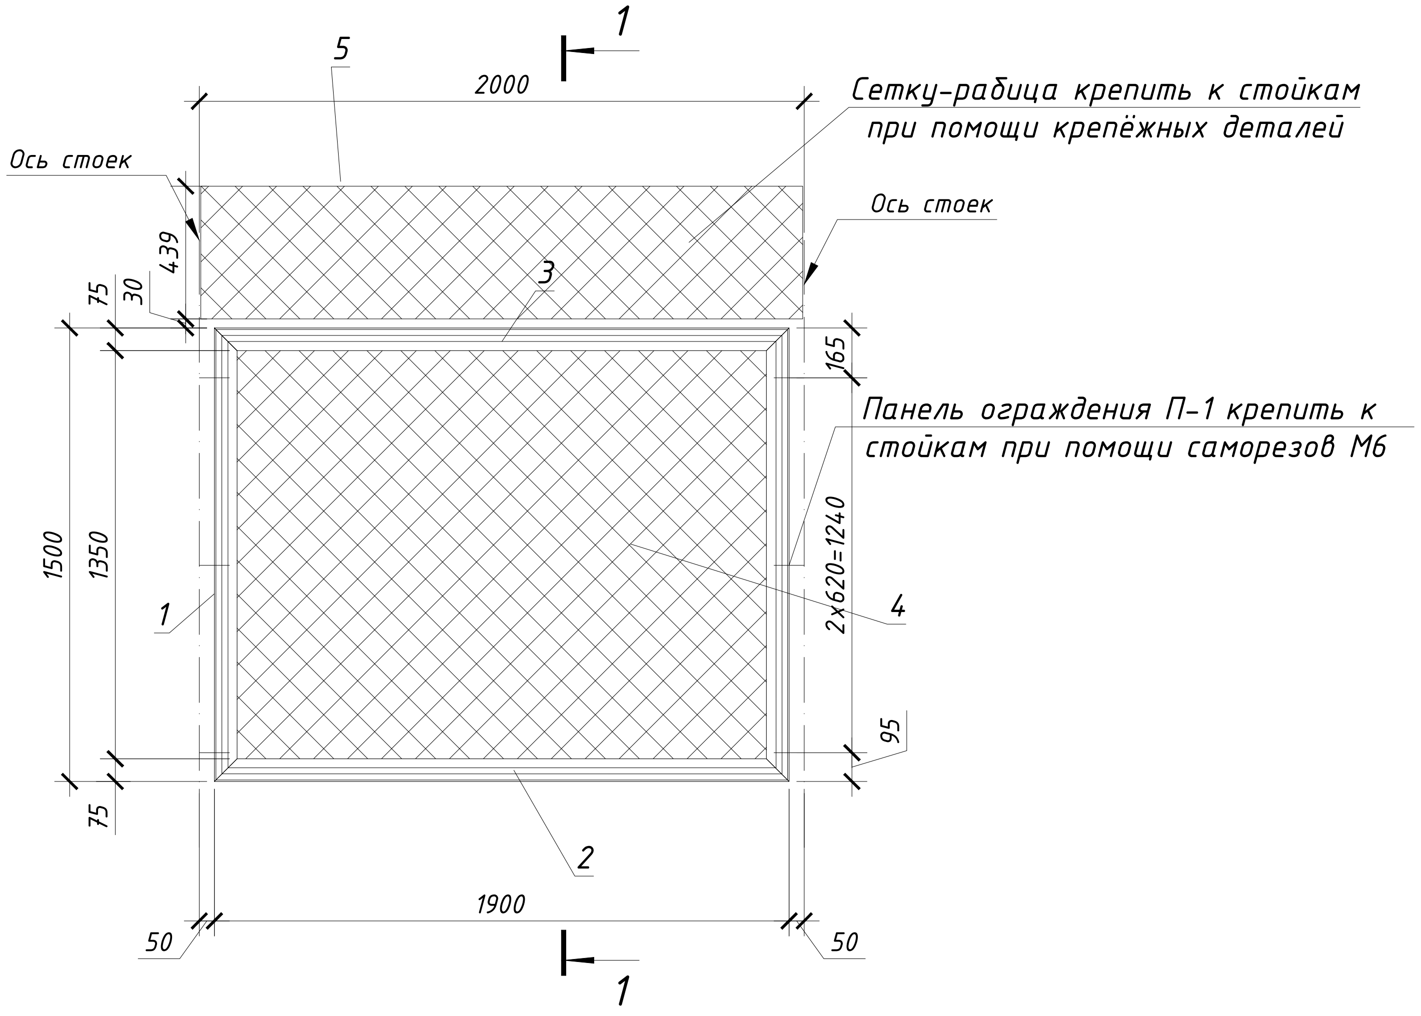

Сетку-рабица крепить к стойкам при помощи крепёжных деталей

Панель ограждения П-1 крепить к стойкам при помощи саморезов М6

Разрез 1-1 м 1:50.

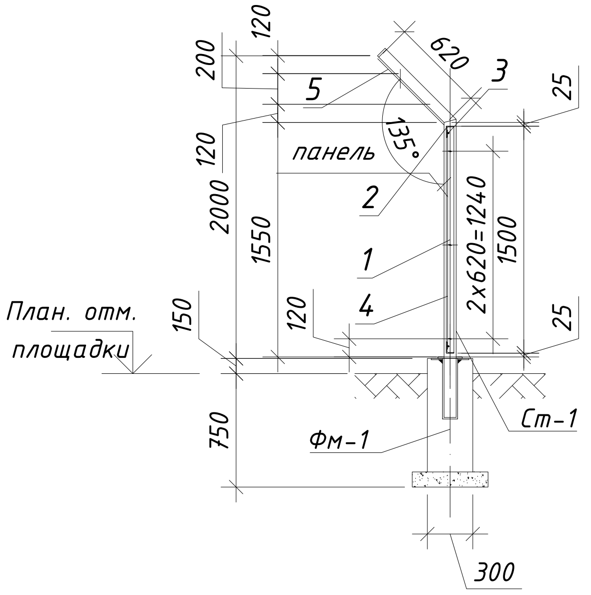

Спецификация расхода материалов

Марка Поз.	Обозначение	Наименование	Кол. шт.	Масса ед.кг.	Примечание
П-1		Панель ограждения П1		43,55	вес на 1 шт.
1	ГОСТ 8510-93, Сталь С235	L75x50x5 L=1500	2	7.19	14.37
2	ГОСТ 8510-93, Сталь С235	L75x50x5 L=1900	2	9.10	18.20
3	ГОСТ 34028-2016	Арматура Ф6.0 А240 Lобщ=6440	1	0.222 кг/м.п	1.43
4	ГОСТ 5336-80*	Сетка рабица №50-3.0,размером			
		1450 х 1870мм; S=2.71м2	1	2,42 кг/м2	6.56
5	ГОСТ 5336-80*	Сетка рабица №50-3.0,размером			
		620 х 1990мм; S=1.23м2	1	2,42 кг/м2	2.99
		Материалы:			
		Окраска металлоконструкций масляной краской за 2 раза			$1{,}71м^2$

Примечания:

1. Сварку вести электродами Э42А ГОСТ9467-75.
2. Конструкция должна быть покрыта масляной краской за 2 раза по грунтовке.

Рев	Дата	Назначение ревизии	Проверил	Утвердил
A1	09.09.2026	Выпущено для строительства		
R1	27.07.2026	Выпущено для рассмотрения		

ЗАКАЗЧИК: UTG UZTRANSGAZ «TRANSGAZINJINIRING»

ГЕНЕРАЛЬНЫЙ ПОДРЯДЧИК: UET UZBEKENERGOTAMIR

ПОДРЯДЧИК: PBG Pro Build Generation

ГЕНЕРАЛЬНЫЙ ПРОЕКТИРОВЩИК: EAST WEST ENGINEERING

EWE0426-MGL1-STR-054-DRW-760511-A1

«СТРОИТЕЛЬСТВО НОВЫХ НИТОК (УЧАСТКОВ) ГАЗОПРОВОДОВ «ГАЗЛИ - САРИМОЙ» И «АКЧАЛОК - ГАЗЛИ - НУКУС» ОБЩЕЙ ПРОТЯЖЕННОСТЬЮ НЕ МЕНЕЕ 275 КМ».

Изм.	Кол.уч.	Лист	№ док.	Подпись	Дата
ГИП		Кирпичников С.			09.09.26
Нач.отд.		Каршиев А.			09.09.26
Исполн.		Юлдашев Ж.			09.09.26
Н.контр		Кирпичников С.			09.09.26

ГАЗОПРОВОД "ГАЗЛИ-САРИМОЙ" (54 КМ)
Линейный крановый узел DN1000 КУП-D7

Стадия	Лист	Листов
РП	1	1

Панель ограждения П1

EAST WEST ENGINEERING
ООО "EAST-WEST Engineering"
г. Ташкент 2026г.

Взам. инв. №
Подпись и дата
Инв.№ подл.

Формат / Format A3