


ВИД

Калитка К1 м 1:25.

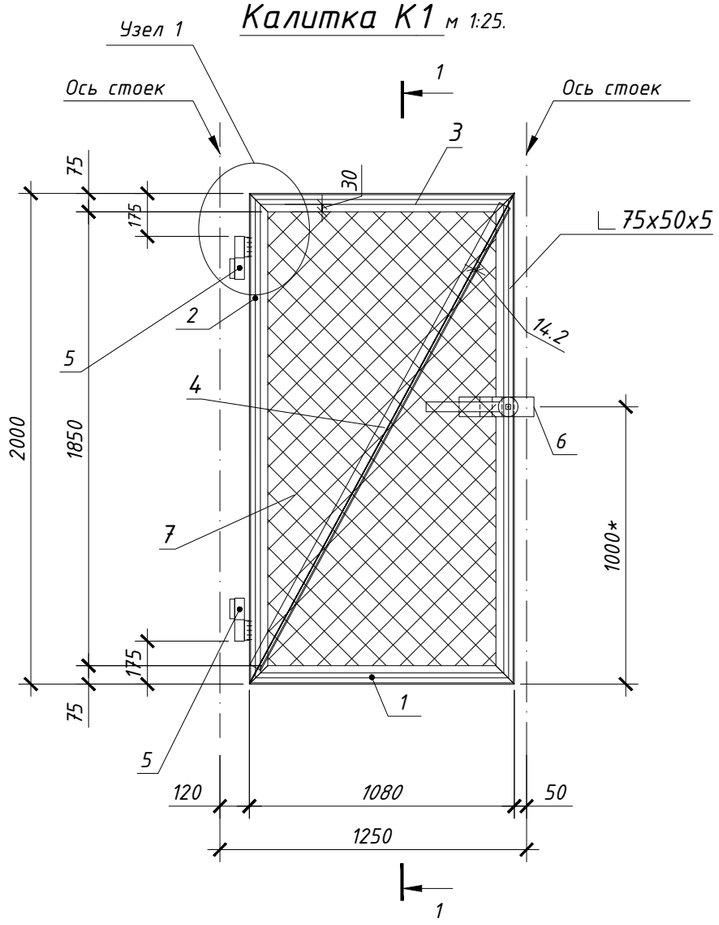

Разрез 1-1 м 1:25.

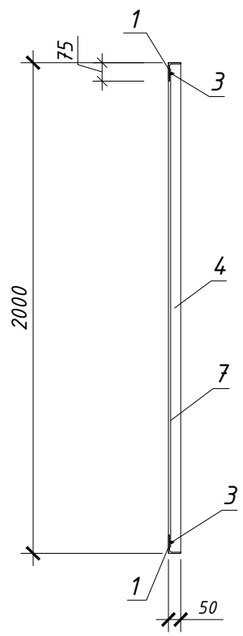

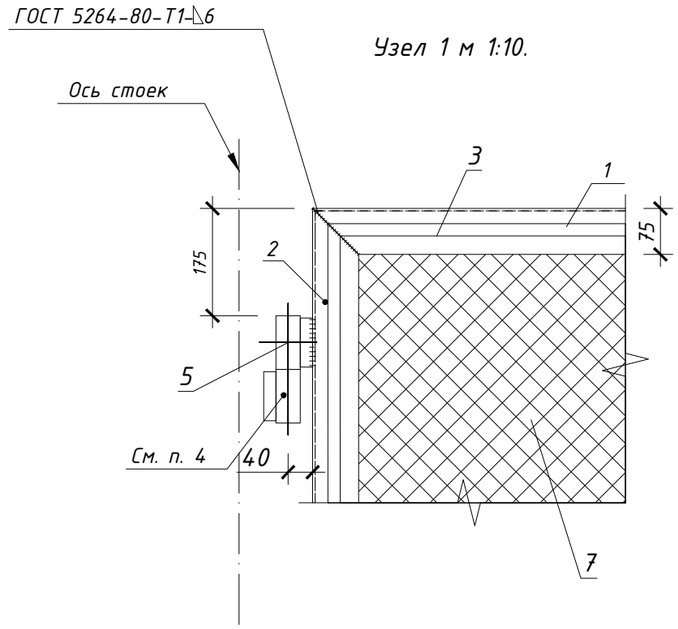

Спецификация расхода материалов

Марка Поз.	Обозначение	Наименование	Кол. шт.	Масса ед., кг	Приме-чание
К-1		Калитка К1		47,73	вес на 1 шт.
1	ГОСТ 8510-93*, Сталь С235	L75x50x5 L=1080	2	5.17	10.35
2	ГОСТ 8510-93*, Сталь С235	L75x50x5 L=2000	2	9.58	19.16
3	ГОСТ 34028-2016	Арматура ф6.0 А240 Lобщ=5800	1	0.222 кг/м.п	1.29
4	ГОСТ 8509-93*, Сталь С235	L50x50x5 L=2140	1	8.07	8.07
5	Серия 3.017-1.05.110.100	Петля крепления калитки	2	2,0	4,0
6		ЭМЗУ типа "Базальт"	1		или аналог
7	ГОСТ 5336-80*	Сетка рабица №50-3.0,размером			
		1030 x 1950мм; S=2.01м2	1	2,42 кг/м2	4.86
		Материалы:			
		Окраска металлоконструкций масляной краской за 2 раза			1,99м²

Примечания:

1. *Сварку вести электродами Э42А ГОСТ9467-85 по РСтУз 865-98*
2. *Конструкция должна быть покрыта масляной краской за 2 раза по грунтовке.*
3. *Сетку прикрепить к элементам обрамления калитки.*
4. *Применять петлю по серии 3.017-1.05.110.100 (2шт.). Петли свариваются к полотну калитки.*
5. *Крепления замка установить по месту.*
6. *Калиток К1 изготовить в количестве 2 шт.*

Рев	Дата	Назначение ревизии	Проверил	Утвердил
A1	09.09.2026	Выпущено для строительства		
R1	27.07.2026	Выпущено для рассмотрения		

ЗАКАЗЧИК: UTG UZTRANSGAZ «TRANSGAZKLIMRING»

ГЕНЕРАЛЬНЫЙ ПОДРЯДЧИК: UET ÖZBEKENERGOTAMIR

ПОДРЯДЧИК: PBG Pro Build Generation

ГЕНЕРАЛЬНЫЙ ПРОЕКТИРОВЩИК: EAST WEST ENGINEERING

Изм.	Кол.уч.	Лист	№ док.	Подпись	Дата
ГИП		Кирпичников С.			09.09.26
Нач.отд.		Каршиев А.			09.09.26
Исполн.		Юлдашев Ж.			09.09.26
Н.контр		Кирпичников С.			09.09.26

EWE0426-MGL1-STR-054-DRW-760514-A1

«СТРОИТЕЛЬСТВО НОВЫХ НИТОК (УЧАСТКОВ) ГАЗОПРОВОДОВ «ГАЗЛИ - САРИМОЙ» И «АКЧАЛОК - ГАЗЛИ - НУКУС» ОБЩЕЙ ПРОТЯЖЕННОСТЬЮ НЕ МЕНЕЕ 275 КМ».

ГАЗОПРОВОД "ГАЗЛИ-САРИМОЙ" (54 КМ)
Линейный крановый узел DN1000 КУП-D7

Стадия	Лист	Листов
РП	1	1

Калитка К1

ООО "EAST-WEST Engineering"
г. Ташкент 2026г.

Взам. инв. №

Подпись и дата

Инв.№ подл.

Формат / Format А3