


Поз.	Обозначение	Наименование	Кол.	Масса ед., кг	Приме-чание
1	ЛСЭ-300	Лента сигнальная	32		м
2	ТУ 2248-019-47022248-2008	Жесткая двустенная гофрированная труба для прокладки в грунте и под автомобильными дорогами, ПНД, ф75мм	5		м
3	ТУ 2248-015-47022248-2006	Труба жесткая гладкая ПНД Ø75 мм для защиты кабельных линий, для прокладки в грунте и на открытом воздухе, УФ-стойкая, без протяжки.	3		м
4	ТУ 2247-011-79523310-2006	Термоусадочная трубка с коэффициентом усадки 2:1 ТНТнг-LS-100/50	2		м


План 1 (1:50)

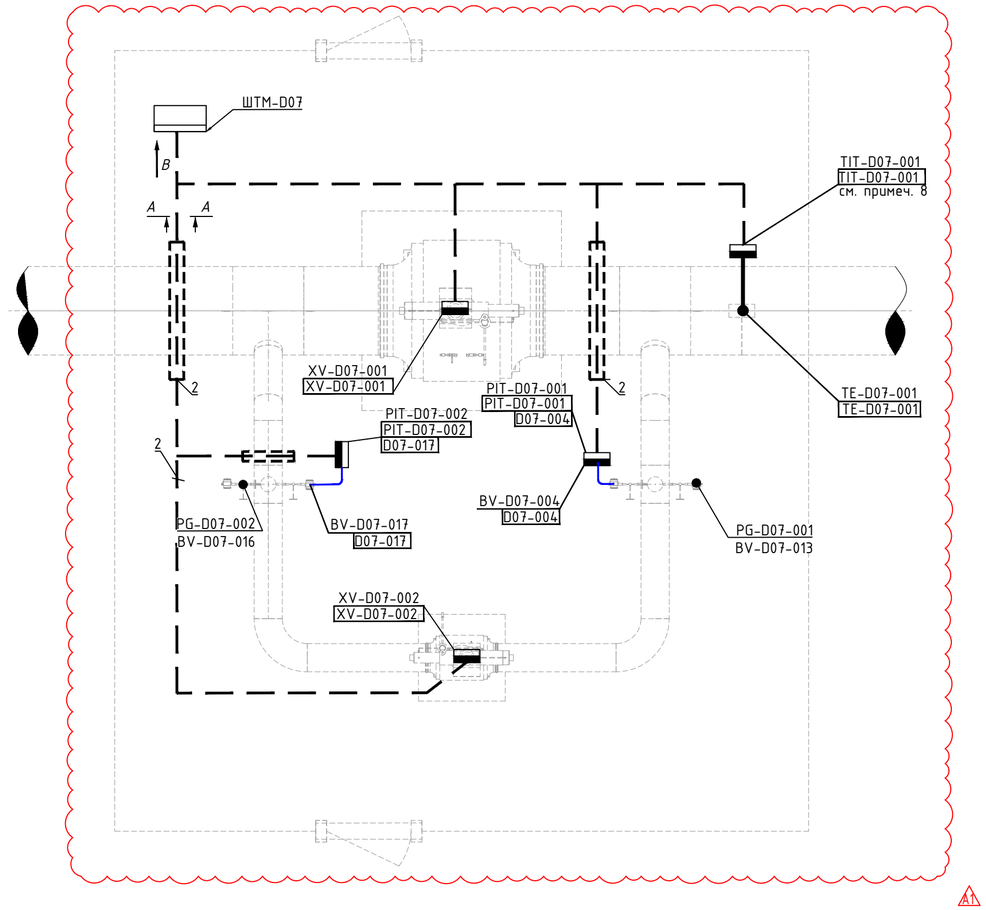


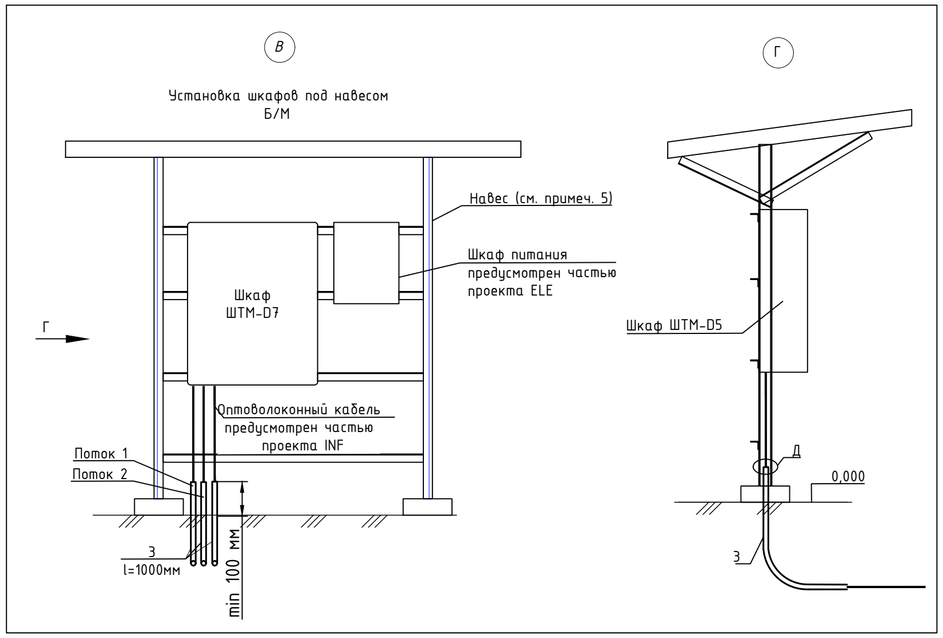

1. Данный чертёж разработан для крановых узлов на основании чертежа EWE0426-MGL1-PRE-054-DRW-760205.
2. Позиции приборов и нумерация кабелей соответствует схеме соединений внешних проводок EWE0426-MGL1-SYS-054-SCM-750305.
3. Все приборы, находящиеся под напряжением, заземлить согласно ПУЭ и руководствам по эксплуатации на приборы.
4. Монтаж защитного заземления выполнить в соответствии с требованиями ПУЭ.
5. Шкаф телемеханики установить под навесом,предусмотрен частью проекта STR. Отверстия для крепления шкафа сверлить по месту.
6. При прокладке кабелей в земле в ПНД трубах выполнить уплотнение кабеля с обоих концов труб джутовыми плетеными шнурами, обмазанными водонепроницаемой (мятой) глиной на глубину не менее 300 мм., согласно узлу Б.
7. При пересечении в земле кабелем КИП технологических трубопроводов кабель проложить на расстоянии не менее 0,25 м в свету по вертикали от трубопровода. На участке пересечения, а также на расстоянии по 2 м в каждую сторону от него, кабель проложить в трубе ПНД двустенной жесткой.
8. Установка приборов на стойке КИПиА см. документ EWE0426-MGL1-SYS-054-DRW-760302.
9. За относительную отметку 0,000 принята проектная отметка уровня земли.
10. Земляные работы на территории площадки производить ручным методом.

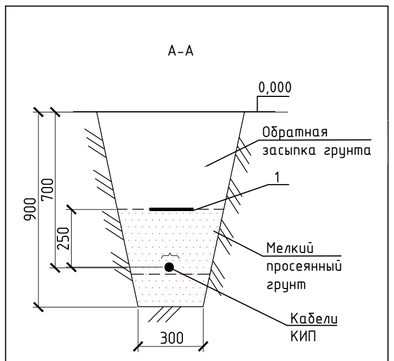

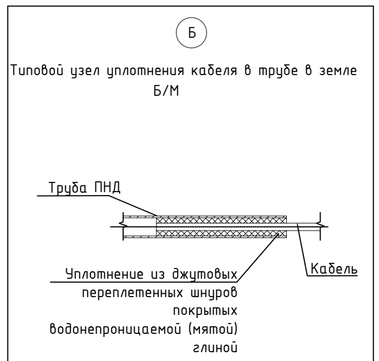

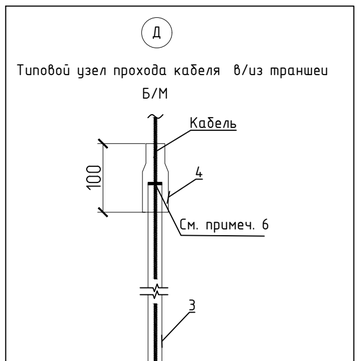

Рев.	Дата	Назначение ревизии	Проверил	Утвердил
A1	18.08.2026	Утверждено для строительства		
R1	13.07.2026	Выпущено для рассмотрения		

ЗАКАЗЧИК: UTG ГЕНЕРАЛЬНЫЙ ПОДРЯДЧИК: UET ПОДРЯДЧИК: PBG ГЕНЕРАЛЬНЫЙ ПРОЕКТИРОВЩИК: EAST WEST ENGINEERING

Изм.	Кол.уч.	Лист	№док.	Подпись	Дата
ГИП		Схабицкий А.			08.2026
Нач.отд.		Кабулова Е.			08.2026
Исполн.		Махмудов И.			08.2026
Н.контр		Схабицкий А.			08.2026

EWE0426-MGL1-SYS-054-PLA-760306-A1

«СТРОИТЕЛЬСТВО НОВЫХ НИТОК (УЧАСТКОВ) ГАЗОПРОВОДОВ «ГАЗЛИ - САРИМОЙ» И «АКЧАЛОК - ГАЗЛИ - НУКУС» ОБЩЕЙ ПРОТЯЖЕННОСТЬЮ НЕ МЕНЕЕ 275 КМ».

Газопрвод «Газли-Сарымой» (54 КМ)
Линейный крановый узел DN1200 КУП-D7

Стадия	Лист	Листов
РД	1	1

План расположения оборудования и проводок

ООО "EAST-WEST Engineering"
г. Ташкент 2026г.

Взам. инв. №
Подпись и дата
Инв.№ подл.

Формат / Format A2