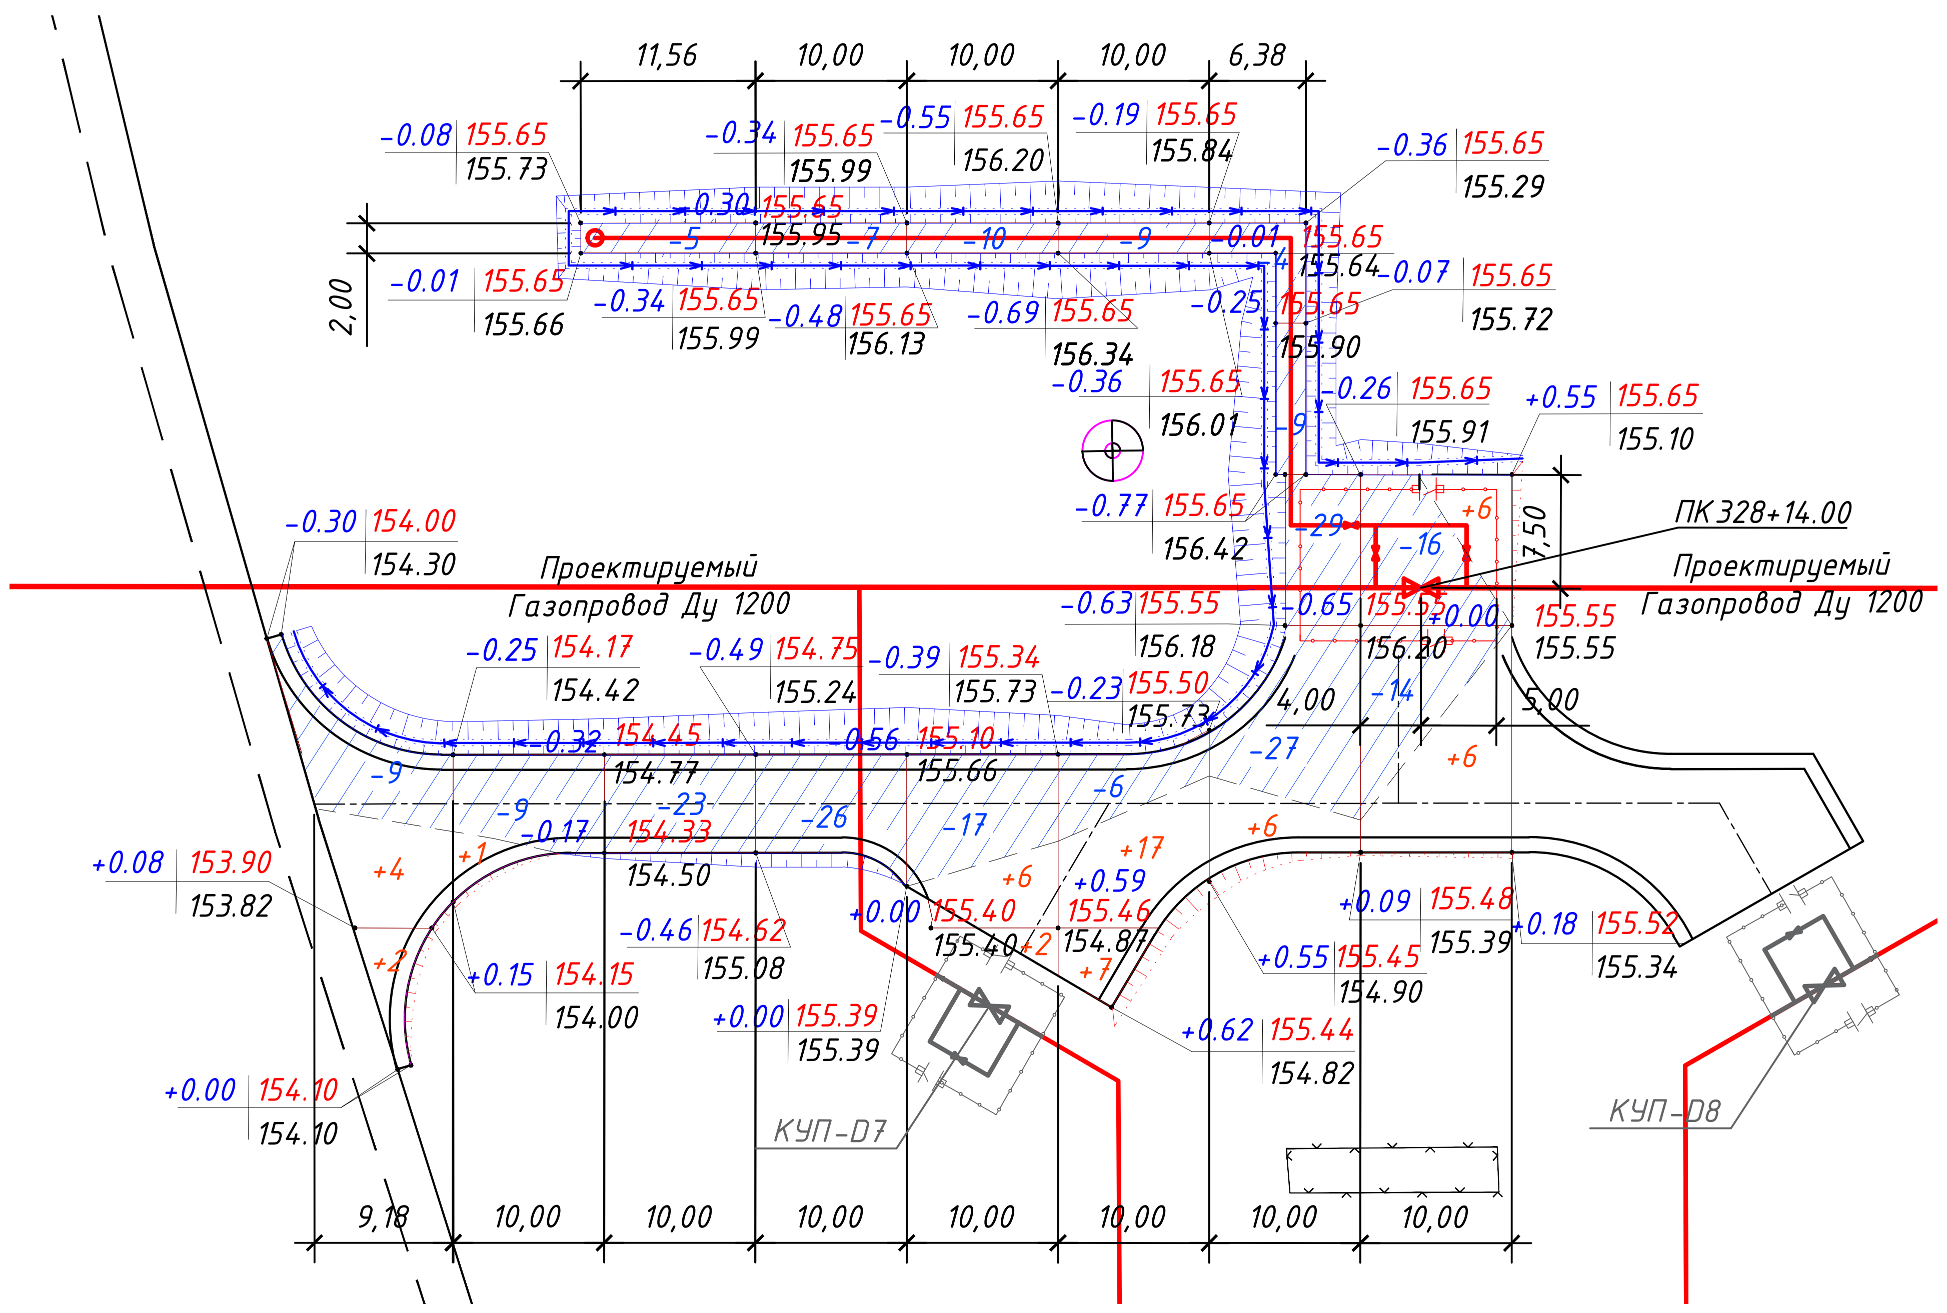

Итого,м3									Всего,м3	
	Насыпь (+)	+6	+1	--	--	+8	+24	+6	+12		+57
	Выемка (-)	-9	-9	-28	-33	-27	-15	-69	-30		-220

Ведомость объемов земляных масс

Наименование грунта	Количество, м^3		Примечание
	Насыпь (+)	Выемка (-)	
1. Грунт планировки территории	57	220	
2. Вытесненный грунт, в т.ч. при устройстве:			
а) автодорожных покрытий		249	
б) покрытий площадок		16	
в) водоотводной канавы		88	
г) плодородной почвы на участках насыпи			
д) плодородной почвы на участках выемки			
3. Замена растительного грунта на участках насыпи			
4. Грунт для устройства откосов насыпи	6		
5. Грунт для устройства откосов выемки		26	
6. Поправка на уплотнение	6.3		
Всего пригодного грунта	69.3	599	
7. Избыток пригодного грунта	529.7		
8. Плодородный грунт, всего в т.ч.:		346.2	
а) Используемый для озеленения территории			
б) Избыток плодородного грунта	346.2		
(рекультивация земель)			
9. Итого перерабатываемого грунта	945.2	945.2	

* С учетом плодородного грунта.

** В карьере. Общая площадь картограммы = 1154 м2

Условные обозначения:

+1	объем насыпи в м^3
-3	объем выемки в м^3
+0.38 | 155.20 154.82	рабочая отм. | проектная отм. отм.сущ.рельефа
⊥⊥⊥⊥⊥⊥	откосы насыпи
⊥⊥⊥⊥⊥⊥	откосы выемки

Примечания:

При составлении настоящего чертежа были использованы :

1. Сетка картограммы привязана линейно к пикету ПК 328+14.00.
2. Сетка квадратов объёмы земляных масс разбита на ячейки размерами 10х10м.
3. Производство земляных работ вести в требованиях КР 02.01.
4. План земляных масс кранового узла КУП-D7 см. EWE0426-MGL1-GLT-054-DRW-760104; КУП-D8 см. EWE0426-MGL1-GLT-054-DRW-770104.

Взам. инв. №

Подпись и дата

Инв.№ подл.

Рев.	Дата	Назначение ревизии	Проверил	Утвердил
A1	28.08.2026	Выпущено для строительства		
R1	24.07.2026	Выпущено для рассмотрения		

ЗАКАЗЧИК: UTG UZTRANSGAZ

ГЕНЕРАЛЬНЫЙ ПОДРЯДЧИК: UET UZBEKENERGOTAMIR

ПОДРЯДЧИК: PBG Pro Build Generation

ГЕНЕРАЛЬНЫЙ ПРОЕКТИРОВЩИК: EAST WEST ENGINEERING

EWE0426-MGL1-GLT-054-DRW-730104-A1

«СТРОИТЕЛЬСТВО НОВЫХ НИТОК (УЧАСТКОВ) ГАЗОПРОВОДОВ «ГАЗЛИ – САРИМОЙ» И «АКЧАЛОК – ГАЗЛИ – НУКУС» ОБЩЕЙ ПРОТЯЖЕННОСТЬЮ НЕ МЕНЕЕ 275 км».

Изм.	Кол.уч.	Лист	№ док.	Подпись	Дата
ГИП		Схабицкий А.			08.2026
Нач.отд.		Нигманова Н.			08.2026
Исполн.		Нигманова Н.			08.2026
Н.контр		Схабицкий А.			08.2026

ГАЗОПРОВОД «ГАЗЛИ-САРИМОЙ» (54 км)

Генеральный план и транспорт.

Стадия	Лист	Листов
РД	1	1

КУП-D4.
План земляных масс М 1:500

EAST WEST ENGINEERING
ООО "EAST-WEST Engineering"
г. Ташкент 2026 г.

Формат / Format A4x3