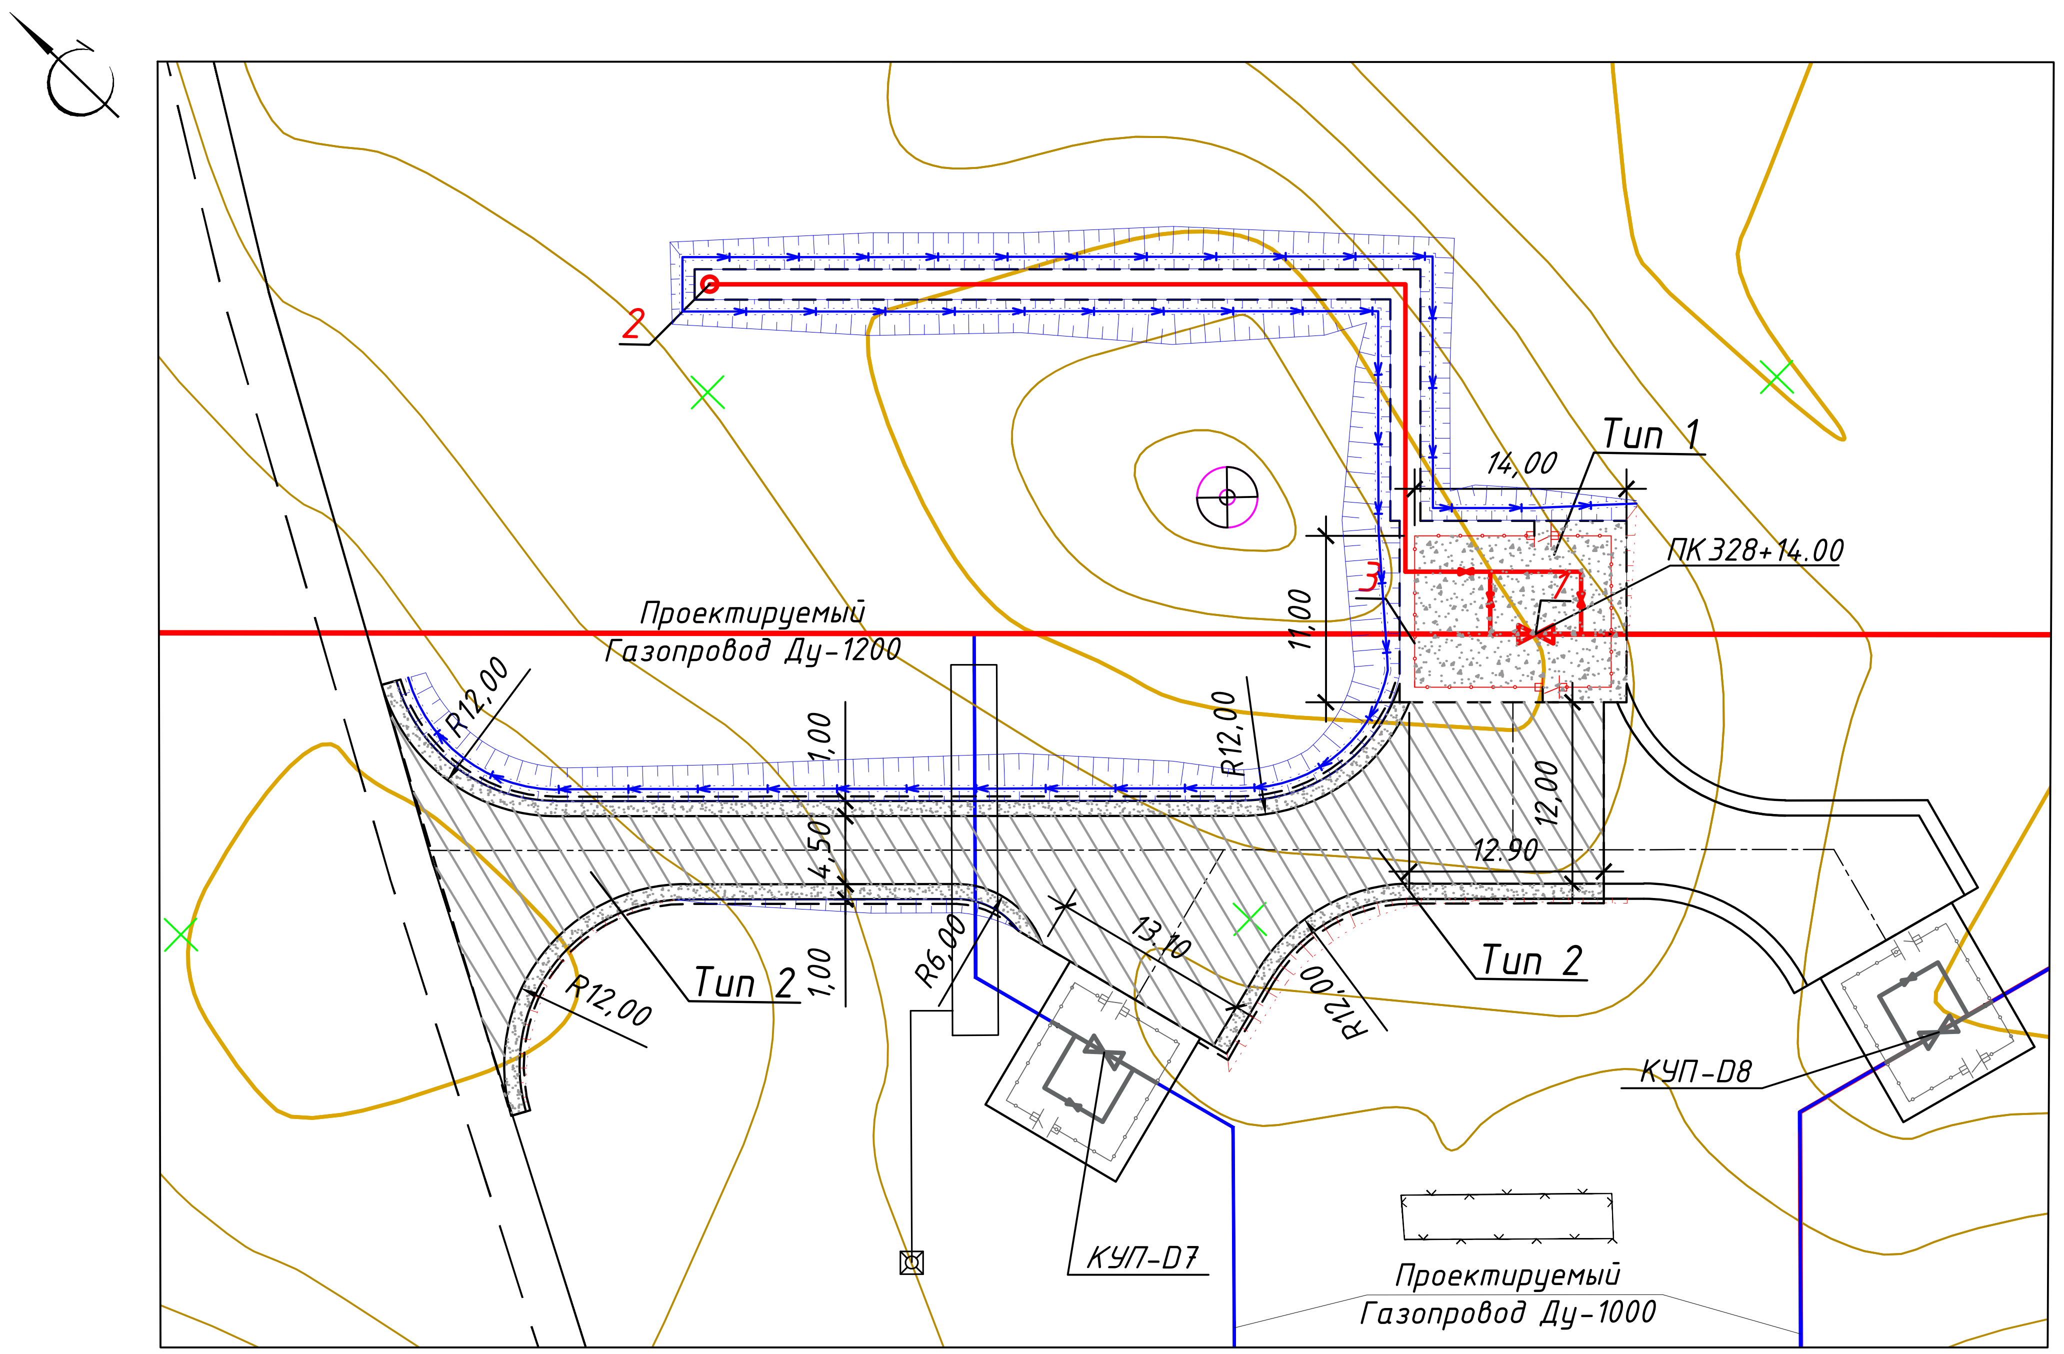

Тип 1

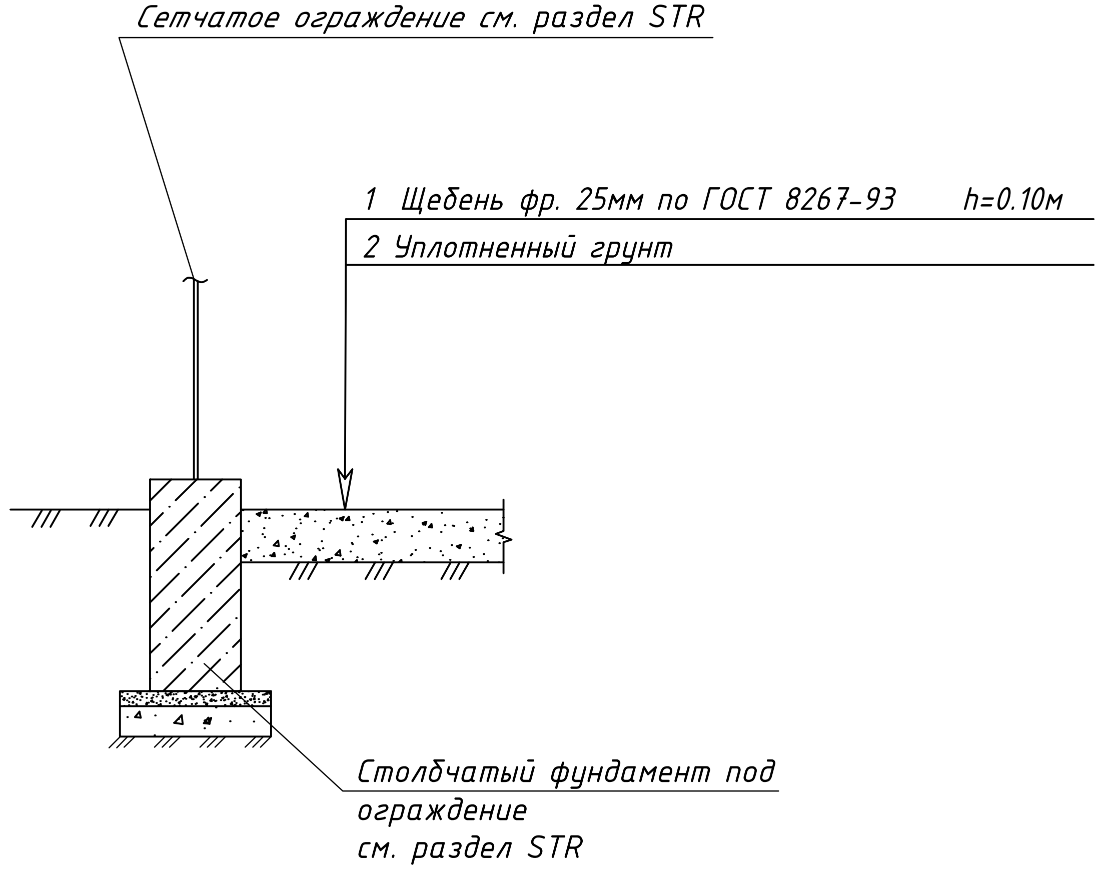
Сетчатое ограждение см. раздел STR
1 Щебень фр. 25мм по ГОСТ 8267-93 h=0.10м
2 Уплотненный грунт
Столбчатый фундамент под ограждение см. раздел STR

Экспликация зданий и сооружений

Номер на плане	Наименование	Примечание
1	Крановый узел Ду 1200	
2	Продувочная свеча	
3	Ограждение сетчатое	

Ведомость тротуаров, дорожек и площадок

Тип	Обозначение	Наименование	Ед. изм.	Примечание
		Покрытие площадки		
1	░	Покрытие из щебня по ГОСТ 8267-93, h=0.10	м²	155
		Покрытие проездов		
2	▨	Покрытие из щебеночно-песчаной смеси по ГОСТ 25607-2009 смесь С1 h=0,15м Основание из гравийно-песчаной смеси по ГОСТ 25607-2009 смесь С3 h=0,15м Укрепление обочин из ГПС ГОСТ 25607-2009 смесь С4 h=0,15м	м² м²	680.0 150.0

Тип 2

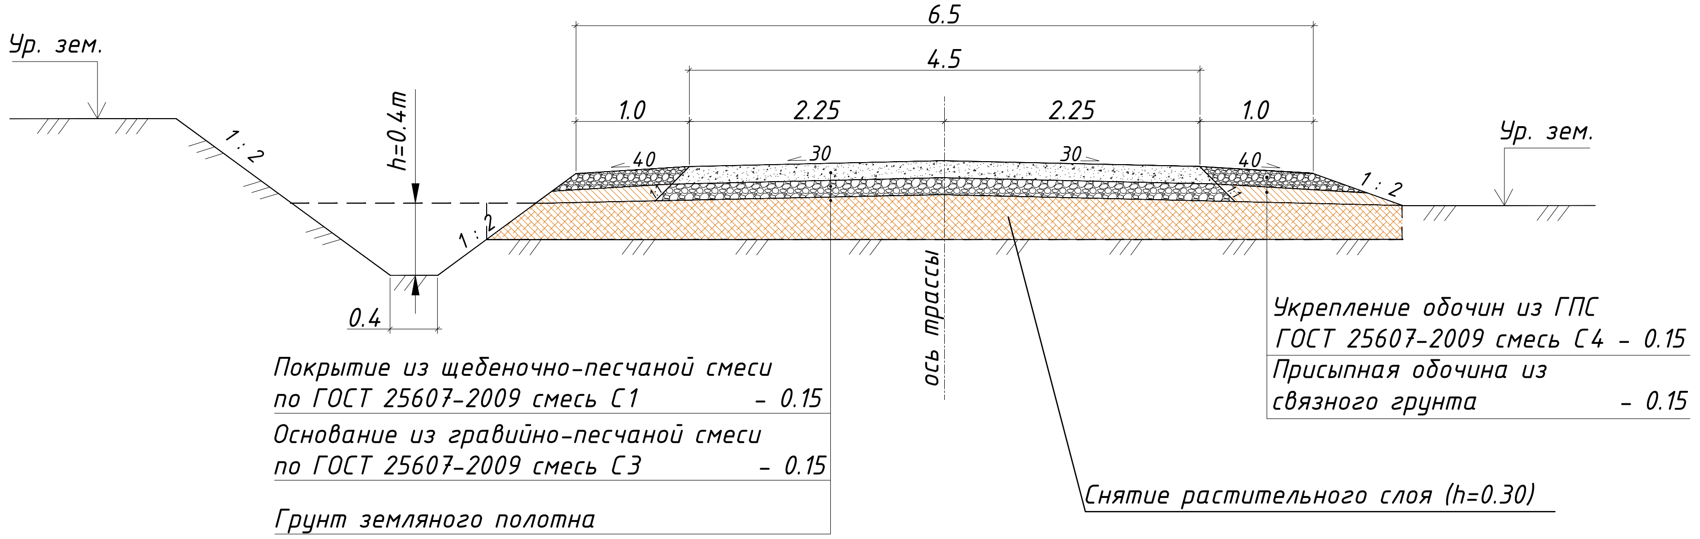

Покрытие из щебеночно-песчаной смеси по ГОСТ 25607-2009 смесь С1 – 0.15

Основание из гравийно-песчаной смеси по ГОСТ 25607-2009 смесь С3 – 0.15

Грунт земляного полотна

Укрепление обочин из ГПС ГОСТ 25607-2009 смесь С4 – 0.15

Присыпная обочина из связного грунта – 0.15

Снятие растительного слоя (h=0.30)

Примечания:

При составлении настоящего чертежа были использованы :

1. Материалы топографо-геодезической съемки, предоставлены АО "O'ZLITINEFTGAZ".
2. Система координат местная. Высотные отметки даны в Балтийской системе.
3. Размеры даны в метрах.
4. Площадка кранового узла КУП-D4 привязана линейно к пикету ПК 328+14.00.
5. Данный лист смотри совместно с листами разделов PIL, PRE, ELE, STR, SYS.
6. Детальный план кранового узла см. EWE0426-MGL1-PRE-054-DRW-730203.
7. План благоустройства территории кранового узла КУП-D7 см. EWE0426-MGL1-GLT-054-DRW-760106; кранового узла КУП-D8 см. EWE0426-MGL1-GLT-054-DRW-770106.
8. Защита Пересечения проектной дороги с проектной перемычкой 4 (КУП-D7) предусмотрена в техническом решении №1 в рамках авторского надзора.

Взам. инв. №

Подпись и дата

Инв.№ подл.

Рев.	Дата	Назначение ревизии	Проверил	Утвердил
A2	06.10.2026	Выпущено для строительства		
A1	28.08.2026	Выпущено для строительства		
R1	24.07.2026	Выпущено для рассмотрения		

ЗАКАЗЧИК: UTG UZTRANSGAZ

ГЕНЕРАЛЬНЫЙ ПОДРЯДЧИК: UET UZBEKENERGOTAMIR

ПОДРЯДЧИК: PBG Pro Build Generation

ГЕНЕРАЛЬНЫЙ ПРОЕКТИРОВЩИК: EAST WEST ENGINEERING

EWE0426-MGL1-GLT-054-DRW-730106-A2

«СТРОИТЕЛЬСТВО НОВЫХ НИТОК (УЧАСТКОВ) ГАЗОПРОВОДОВ «ГАЗЛИ – САРИМОЙ» И «АКЧАЛОК – ГАЗЛИ – НУКУС» ОБЩЕЙ ПРОТЯЖЕННОСТЬЮ НЕ МЕНЕЕ 275 км».

Изм.	Кол.уч.	Лист	№ док.	Подпись	Дата
ГИП		Кирпичников С.			10.2026
Нач.отд.		Нигманова Н.			10.2026
Исполн.		Нигманова Н.			10.2026
Н.контр		Кирпичников С.			10.2026

ГАЗОПРОВОД «ГАЗЛИ-САРИМОЙ» (54 км)

Генеральный план и транспорт.

Стадия	Лист	Листов
РД	1	1

КУП-D4.
План благоустройства территории
М 1:500

ООО "EAST-WEST Engineering"
г. Ташкент 2026 г.

Формат / Format A4x3