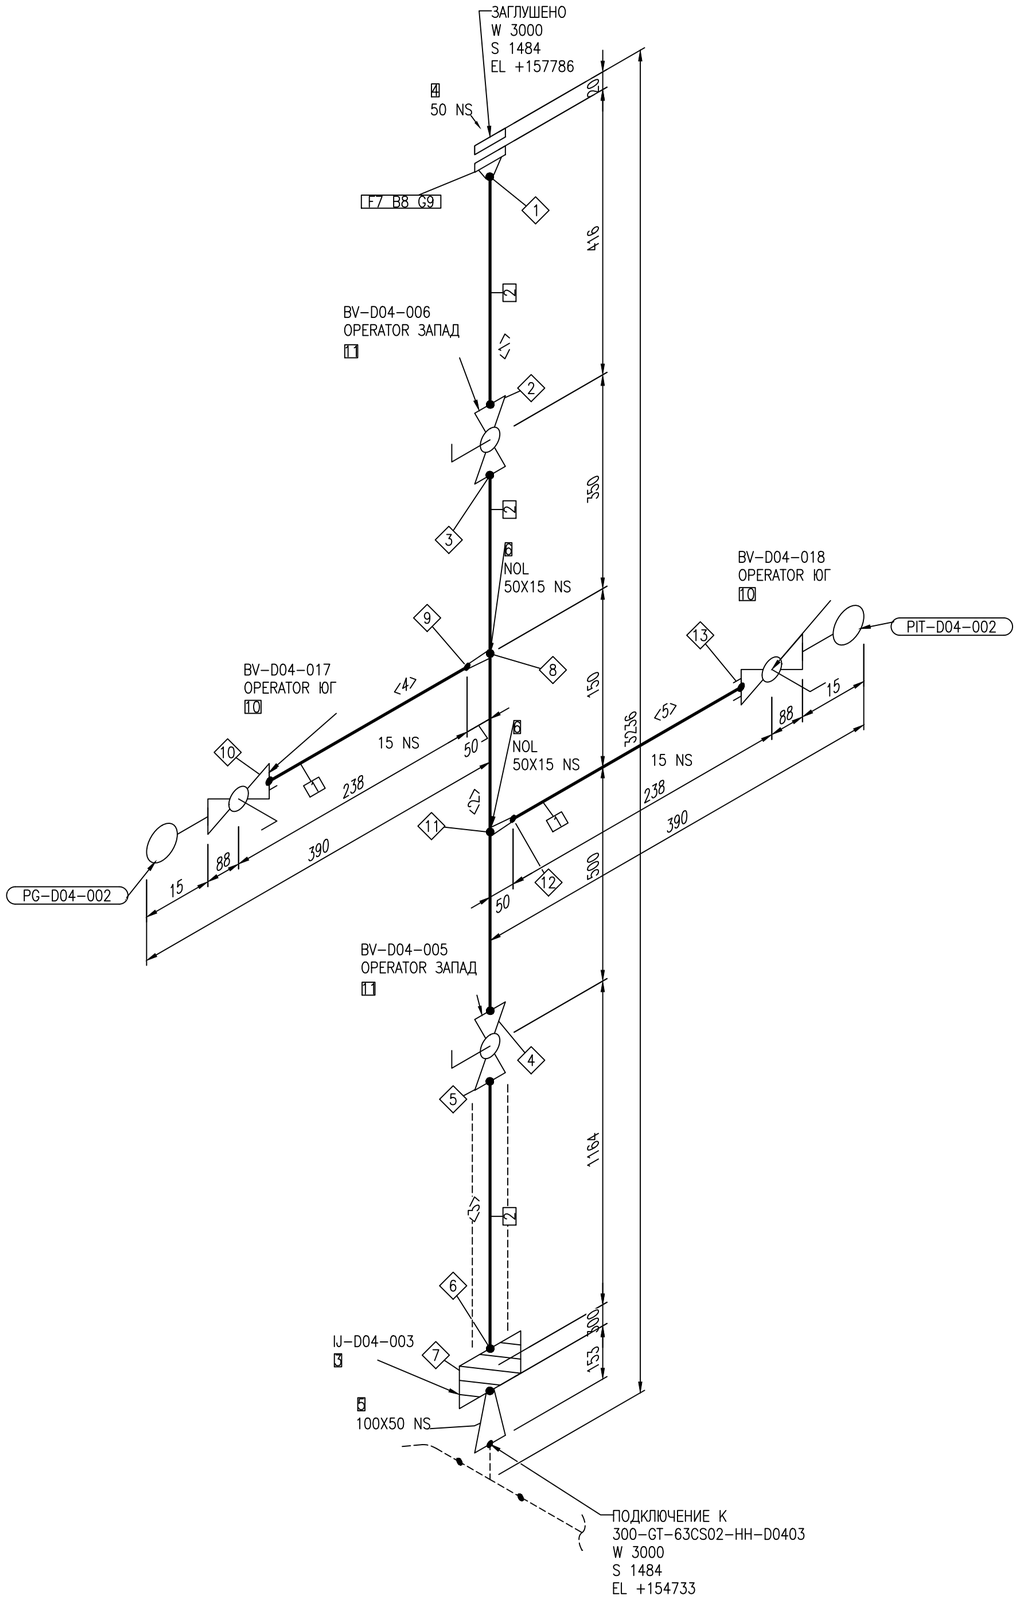


ПЕРЕЧЕНЬ СВАРНЫХ ШВОВ		
№	DN	ТИП
1	50	BUTTWELD
2	50	BUTTWELD
3	50	BUTTWELD
4	50	BUTTWELD
5	50	BUTTWELD
6	50	BUTTWELD
7	50	BUTTWELD
8	50	TAPWELD
9	15	WELD
10	15	SOCKETWELD
11	50	TAPWELD
12	15	WELD
13	15	SOCKETWELD

ПЕРЕЧЕНЬ ТРУБНЫХ КАТУШЕК		
№	DN	ДЛИНА
1	50	234ММ
2	50	770ММ
3	50	749ММ
4	15	150ММ
5	15	150ММ

СПЕЦИФИКАЦИЯ ИЗДЕЛИЙ И МАТЕРИАЛОВ

ПОЗ.	НАИМЕНОВАНИЕ	СТАНДАРТ	КОЛ.	ПРИМЕЧАНИЕ
1	Трубы стальные бесшовные холоднодеформированные Ст20, 22Х3	ГОСТ 8734-75/ ГОСТ 8733-74	0.3М	
2	Трубы стальные бесшовные горячедеформированные Ст20, 57Х4	ГОСТ 8732-78/ ГОСТ 8731-74	1.8М	
3	Изолирующее соединение приварное, 6.3 МПа, 57Х4	EWE0426-MGL1-PRE-054-DSH-610135	1	
4	Заглушка фланцевая стальная АТК 24.200.02-90, исполнение 4, 6.3 МПа, Ст20, DN50	АТК 24.200.02-90	1	
5	Переход ПШК I 114(5К48)Х57(4К42)-5,5(6,9)-0.75-30, сталь 09Г2С	ТУ 1469-017-38948552-2015	1	
6	Штуцер приварной ШУсТ-1-50-22Х3.0-6,3-20-2	ТУ 3600-010-88626180-2012	2	
7	Фланец стальной приварной встык, тип 11, исполнение J, ряд 1, 6.3 МПа, Ст20, 57Х4	ГОСТ 33259-2015	1	
8	Крепежный комплект 2-1-М20х110, шпильки Ст35, шайбы Ст20, гайки Ст25, для DN50	ОСТ 26-2040-96	4	
9	Прокладка овального сечения, линзовая стальная, тип 1, Сталь 08КП, 6.3 МПа, DN50	ГОСТ 34655-2020	1	
10	Кран шаровой DN15 PN-6,3 МПа с ручным приводом, приварной х резьбовой, 1/2" NPT F, надземный	EWE0426-MGL1-PRE-054-DSH-610122	2	
11	Кран шаровой DN50 PN-6,3 МПа с ручным приводом,приварной, надземный	EWE0426-MGL1-PRE-054-DSH-610122	2	

Трубопровод	ДАННЫЕ ПО ТРУБОПРОВОДУ		
50-GT-63CS02-HH-D0405	Расчетные параметры	Температура	-26,9...+85 °C
		Давление	6,3 MPa
	Рабочие параметры	Температура	-20...+40 °C
		Давление	5,5 MPa
Ссылочные чертежи No	Параметры испытания	Тип	Гидравлическое
EWE0426-MGL1-PRE-054-SCM-610106		Давление	6,9 MPa
	Изоляция	Тип	HH
		Толщина	mm
	Катодная защита	Да или Нет	Да

Рев.	Дата	Назначение ревизии	Проверил	Утвердил
A1	07.09.2026	Выпущено для рассмотрения		
R1	22.06.2026	Выпущено для рассмотрения		

ЗАКАЗЧИК: UTG UZBEKHYDROCARBON | ГЕНЕРАЛЬНЫЙ ПОДРЯДЧИК: UET UZBEKENERGOSTROY | ПОДРЯДЧИК: PBG Pre Build Generation | ГЕНЕРАЛЬНЫЙ ПРОЕКТИРОВЩИК: EAST WEST ENGINEERING

Изм.	Кол.уч.	Лист	№док.	Подпись	Дата
ГИП		Кирпичников С.			09.2026
Нач.отд.		Рябинин А.			09.2026
Исполн.		Таштимуров Р.			09.2026
Н.контр		Кирпичников С.			09.2026

EWE0426-MGL1-PRE-054-ISO-730606-A1

«СТРОИТЕЛЬСТВО НОВЫХ НИТОК (УЧАСТКОВ) ГАЗОПРОВОДОВ «ГАЗЛИ - САРИМОЙ» И «АКЧАЛОК - ГАЗЛИ - НУКУС» ОБЩЕЙ ПРОТЯЖЕННОСТЬЮ НЕ МЕНЕЕ 275 КМ».

ГАЗОПРОВОД «ГАЗЛИ-САРИМОЙ» (54 КМ)
Линейный крановый узел DN1200 КУП-D4

Стадия	Лист	Листов
РД	1	1

Изометрический чертеж трубопровода
50-GT-63CS02-HH-D0405

ООО "EAST-WEST Engineering"
г. Ташкент 2026г.

Взам. инв. №
Подпись и дата
Инв.№ подл.

Формат А2 594х420