
Линейный крановый узел КУП-D4.
План 1 (1:50)

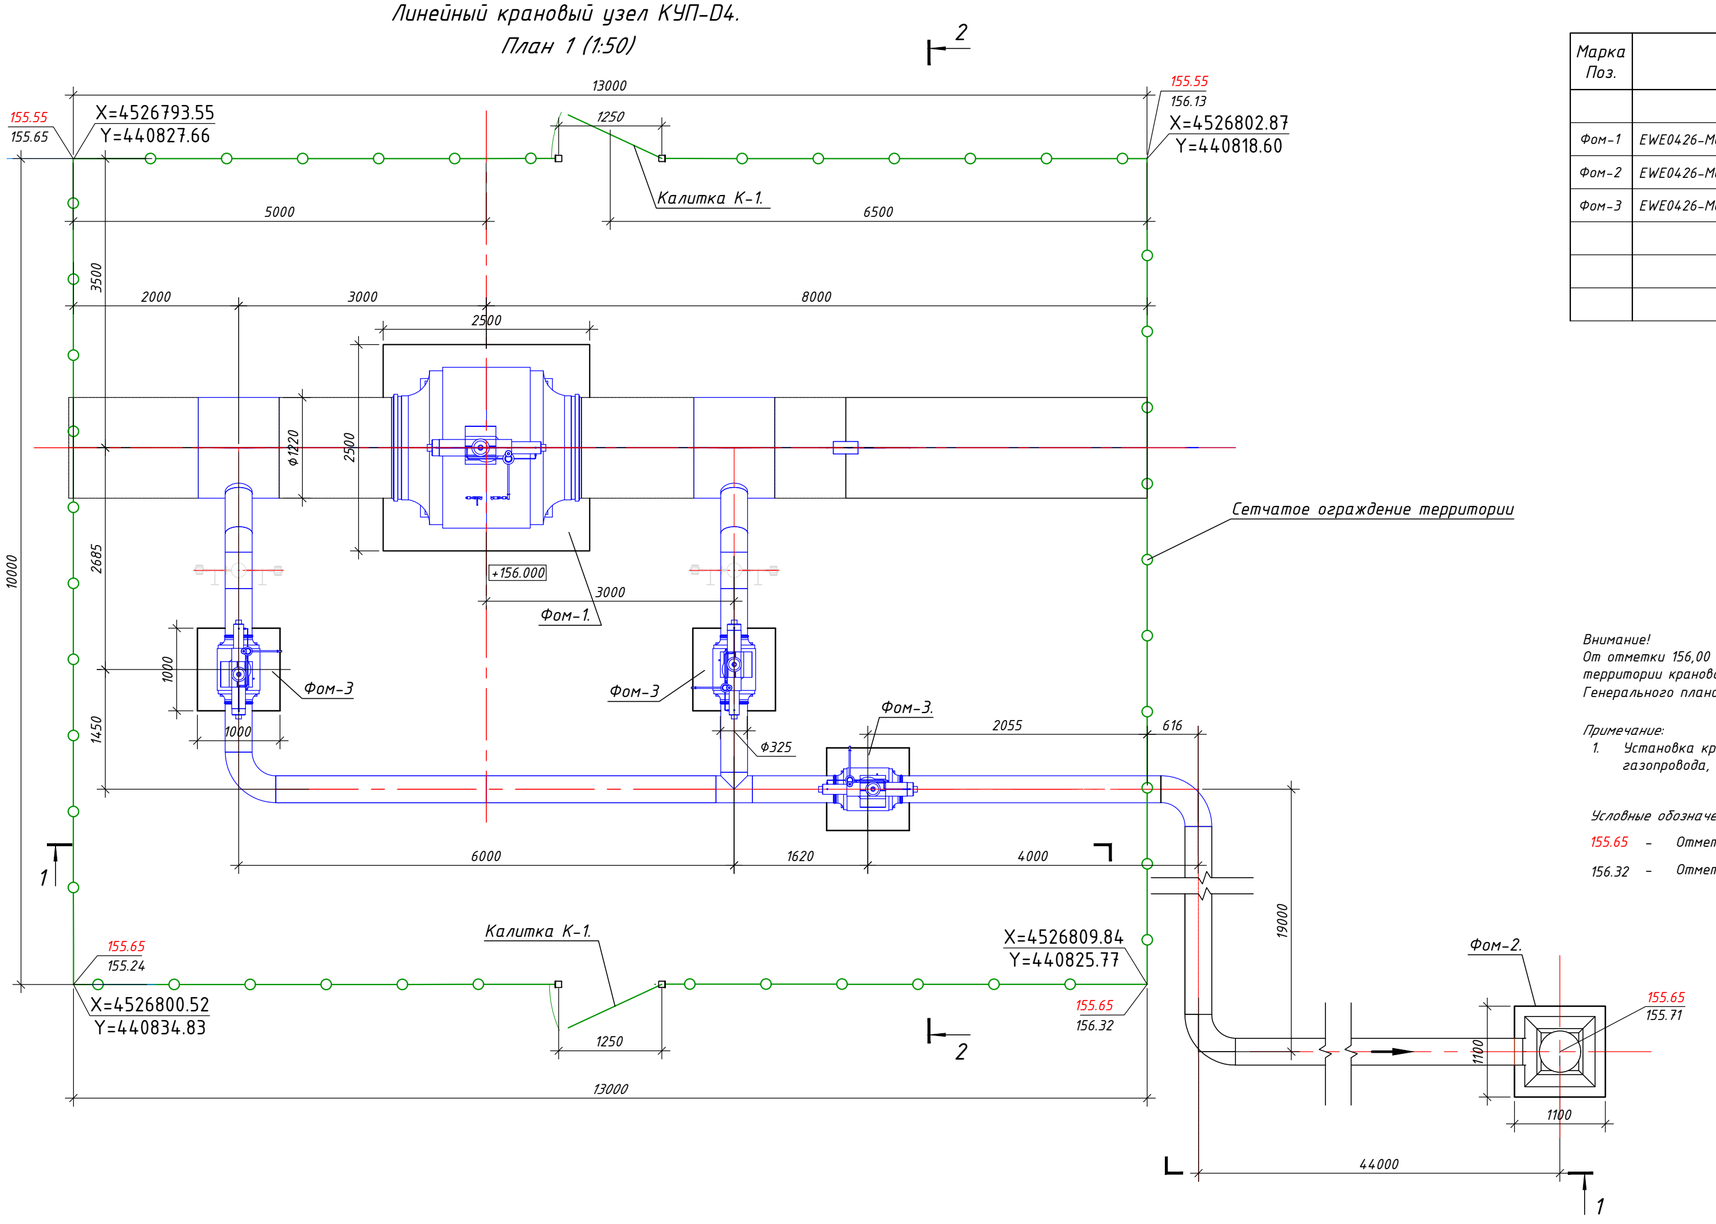

Спецификация элементов

Марка Поз.	Обозначение	Наименование	Кол. шт.	Масса ед.кг	Примеч.
		Линейный крановый узел КУП-D4.			
Фом-1	EWE0426-MGL1-STR-054-DRW-730504	Фундамент оборудования, монолитный Фом-1	1		
Фом-2	EWE0426-MGL1-STR-054-DRW-730505	Фундамент оборудования, монолитный Фом-2	1		
Фом-3	EWE0426-MGL1-STR-054-DRW-730506	Фундамент оборудования, монолитный Фом-3	3		

Внимание!
От отметки 156,00 предусмотреть срезку грунта до спланированных, планировочных отметок земли на территории кранового узла КУП-D4 - 155,55 и 155,65, данная срезка грунта учтена в части проекта Генерального плана (ГП).

Примечание:
1. Установка кранового узла КУП-D4 (Ду1200) расположена на ПК328+14 трассы проектного газопровода, продольный профиль газопровода ПК320 - ПК340.

Условные обозначения:

155.65 - Отметка спланированной поверхности земли

156.32 - Отметка существующей поверхности земли

A1	09.09.2026	Выпущено для строительства			
R1	27.07.2026	Выпущено для рассмотрения			
Рев	Дата	Назначение ревизии		Проверил	Утвердил

ЗАКАЗЧИК: | ГЕНЕРАЛЬНЫЙ ПОДРЯДЧИК: | ПОДРЯДЧИК: | ГЕНЕРАЛЬНЫЙ ПРОЕКТИРОВЩИК: EAST WEST ENGINEERING

Изм.	Кол.уч.	Лист	№ док.	Подпись	Дата
ГИП		Кирпичников С.			09.09.26
Нач.отд.		Каршиев А.			09.09.26
Исполн.		Хабиров Х.			09.09.26
Н.контр		Кирпичников С.			09.09.26

EWE0426-MGL1-STR-054-DRW-730502-A1

«СТРОИТЕЛЬСТВО НОВЫХ НИТОК (УЧАСТКОВ) ГАЗОПРОВОДОВ «ГАЗЛИ - САРИМОЙ» И «АКЧАЛОК - ГАЗЛИ - НУКУС» ОБЩЕЙ ПРОТЯЖЕННОСТЬЮ НЕ МЕНЕЕ 275 КМ».

ГАЗОПРОВОД "ГАЗЛИ-САРИМОЙ" (54 КМ)
Линейный крановый узел DN1200 КУП-D4

Стадия	Лист	Листов
РП	1	1

Схема расположения кранового узла КУП-D4.

EAST WEST ENGINEERING
ООО "EAST-WEST Engineering"
г. Ташкент 2026г.

Взам. инв. №
Подпись и дата
Инв.№ подл.

Формат / Format A2