

Разрез 1-1 м 1:25

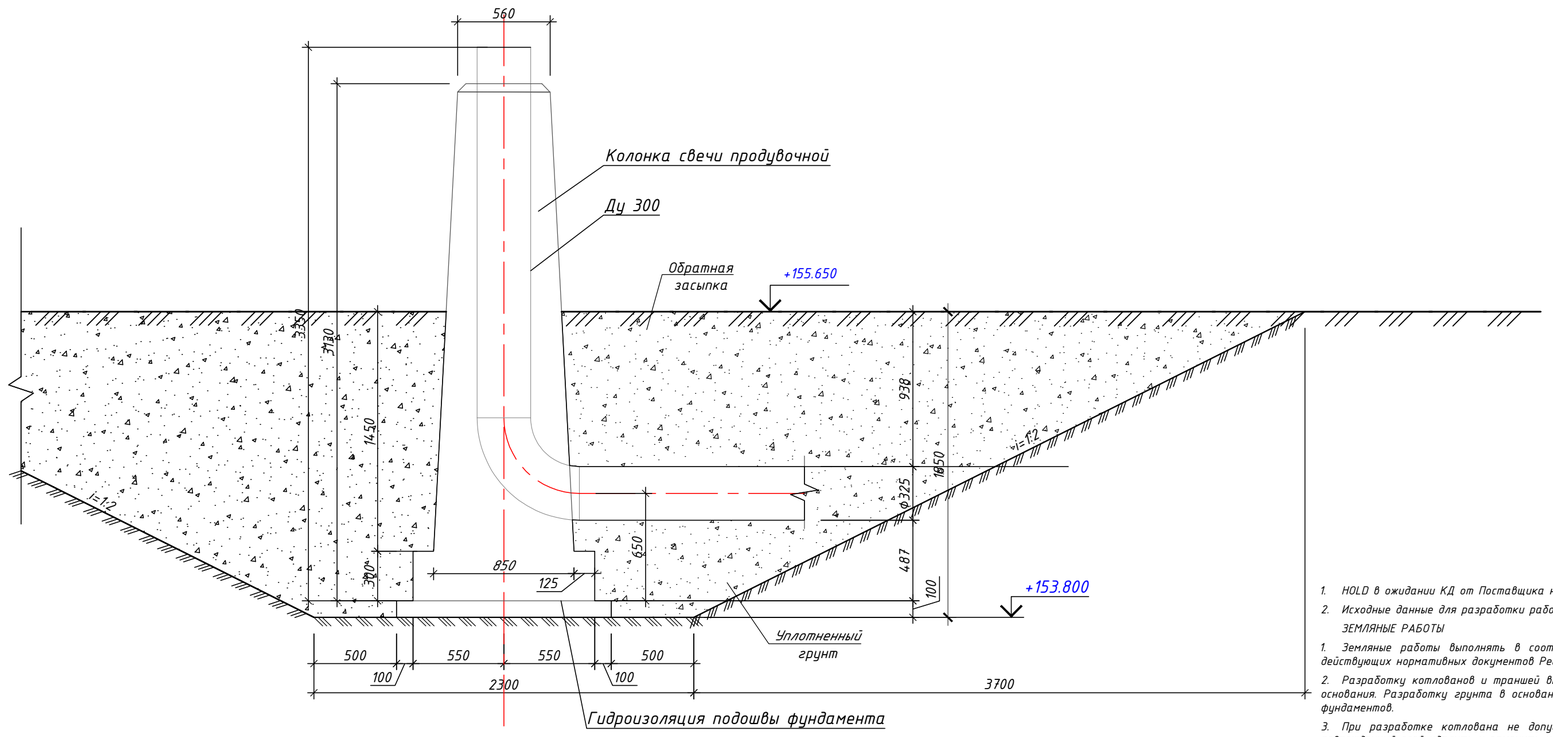

План котлована м 1:100.

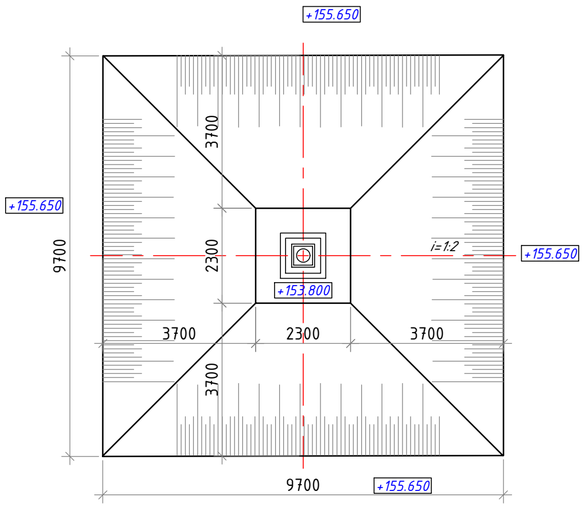

План м 1:25.

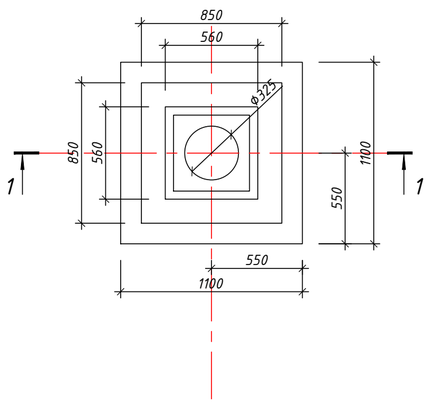


Таблица объемов земляных работ

Поз.	Наименование	Ед. изм.	Кол-во	Примечание
1	Выемка грунта	$м^3$ m^3	91,93	
2	Обратная засыпка	$м^3$ m^3	90,33	
3	Лишний грунт выемки для планировки по территории площадки строительства	$м^3$ m^3	1,60	

Спецификация элементов

Марка Поз.	Обозначение	Наименование	Кол. шт.	Масса ед.кг	Примеч.
		Линейный крановый узел КУП-03.			
Фом-2	по Серии 7.402-3 Выпуск III	Фундамент оборудования, монолитный Фом-2	1		
		Сборочные единицы и детали:			
		Стержни одиночные		29,10	
		Хомут из арматурной стали		15,20	
		Изделие закладное - рым из круга L=470мм		1,80	
		Заготовка для колонки свечи		311,20	
		Материалы:			
		Бетон подготовки кл. В7.5 (М100)			0.17м^3
		Бетон кл. В 15 (М200)			2,20м^3
		Гидроизоляция фундамента на площади:			8.00м^2
		Детали:			
	ГОСТ 34028-2016	Арматура Ф10 А-240		14,40	
	ГОСТ 34028-2016	Арматура Ф10 А-500		29,10	

Общие указания

1. HOLD в ожидании КД от Поставщика на приводные краны.
2. Исходные данные для разработки рабочих чертежей комплекта КЖ:

ЗЕМЛЯНЫЕ РАБОТЫ

1. Земляные работы выполнять в соответствии с требованиями КР 02.01 «Земляные сооружения, основания и фундаменты», проектной документацией и требованиями действующих нормативных документов Республики Узбекистан.
2. Разработку котлованов и траншей выполнять с соблюдением проектных отметок, размеров и уклонов откосов. Не допускается нарушение естественной структуры грунта основания. Разработку грунта в основании фундаментов, при необходимости, выполнять с недобором с последующей зачисткой основания непосредственно перед устройством фундаментов.
3. При разработке котлована не допускать переувлажнения, разрыхления и промерзания грунта основания. При нарушении естественной структуры грунта основания поврежденный слой удалить и заменить уплотненным грунтом либо выполнить предусмотренные проектом мероприятия по подготовке основания.
4. Грунт, используемый для обратной засыпки пазух фундаментов, должен быть однородным, пригодным для уплотнения, без органических и растительных включений, строительного мусора, мерзлых комков и других включений, снижающих качество уплотнения.
5. Для обратной засыпки применять местный грунт, пригодность которого подтверждена результатами лабораторных исследований. При невозможности обеспечения требуемого уплотнения местным грунтом предусмотреть замену его на подходящий минеральный грунт.
6. Обратную засыпку выполнять после достижения бетоном конструкций требуемой прочности и завершения работ по гидроизоляции и антикоррозионной защите конструкций, предусмотренных проектом.
7. Обратную засыпку выполнять послойно. Толщина уплотняемого слоя в рыхлом состоянии принимать не более 200–300 мм в зависимости от применяемых механизмов и средств уплотнения. Каждый последующий слой отсыпать только после достижения требуемой степени уплотнения предыдущего слоя.
8. При обратной засыпке в проекте плотность сухого грунта γ = 1,65 т/м^3 считать контрольным показателем только при наличии лабораторного обоснования. Максимальную стандартную плотность сухого грунта и соответствующую ей оптимальную влажность определить лабораторными испытаниями. Проектную плотность сухого грунта при коэффициенте уплотнения Ку ≥ 0,95 определять по результатам указанных испытаний.
9. Уплотнение грунта выполнять механизированным способом соответствующими типу грунта катками, виброплитами, трамбовками или другими механизмами. Количество проходов уплотняющей техники и оптимальную влажность грунта устанавливать с учетом вида грунта и результатов пробного уплотнения.
10. Контроль качества уплотнения обратной засыпки осуществлять в процессе производства работ путем определения фактической плотности сухого грунта и коэффициента уплотнения с оформлением результатов операционного контроля.
11. Контрольные испытания выполнять в местах и с периодичностью, установленных проектом производства работ, строительными нормами и требованиями КР 02.01 «Земляные сооружения, основания и фундаменты».
12. При получении коэффициента уплотнения ниже установленного значения соответствующий участок подлежит дополнительному уплотнению. Засыпку последующих слоев до устранения выявленного несоответствия не производить.
13. Работы по обратной засыпке и уплотнению грунта выполнять с обеспечением сохранности гидроизоляции, антикоррозионного покрытия и конструкций фундаментов.

Примечания:

1. Фундамент Фом-2 предусмотрен для установки свечи. Выполнить по Серии 7.402-3 Выпуск III КЖ03.
2. Масса колонки свечи - 5280кг.

Безопасность на бровке: Не допускается размещение строительной техники, отвалов грунта и материалов в пределах призмы обрушения откосов котлована.

Гидроизоляция фундамента из двух слоев полимерного покрытия на основе лака ХП-734 по ГОСТ 52165-2003 толщиной 25 мкм.

Рев	Дата	Назначение ревизии	Проверил	Утвердил
A1	09.09.2026	Выпущено для строительства		
R1	27.07.2026	Выпущено для рассмотрения		

ЗАКАЗЧИК: UTG UZTRANSGAZ

ГЕНЕРАЛЬНЫЙ ПОДРЯДЧИК: UET

ПОДРЯДЧИК: PBG

ГЕНЕРАЛЬНЫЙ ПРОЕКТИРОВЩИК: EAST WEST ENGINEERING

Изм.	Кол.уч.	Лист	№ док.	Подпись	Дата
ГИП		Кирпичников С.			09.09.26
Нач.отд.		Каршиев А.			09.09.26
Исполн.		Хабиров Х.			09.09.26
Н.контр		Кирпичников С.			09.09.26

EWE0426-MGL1-STR-054-DRW-730505-A1

«СТРОИТЕЛЬСТВО НОВЫХ НИТОК (УЧАСТКОВ) ГАЗОПРОВОДОВ «ГАЗЛИ - САРИМОЙ» И «АКЧАЛОК - ГАЗЛИ - НУКУС» ОБЩЕЙ ПРОТЯЖЕННОСТЬЮ НЕ МЕНЕЕ 275 КМ».

ГАЗОПРОВОД "ГАЗЛИ-САРИМОЙ" (54 КМ)
Линейный крановый узел DN1200 КУП-D4

Стадия	Лист	Листов
РП	1	1

Фундамент Фом-2.

ООО "EAST-WEST Engineering"
г. Ташкент 2026г.

Взам. инв. №

Подпись и дата

Инв.№ подл.

Формат / Format A2