
Линейный крановый узел КУП-D4.


Схема расположения сетчатого ограждения (1:50).

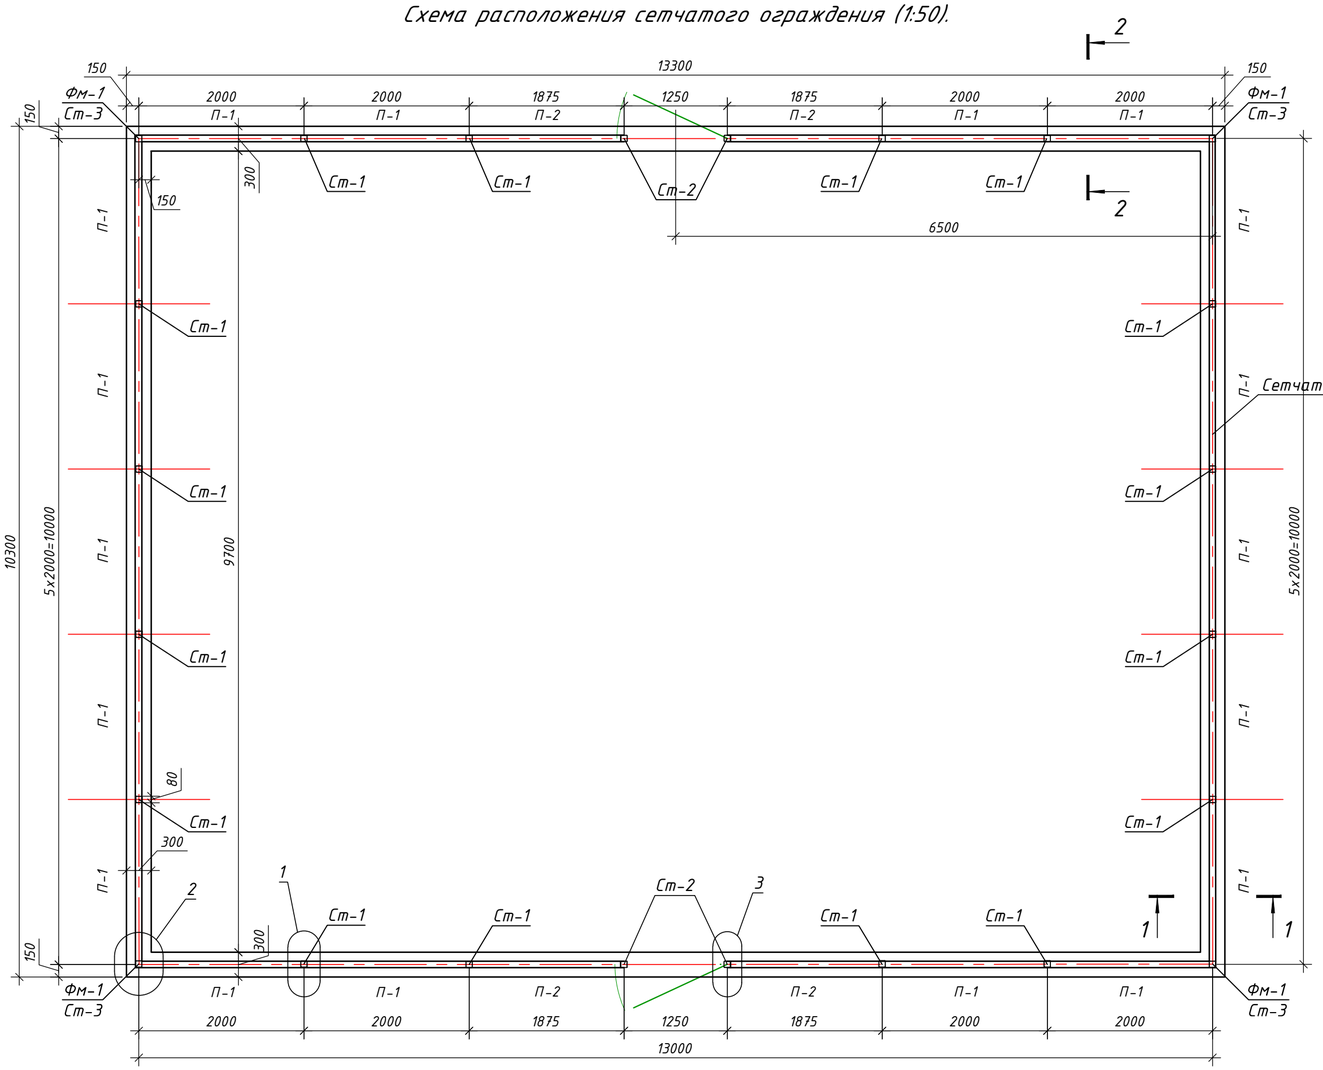


Спецификация элементов

Марка Поз.	Обозначение	Наименование	Кол. шт.	Масса ед.кг	Примеч.
		Линейный крановый узел КУП-D4.			
Фм-1	EWE0426-MGL1-STR-054-DRW-730509	Фундамент ленточный, монолитный Фм-1	1		
Ст-1	EWE0426-MGL1-STR-054-DRW-730510	Стойка ограждения Ст-1	16		
Ст-2	EWE0426-MGL1-STR-054-DRW-730511	Стойка ограждения Ст-2	4		
Ст-3	EWE0426-MGL1-STR-054-DRW-730512	Стойка ограждения Ст-3	4		
П-1	EWE0426-MGL1-STR-054-DRW-730513	Панель ограждения П-1	18		
П-2	EWE0426-MGL1-STR-054-DRW-730514	Панель ограждения П-2	4		
К-1	EWE0426-MGL1-STR-054-DRW-730515	Калитка К-1	2		
КД1	EWE0426-MGL1-STR-054-DRW-730516	Крепежная деталь КД1	24		
КД2	EWE0426-MGL1-STR-054-DRW-730516	Крепежная деталь КД2	32		


Узел 1

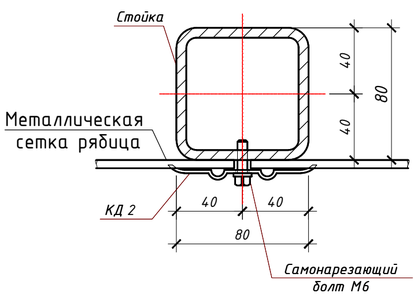

Узел 2

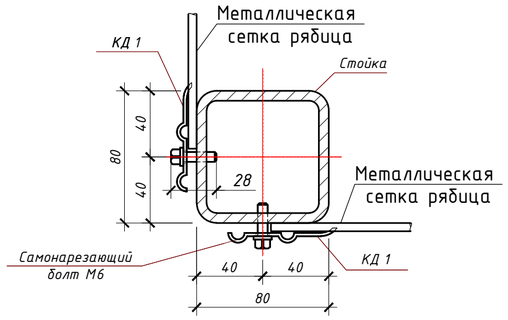

Узел 3

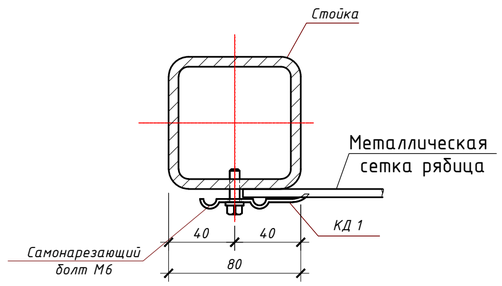

Примечания:

1. Данный чертёж читать совместно с ленточным фундаментом Фм-1.
2. Изготовить общее количество узлов:
   - узел 1 - 16шт.
   - узел 2 - 4шт.
   - узел 3 - 4шт.

Рев	Дата	Назначение ревизии	Проверил	Утвердил
A1	09.09.2026	Выпущено для строительства		
R1	27.07.2026	Выпущено для рассмотрения		

ЗАКАЗЧИК: UTG

ГЕНЕРАЛЬНЫЙ ПОДРЯДЧИК: UET

ПОДРЯДЧИК: PBG

ГЕНЕРАЛЬНЫЙ ПРОЕКТИРОВЩИК: EAST WEST ENGINEERING

Изм.	Кол.уч.	Лист	№ док.	Подпись	Дата	
ГИП		Кирпичников С.			09.09.26	EWE0426-MGL1-STR-054-DRW-730507-A1
Нач.отд.		Каршиев А.			09.09.26	«СТРОИТЕЛЬСТВО НОВЫХ НИТОК (УЧАСТКОВ) ГАЗОПРОВОДОВ «ГАЗЛИ - САРИМОЙ» И «АКЧАЛОК - ГАЗЛИ - НУКУС» ОБЩЕЙ ПРОТЯЖЕННОСТЬЮ НЕ МЕНЕЕ 275 КМ».
Исполн.		Хабиров Х.			09.09.26	ГАЗОПРОВОД "ГАЗЛИ-САРИМОЙ" (54 КМ) Линейный крановый узел DN1200 КУП-D4
Н.контр		Кирпичников С.			09.09.26	Схема расположения сетчатого ограждения.

Стадия	Лист	Листов
РП	1	1

EAST WEST ENGINEERING

ООО "EAST-WEST Engineering"
г. Ташкент 2026г.

Взам. инв. №

Подпись и дата

Инв.№ подл.

Формат / Format A2