


Стойка ограждения Ст-1

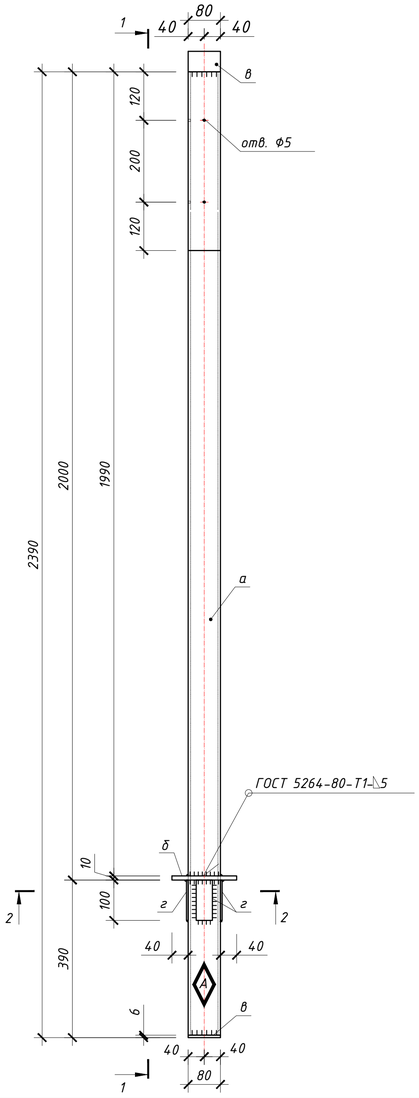


1-1 м 1:10.

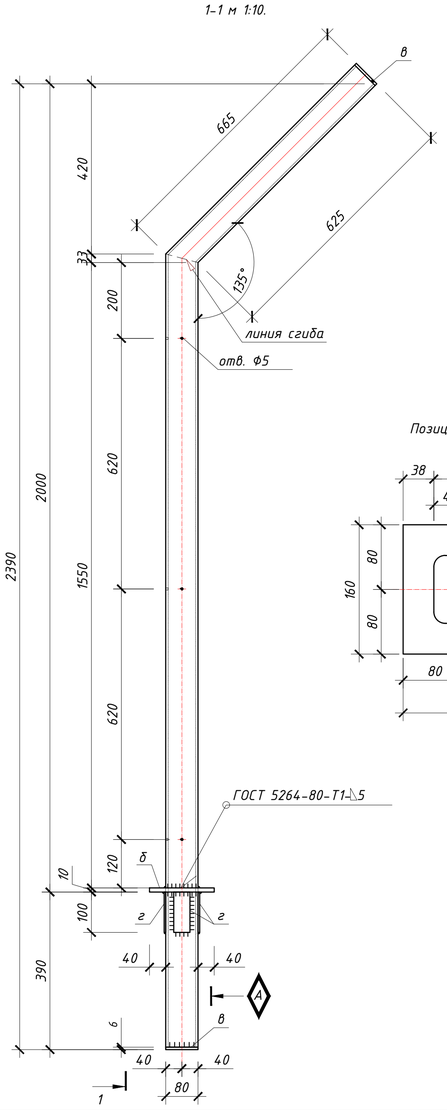

2-2

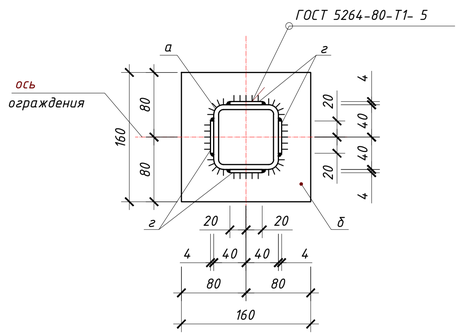

Позиция "б".

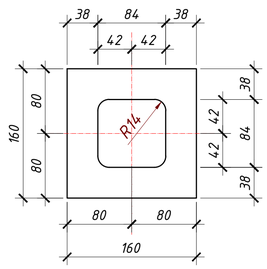


Спецификация элементов на одну марку

Марка поз.	Обозначение	Наименование	Кол. шт.	Масса ед.кг	Примечание
Ст-1	ГОСТ 30245-2003	Стойка ограждения Ст-1		27,6	вес на 1 стойку
а	ГОСТ 30245-2003	Профиль 80х80х4 ГОСТ 30245-2003 / С255 ГОСТ 27772-2015 L=2631мм	1	24,55	24,55
б	ГОСТ 19903-90*	Лист t=10 ГОСТ 19903-90 / С245 Гост 27772-2015 160х160мм	1	2,01	2,01
в	ГОСТ 19903-90*	Лист t=4 ГОСТ 19903-90 / С245 Гост 27772-2015 80х80мм	2	0,20	0,4
г	ГОСТ 19903-90*	Лист t=4 ГОСТ 19903-90 / С245 Гост 27772-2015 40х124мм	4	0,16	0,64
		Материалы:			
		Окраска металлоконструкций масляной краской за 2 раза			0.95м²

А – Знак ориентации. Нанести несмываемой краской!

Деталь срезки стойки Ст-1. (поз. а)

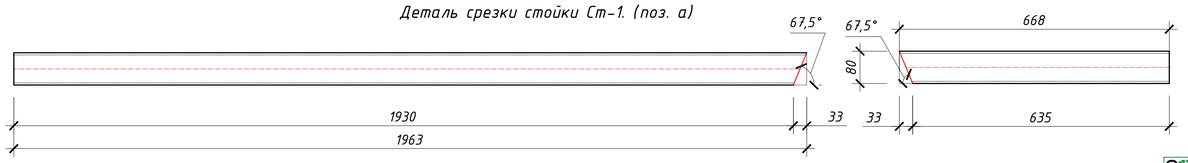

Примечания:
1. Сварку вести электродами Э42А ГОСТ 9467-75.
2. Конструкция должна быть покрыта масляной краской за 2 раза по грунтовке.
3. Элемент "г" следует приварить к "а" в первую очередь.
4. Крепления стойки смотри чертёж Фундамента Фм-1.

● Отверстие для болта
◊ Болт постоянный, нормальной точности
♦ Болт временный, нормальной точности
Сварной шов заводской
Сварной шов монтажный

Рев	Дата	Назначение ревизии	Проверил	Утвердил
A1	09.09.2026	Выпущено для строительства		
R1	27.07.2026	Выпущено для рассмотрения		

ЗАКАЗЧИК: UTG UZTRANSGAZ | ГЕНЕРАЛЬНЫЙ ПОДРЯДЧИК: UET UZBEKNEFTEGAZ | ПОДРЯДЧИК: PBG Pro Build Generation | ГЕНЕРАЛЬНЫЙ ПРОЕКТИРОВЩИК: EAST WEST ENGINEERING

EWE0426-MGL1-STR-054-DRW-730510-A1

«СТРОИТЕЛЬСТВО НОВЫХ НИТОК (УЧАСТКОВ) ГАЗОПРОВОДОВ «ГАЗЛИ - САРИМОЙ» И «АКЧАЛОК - ГАЗЛИ - НУКУС» ОБЩЕЙ ПРОТЯЖЕННОСТЬЮ НЕ МЕНЕЕ 275 КМ».

Изм.	Кол.уч.	Лист	№ док.	Подпись	Дата			
ГИП		Кирпичников С.			09.09.26	ГАЗОПРОВОД "ГАЗЛИ-САРИМОЙ" (54 КМ) / Линейный крановый узел DN1200 КУП-D4	Стадия	Лист	Листов
Нач.отд.		Каршиев А.			09.09.26		РП	1	1
Исполн.		Хабиров Х.			09.09.26				
Н.контр		Кирпичников С.			09.09.26	Стойка ограждения Ст-1.	EAST WEST ENGINEERING	ООО "EAST-WEST Engineering" г. Ташкент 2026г.	

Взам. инв. №
Подпись и дата
Инв.№ подл.

Формат / Format A4X3