




Стойка ограждения Ст-3

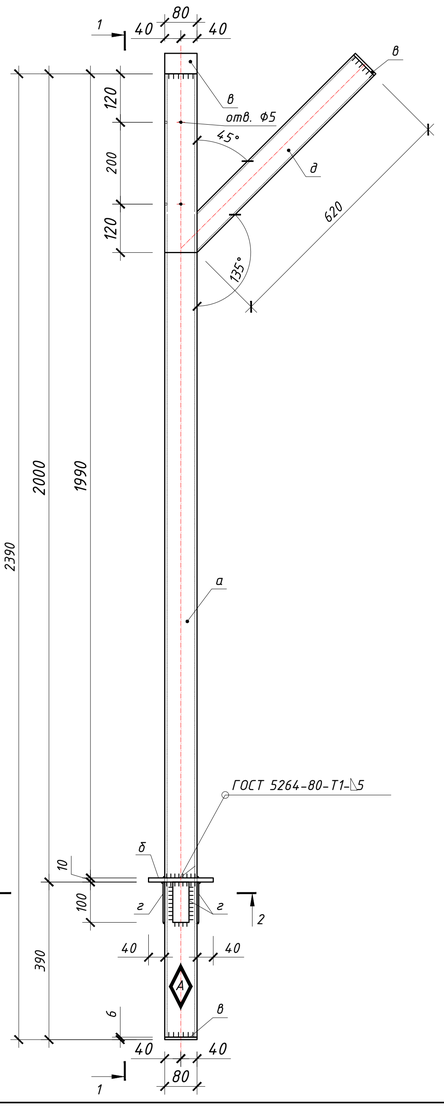

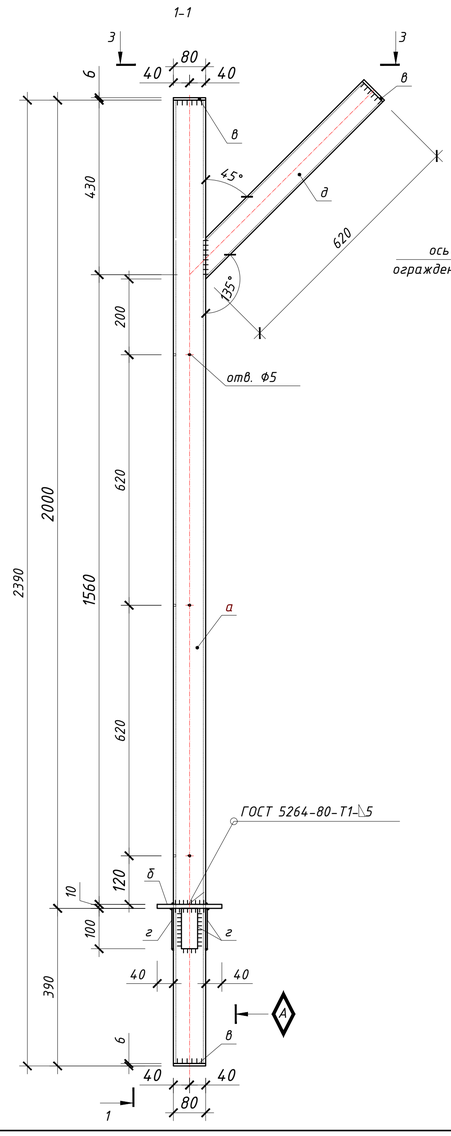


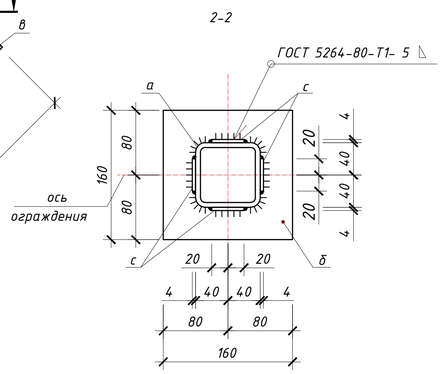

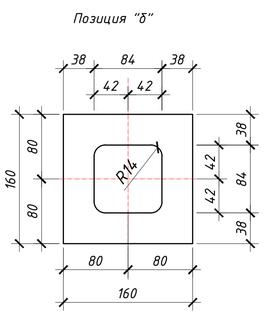

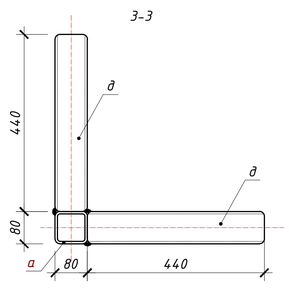

Деталь срезки стойки Ст-1. (поз. а)

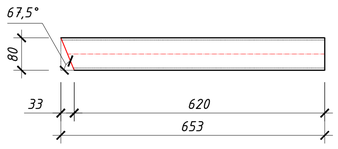

Спецификация элементов на одну марку

Марка поз.	Обозначение	Наименование	Кол. шт.	Масса ед.кг	Примечание
Ст-3	ГОСТ 30245-2003	Стойка ограждения Ст-3		27,6	вес на 1 стойку
а	ГОСТ 30245-2003	Профиль 80х80х4 ГОСТ 30245-2003 С255 ГОСТ 27772-2015 L=2390мм	1	24,55	24,55
б	ГОСТ 19903-90*	Лист t=10 ГОСТ 19903-90 С245 Гост 27772-2015 160х160мм	1	2,01	2,01
в	ГОСТ 19903-90*	Лист t=4 ГОСТ 19903-90 С245 Гост 27772-2015 80х80мм	2	0,20	0,4
г	ГОСТ 19903-90*	Лист t=4 ГОСТ 19903-90 С245 Гост 27772-2015 40х124мм	4	0,16	0,64
д	ГОСТ 30245-2003	Профиль 80х80х4 ГОСТ 30245-2003 С255 ГОСТ 27772-2015 L=620мм	1	5,72	5,72
		Материалы:			
		Окраска металлоконструкций масляной краской за 2 раза			1,14м²

Примечания:

1. Сварку вести электродами Э42А ГОСТ 9467-75.
2. Конструкция должна быть покрыта масляной краской за 2 раза по грунтовке.
3. Элемент "г" следует приварить к "а" в первую очередь.
4. Деталь-1 - деталь срезки стойки Ст-1. (поз. в)
5. Крепления стойки смотри лист Фундамента Фм-1.

А - Знак ориентации. Нанести несмываемой краской!

- Отверстие для болта
- Болт постоянный, нормальной точности
- Болт временный, нормальной точности
- Сварной шов заводской
- Сварной шов монтажный

Рев	Дата	Назначение ревизии	Проверил	Утвердил
А1	09.09.2026	Выпущено для строительства		
R1	27.07.2026	Выпущено для рассмотрения		

ЗАКАЗЧИК: UTG UZTRANSGAZ

ГЕНЕРАЛЬНЫЙ ПОДРЯДЧИК: UET

ПОДРЯДЧИК: PBG Pro Build Generation

ГЕНЕРАЛЬНЫЙ ПРОЕКТИРОВЩИК: EAST WEST ENGINEERING

EWE0426-MGL1-STR-054-DRW-730512-A1

«СТРОИТЕЛЬСТВО НОВЫХ НИТОК (УЧАСТКОВ) ГАЗОПРОВОДОВ «ГАЗЛИ - САРИМОЙ» И «АКЧАЛОК - ГАЗЛИ - НУКУС» ОБЩЕЙ ПРОТЯЖЕННОСТЬЮ НЕ МЕНЕЕ 275 КМ».

Изм.	Кол.уч.	Лист	№ док.	Подпись	Дата
ГИП		Кирпичников С.			09.09.26
Нач.отд.		Каршиев А.			09.09.26
Исполн.		Хабиров Х.			09.09.26
Н.контр		Кирпичников С.			09.09.26

ГАЗОПРОВОД "ГАЗЛИ-САРИМОЙ" (54 КМ) Линейный крановый узел DN1200 КУП-04

Стадия	Лист	Листов
РП	1	1

Стойка ограждения Ст-3.

ООО "EAST-WEST Engineering" г. Ташкент 2026г.

Взам. инв. №

Подпись и дата

Инв.№ подл.

Формат / Format A4X3