

План 1 (1:50)

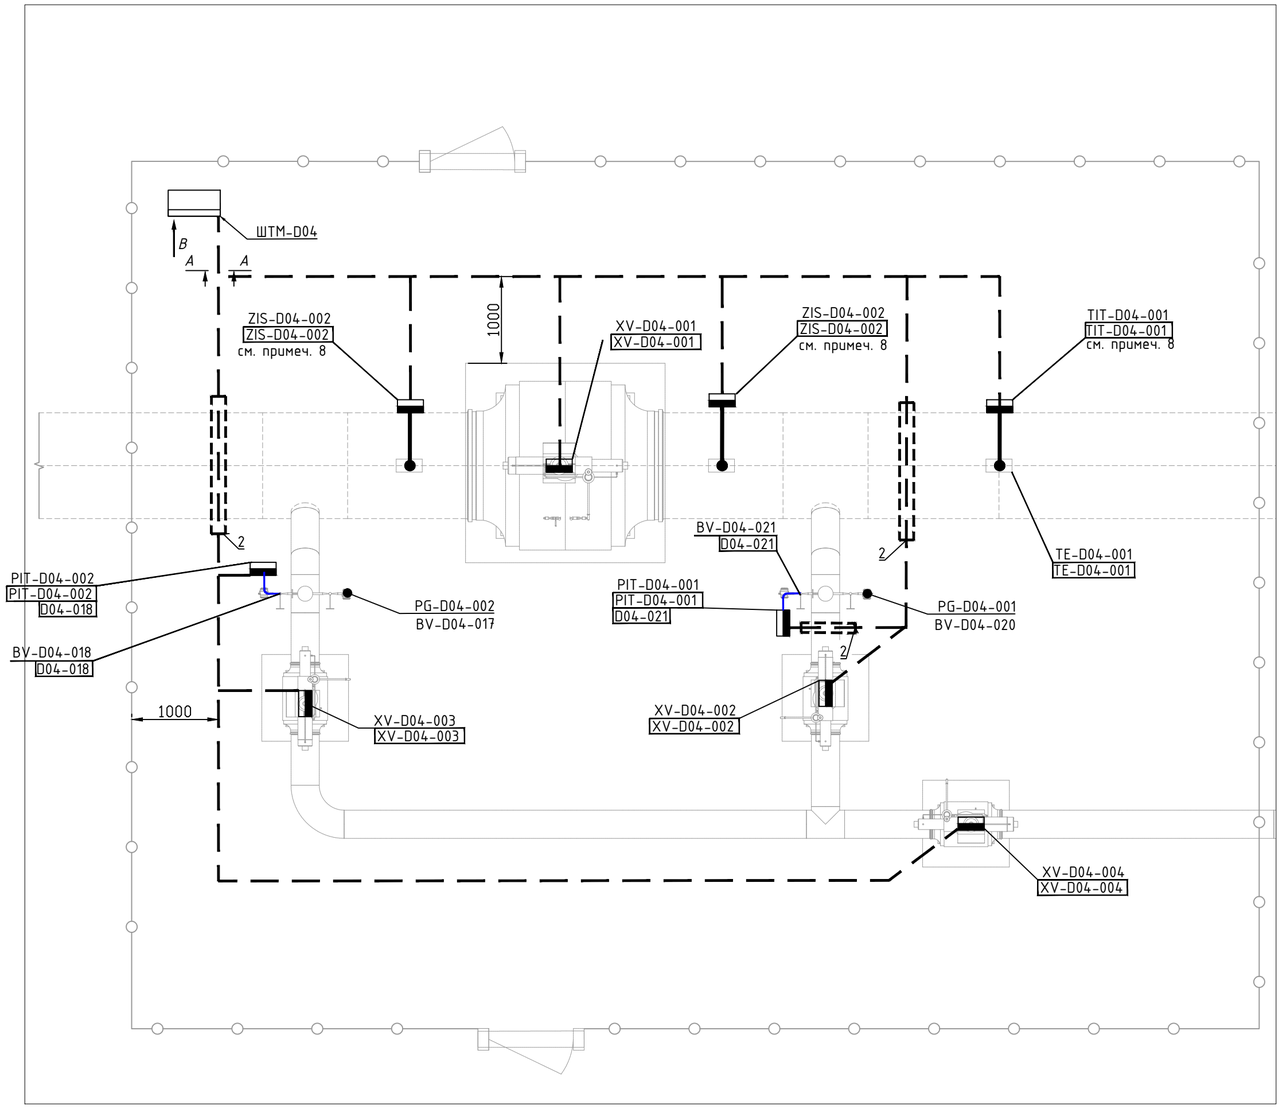

Поз.	Обозначение	Наименование	Кол.	Масса ед., кг	Приме-чание
1	ЛСЭ-300	Лента сигнальная	40		м
2	ТУ 2248-019-47022248-2008	Жесткая двустенная гофрированная труба для прокладки в грунте и под автомобильными дорогами, ПНД, ф75мм	3		м
3	ТУ 2248-015-47022248-2006	Труба жесткая гладкая ПНД Ø75 мм для защиты кабельных линий, для прокладки в грунте и на открытом воздухе, УФ-стойкая, без протяжки.	3		м
4	ТУ 2247-011-79523310-2006	Термоусадочная трубка с коэффициентом усадки 2:1 ТНТнг-LS-100/50	2		м

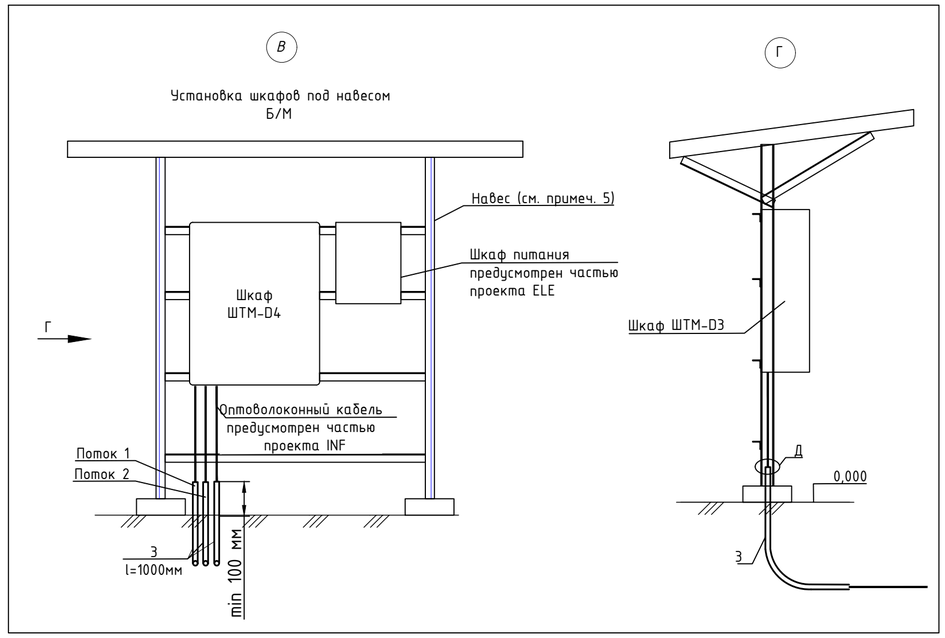


1. Данный чертёж разработан для крановых узлов на основании чертежа EWE0426-MGL1-PRE-054-DRW-720205.
2. Позиции приборов и нумерация кабелей соответствует схеме соединений внешних проводок EWE0426-MGL1-SYS-054-SCM-700305.
3. Все приборы, находящиеся под напряжением, заземлить согласно ПУЭ и руководствам по эксплуатации на приборы.
4. Монтаж защитного заземления выполнить в соответствии с требованиями ПУЭ.
5. Шкаф телемеханики установить под навесом,предусмотрен частью проекта STR. Отверстия для крепления шкафа сверлить по месту.
6. При прокладке кабелей в земле в ПНД трубах выполнить уплотнение кабеля с обоих концов труб джутовыми плетеными шнурами, обмазанными водонепроницаемой (мятой) глиной на глубину не менее 300 мм., согласно узлу Б.
7. При пересечении в земле кабелем КИП технологических трубопроводов кабель проложить на расстоянии не менее 0,25 м в свету по вертикали от трубопровода. На участке пересечения, а также на расстоянии по 2 м в каждую сторону от него, кабель проложить в трубе ПНД двустенной жесткой.
8. Установка приборов на стойке КИПиА см. документ EWE0426-MGL1-SYS-054-DRW-720302.
9. За относительную отметку 0,000 принята проектная отметка уровня земли.
10. Земляные работы на территории площадки производить ручным методом.

А1


Поток 1	Поток 2
TIT-D04-001	XV-D04-002
PIT-D04-001	XV-D04-003
PIT-D04-002	XV-D04-004
ZIS-D04-002	XV-D04-001
ZIS-D04-002	

А-А

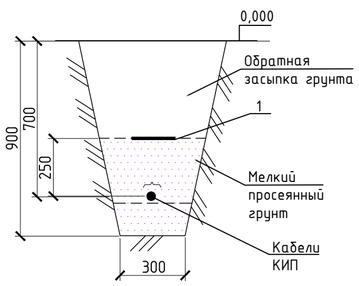


Б

Типовой узел уплотнения кабеля в трубе в земле
Б/М

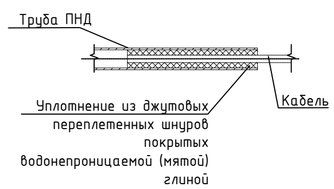

Д

Типовой узел прохода кабеля в/из траншеи
Б/М

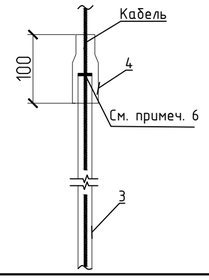

Ред.	Дата	Назначение ревизии	Проверил	Утвердил
A1	18.08.2026	Утверждено для строительства		
R1	10.07.2026	Выпущено для рассмотрения		

ЗАКАЗЧИК: UTG ГЕНЕРАЛЬНЫЙ ПОДРЯДЧИК: UET ПОДРЯДЧИК: PBG ГЕНЕРАЛЬНЫЙ ПРОЕКТИРОВЩИК: EAST WEST ENGINEERING

EWE0426-MGL1-SYS-054-PLA-730306-A1

«СТРОИТЕЛЬСТВО НОВЫХ НИТОК (УЧАСТКОВ) ГАЗОПРОВОДОВ «ГАЗЛИ – САРИМОЙ» И «АКЧАЛОК – ГАЗЛИ – НУКУС» ОБЩЕЙ ПРОТЯЖЕННОСТЬЮ НЕ МЕНЕЕ 275 КМ».

Изм.	Кол.уч.	Лист	№док.	Подпись	Дата
ГИП		Схабицкий А.			08.2026
Нач.отд.		Кабулова Е.			08.2026
Исполн.		Махмудов И.			08.2026
Н.контр		Схабицкий А.			08.2026

Газопрвод «Газли-Сарымой» (54 КМ)
Линейный крановый узел DN1200 КУП-D4

Стадия	Лист	Листов
РД	1	1

План расположения оборудования и проводок

ООО "EAST-WEST Engineering"
г. Ташкент 2026г.

Взам. инв. №
Подпись и дата
Инв.№ подл.

Формат / Format A2