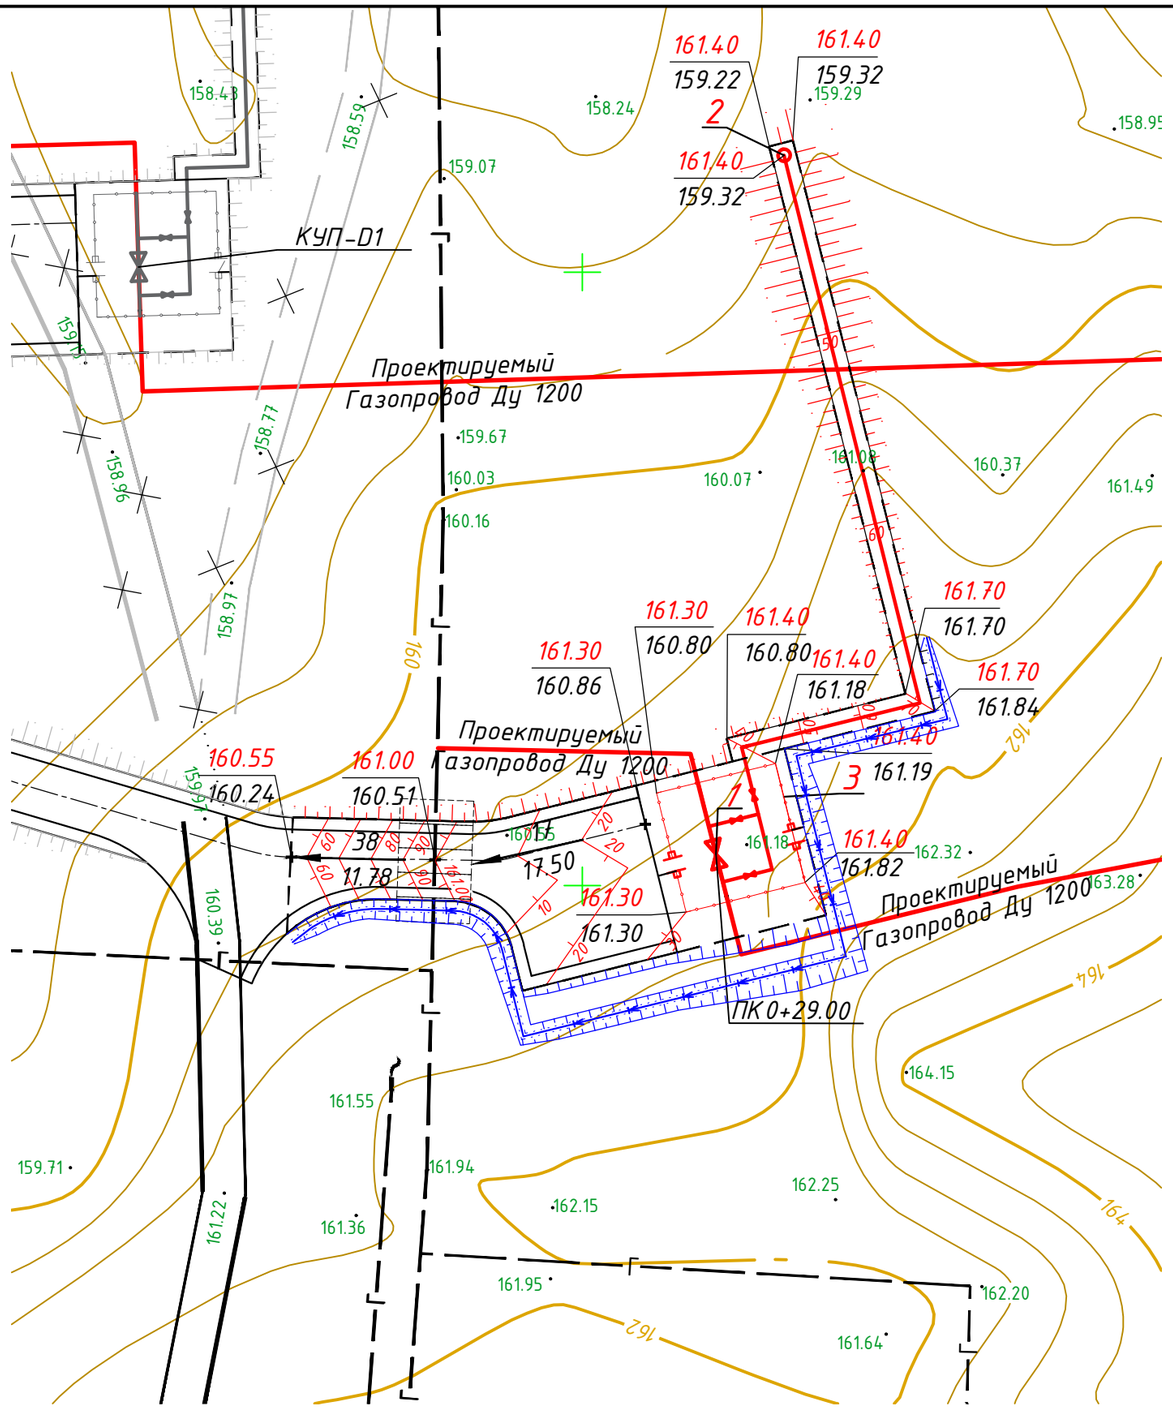


Экспликация зданий и сооружений

Номер на плане	Наименование	Примечание
1	Крановый узел Ду 1200	
2	Продувочная свеча	
3	Проектируемое сетчатое ограждение	

Условные обозначения

- Ограждение
- Калитка
- Граница планировки
- Существующий газопровод
- Проектируемый газопровод ДУ-1200
- 161.40 / 160.80 — Проектная отметка / Существующая отметка
- 20 — Проектные красные горизонтали
- Откосы насыпи
- Откосы выемки
- Водоотводная канава

Примечания:

При составлении настоящего чертежа были использованы :

1. Материалы топографо-геодезической съемки, предоставлены АО "O'ZLITINEFTGAZ".
2. Система координат местная. Высотные отметки даны в Балтийской системе.
3. Размеры даны в метрах.
4. Площадка кранового узла КУП-D2 привязана линейно к пикету ПК 0+29.00.
5. Данный лист смотри совместно с листами разделов PIL, PRE, ELE, STR, SYS.
6. Детальный план кранового узла см. EWE0426-MGL1-PRE-054-DRW-710203.
7. План организации рельефа кранового узла узла КУП-D1 см. EWE0426-MGL1-GLT-054-DRW-700103.
8. Угол пересечения подземного газопровода с автомобильной дорогой показан на разбивочном плане см. EWE0426-MGL1-GLT-054-DRW-710102.

Рев.	Дата	Назначение ревизии	Проверил	Утвердил
A2	24.09.2026	Выпущено для строительства		
A1	20.08.2026	Выпущено для строительства		
R1	14.07.2026	Выпущено для рассмотрения		

ЗАКАЗЧИК: UTG UKTRANSGAZ

ГЕНЕРАЛЬНЫЙ ПОДРЯДЧИК: UET UZBEKENERGOTAMIR

ПОДРЯДЧИК: PBG Pro Build Generation

ГЕНЕРАЛЬНЫЙ ПРОЕКТИРОВЩИК: EAST WEST ENGINEERING

Изм.	Кол.уч.	Лист	№ док.	Подпись	Дата	
ГИП		Схабицкий А.			09.2026	
Нач.отд.		Нигманова Н.			09.2026	
Исполн.		Нигманова Н.			09.2026	
Н.контр		Схабицкий А.			09.2026	

EWE0426-MGL1-GLT-054-DRW-710103-A2

«СТРОИТЕЛЬСТВО НОВЫХ НИТОК (УЧАСТКОВ) ГАЗОПРОВОДОВ «ГАЗЛИ - САРИМОЙ» И «АКЧАЛОК - ГАЗЛИ - НУКУС» ОБЩЕЙ ПРОТЯЖЕННОСТЬЮ НЕ МЕНЕЕ 275 км».

ГАЗОПРОВОД «ГАЗЛИ-САРИМОЙ» (54 км)

Генеральный план и транспорт.

Стадия	Лист	Листов
РД	1	1

КУП_D2.
План организации рельефа М 1:500

EAST WEST ENGINEERING

ООО "EAST-WEST Engineering"
г. Ташкент 2026 г.

Взам. инв. N | Подпись и дата | Инв. N подл.

Формат / Format A3