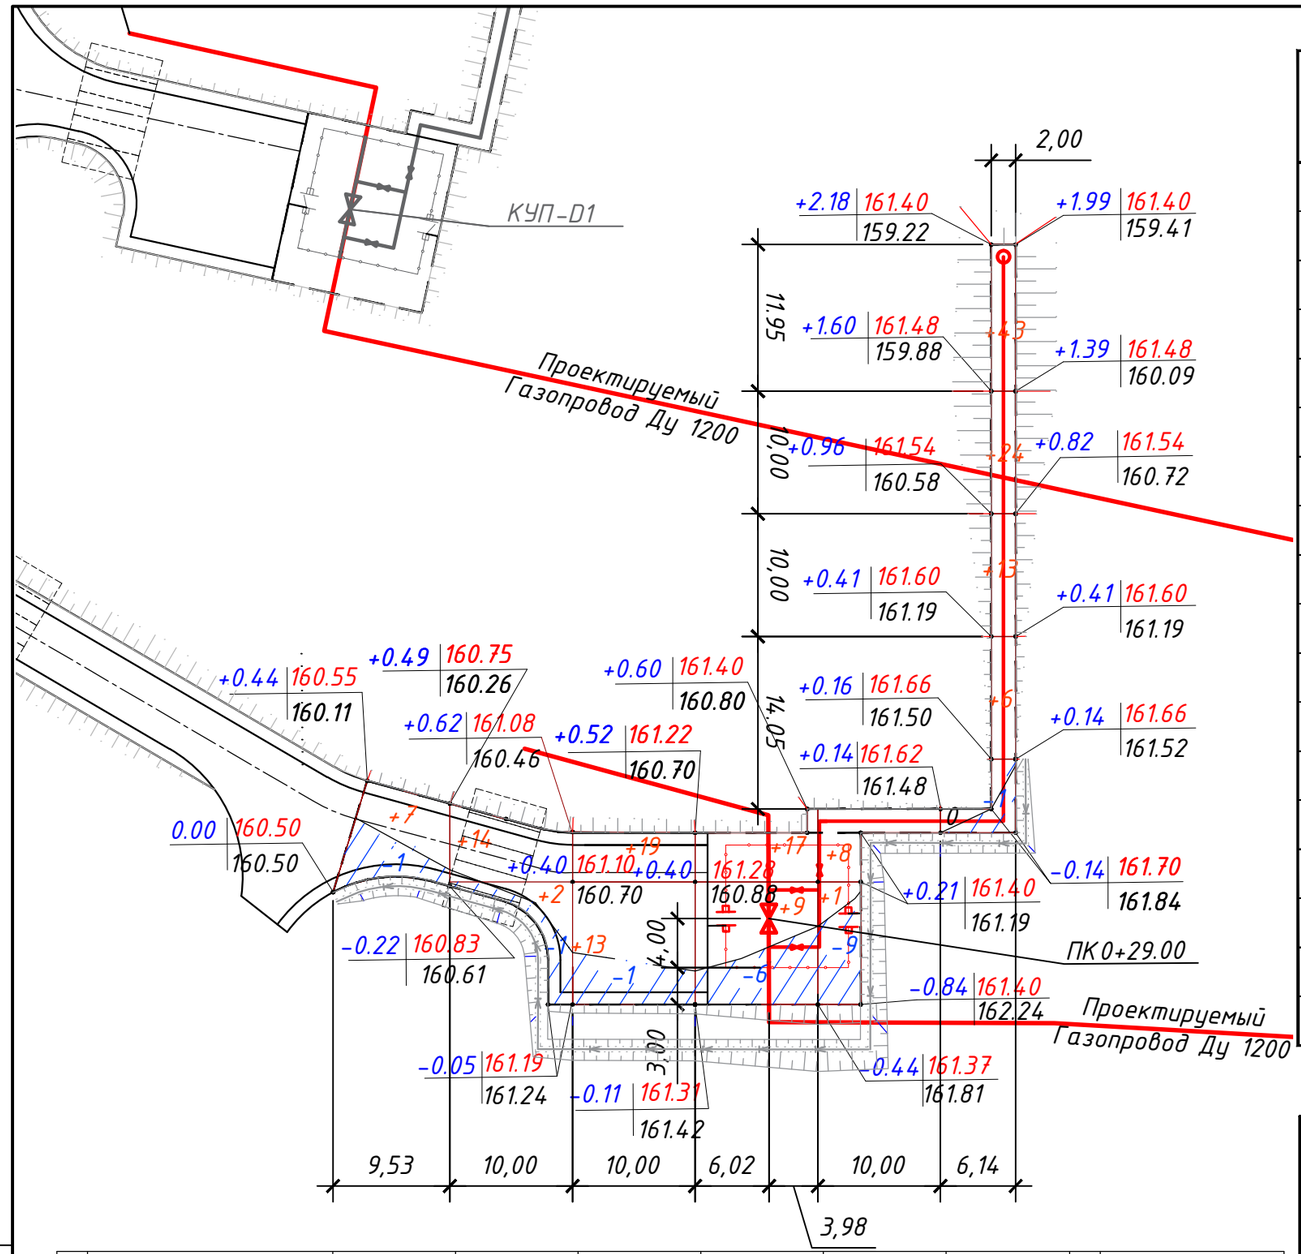


Итого,м3							Всего,м3	
	Насыпь (+)	+7	+16	+32	+26	+9	+86	+176
	Выемка (-)	-1	-1	-1	-6	-9	-1	-19

Примечания:

При составлении настоящего чертежа были использованы :

1. Сетка картограммы привязана линейно к пикету ПК 0+29.00.
2. Сетка квадратов объёмы земляных масс разбита на ячейки размерами 10х10м.
3. Производство земляных работ вести в соответствии с требованиями КР 02.01.
4. План земляных масс кранового узла КУП-D1 см. EWE0426-MGL1-GLT-054-DRW-700104;

Условные обозначения:

+10 — объем насыпи в м³

-3 — объем выемки в м³

+0.59 | 159.34 / 158.71 — рабочая отм. | проектная отм. / отм.сущ.рельефа

откосы насыпи

откосы выемки

Ведомость объемов земляных масс

Наименование грунта	Количество, м³		Примечание
	Насыпь (+)	Выемка (-)	
1. Грунт планировки территории	176	19	
2. Вытесненный грунт, в т.ч. при устройстве:			
а) автодорожных покрытий		91	
б) покрытий площадок		13	
в) водоотводной канавы		34	
г) плодородной почвы на участках насыпи			
д) плодородной почвы на участках выемки			
3. Замена растительного грунта на участках насыпи			
4. Грунт для устройства откосов насыпи	162		
5. Грунт для устройства откосов выемки		4	
6. Поправка на уплотнение	34		
Всего пригодного грунта	372	161	
5. Недостаток пригодного грунта		211**	
8. Плодородный грунт, всего в т.ч.:		175	
а) Используемый для озеленения территории			
б) Избыток плодородного грунта	175		
(рекультивация земель)			
9. Итого перерабатываемого грунта	547	547	

* С учетом плодородного грунта.

** В карьере. Общая площадь картограммы = 584 м2

Рев.	Дата	Назначение ревизии	Проверил	Утвердил
A2	24.09.2026	Выпущено для строительства		
A1	20.08.2026	Выпущено для строительства		
R1	14.07.2026	Выпущено для рассмотрения		

ЗАКАЗЧИК: UTG UKTRANSGAZ

ГЕНЕРАЛЬНЫЙ ПОДРЯДЧИК: UET UZBEKENERGOTAMIR

ПОДРЯДЧИК: PBG Pro Build Generation

ГЕНЕРАЛЬНЫЙ ПРОЕКТИРОВЩИК: EAST WEST ENGINEERING

Изм.	Кол.уч.	Лист	№док.	Подпись	Дата			
ГИП		Схабицкий А.			08.2026	EWE0426-MGL1-GLT-054-DRW-710104-A2		
Нач.отд.		Нигманова Н.			08.2026	«СТРОИТЕЛЬСТВО НОВЫХ НИТОК (УЧАСТКОВ) ГАЗОПРОВОДОВ «ГАЗЛИ - САРИМОЙ» И «АКЧАЛОК - ГАЗЛИ - НУКУС» ОБЩЕЙ ПРОТЯЖЕННОСТЬЮ НЕ МЕНЕЕ 275 км».		
Исполн.		Нигманова Н.			08.2026	ГАЗОПРОВОД «ГАЗЛИ-САРИМОЙ» (54 км) Генеральный план и транспорт.	Стадия: РД; Лист: 1; Листов: 1	
Н.контр		Схабицкий А.			08.2026	КУП_D2. План земляных масс М 1:500	EAST WEST ENGINEERING	ООО "EAST-WEST Engineering" г. Ташкент 2026 г.

Взам. инв. N | Подпись и дата | Инв. N подл.

Формат / Format A3