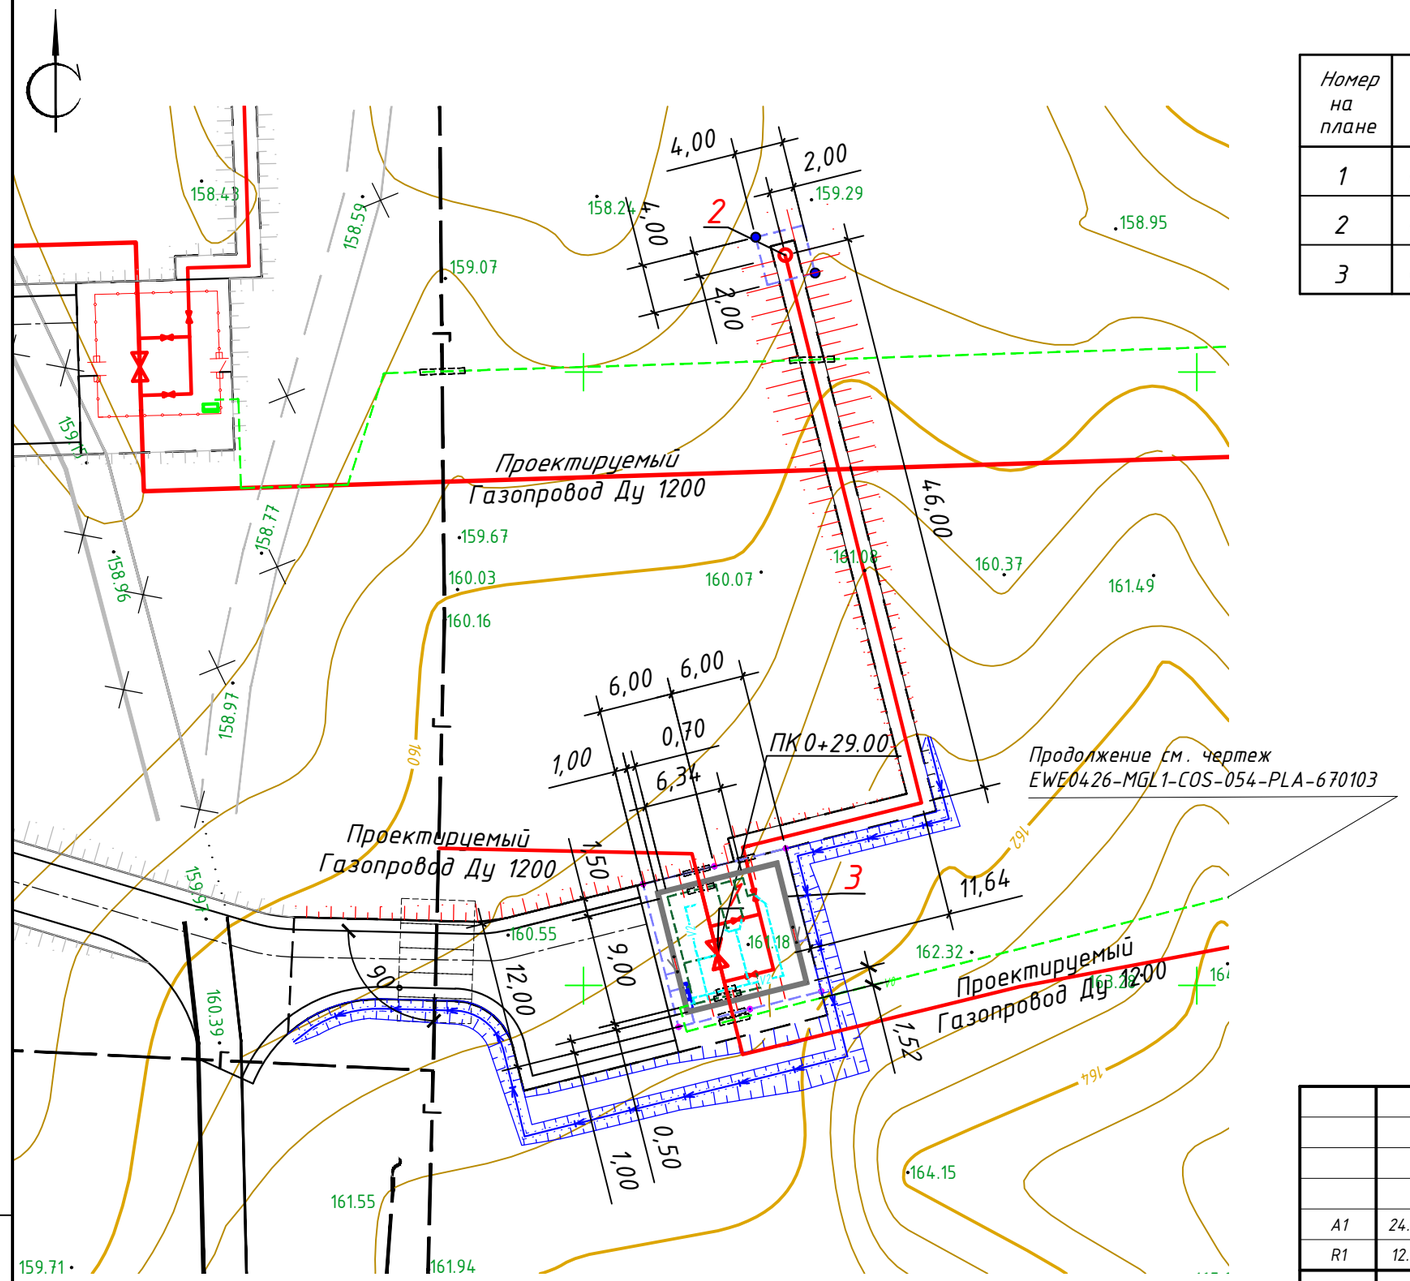


Экспликация зданий и сооружений

Номер на плане	Наименование	Примечание
1	Крановый узел Ду 1200	
2	Продувочная свеча	
3	Ограждение сетчатое	

Условные обозначения

- Существующий газопровод
- Проектируемый газопровод ДУ-1200
- Проектируемый газопровод ДУ-1000
- Вертикальный заземлитель Ф 16
- Полоса заземления 4х40
- Гибкий провод
- Стальная труба
- Шкаф телемеханики (ШТМ)
- Датчики давления
- V2 — Проектный кабель КИПиА в траншее
- V2 — Проектный кабель КИПиА в ПНД трубе
- V0 — Проектируемый волоконно-оптический кабель в траншее
- V0 — Проектируемый волоконно-оптический кабель в трубе

Примечания:

При составлении настоящего чертежа были использованы :

1. Материалы топографо-геодезической съемки, предоставлены АО "O'ZLITINEFTGAZ".
2. Площадка кранового узла КУП-D2 привязана линейно к пикету ПК 0+29.00
3. Расстояние по горизонтали (в свету) от подземных инженерных сетей до зданий и сооружений следует принимать не менее указанных в табл. 9 см. ШНК 2.09.17-21 "Проектирование генеральных планов промышленных предприятий".
4. Расположение оборудования и прокладку кабелей уточнить по месту при монтаже.
5. Данный лист смотри совместно с листами разделов PIL, PRE, ELE, STR, SYS.
6. Детальный план кранового узла см. EWE0426-MGL1-PRE-054-DRW-710203.
7. Детальный план сетей КИПиА см. EWE0426-MGL1-SYS-054-PLA-710306.
8. Детальный план сетей заземления см. EWE0426-MGL1-ELE-054-DRW-710402.
9. Детальный план ограждения см. EWE0426-MGL1-STR-054-DRW-710507.

Рев.	Дата	Назначение ревизии	Проверил	Утвердил
A1	24.09.2026	Выпущено для строительства		
R1	12.08.2026	Выпущено для рассмотрения		

ЗАКАЗЧИК: UTG UKTAMNEFTEGAZ | ГЕНЕРАЛЬНЫЙ ПОДРЯДЧИК: UET UZBEKENERGOTAMIR | ПОДРЯДЧИК: PBG Pro Build Generation | ГЕНЕРАЛЬНЫЙ ПРОЕКТИРОВЩИК: EAST WEST ENGINEERING

Изм.	Кол.уч.	Лист	№док.	Подпись	Дата
ГИП		Схабицкий А.			09.2026
Нач.отд.		Нигманова Н.			09.2026
Исполн.		Горлова О.			09.2026
Н.контр		Схабицкий А.			09.2026

EWE0426-MGL1-GLT-054-DRW-710105-A1

«СТРОИТЕЛЬСТВО НОВЫХ НИТОК (УЧАСТКОВ) ГАЗОПРОВОДОВ «ГАЗЛИ - САРИМОЙ» И «АКЧАЛОК - ГАЗЛИ - НУКУС» ОБЩЕЙ ПРОТЯЖЕННОСТЬЮ НЕ МЕНЕЕ 275 км».

ГАЗОПРОВОД «ГАЗЛИ-САРИМОЙ» (54 км)

Генеральный план и транспорт.

Стадия	Лист	Листов
РД	1	1

КУП-D2.
Сводный план инженерных сетей.
М 1:500

EAST WEST ENGINEERING

ООО "EAST-WEST Engineering"
г. Ташкент 2026 г.

Взам. инв. N | Подпись и дата | Инв. N подл.

Формат / Format A3