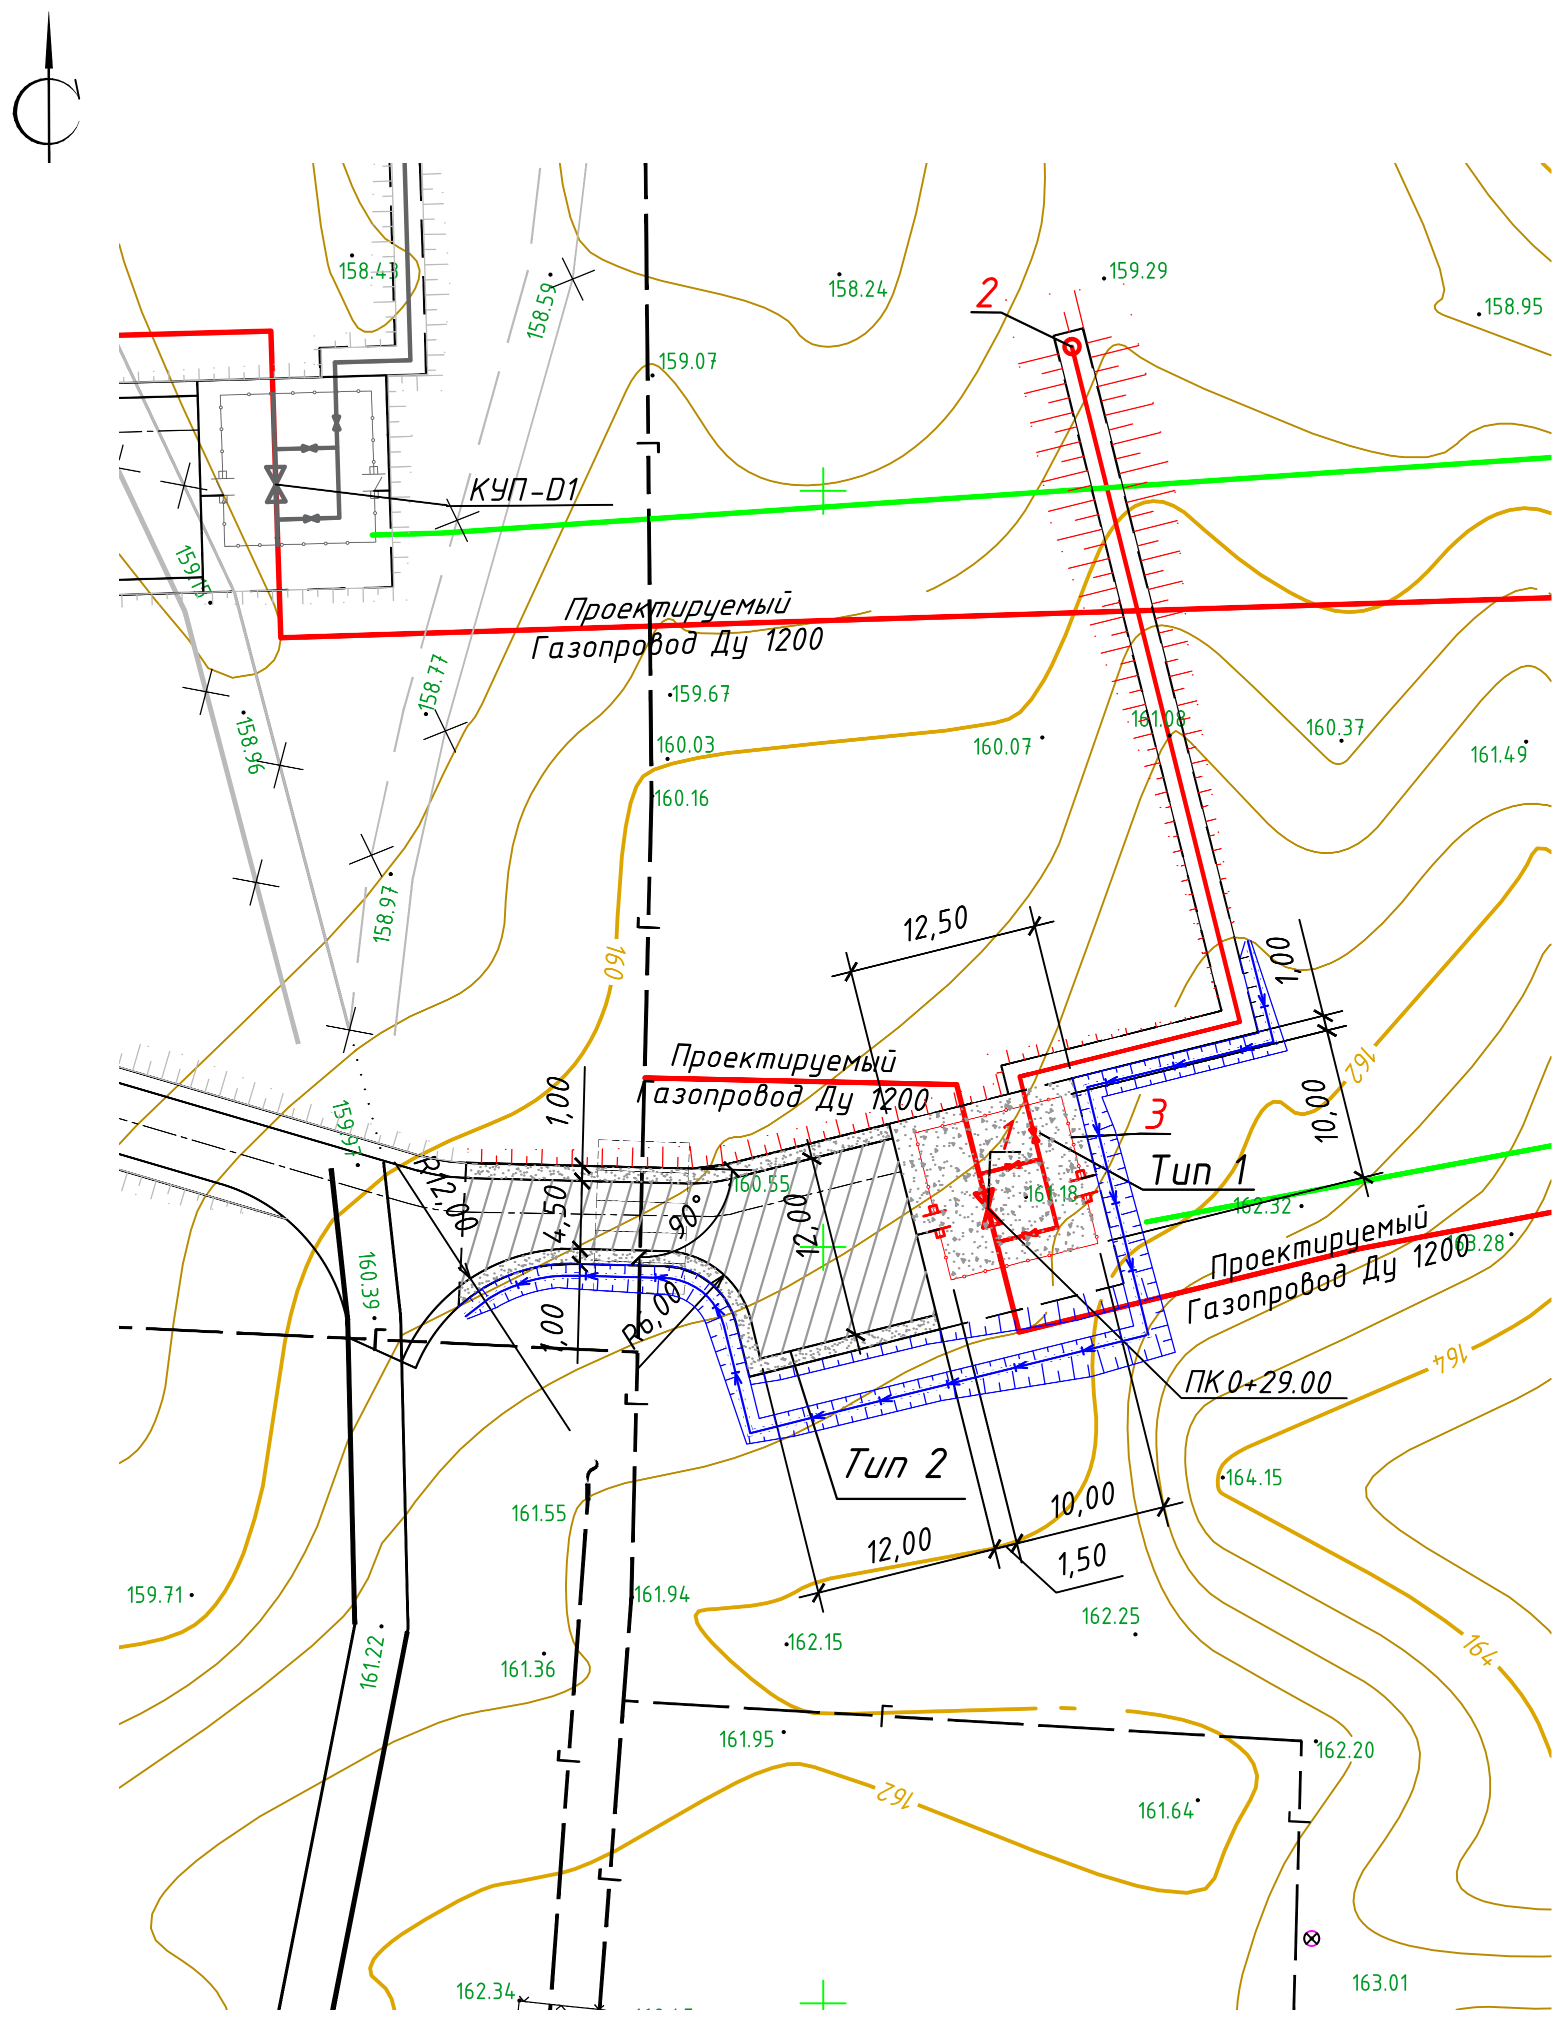

Спецификация элемента пересечения дороги с газопроводом
(Спецификация на 1 элемент)

Поз.	Обозначение	Наименование	Кол. шт.	Масса ед., кг	Примечание
1	Серия 3.503.1-91	Плита дорожная ПДН-6х2	5	шт	
2	ГОСТ Р 50970-2011	Столбик сигнальный типа С1	8	шт	
3		Предупреждающий знак	2	шт	

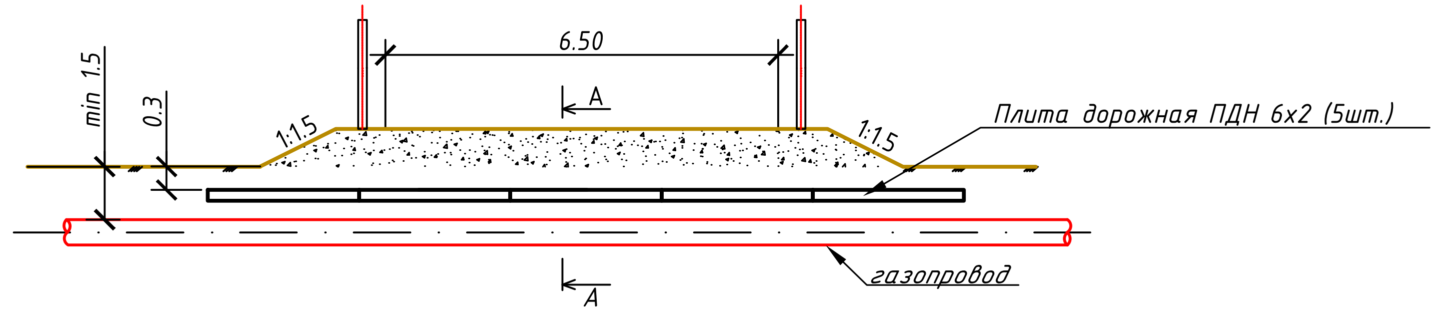

А – А

Пересечение газопроводом автомобильной дороги

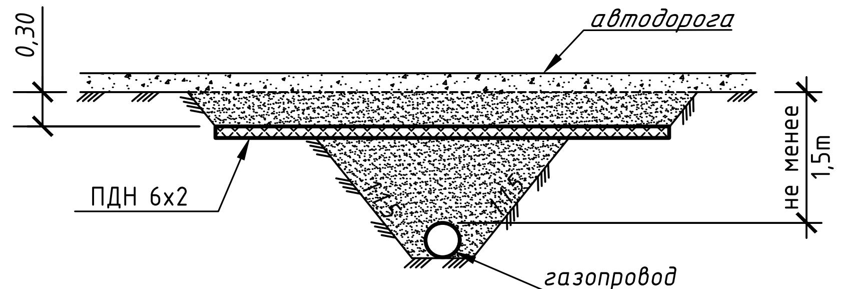

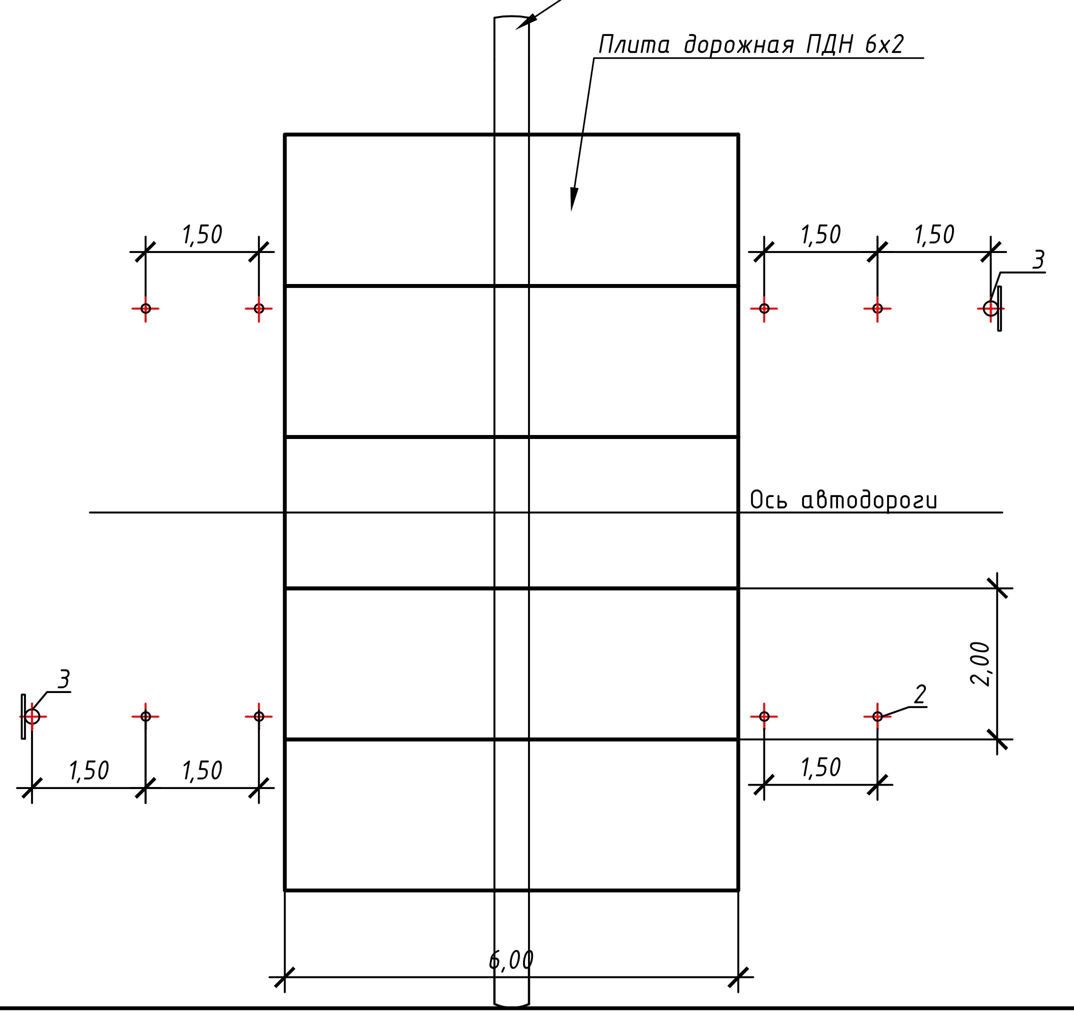

Тип 1

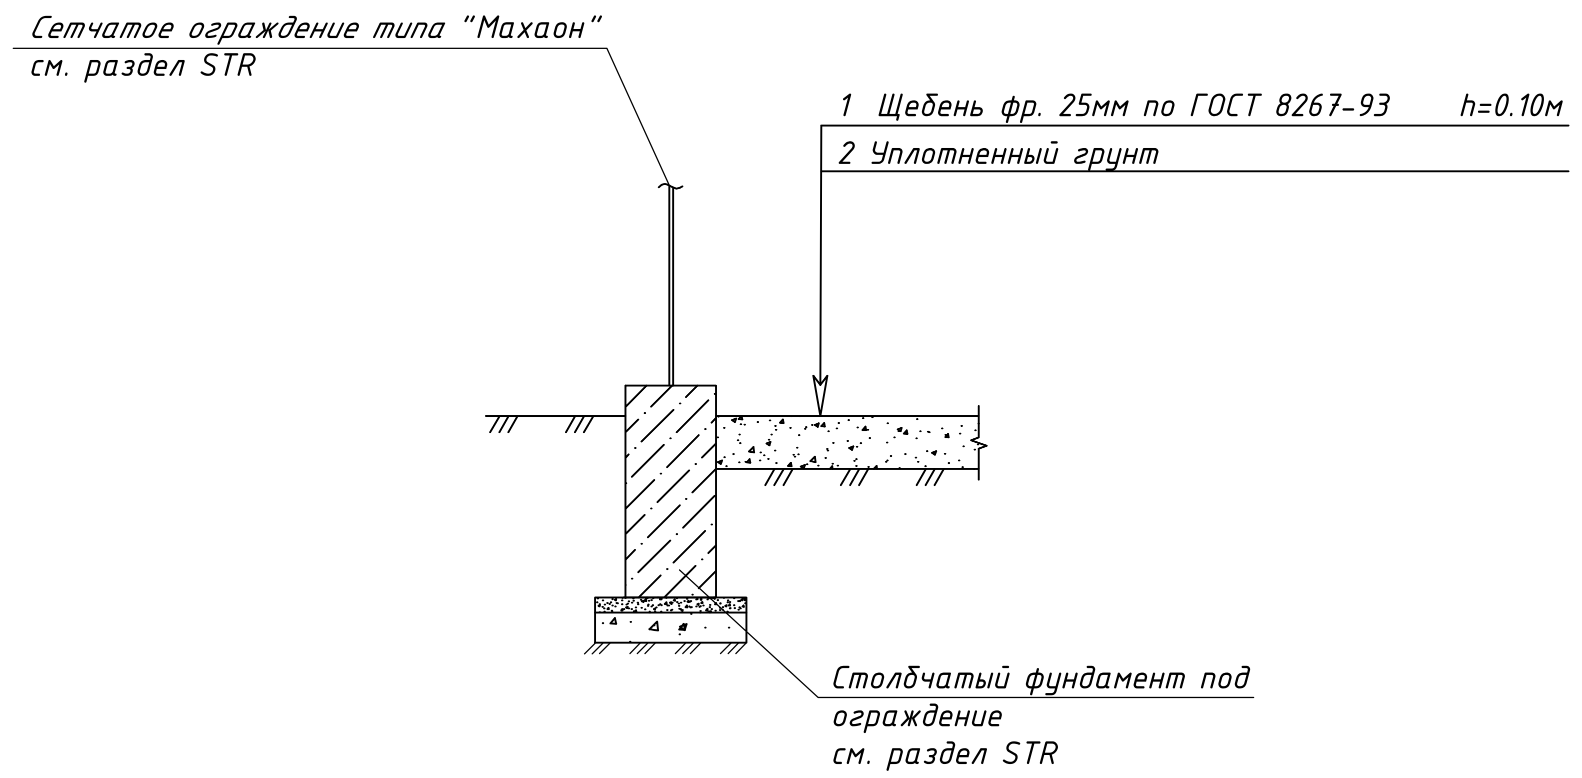

Тип 2

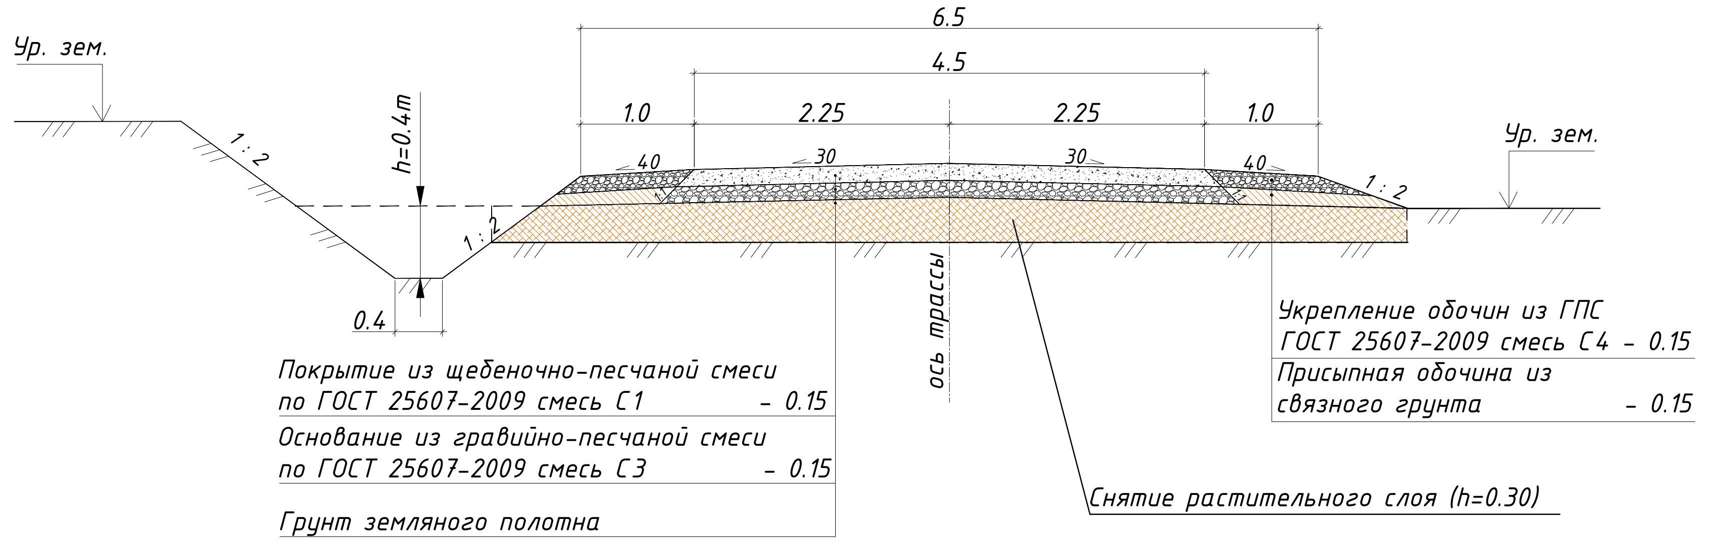
Ур. зем.
Ур. зем.
6.5
4.5
1.0
2.25
2.25
1.0
40
30
30
40
1 : 2
1 : 2
1 : 2
h=0.4m
0.4
ось трассы
Покрытие из щебеночно-песчаной смеси
по ГОСТ 25607-2009 смесь С1 - 0.15
Основание из гравийно-песчаной смеси
по ГОСТ 25607-2009 смесь С3 - 0.15
Грунт земляного полотна
Снятие растительного слоя (h=0.30)
Укрепление обочин из ГПС
ГОСТ 25607-2009 смесь С4 - 0.15
Присыпная обочина из
связного грунта - 0.15

Примечания:

При составлении настоящего чертежа были использованы :
1. Материалы топографо-геодезической съемки, предоставлены АО "O'ZLITINEFTGAZ".
2. Система координат местная. Высотные отметки даны в Балтийской системе.
3. Размеры даны в метрах.
4. Площадка кранового узла КУП-D2 привязана линейно к пикету ПК 0+29.00.
5. Данный лист смотри совместно с листами разделов PIL, PRE, ELE, STR, SYS.
6. Детальный план кранового узла см. EWE0426-MGL1-PRE-054-DRW-710203.
6. План благоустройства территории кранового узла КУП-D1 см. EWE0426-MGL1-GLT-054-DRW-700106.

Экспликация зданий и сооружений

Номер на плане	Наименование	Примечание
1	Крановый узел Ду 1200	
2	Продувочная свеча	
3	Проектируемое сетчатое ограждение	

Ведомость тротуаров, дорожек и площадок

Тип	Обозначение	Наименование	Ед. изм.	Примечание
		Покрытие площадки		
1	▒	Покрытие из щебня по ГОСТ 8267-93, h=0.10	$м^2$	130.0
		Покрытие проездов		
2	▨	Покрытие из щебеночно-песчаной смеси по ГОСТ 25607-2009 смесь С1 h=0,15м Основание из гравийно-песчаной смеси по ГОСТ 25607-2009 смесь С3 h=0,15м	$м^2$	240.0
		Укрепление обочин из ГПС ГОСТ 25607-2009 смесь С4 h=0,15м	$м^2$	65.0

Рев.	Дата	Назначение ревизии	Проверил	Утвердил
А2	24.09.2026	Выпущено для строительства		
А1	20.08.2026	Выпущено для строительства		
R1	10.07.2026	Выпущено для рассмотрения		

ЗАКАЗЧИК: UTG UZTRANSGAZ

ГЕНЕРАЛЬНЫЙ ПОДРЯДЧИК: UET UZBEKENERGOTAMIR

ПОДРЯДЧИК: PBG Pro Build Generation

ГЕНЕРАЛЬНЫЙ ПРОЕКТИРОВЩИК: EAST WEST ENGINEERING

EWE0426-MGL1-GLT-054-DRW-710106-A2

«СТРОИТЕЛЬСТВО НОВЫХ НИТОК (УЧАСТКОВ) ГАЗОПРОВОДОВ «ГАЗЛИ - САРИМОЙ» И «АКЧАЛОК - ГАЗЛИ - НУКУС» ОБЩЕЙ ПРОТЯЖЕННОСТЬЮ НЕ МЕНЕЕ 275 км».

Изм.	Кол.уч.	Лист	№ док.	Подпись	Дата
ГИП		Схабицкий А.			09.2026
Нач.отд.		Нигманова Н.			09.2026
Исполн.		Нигманова Н.			09.2026
Н.контр		Схабицкий А.			09.2026

ГАЗОПРОВОД «ГАЗЛИ-САРИМОЙ» (54 км)

Генеральный план и транспорт.

Стадия	Лист	Листов
РД	1	1

КУП_D2.
План благоустройства территории
М 1:500

EAST WEST ENGINEERING

ООО "EAST-WEST Engineering"
г. Ташкент 2026 г.

Формат / Format A4x4

Инв. N подл.
Подпись и дата
Взам. инв. N