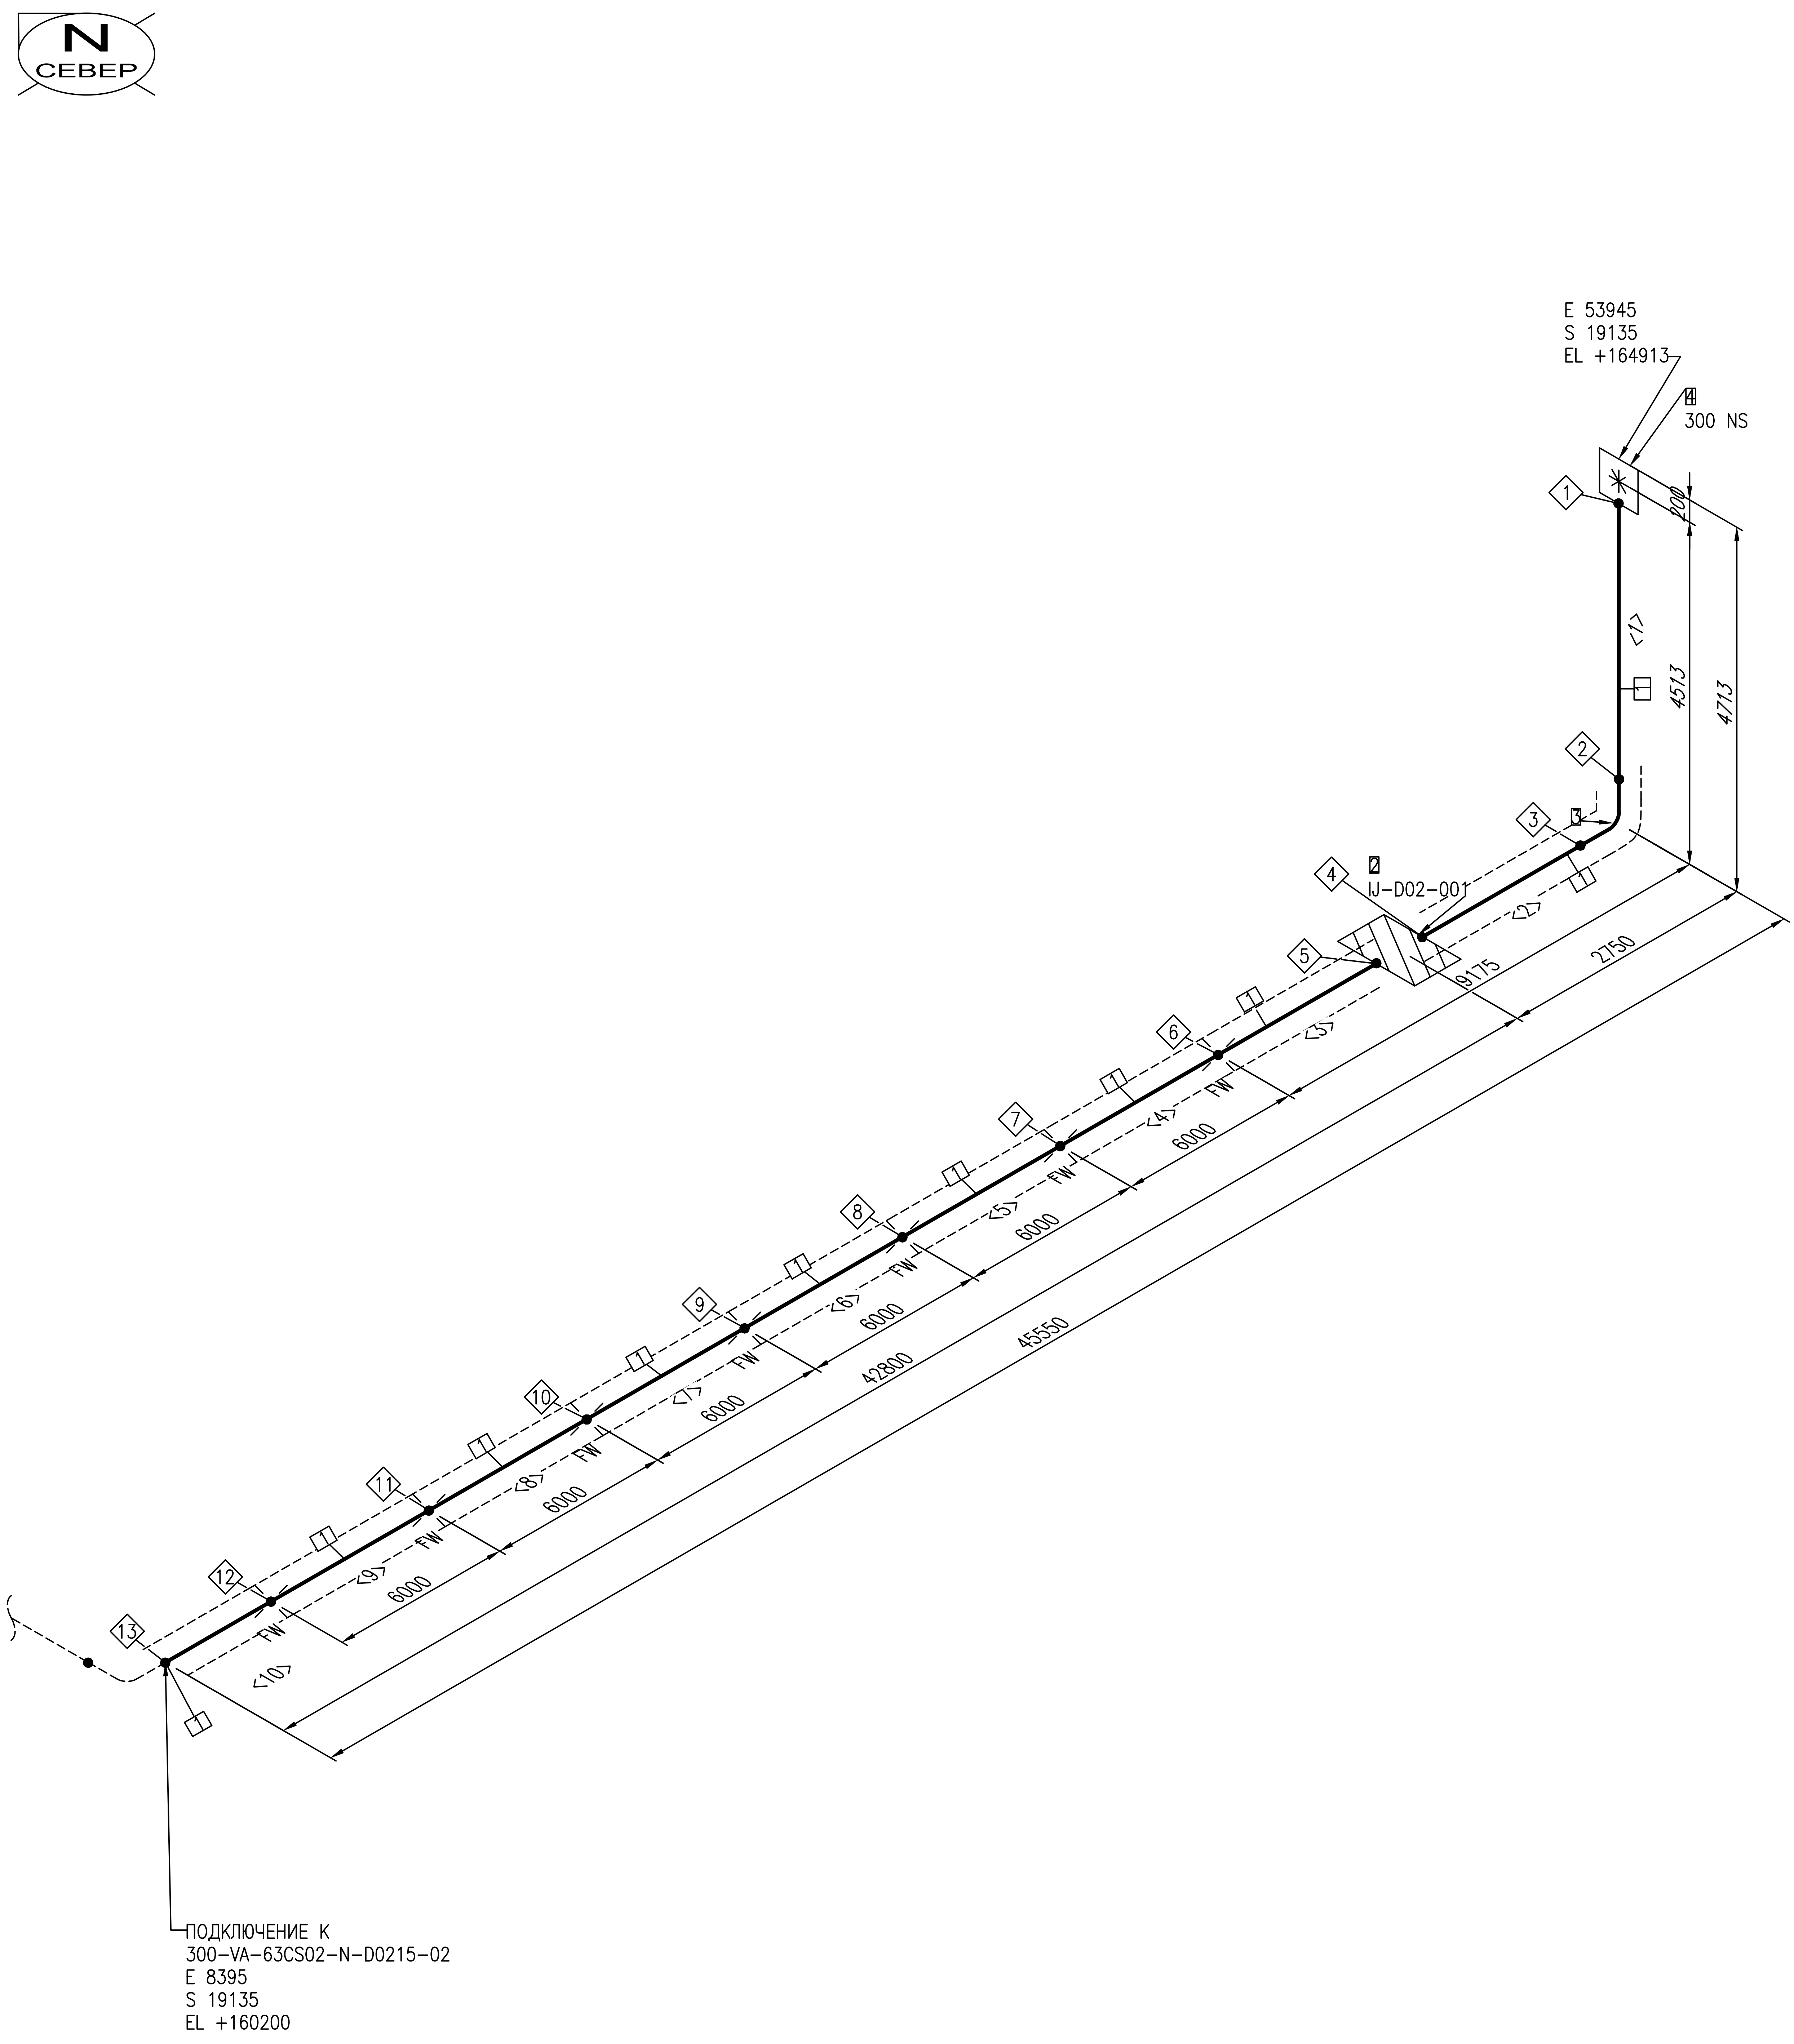
N
СЕВЕР
E 53945
S 19135
EL +164913
4
300 NS
1
200
<1>
1
4513
4713
2
3
3
4
2
IJ-D02-001
<2>
2750
9175
5
1
<3>
6
FW
1
<4>
6000
7
FW
1
<5>
6000
8
FW
1
<6>
6000
42800
45550
9
FW
1
<7>
6000
10
FW
1
<8>
6000
11
FW
1
<9>
6000
12
FW
1
13
<10>
1
ПОДКЛЮЧЕНИЕ К
300-VA-63CS02-N-D0215-02
E 8395
S 19135
EL +160200

ПЕРЕЧЕНЬ СВАРНЫХ ШВОВ

№	DN	ТИП
1	300	BUTTWELD
2	300	BUTTWELD
3	300	BUTTWELD
4	300	BUTTWELD
5	300	BUTTWELD
6	300	FIELDWELD
7	300	FIELDWELD
8	300	FIELDWELD
9	300	FIELDWELD
10	300	FIELDWELD
11	300	FIELDWELD
12	300	FIELDWELD
13	300	BUTTWELD

ПЕРЕЧЕНЬ ТРУБНЫХ КАТУШЕК

№	DN	ДЛИНА
1	300	3863MM
2	300	1875MM
3	300	6000MM
4	300	6000MM
5	300	6000MM
6	300	6000MM
7	300	6000MM
8	300	6000MM
9	300	6000MM
10	300	375MM

СПЕЦИФИКАЦИЯ ИЗДЕЛИЙ И МАТЕРИАЛОВ

ПОЗ.	НАИМЕНОВАНИЕ	СТАНДАРТ	КОЛ.	ПРИМЕЧАНИЕ
1	Трубы стальные бесшовные горячедеформированные 09Г2С, 325X10	ТУ 14–3–1128–2000	48.2M	
2	Изолирующее соединение приварное, 6.3 МПа, 325X10	EWE0426–MGL1–PRE–054–DSH–610135	1	
3	Отвод ОК I 90–325(10K48)–5,5(6,9)–0,75–1,5DN–30, сталь 09Г2С	ТУ 1469–017–38948552–2015	1	
4	Оголовок продувочной свечи, приварной, 6.3 МПа, ОПС–325–С–У, 325X10	ТУ 1469–020–96950580–2011	1	

Трубопровод	ДАННЫЕ ПО ТРУБОПРОВОДУ		
300-VA-63CS02-N-D0215	Расчетные параметры	Температура	-26,9...+85 °C
		Давление	6,3 MPa
	Рабочие параметры	Температура	-20...+40 °C
		Давление	5,5 MPa
	Параметры испытания	Тип	Гидравлическое
Ссылочные чертежи No		Давление	6,9 MPa
EWE0426-MGL1-PRE-054-SCM-610104	Изоляция	Тип	HH
		Толщина	mm
	Катодная защита	Да или Нет	Да

Рев.	Дата	Назначение ревизии	Проверил	Утвердил
A1	07.09.2026	Утверждено для строительства		
R1	22.06.2026	Выпущено для рассмотрения		

ЗАКАЗЧИК: UTG UZTRANSGAZ

ГЕНЕРАЛЬНЫЙ ПОДРЯДЧИК: UET UZBEKENERGOTAMIR

ПОДРЯДЧИК: PBG Pro Build Generation

ГЕНЕРАЛЬНЫЙ ПРОЕКТИРОВЩИК: EAST WEST ENGINEERING

EWE0426-MGL1-PRE-054-ISO-710607-A1

«СТРОИТЕЛЬСТВО НОВЫХ НИТОК (УЧАСТКОВ) ГАЗОПРОВОДОВ «ГАЗЛИ – САРИМОЙ» И «АКЧАЛОК – ГАЗЛИ – НУКУС» ОБЩЕЙ ПРОТЯЖЕННОСТЬЮ НЕ МЕНЕЕ 275 КМ».

Изм.	Кол.уч.	Лист	№док.	Подпись	Дата
ГИП		Кирпичников С.			09.2026
Нач.отд.		Рябинин А.			09.2026
Исполн.		Таштимуров Р.			09.2026
Н.контр		Кирпичников С.			09.2026

ГАЗОПРОВОД «ГАЗЛИ-САРИМОЙ» (54 KM)
Линейный крановый узел DN1200 КУП-D2

Стадия	Лист	Листов
РД	1	2

Изометрический чертеж трубопровода
300-VA-63CS02-N-D0215

EAST WEST ENGINEERING
ООО "EAST-WEST Engineering"
г. Ташкент 2026г.

Взам. инв. №

Подпись и дата

Инв.№ подл.

Формат A2 594x420

ПЕРЕЧЕНЬ СВАРНЫХ ШВОВ		
№	DN	ТИП
1	300	BUTTWELD
2	300	BUTTWELD
3	300	BUTTWELD
4	300	BUTTWELD
5	300	FIELDWELD
6	300	FIELDWELD
7	300	BUTTWELD

СПЕЦИФИКАЦИЯ ИЗДЕЛИЙ И МАТЕРИАЛОВ				
ПОЗ.	НАИМЕНОВАНИЕ	СТАНДАРТ	КОЛ.	ПРИМЕЧАНИЕ
1	Трубы стальные бесшовные горячедеформированные 09Г2С, 325X10	ТУ 14-3-1128-2000	17.3M	
2	Отвод ОК I 90-325(10K48)-5,5(6,9)-0,75-1,5DN-30, сталь 09Г2С	ТУ 1469-017-38948552-2015	2	
3	Кран шаровой DN300 PN-6,3 МПа с пневмогидроприводом, приварной, подземный	EWE0426-MGL1-PRE-054-DSH-610121	1	


4418
4000
418
2550
6000
15000
450
<1>
<2>
<3>
<4>
1
2
3
4
5
6
7
FW
FW
1
2
2
3
XV-D02-004
300 NS
ПОДКЛЮЧЕНИЕ К
300-GT-63CS02-HH-D0202
E 3527
S 4135
EL +160200
ПОДКЛЮЧЕНИЕ К
300-VA-63CS02-N-D0215-01
E 8395
S 19135
EL +160200

ПЕРЕЧЕНЬ ТРУБНЫХ КАТУШЕК		
№	DN	ДЛИНА
1	300	3132MM
2	300	2100MM
3	300	6000MM
4	300	6000MM

Трубопровод
300-VA-63CS02-N-D0215
Ссылочные чертежи No
EWE0426-MGL1-PRE-054-SCM-610104

ДАННЫЕ ПО ТРУБОПРОВОДУ		
Расчетные параметры	Температура	-26,9...+85 °C
	Давление	6,3 MPa
Рабочие параметры	Температура	-20...+40 °C
	Давление	5,5 MPa
Параметры испытания	Тип	Гидравлическое
	Давление	6,9 MPa
Изоляция	Тип	HH
	Толщина	mm
Катодная защита	Да или Нет	Да

Рев.	Дата	Назначение ревизии	Проверил	Утвердил
A1	07.09.2026	Утверждено для строительства		
R1	22.06.2026	Выпущено для рассмотрения		

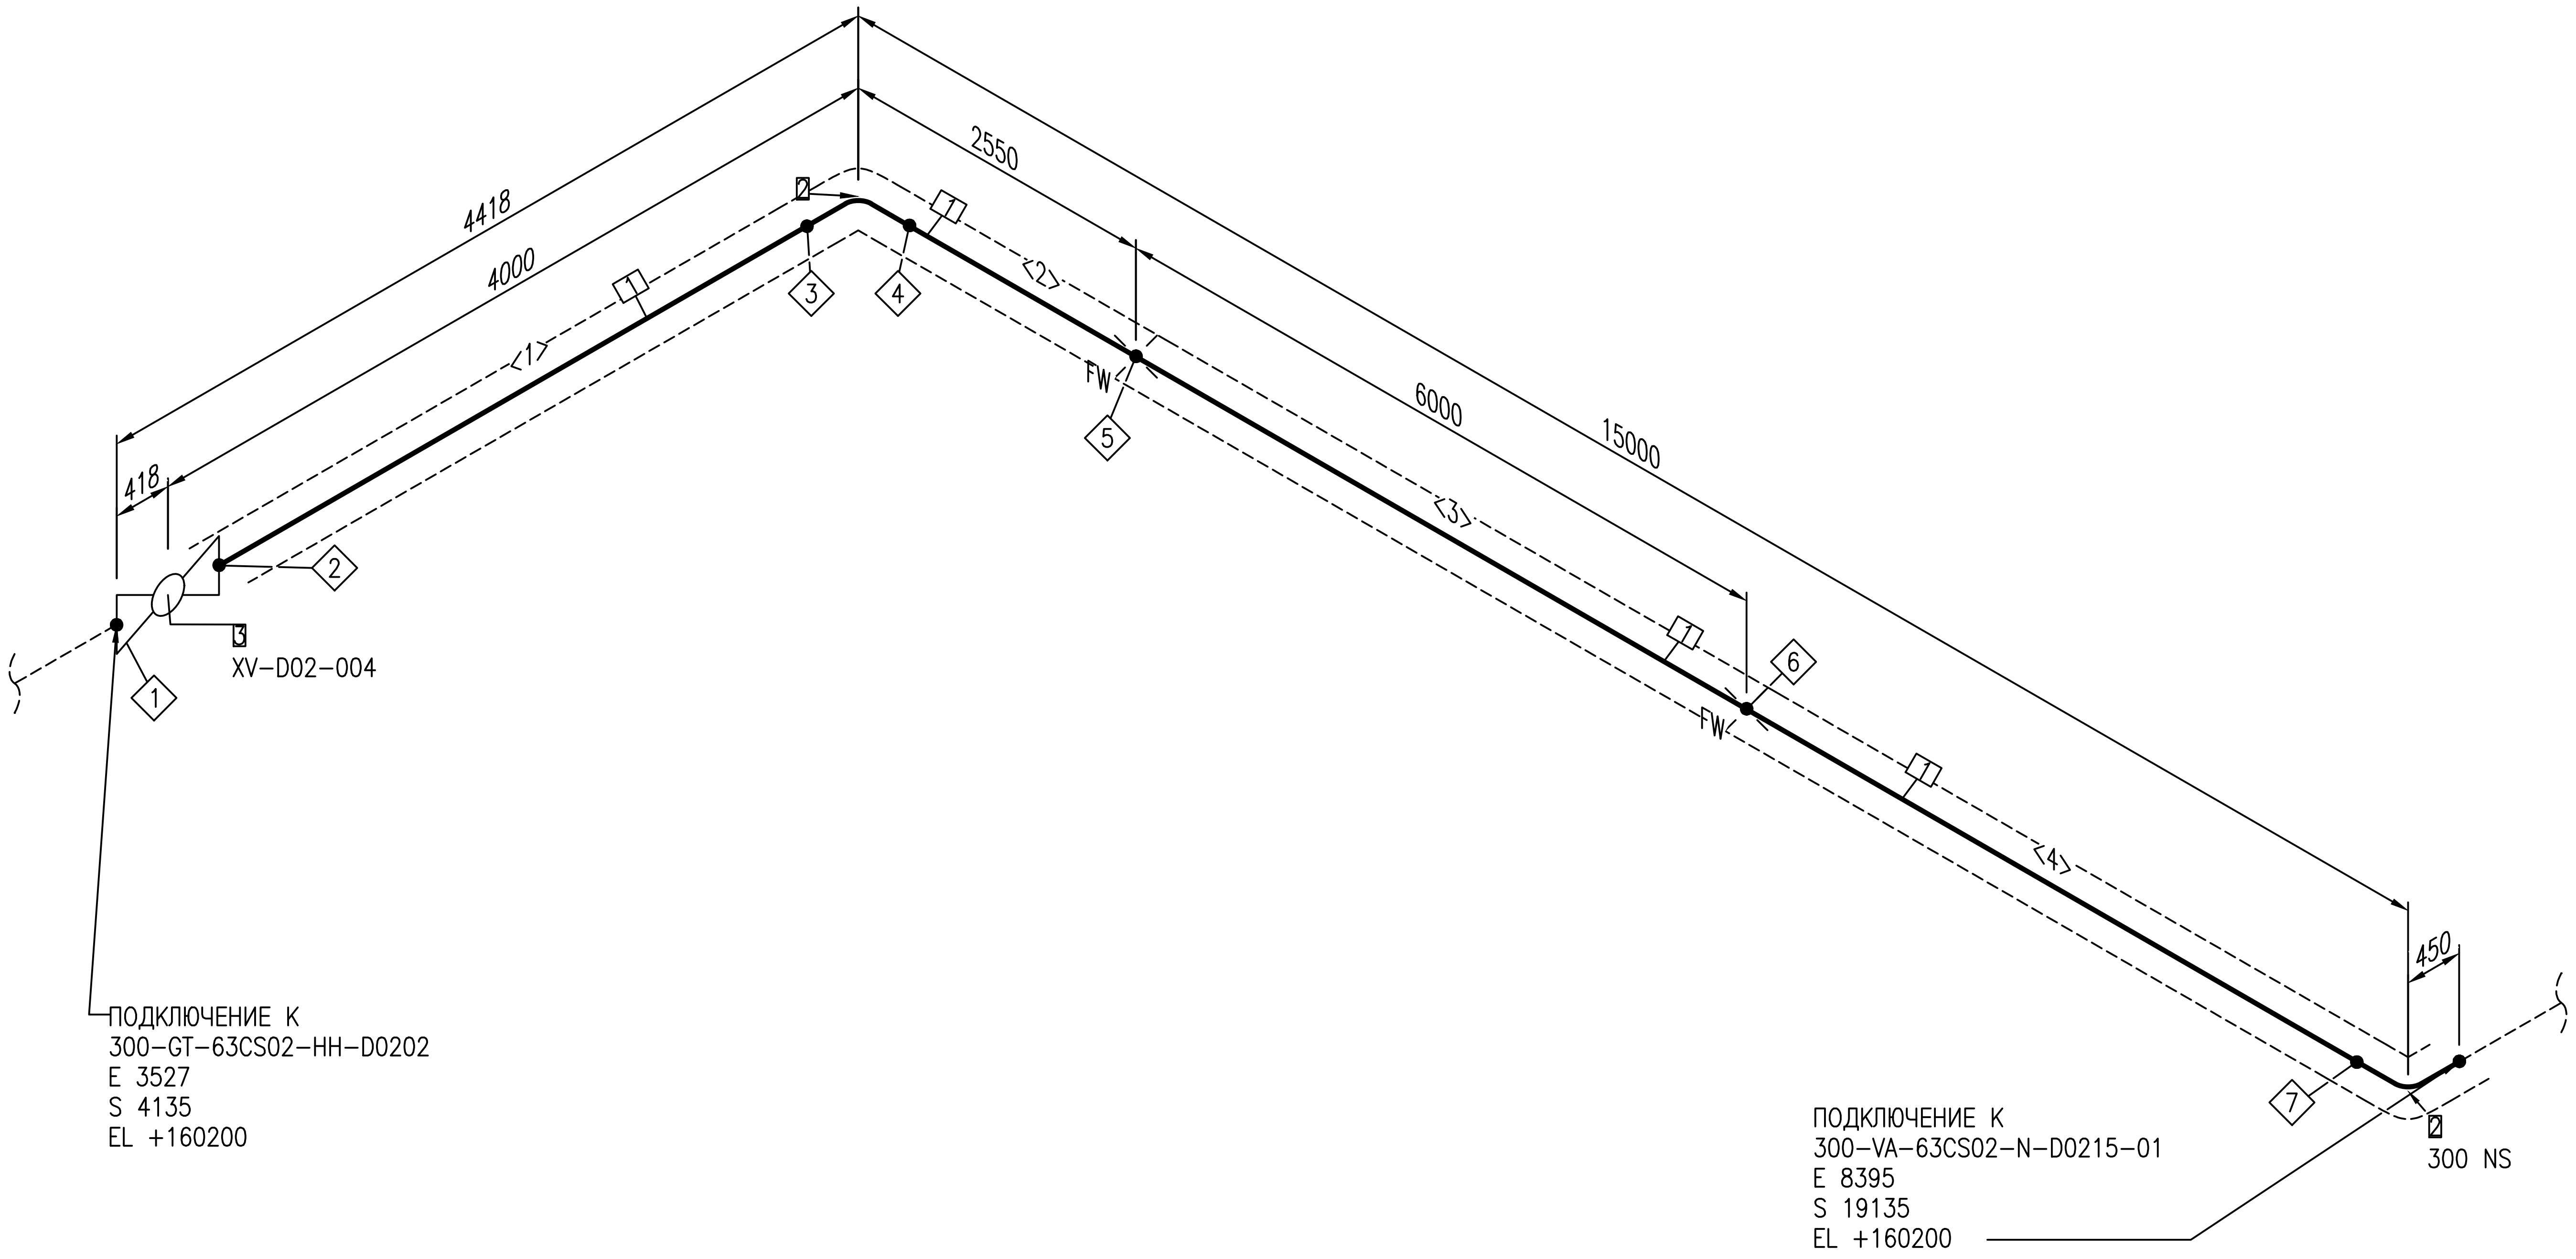ЗАКАЗЧИК: UTG UZTRANSGAZ
ГЕНЕРАЛЬНЫЙ ПОДРЯДЧИК: UET UZBEKENERGOTAMIR
ПОДРЯДЧИК: PBG Pro Build Generation
ГЕНЕРАЛЬНЫЙ ПРОЕКТИРОВЩИК: EAST WEST ENGINEERING

EWE0426-MGL1-PRE-054-ISO-710607-A1

«СТРОИТЕЛЬСТВО НОВЫХ НИТОК (УЧАСТКОВ) ГАЗОПРОВОДОВ «ГАЗЛИ - САРИМОЙ» И «АКЧАЛОК - ГАЗЛИ - НУКУС» ОБЩЕЙ ПРОТЯЖЕННОСТЬЮ НЕ МЕНЕЕ 275 КМ».

Изм.	Кол.уч.	Лист	№док.	Подпись	Дата
ГИП		Кирпичников С.			09.2026
Нач.отд.		Рябинин А.			09.2026
Исполн.		Таштимуров Р.			09.2026
Н.контр		Кирпичников С.			09.2026

ГАЗОПРОВОД «ГАЗЛИ-САРИМОЙ» (54 КМ)
Линейный крановый узел DN1200 КУП-D2

Стадия	Лист	Листов
РД	2	2

Изометрический чертеж трубопровода
300-VA-63CS02-N-D0215

EAST WEST ENGINEERING
ООО "EAST-WEST Engineering"
г. Ташкент 2026г.

Взам. инв. №
Подпись и дата
Инв.№ подл.

Формат А2 594х420