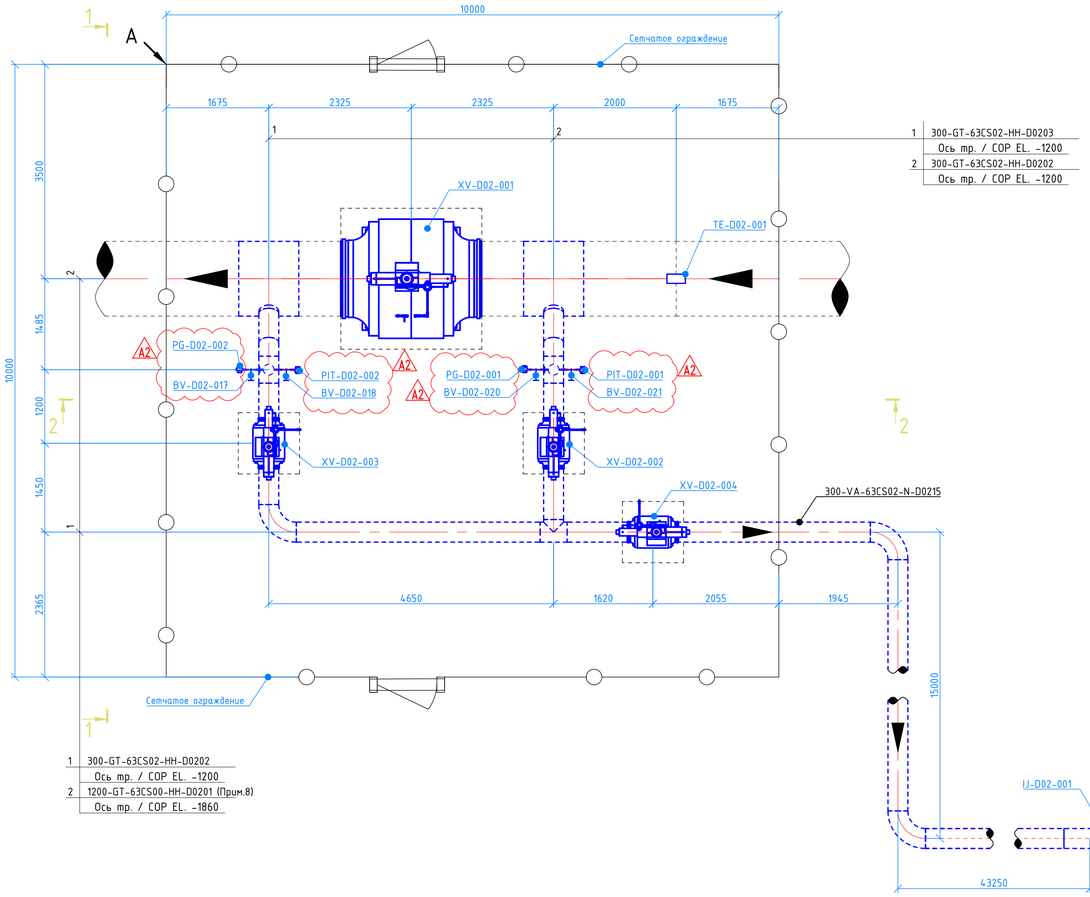
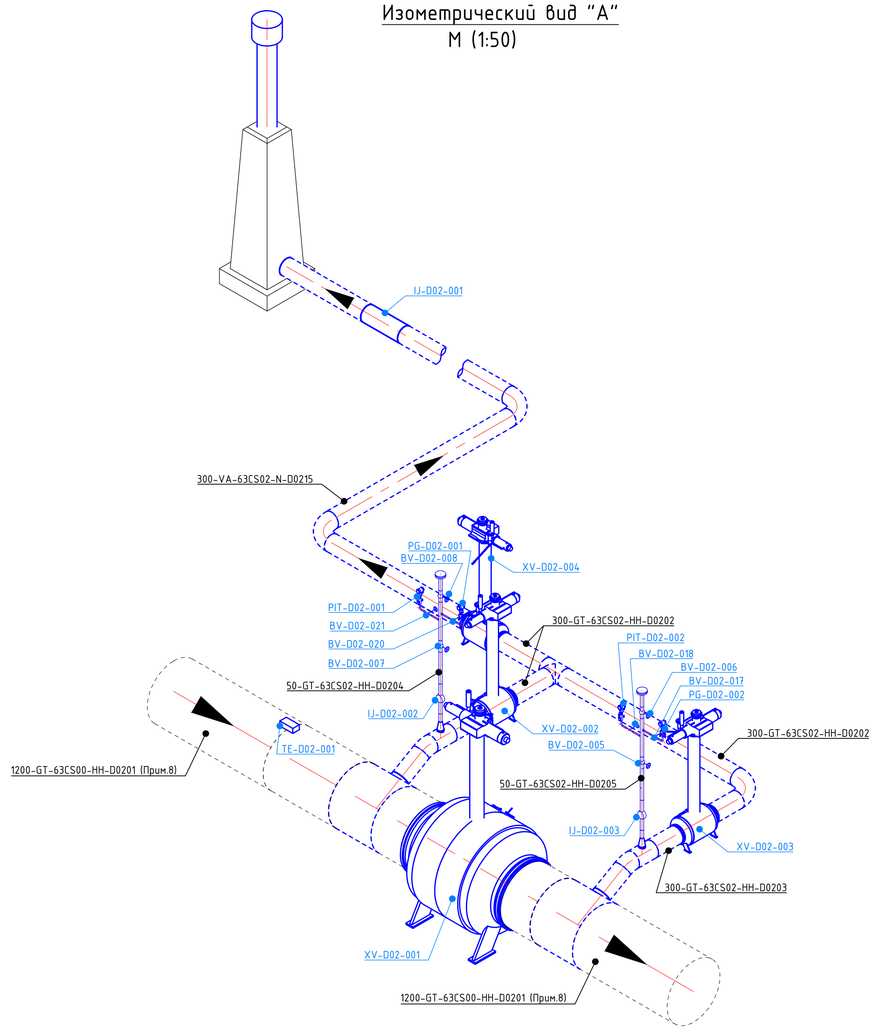
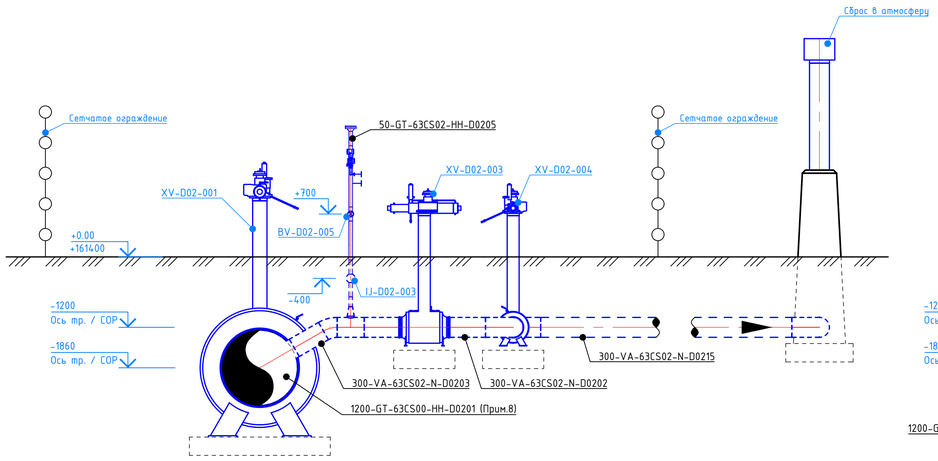
## План / Plan
М (1:50)



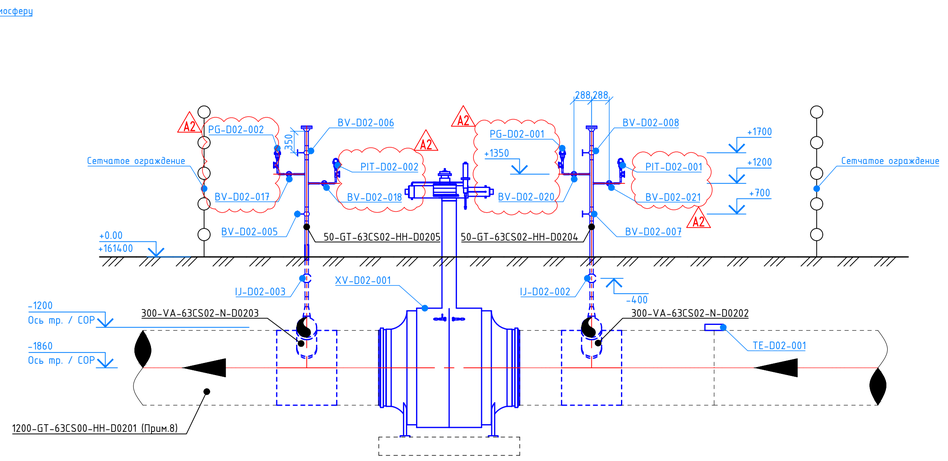

## Изометрический вид "А"
М (1:50)




## Разрез / Section 1-1
М (1:50)




## Разрез / Section 2-2
М (1:50)




## Условные обозначения:

N - нет изоляции
НН - гидроизоляция от почвенной коррозии

## ПРИМЕЧАНИЯ

1. Общие данные см. EWE0426-MGL1-PRE-054-COM-710201;
2. * - Размеры для справок;
3. ** - Размеры уточнить по месту;
4. Кран XV-D02-001 расположен на пикете ПК 0+29 проектного газопровода;
5. Размеры фитингов - по ГОСТ. Все размеры указаны в миллиметрах;
6. Высотные отметки уточнить по месту;
7. Данный чертеж составлен на основе EWE0426-MGL1-PIL-054-COM-660201;
8. Труба учтена в линейной части проекта;
9. Привязка к пикетажу указана в EWE0426-MGL1-PRE-054-PLA-710202;
10. Фундаменты под опоры, шаровой кран XV-D02-001, продувочную свечу см. EWE0426-MGL1-STR-054-COM-710501;
11. Детальную информацию по трубопроводам см. изометрические чертежи;
12. На схеме указано основное направление потока газа, согласно схеме PFD, см. EWE0426-MGL1-PRE-054-PFD-610101. В процессе эксплуатации поток может быть направлен в обратном направлении.

| Рев | Дата | Назначение ревизии | Проверил | Утвердил |
|---|---|---|---|---|
| A2 | 28.08.2026 | Утверждено для строительства | | |
| A1 | 24.07.2026 | Утверждено для строительства | | |
| R1 | 19.06.2026 | Выпущено для рассмотрения | | |

ЗАКАЗЧИК: UTG | ГЕНЕРАЛЬНЫЙ ПОДРЯДЧИК: UET | ПОДРЯДЧИК: PBG | ГЕНЕРАЛЬНЫЙ ПРОЕКТИРОВЩИК: EAST WEST ENGINEERING

EWE0426-MGL1-PRE-054-DRW-710203-A2

«СТРОИТЕЛЬСТВО НОВЫХ НИТОК (УЧАСТКОВ) ГАЗОПРОВОДОВ «ГАЗЛИ - САРИМОЙ» И «АКЧАЛОК - ГАЗЛИ - НУКУС» ОБЩЕЙ ПРОТЯЖЕННОСТЬЮ НЕ МЕНЕЕ 275 КМ».

| Изм. | Кол.уч. | Лист | № док. | Подпись | Дата |
|---|---|---|---|---|---|
| ГИП | | Схабицкий А. | | | 08.2026 |
| Нач.отд. | | Ревинин А. | | | 08.2026 |
| Испол. | | Таштимуров Р. | | | 08.2026 |
| Н.контр | | Схабицкий А. | | | 08.2026 |

ГАЗОПРОВОД «ГАЗЛИ-САРИМОЙ» (54 КМ). Линейный крановый узел DN1200 КУП-D2.

| Стадия | Лист | Листов |
|---|---|---|
| РП | 1 | 1 |

КУП-D2. План. Разрезы. Виды. М 1:50

ООО "EAST-WEST Engineering" г. Ташкент 2026г.

Взам. инв. №
Подпись и дата
Инв.№ подл.

Формат / Format A1