Линейный крановый узел КУП-D2.
План 1 (1:50)

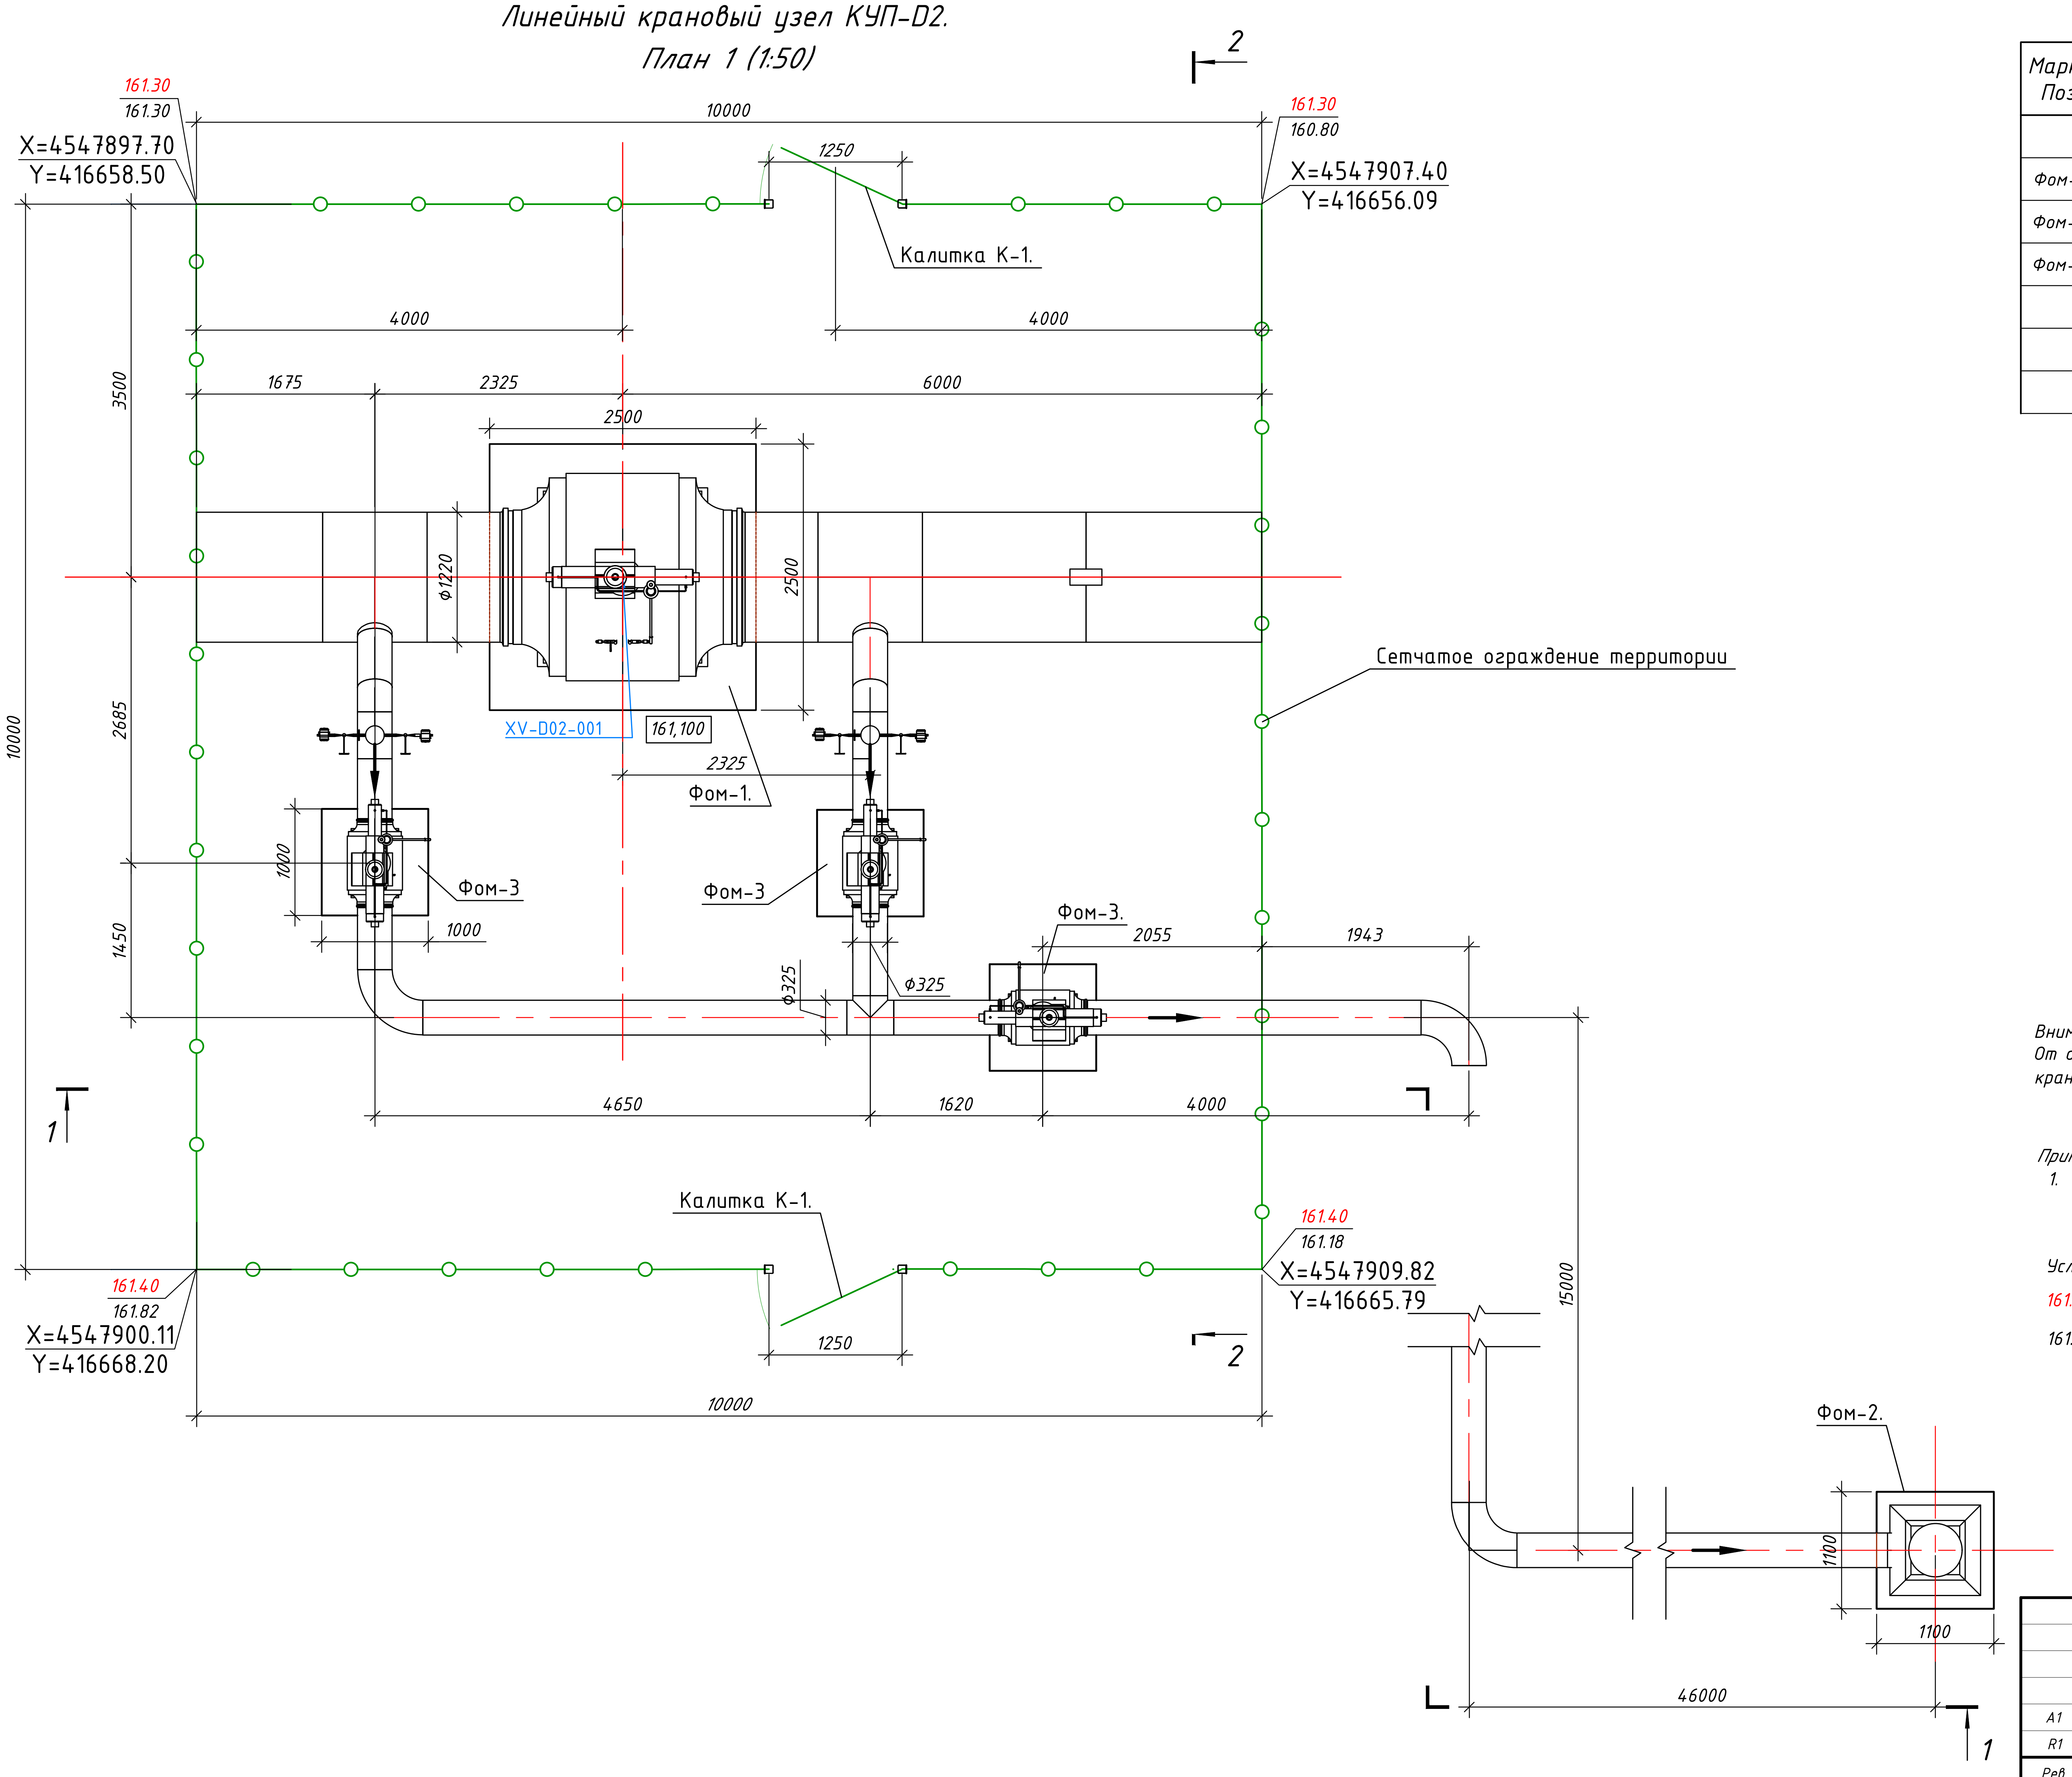

Спецификация элементов

Марка Поз.	Обозначение	Наименование	Кол. шт.	Масса ед.кг	Примеч.
		Линейный крановый узел КУП-D2.			
Фом-1	EWE0426-MGL1-STR-054-DRW-710504	Фундамент оборудования, монолитный Фом-1	1		
Фом-2	EWE0426-MGL1-STR-054-DRW-710505	Фундамент оборудования, монолитный Фом-2	1		
Фом-3	EWE0426-MGL1-STR-054-DRW-710506	Фундамент оборудования, монолитный Фом-3	3		

Внимание!
От отметки 161,10 предусмотреть насыпь до спланированных, планировочных отметок земли на территории кранового узла КУП-D2 - 161,40 и 161,30, данная насыпь учтена в части проекта Генерального плана (ГП).

Примечание:
1. Установка кранового узла КУП-D2 (Ду1200) расположена на ПК0+29 перемычки 1 с ПК0+00 по ПК0+99

Условные обозначения:

161.40 – Отметка спланированной поверхности земли

161.18 – Отметка существующей поверхности земли

Рев	Дата	Назначение ревизии	Проверил	Утвердил
A1	08.09.2026	Выпущено для строительство		
R1	20.07.2026	Выпущено для рассмотрения		

ЗАКАЗЧИК: UTG UZTRANSGAZ
ГЕНЕРАЛЬНЫЙ ПОДРЯДЧИК: UET UZBEKENERGOTAMIR
ПОДРЯДЧИК: PBG Pro Build Generation
ГЕНЕРАЛЬНЫЙ ПРОЕКТИРОВЩИК: EAST WEST ENGINEERING

EWE0426-MGL1-STR-054-DRW-710502-A1

«СТРОИТЕЛЬСТВО НОВЫХ НИТОК (УЧАСТКОВ) ГАЗОПРОВОДОВ «ГАЗЛИ - САРИМОЙ» И «АКЧАЛОК - ГАЗЛИ - НУКУС» ОБЩЕЙ ПРОТЯЖЕННОСТЬЮ НЕ МЕНЕЕ 275 КМ».

Изм.	Кол.уч.	Лист	№ док.	Подпись	Дата
ГИП		Кирпичников С.			08.09.26
Нач.отд.		Каршиев А.			08.09.26
Исполн.		Хабиров Х.			08.09.26
Н.контр		Кирпичников С.			08.09.26

ГАЗОПРОВОД "ГАЗЛИ-САРИМОЙ" (54 КМ)
Линейный крановый узел DN1200 КУП-D2

Стадия	Лист	Листов
РП	1	1

Схема расположения кранового узла КУП-D2.

EAST WEST ENGINEERING
ООО "EAST-WEST Engineering"
г. Ташкент 2026г.

Формат / Format A2

Взам. инв. №
Подпись и дата
Инв.№ подл.