
Разрез 1 – 1 м 1:25.

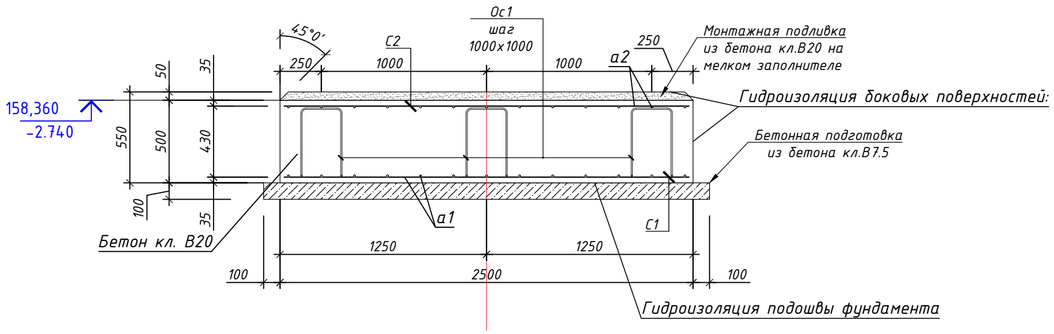

Ведомость деталей


Поз.	Эскиз
Ос1	250, 410, 410, 250, 250, L=1570

Размеры хомутов даны по центру стержня.


Спецификация элементов

Марка Поз.	Обозначение	Наименование	Кол.шт	Масса ед., кг	Прим.
		Фундамент Фом-1			
		Сборные единицы			
C1	См. данный лист	Сетка C1	1		127.18
C2	См. данный лист	Сетка C2	1		56.53
		Сетка C1			
a1	ГОСТ 34028-2016	Ф18 A500 L=2450 мм	26	4.89	127.18
		Детали			
Ос1	ГОСТ 34028-2016	Ф12 A240 L=1570 мм	13	1.39	18.11
		Сетка C2			
a2	ГОСТ 34028-2016	Ф12 A500 L=2450 мм	26	2.17	56.53
		Материалы			
	на подливку	Бетон на мелком заполнителе кл. B20, W6, F50			0.30 м³
		Бетон кл. B20, W6, F50			3.13 м³
	на подготовку	Бетон кл. B7.5			0.73 м³
		Гидроизоляция фундамента на площади:			18,55 м²

План фундамента Фом-1 м 1:50.

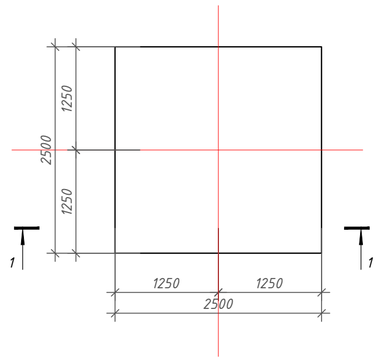

Сетка C1 м 1:50.

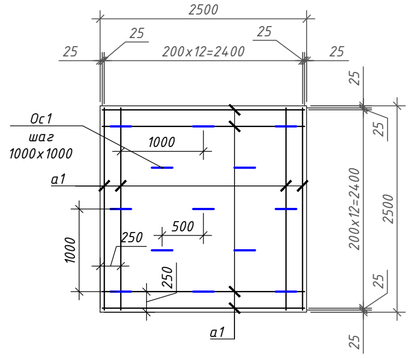

Примечания:

1. Объединение арматурных стержней в плоские сетки или пространственные каркасы выполнять вязальной стальной отожженной проволокой d=0.8-1.0мм. Применение ручной электродуговой сварки не допускается.
2. Подливку выполнить из бетона кл. B20 на мелком заполнителе.
3. Фундамент Фом-1 разработан под шаровой кран. Бетонирование выполнять после получения оборудования и сверки с паспортными данными.
4. Фиксаторы для крепления двух сеток марки Ос-1 устанавливать в шахматном порядке.
5. Расположение фундамента смотри чертёж: Схема расположения кранового узла КУП-D2.
6. Фундаментов Фом-1 изготовить в количестве – 1шт.
7. Бетон для фундамента применять на сульфатостойком портландцементе.

Гидроизоляция фундамента из двух слоев полимерного покрытия на основе лака ХП-734 в два слоя по ГОСТ 52165-2003 толщиной 25 мкм.

Ведомость расхода стали, кг

Марка элемента	Изделия арматурные					Всего	Общий расход
	Арматура класса						
	A240		A500				
	ГОСТ 34028-2016		ГОСТ 34028-2016				
	Ф12	Итого	Ф18	Ф12	Итого		
Фундамент Фом1	18.11	18.11	127.18	56.53	183.71	201.82	201.82

Рев	Дата	Назначение ревизии	Проверил	Утвердил
A1	08.09.2026	Выпущено для строительства		
R1	20.07.2026	Выпущено для рассмотрения		

ЗАКАЗЧИК: UTG UZTRANSGAZ

ГЕНЕРАЛЬНЫЙ ПОДРЯДЧИК: UET

ПОДРЯДЧИК: PBG

ГЕНЕРАЛЬНЫЙ ПРОЕКТИРОВЩИК: EAST WEST ENGINEERING

EWE0426-MGL1-STR-054-DRW-710504-A1

«СТРОИТЕЛЬСТВО НОВЫХ НИТОК (УЧАСТКОВ) ГАЗОПРОВОДОВ «ГАЗЛИ – САРИМОЙ» И «АКЧАЛОК – ГАЗЛИ – НУКУС» ОБЩЕЙ ПРОТЯЖЕННОСТЬЮ НЕ МЕНЕЕ 275 КМ».

Изм.	Кол.уч.	Лист	№ док.	Подпись	Дата
ГИП		Кирпичников С.			08.09.26
Нач.отд.		Каршиев А.			08.09.26
Исполн.		Хабиров Х.			08.09.26
Н.контр		Кирпичников С.			08.09.26

ГАЗОПРОВОД "ГАЗЛИ-САРИМОЙ" (54 КМ)
Линейный крановый узел DN1200 КУП-D2

Стадия	Лист	Листов
РП	1	1

Фундамент Фом-1.

ООО "EAST-WEST Engineering" г. Ташкент 2026г.

Взам. инв. №

Подпись и дата

Инв.№ подл.

Формат / Format A2