
Линейный крановый узел КУП-D2.

Схема расположения сетчатого ограждения (1:50).

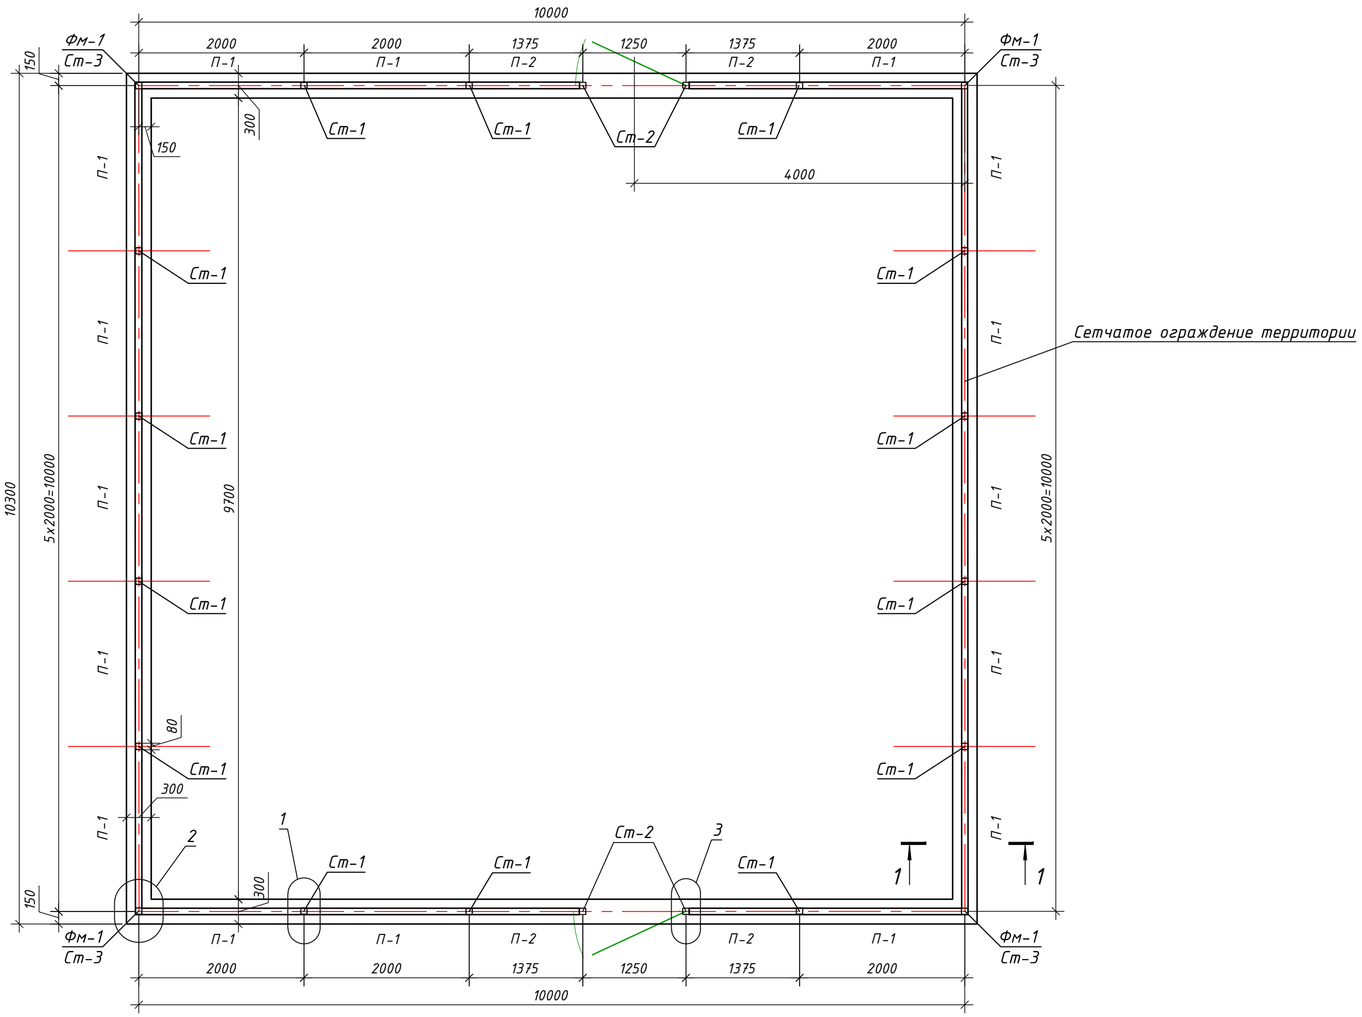


Спецификация элементов

Марка Поз.	Обозначение	Наименование	Кол. шт.	Масса ед.кг	Примеч.
		Линейный крановый узел КУП-D2.			
Фм-1	EWE0426-MGL1-STR-054-DRW-710509	Фундамент ленточный, монолитный Фм-1	1		
Ст-1	EWE0426-MGL1-STR-054-DRW-710510	Стойка ограждения Ст-1	14		
Ст-2	EWE0426-MGL1-STR-054-DRW-710511	Стойка ограждения Ст-2	4		
Ст-3	EWE0426-MGL1-STR-054-DRW-710512	Стойка ограждения Ст-3	4		
П-1	EWE0426-MGL1-STR-054-DRW-710513	Панель ограждения П-1	16		
П-2	EWE0426-MGL1-STR-054-DRW-710514	Панель ограждения П-2	4		
К-1	EWE0426-MGL1-STR-054-DRW-710515	Калитка К-1	2		
КД1	EWE0426-MGL1-STR-054-DRW-710516	Крепежная деталь КД1	24		
КД2	EWE0426-MGL1-STR-054-DRW-710516	Крепежная деталь КД2	28		


Примечания:

1. Данный чертёж читать совместно с ленточным фундаментом Фм-1.
2. Изготовить общее количество узлов:
   - узел 1 - 14 шт.
   - узел 2 - 4шт.
   - узел 3 - 4шт.


Узел 1

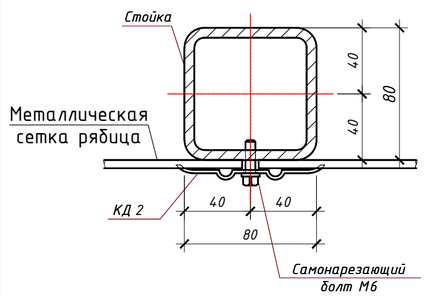

Узел 2

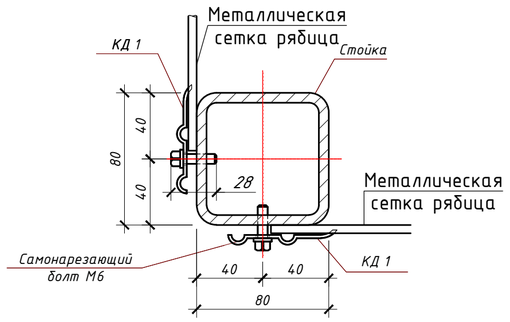

Узел 3

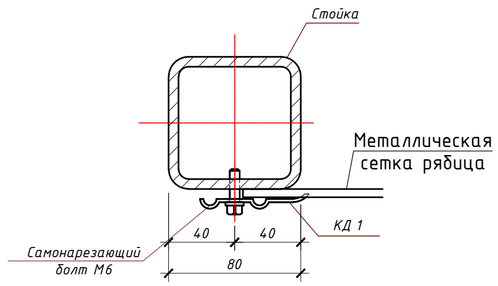

A1	08.09.2026	Выпущено для строительства		
R1	20.07.2026	Выпущено для рассмотрения		
Рев	Дата	Назначение ревизии	Проверил	Утвердил

ЗАКАЗЧИК: UTG ГЕНЕРАЛЬНЫЙ ПОДРЯДЧИК: UET ПОДРЯДЧИК: PBG ГЕНЕРАЛЬНЫЙ ПРОЕКТИРОВЩИК: EAST WEST ENGINEERING

Изм.	Кол.уч.	Лист	№ док.	Подпись	Дата	EWE0426-MGL1-STR-054-DRW-710507-A1			
						«СТРОИТЕЛЬСТВО НОВЫХ НИТОК (УЧАСТКОВ) ГАЗОПРОВОДОВ «ГАЗЛИ - САРИМОЙ» И «АКЧАЛОК - ГАЗЛИ - НУКУС» ОБЩЕЙ ПРОТЯЖЕННОСТЬЮ НЕ МЕНЕЕ 275 КМ».			
ГИП		Кирпичников С.			08.09.26	ГАЗОПРОВОД "ГАЗЛИ-САРИМОЙ" (54 КМ) Линейный крановый узел DN1200 КУП-D2	Стадия	Лист	Листов
Нач.отд.		Каршиев А.			08.09.26		РП	1	1
Исполн.		Хабиров Х.			08.09.26	Схема расположения сетчатого ограждения.	EAST WEST ENGINEERING	ООО "EAST-WEST Engineering" г. Ташкент 2026г.	
Н.контр		Кирпичников С.			08.09.26				

Взам. инв. № | Подпись и дата | Инв.№ подл.

Формат / Format A2