Вид м 1:20 (опалубочный)

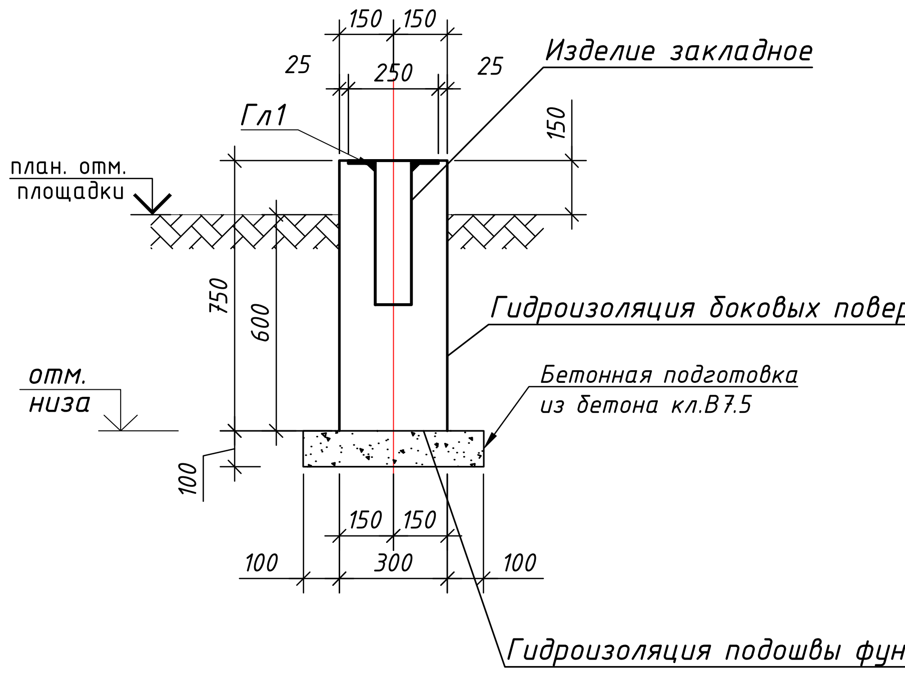

Разрез 1-1 м 1:20. (армирование)

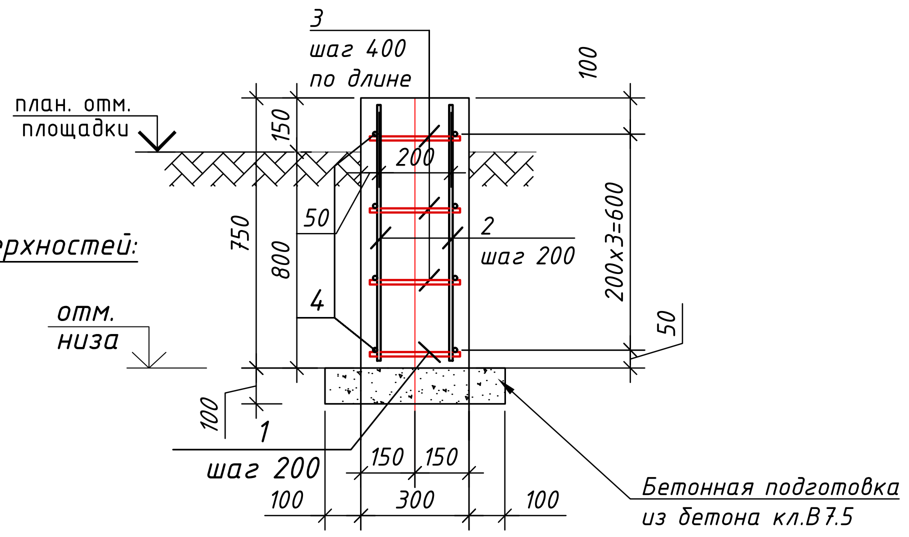

Ведомость деталей

Поз.	Эскиз
3	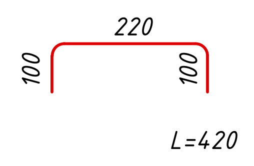

Спецификация элементов

Марка Поз.	Обозначение	Наименование	Кол.шт	Масса ед., кг	Прим.
		Фундамент Фм-1			
		Сборные единицы			
Гл-1		Гильза Гл-1	22	9.014	198.308
		Детали			
1	ГОСТ 34028-2016	Ф12 А500 L=250 мм	192	0.22	42.59
2	ГОСТ 34028-2016	Ф12 А500 L=710 мм	384	0.63	241.93
3	ГОСТ 34028-2016	Ф8 А240 L=420 мм	288	0.17	47.70
4	ГОСТ 34028-2016	Ф8 А240 L=10260 мм	32	4.05	129.48
		Гильза Гл-1			на 1 шт.
5	ГОСТ 30245-2003	Профиль 100х100х4, L=396	1	4,77	4.770
6	ГОСТ 19903-90*	Лист 4х100х100	1	0,314	0.314
7	ГОСТ 19903-90*	Лист 8х250х250	1	3,93	3.930
		Материалы			
		Бетон кл. В15, W6, F50			8.91 м³
	на подготовку	Бетон кл. В7.5			2.00 м³
		Гидроизоляция фундамента на площади:			44,72 м²

Гильза Гл-1 м 1:10.

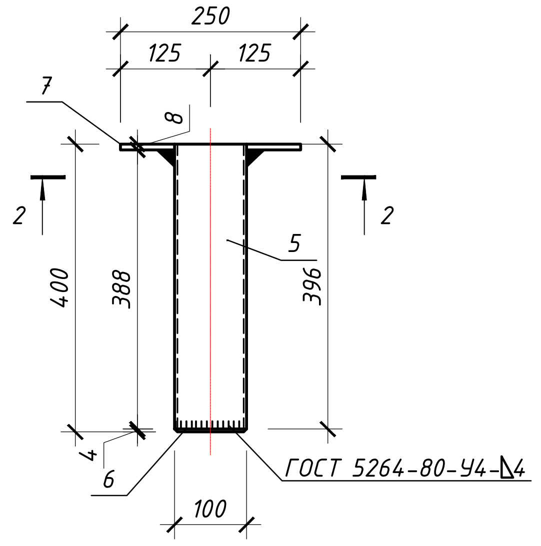

Разрез 2-2 м 1:10.

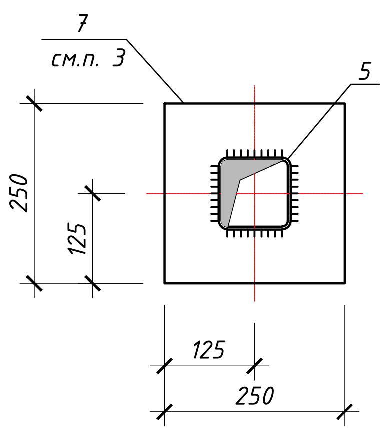

Примечания:
1. Данный чертёж читать совместно со схемой расположения сетчатого ограждения.
2. Объединение арматурных стержней в плоские сетки или пространственные каркасы выполнять вязальной стальной отожженной проволокой d=0.8-1.0мм. Применение ручной электродуговой сварки не допускается.
3. Поз.7 предназначена для крепления стойки ограждения на сварке.

Гидроизоляция фундамента из двух слоев полимерного покрытия на основе лака ХП-734 в два слоя по ГОСТ 52165-2003 толщиной 25 мкм.

Ведомость расхода стали, кг

Марка элемента	Изделия арматурные					Изделия закладные						Общий расход
	Арматура класса				Всего	Прокат стали					Всего	
	А240		А500			С245						
	ГОСТ 34028-2016		ГОСТ 34028-2016			ГОСТ 19903-90*			ГОСТ 30245-2003			
	Ф8	Итого	Ф12	Итого		t=4	t=8	Итого	□ 100х100х4	Итого		
Фундамент Фм-1	177,18	177,18	284,52	284,52	461,70	6,91	86.46	93,37	104.94	104.94	198,31	660,01

Рев	Дата	Назначение ревизии	Проверил	Утвердил
А1	08.09.2026	Выпущено для строительство		
R1	20.07.2026	Выпущено для рассмотрения		

ЗАКАЗЧИК: UTG UZTRANSGAZ
ГЕНЕРАЛЬНЫЙ ПОДРЯДЧИК: UET UZBEKENERGOTAMIR
ПОДРЯДЧИК: PBG Pro Build Generation
ГЕНЕРАЛЬНЫЙ ПРОЕКТИРОВЩИК: EAST WEST ENGINEERING

EWE0426-MGL1-STR-054-DRW-710509-A1

«СТРОИТЕЛЬСТВО НОВЫХ НИТОК (УЧАСТКОВ) ГАЗОПРОВОДОВ «ГАЗЛИ - САРИМОЙ» И «АКЧАЛОК - ГАЗЛИ - НУКУС» ОБЩЕЙ ПРОТЯЖЕННОСТЬЮ НЕ МЕНЕЕ 275 КМ».

Изм.	Кол.уч.	Лист	№ док.	Подпись	Дата
ГИП		Кирпичников С.			08.09.26
Нач.отд.		Каршиев А.			08.09.26
Исполн.		Хабиров Х.			08.09.26
Н.контр		Кирпичников С.			08.09.26

ГАЗОПРОВОД "ГАЗЛИ-САРИМОЙ" (54 КМ)
Линейный крановый узел DN1200 КУП-D2

Стадия	Лист	Листов
РП	1	1

Ленточный фундамент Фм-1.

EAST WEST ENGINEERING
ООО "EAST-WEST Engineering"
г. Ташкент 2026г.

Взам. инв. №
Подпись и дата
Инв.№ подл.

Формат / Format A2