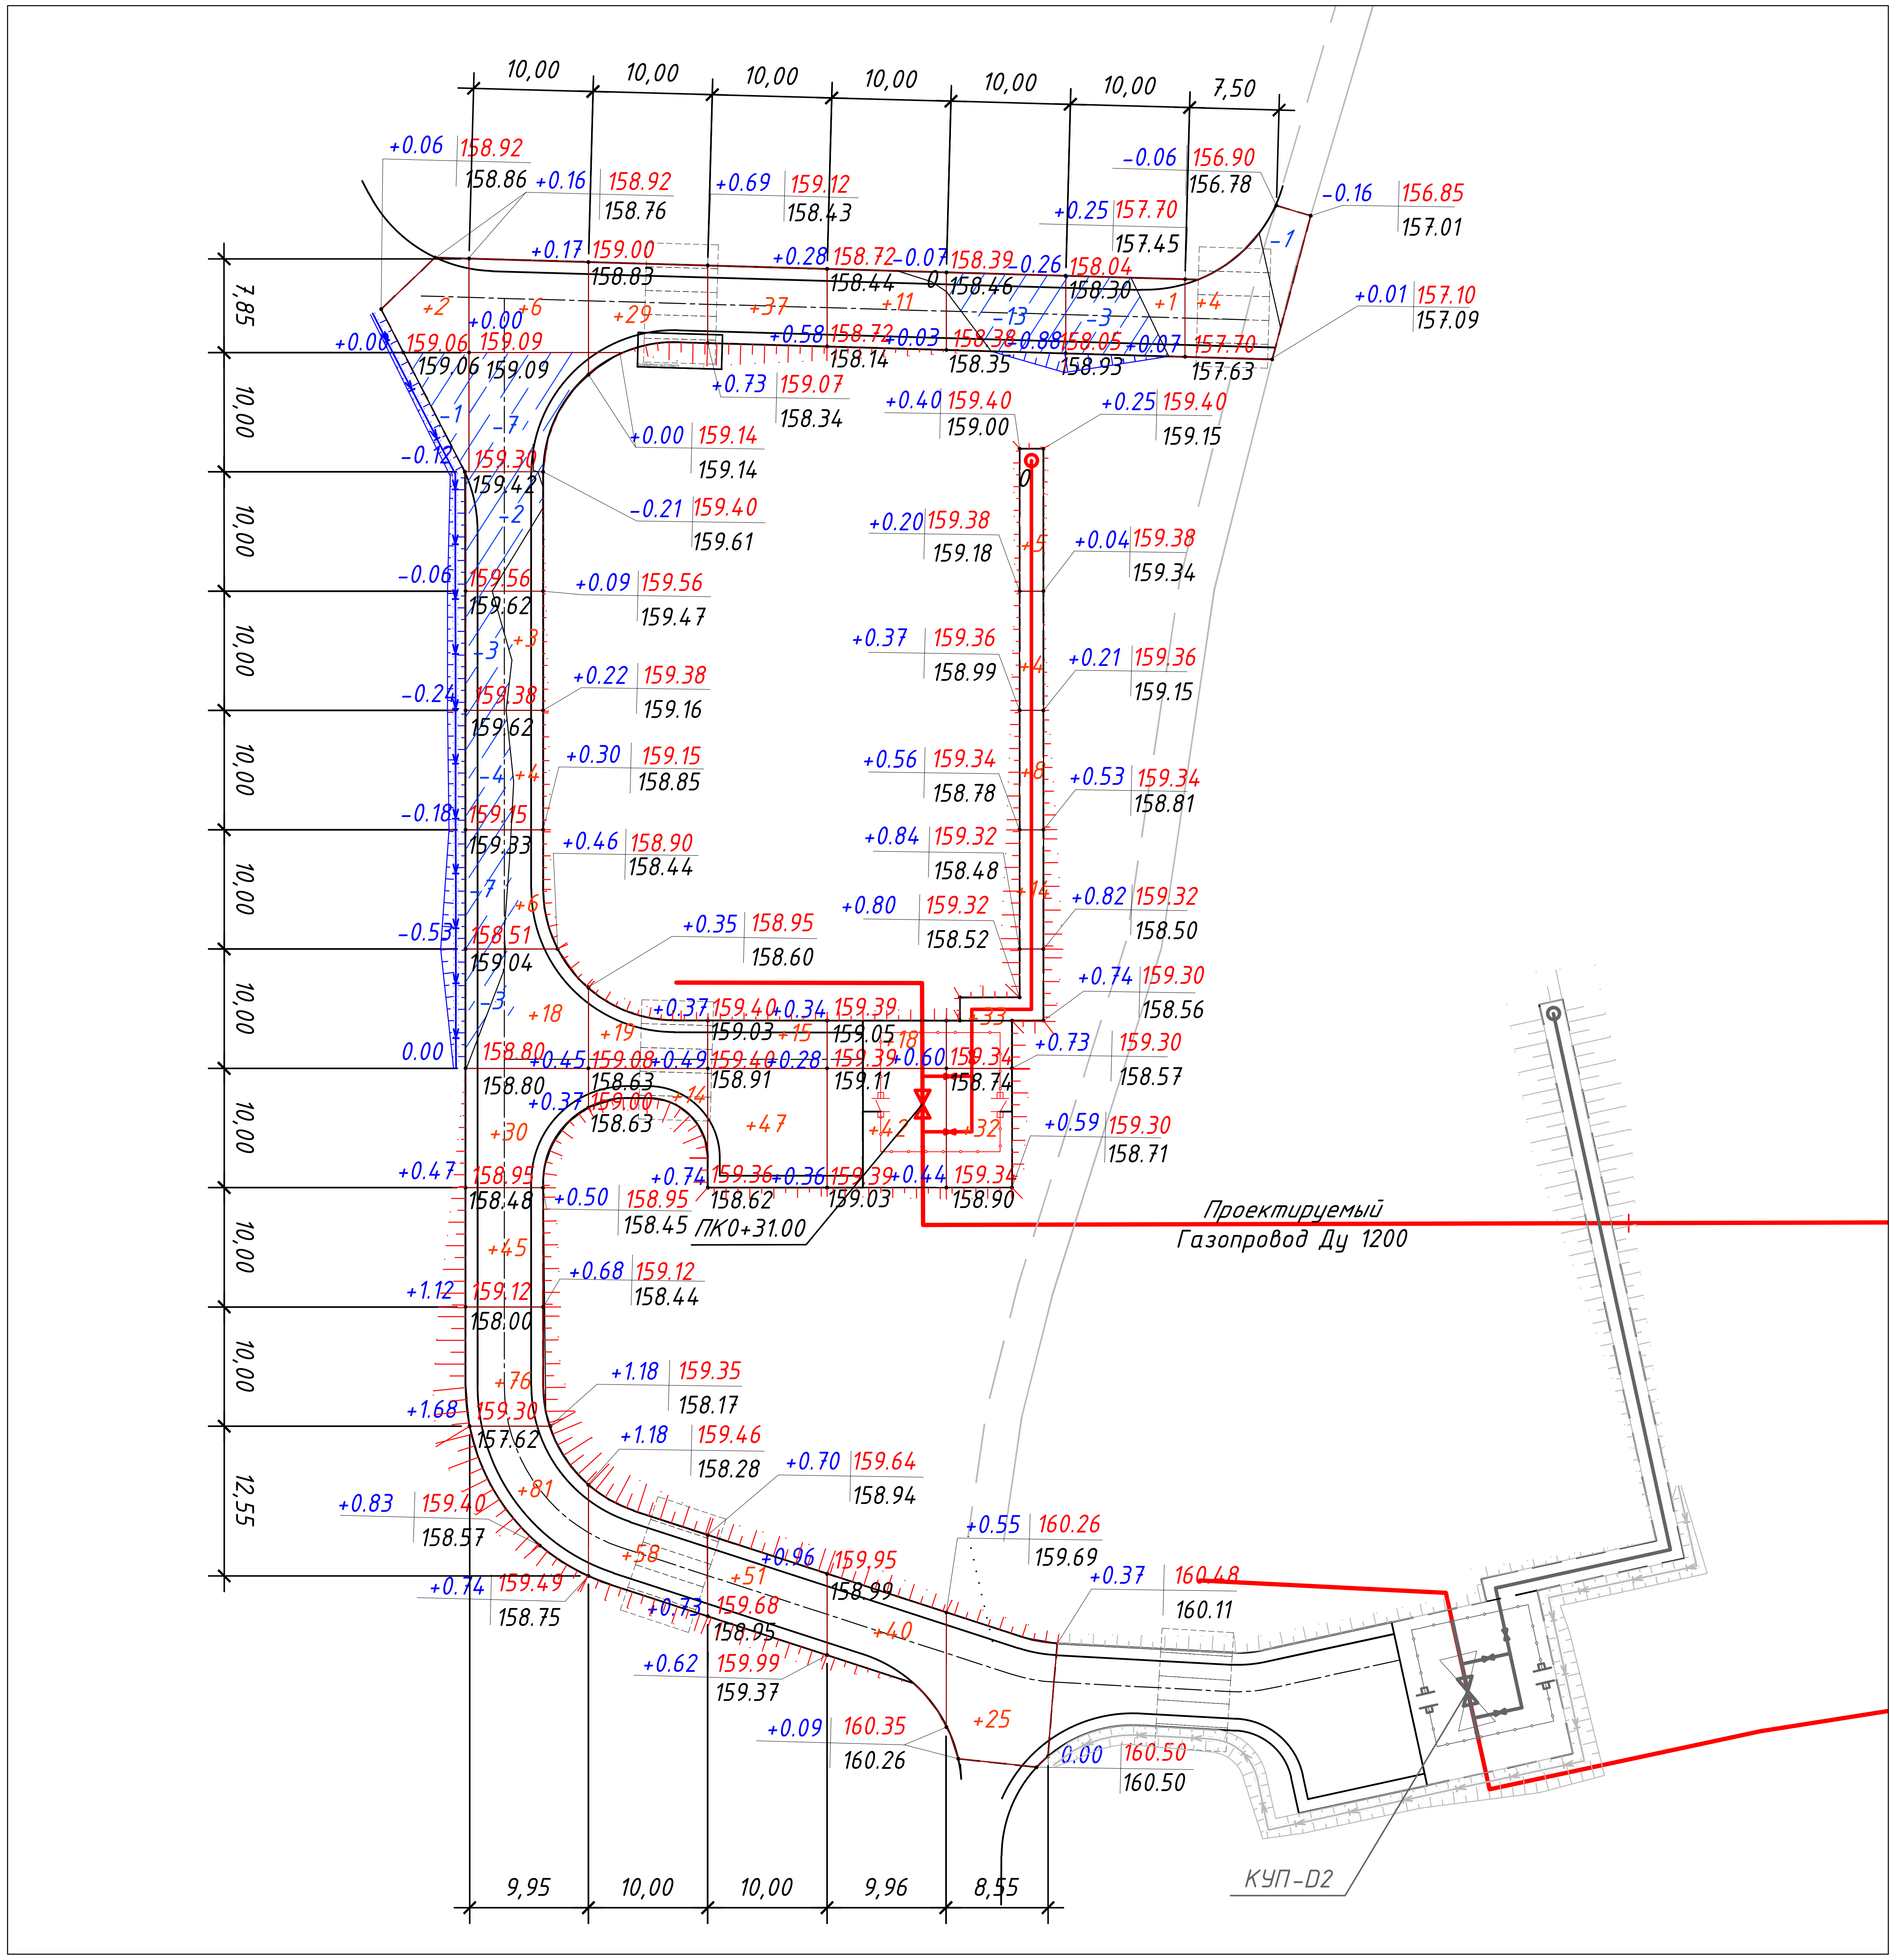

Итого, м³									Всего м³	
	Насыпь (+)	+2	+269	+120	+150	+111	+121	+1	+4		+778
	Выемка (-)	-1	-26	--	--	--	-13	-3	-1		-44

Ведомость объемов земляных масс

Наименование грунта	Количество, м³		Примечание
	Насыпь (+)	Выемка (-)	
1. Грунт планировки территории	778	44	
2. Вытесненный грунт, в т.ч. при устройстве:			
а) автодорожных покрытий		559	
б) покрытий площадок		13	
в) водоотводной канавы		26	
г) плодородной почвы на участках насыпи			
д) плодородной почвы на участках выемки			
3. Замена растительного грунта на участках насыпи			
4. Грунт для устройства откосов насыпи	88		
5. Грунт для устройства откосов выемки		2	
6. Поправка на уплотнение	86.6		
Всего пригодного грунта	952.6	644	
5. Недостаток пригодного грунта		308.6**	
8. Плодородный грунт, всего в т.ч.:		645	
а) Используемый для озеленения территории			
б) Избыток плодородного грунта	645		
(рекультивация земель)			
9. Итого перерабатываемого грунта	1597.6	1597.6	

* С учетом плодородного грунта.
** В карьере.
Общая площадь картограммы = 2150 м2

Условные обозначения:

+10	объем насыпи в м³
-3	объем выемки в м³
+0.59 | 159.34 / 158.71	рабочая отм. | проектная отм. / отм.сущ.рельефа
┬┬┬┬┬┬	откосы насыпи
┴┴┴┴┴┴	откосы выемки

Примечание:

При составлении настоящего чертежа были использованы :
1. Сетка картограммы привязана линейно к пикету ПК 0+31.00.
2. Сетка квадратов объёмы земляных масс разбита на ячейки размерами 10x10м.
3. Производство земляных работ вести в соответствии с требованиями ҚР 02.01.
4. План земляных масс кранового узла КУП-D2 см. EWE0426-MGL1-GLT-054-DRW-710104.

Рев.	Дата	Назначение ревизии	Проверил	Утвердил
A2	25.09.2026	Выпущено для строительства		
A1	20.08.2026	Выпущено для строительства		
R1	14.07.2026	Выпущено для рассмотрения		

ЗАКАЗЧИК: UTG UZTRANSGAZ
ГЕНЕРАЛЬНЫЙ ПОДРЯДЧИК: UET UZBEKENERGOTAMIR
ПОДРЯДЧИК: PBG Pro Build Generation
ГЕНЕРАЛЬНЫЙ ПРОЕКТИРОВЩИК: EAST WEST ENGINEERING

EWE0426-MGL1-GLT-054-DRW-700104-A2

«СТРОИТЕЛЬСТВО НОВЫХ НИТОК (УЧАСТКОВ) ГАЗОПРОВОДОВ «ГАЗЛИ - САРИМОЙ» И «АКЧАЛОК - ГАЗЛИ - НУКУС» ОБЩЕЙ ПРОТЯЖЕННОСТЬЮ НЕ МЕНЕЕ 275 км».

Изм.	Кол.уч.	Лист	№ док.	Подпись	Дата
ГИП		Схабицкий А.			09.2026
Нач.отд.		Нигманова Н.			09.2026
Исполн.		Нигманова Н.			09.2026
Н.контр		Схабицкий А.			09.2026

ГАЗОПРОВОД «ГАЗЛИ-САРИМОЙ» (54 км)
Генеральный план и транспорт.

Стадия	Лист	Листов
РД	1	1

КУП_D1.
План земляных масс М 1:500

ООО "EAST-WEST Engineering"
г. Ташкент 2026г.

Взам. инв. №
Подпись и дата
Инв.№ подл.

Формат / Format A2