Инв. N подл.
Подпись и дата
Взам. инв. N

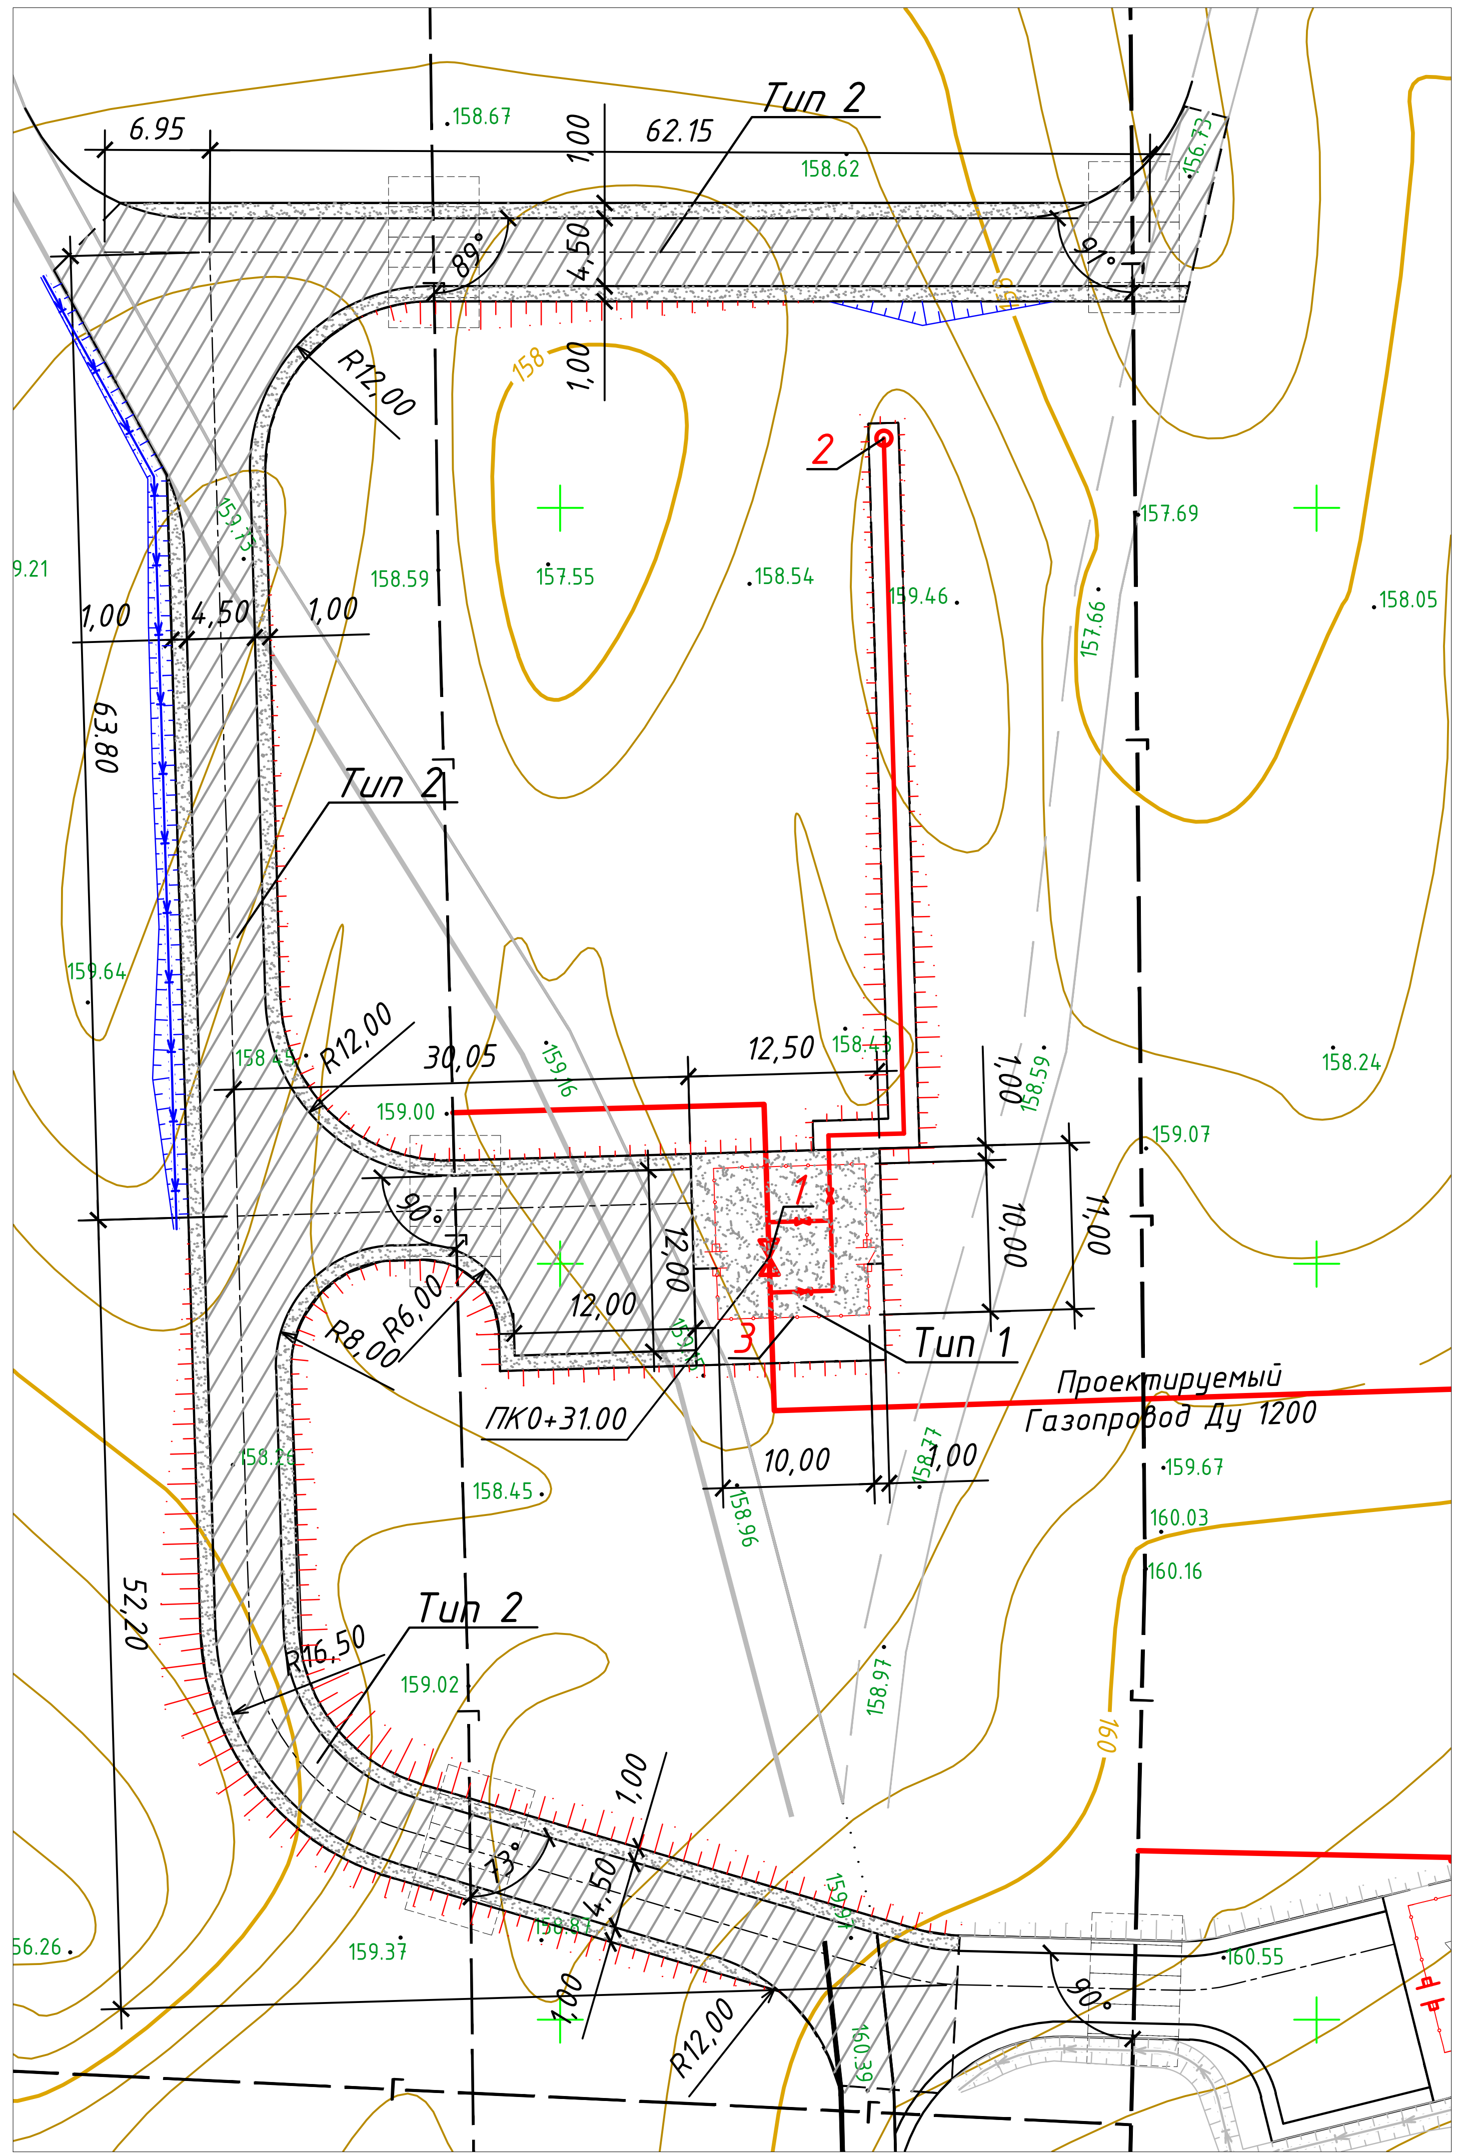

Спецификация элемента пересечения дороги с газопроводом (Спецификация на 1 элемент)

Поз.	Обозначение	Наименование	Кол. шт.	Масса ед., кг	Примечание
1	Серия 3.503.1-91	Плита дорожная ПДН-6х2	5	шт	
2	ГОСТ Р 50970-2011	Столбик сигнальный типа С1	8	шт	
3		Предупреждающий знак	2	шт	

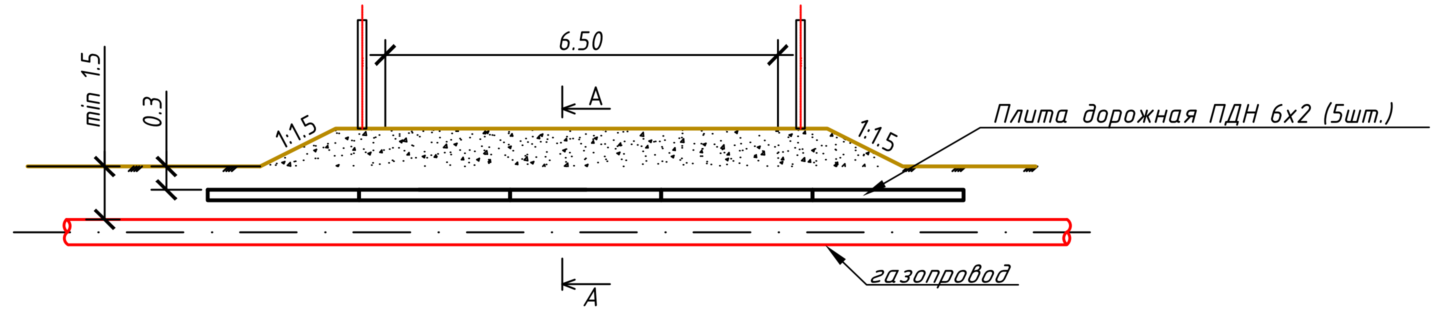

A - A

Пересечение газопроводом автомобильной дороги

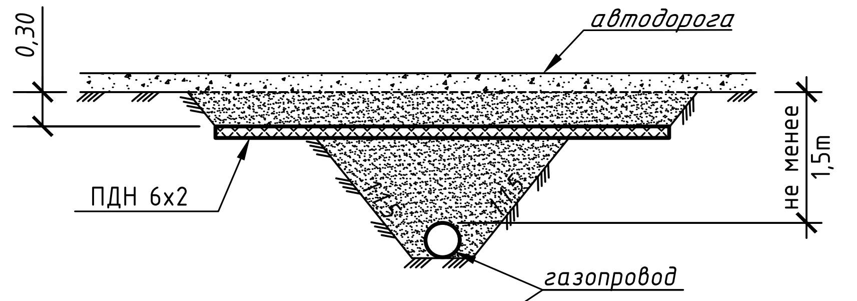

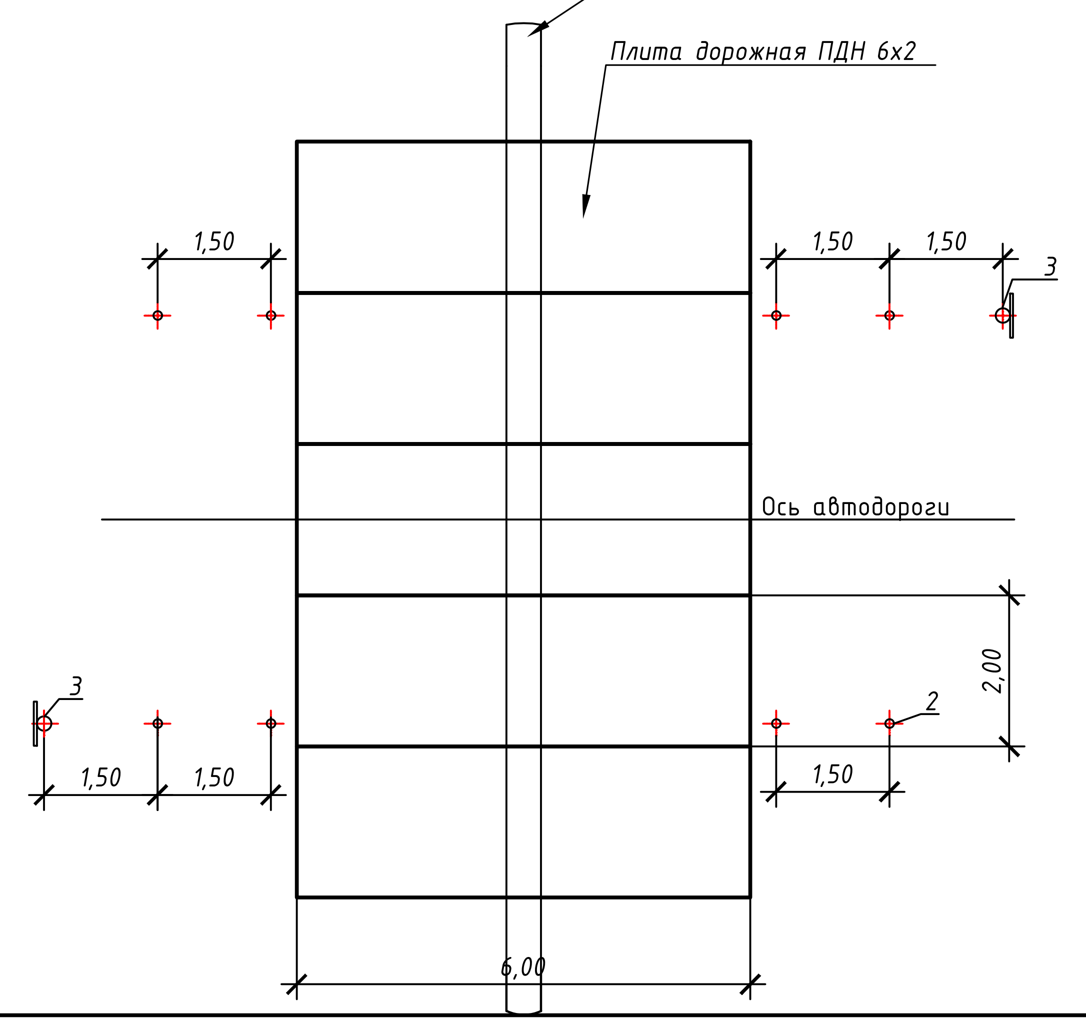

Тип 2

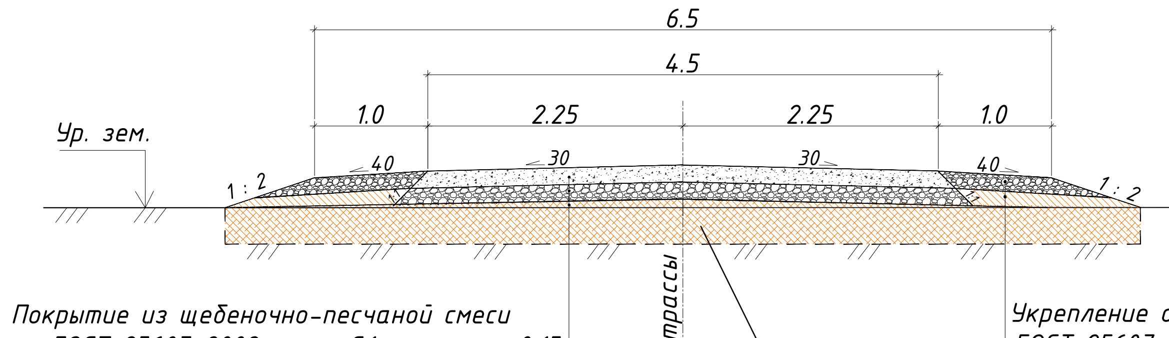

Покрытие из щебеночно-песчаной смеси по ГОСТ 25607-2009 смесь С1 - 0.15

Основание из гравийно-песчаной смеси по ГОСТ 25607-2009 смесь С3 - 0.15

Грунт земляного полотна

Укрепление обочин из ГПС ГОСТ 25607-2009 смесь С4 - 0.15

Присыпная обочина из связного грунта - 0.15

Снятие растительного слоя (h=0.30)

Тип 1

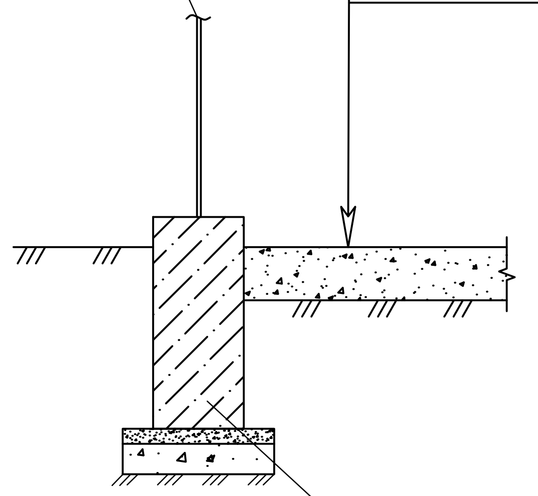

Сетчатое ограждение типа "Махаон" см. раздел STR

1 Щебень фр. 25мм по ГОСТ 8267-93 h=0.10м

2 Уплотненный грунт

Столбчатый фундамент под ограждение см. раздел STR

Примечание:

При составлении настоящего чертежа были использованы :
1. Материалы топографо-геодезической съемки, предоставлены АО "O'ZLITINEFTGAZ".
2. Система координат местная. Высотные отметки даны в Балтийской системе.
3. Размеры даны в метрах.
4. Площадка кранового узла привязана линейно к пикету ПК 0+31.00.
5. Данный лист смотри совместно с листами PIL, PRE, ELE, STR, SYS.
6. Детальный план кранового узла см. EWE0426-MGL1-PRE-054-DRW-700203.

Экспликация зданий и сооружений

Номер на плане	Наименование	Примечание
1	Крановый узел Ду 1200	
2	Продувочная свеча	
3	Проектируемое сетчатое ограждение	

Ведомость тротуаров, дорожек и площадок

Тип	Обозначение	Наименование	Ед. изм.	Примечание
		Покрытие площадки		
1	░	Покрытие из щебня по ГОСТ 8267-93, h=0.10	м²	130
		Покрытие проездов		
2	▨	Покрытие из щебеночно-песчаной смеси по ГОСТ 25607-2009 смесь С1 h=0,15м Основание из гравийно-песчаной смеси по ГОСТ 25607-2009 смесь С3 h=0,15м	м²	1440.0
		Укрепление обочин из ГПС ГОСТ 25607-2009 смесь С4 h=0,15м	м²	425.0

Рев.	Дата	Назначение ревизии	Проверил	Утвердил
A2	25.09.2026	Выпущено для строительства		
A1	20.08.2026	Выпущено для строительства		
R1	10.07.2026	Выпущено для рассмотрения		

ЗАКАЗЧИК: UTG UZTRANSGAZ
ГЕНЕРАЛЬНЫЙ ПОДРЯДЧИК: UET UZBEKENERGOTAMIR
ПОДРЯДЧИК: PBG Pro Build Generation
ГЕНЕРАЛЬНЫЙ ПРОЕКТИРОВЩИК: EAST WEST ENGINEERING

EWE0426-MGL1-GLT-054-DRW-700106-A2

«СТРОИТЕЛЬСТВО НОВЫХ НИТОК (УЧАСТКОВ) ГАЗОПРОВОДОВ «ГАЗЛИ - САРИМОЙ» И «АКЧАЛОК - ГАЗЛИ - НУКУС» ОБЩЕЙ ПРОТЯЖЕННОСТЬЮ НЕ МЕНЕЕ 275 км».

Изм.	Кол.уч.	Лист	№ док.	Подпись	Дата
ГИП		Схабицкий А.			09.2026
Нач.отд.		Нигманова Н.			09.2026
Исполн.		Нигманова Н.			09.2026
Н.контр		Схабицкий А.			09.2026

ГАЗОПРОВОД «ГАЗЛИ-САРИМОЙ» (54 км)
Генеральный план и транспорт.

Стадия	Лист	Листов
РД	1	1

КУП_D1.
План благоустройства территории
М 1:500

EAST WEST ENGINEERING
ООО "EAST-WEST Engineering"
г. Ташкент 2026 г.

Формат / Format A4x4