
ПЕРЕЧЕНЬ СВАРНЫХ ШВОВ		
№	DN	ТИП
1	300	BUTTWELD
2	300	BUTTWELD
3	300	BUTTWELD
4	300	BUTTWELD
5	300	BUTTWELD
6	300	FIELDWELD
7	300	FIELDWELD
8	300	FIELDWELD
9	300	FIELDWELD
10	300	FIELDWELD
11	300	FIELDWELD
12	300	FIELDWELD
13	300	BUTTWELD
14	300	BUTTWELD
15	300	BUTTWELD
16	300	BUTTWELD
17	300	BUTTWELD
18	300	BUTTWELD

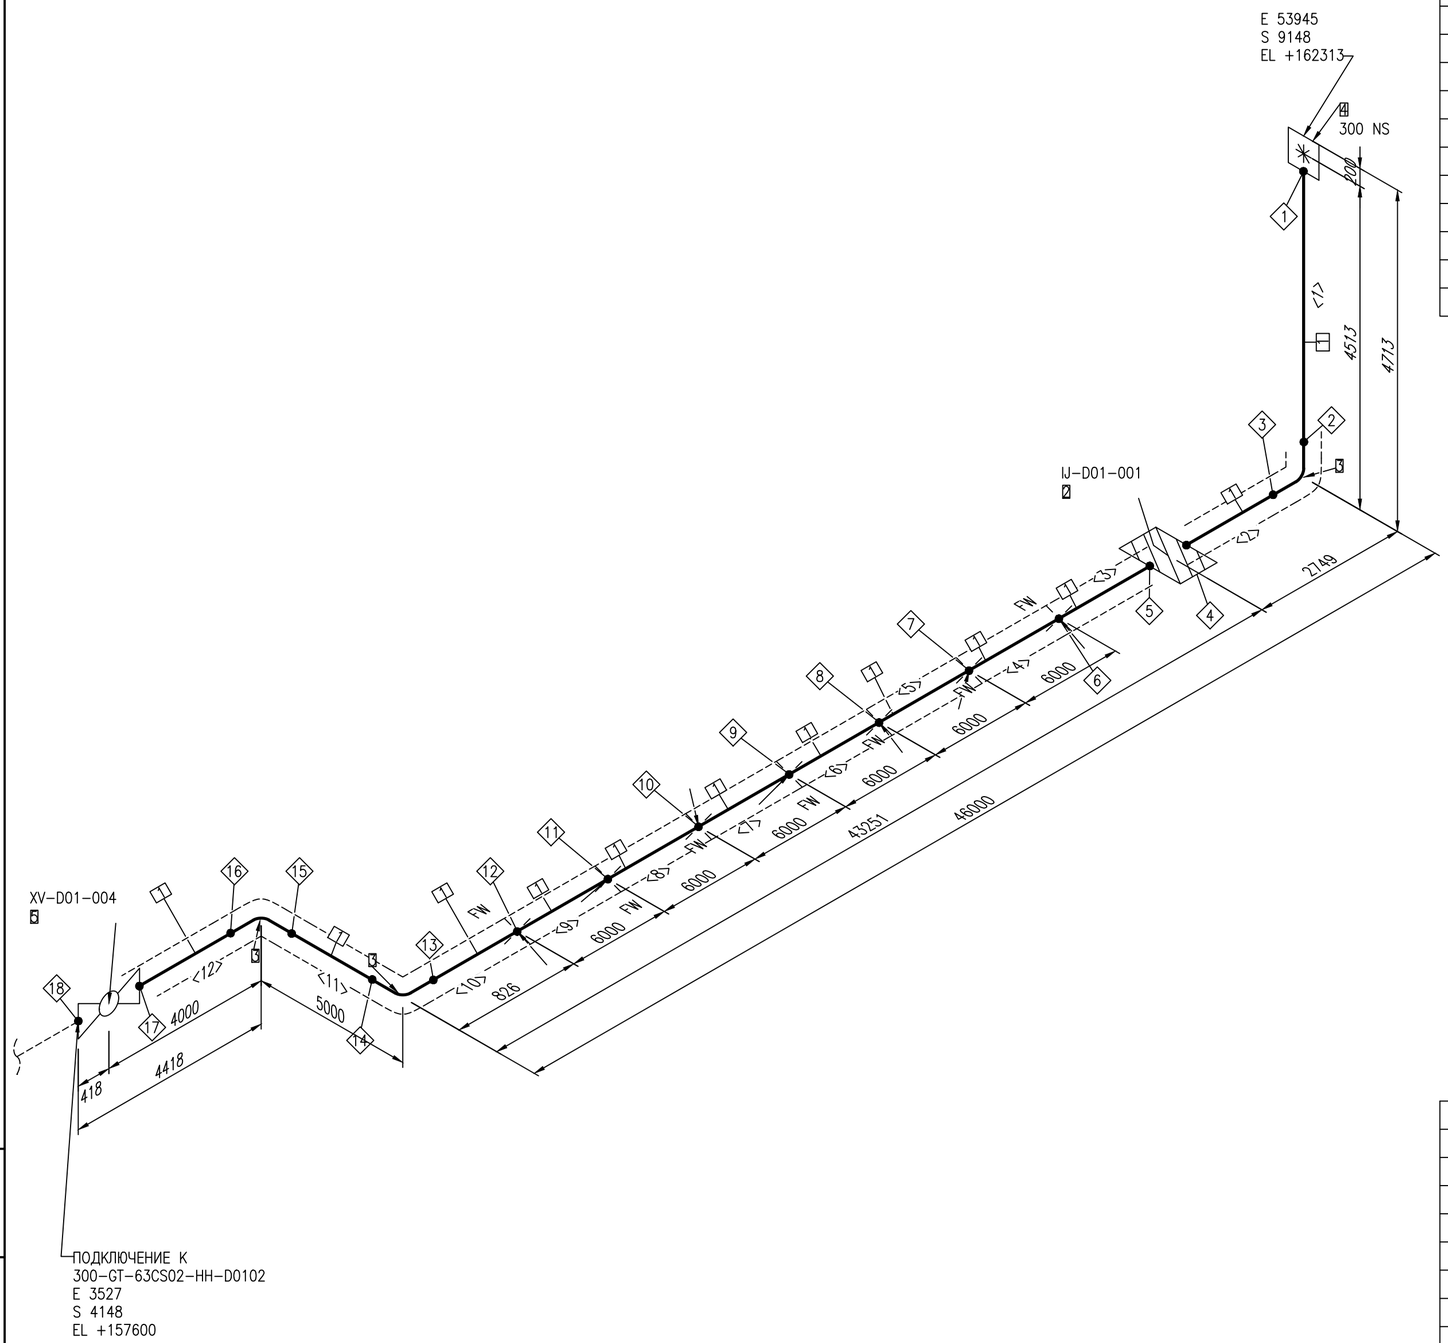

ПОДКЛЮЧЕНИЕ К
300-GT-63CS02-HH-D0102
E 3527
S 4148
EL +157600

ПЕРЕЧЕНЬ ТРУБНЫХ КАТУШЕК		
№	DN	ДЛИНА
1	300	3863MM
2	300	1874MM
3	300	6000MM
4	300	6000MM
5	300	6000MM
6	300	6000MM
7	300	6000MM
8	300	6000MM
9	300	6000MM
10	300	377MM
11	300	4100MM
12	300	3132MM

СПЕЦИФИКАЦИЯ ИЗДЕЛИЙ И МАТЕРИАЛОВ

ПОЗ.	НАИМЕНОВАНИЕ	СТАНДАРТ	КОЛ.	ПРИМЕЧАНИЕ
1	Трубы стальные бесшовные горячедеформированные 09Г2С, 325Х10	ТУ 14-3-1128-2000	55.4M	
2	Изолирующее соединение приварное, 6.3 МПа, 325Х10	EWE0426-MGL1-PRE-054-DSH-610135	1	
3	Отвод ОК I 90-325(10К48)-5,5(6,9)-0,75-1,5DN-30, сталь 09Г2С	ТУ 1469-017-38948552-2015	3	
4	Оголовок продувочной свечи, приварной, 6.3 МПа, ОПС-325-С-У, 325Х10	ТУ 1469-020-96950580-2011	1	
5	Кран шаровой DN300 PN-6,3 МПа с пневмогидроприводом, приварной, подземный	EWE0426-MGL1-PRE-054-DSH-610121	1	

Трубопровод	ДАННЫЕ ПО ТРУБОПРОВОДУ		
300-VA-63CS02-N-D0115	Расчетные параметры	Температура	-26,9...+85 °C
		Давление	6,3 MPa
	Рабочие параметры	Температура	-20...+40 °C
		Давление	5,5 MPa
	Параметры испытания	Тип	Гидравлическое
Ссылочные чертежи No		Давление	6,9 MPa
EWE0426-MGL1-PRE-054-SCM-610103	Изоляция	Тип	HH
		Толщина	mm
	Катодная защита	Да или Нет	Да

Рев.	Дата	Назначение ревизии	Проверил	Утвердил
A1	07.09.2026	Утверждено для строительства		
R1	22.06.2026	Выпущено для рассмотрения		

ЗАКАЗЧИК: UTG | ГЕНЕРАЛЬНЫЙ ПОДРЯДЧИК: UET | ПОДРЯДЧИК: PBG | ГЕНЕРАЛЬНЫЙ ПРОЕКТИРОВЩИК: EAST WEST ENGINEERING

Изм.	Кол.уч.	Лист	№док.	Подпись	Дата
ГИП		Кирпичников С.			09.2026
Нач.отд.		Рябинин А.			09.2026
Исполн.		Таштимуров Р.			09.2026
Н.контр		Кирпичников С.			09.2026

EWE0426-MGL1-PRE-054-ISO-700607-A1

«СТРОИТЕЛЬСТВО НОВЫХ НИТОК (УЧАСТКОВ) ГАЗОПРОВОДОВ «ГАЗЛИ - САРИМОЙ» И «АКЧАЛОК - ГАЗЛИ - НУКУС» ОБЩЕЙ ПРОТЯЖЕННОСТЬЮ НЕ МЕНЕЕ 275 КМ».

ГАЗОПРОВОД «ГАЗЛИ-САРИМОЙ» (54 КМ)
Линейный крановый узел DN1200 КУП-D1

Стадия	Лист	Листов
РД	1	1

Изометрический чертеж трубопровода
300-VA-63CS02-N-D0115

ООО "EAST-WEST Engineering"
г. Ташкент 2026г.

Взам. инв. №
Подпись и дата
Инв.№ подл.

Формат А2 594x420