


План / Plan
М (1:50)

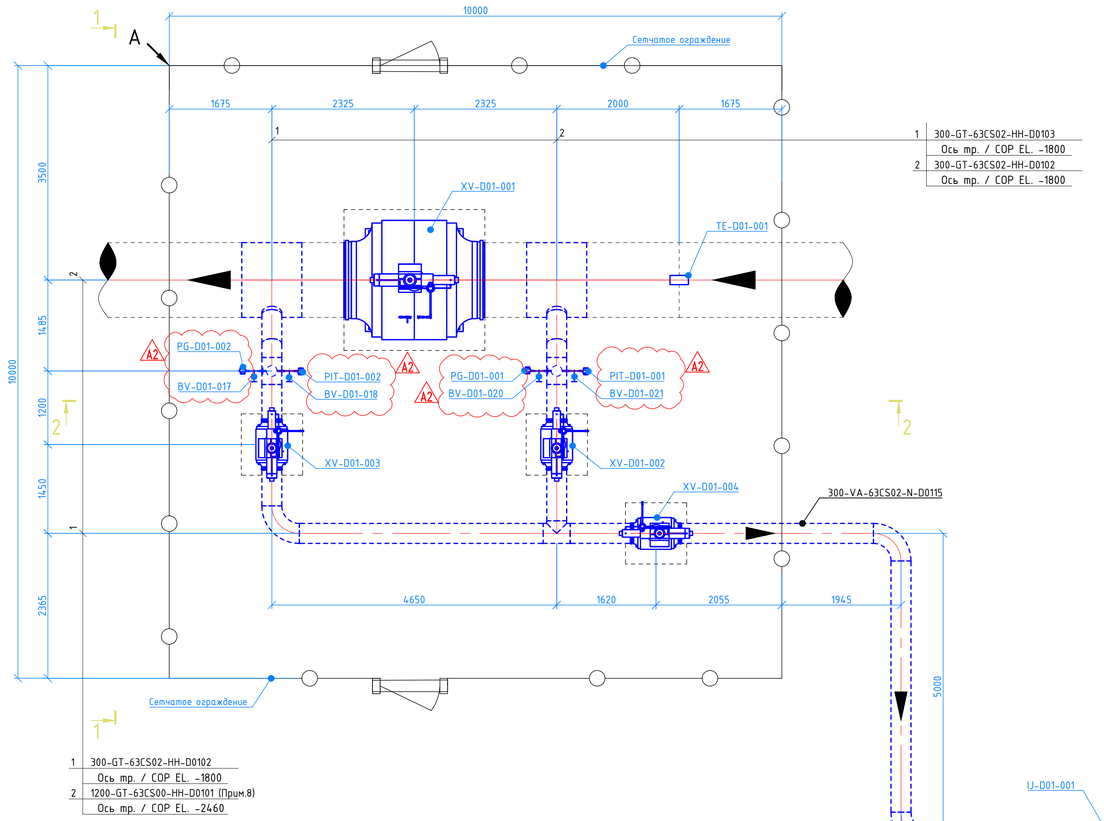


Изометрический вид "А"
М (1:50)

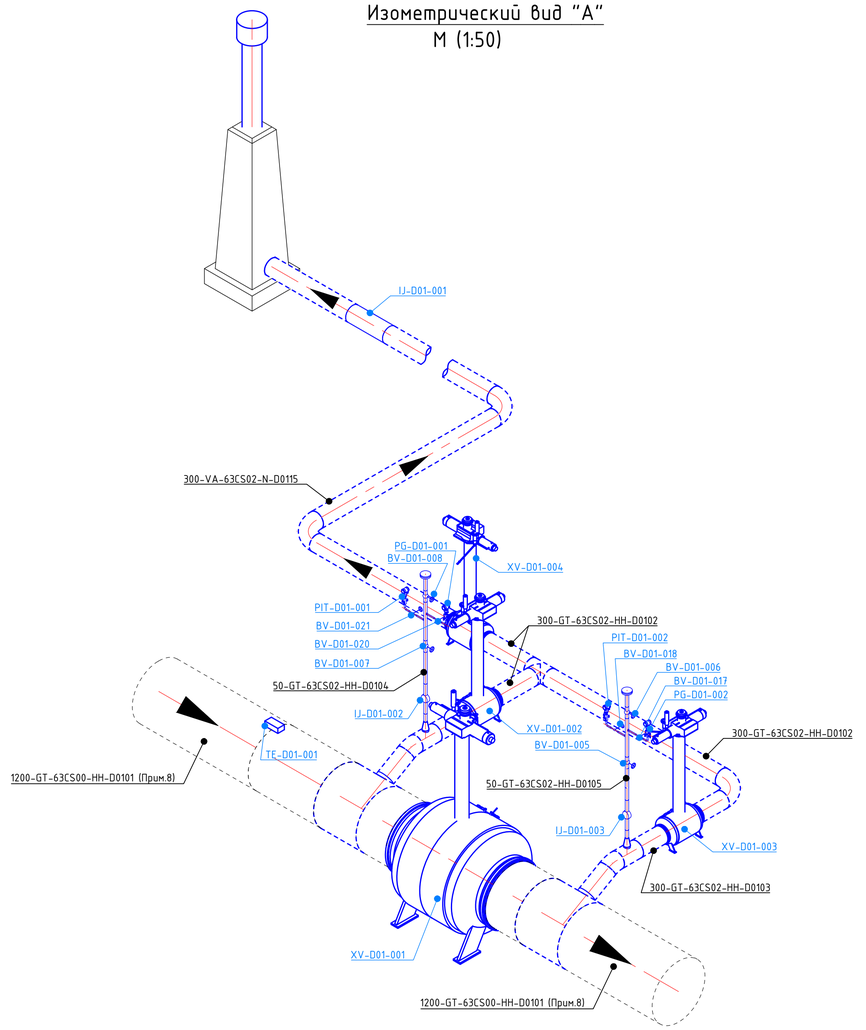

Разрез / Section 1-1
М (1:50)

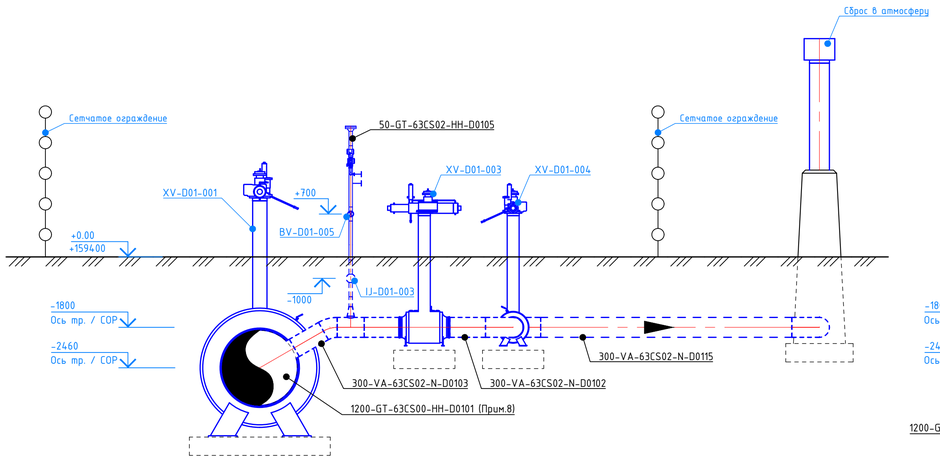

Разрез / Section 2-2
М (1:50)

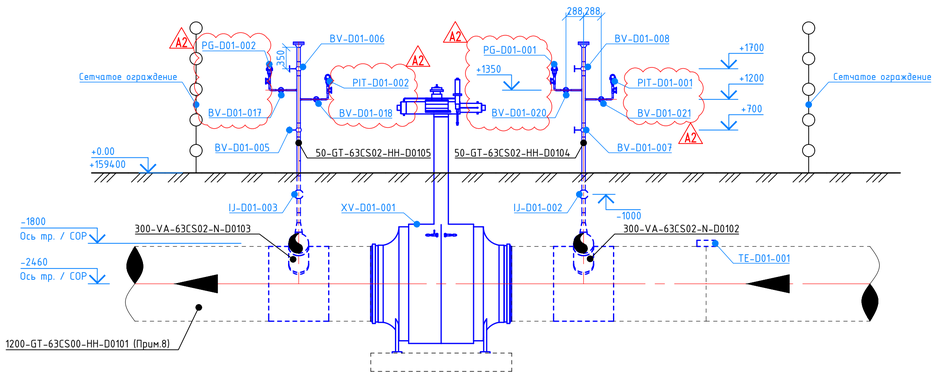

Условные обозначения:

N - нет изоляции
НН - гидроизоляция от почвенной коррозии

ПРИМЕЧАНИЯ

1. Общие данные см. EWE0426-MGL1-PRE-054-COM-700201;
2. * - Размеры для справок;
3. ** - Размеры уточнить по месту;
4. Кран XV-D01-001 расположен на пикете ПК 0+31 проектного газопровода;
5. Размеры фитингов - по ГОСТ. Все размеры указаны в миллиметрах;
6. Высотные отметки уточнить по месту;
7. Данный чертеж составлен на основе EWE0426-MGL1-PIL-054-COM-660201;
8. Труба учтена в линейной части проекта;
9. Привязка к пикетажу указана в EWE0426-MGL1-PRE-054-PLA-700202;
10. Фундаменты под опоры, шаровой кран XV-D01-001, продувочную свечу см. EWE0426-MGL1-STR-054-COM-700501;
11. Детальную информацию по трубопроводам см. изометрические чертежи;
12. На схеме указано основное направление потока газа, согласно схеме PFD, см. EWE0426-MGL1-PRE-054-PFD-610101. В процессе эксплуатации поток может быть направлен в обратном направлении.

A2	28.08.2026	Утверждено для строительства		
A1	24.07.2026	Утверждено для строительства		
R1	19.06.2026	Выпущено для рассмотрения		
Рев	Дата	Назначение ревизии	Проверил	Утвердил

ЗАКАЗЧИК: UTG | ГЕНЕРАЛЬНЫЙ ПОДРЯДЧИК: UET | ПОДРЯДЧИК: PBG | ГЕНЕРАЛЬНЫЙ ПРОЕКТИРОВЩИК: EAST WEST ENGINEERING

EWE0426-MGL1-PRE-054-DRW-700203-A2

«СТРОИТЕЛЬСТВО НОВЫХ НИТОК (УЧАСТКОВ) ГАЗОПРОВОДОВ «ГАЗЛИ - САРИМОЙ» И «АКЧАЛОК - ГАЗЛИ - НУКУС» ОБЩЕЙ ПРОТЯЖЕННОСТЬЮ НЕ МЕНЕЕ 275 КМ».

Изм.	Кол.уч.	Лист	№док.	Подпись	Дата
ГИП		Схабицкий А.			08.2026
Нач.отд.		Радинин А.			08.2026
Исполн.		Таштимуров Р.			08.2026
Н.контр		Схабицкий А.			08.2026

ГАЗОПРОВОД «ГАЗЛИ-САРИМОЙ» (54 КМ). Линейный крановый узел DN1200 КУП-D1.

КУП-D1. План. Разрезы. Виды. М 1:50

Стадия	Лист	Листов
РП	1	1

ООО "EAST-WEST Engineering" г. Ташкент 2026г.

Взам. инв. №

Подпись и дата

Инв.№ подл.

Формат / Format A1