
Линейный крановый узел КУП-D1.

План 1 (1:50)

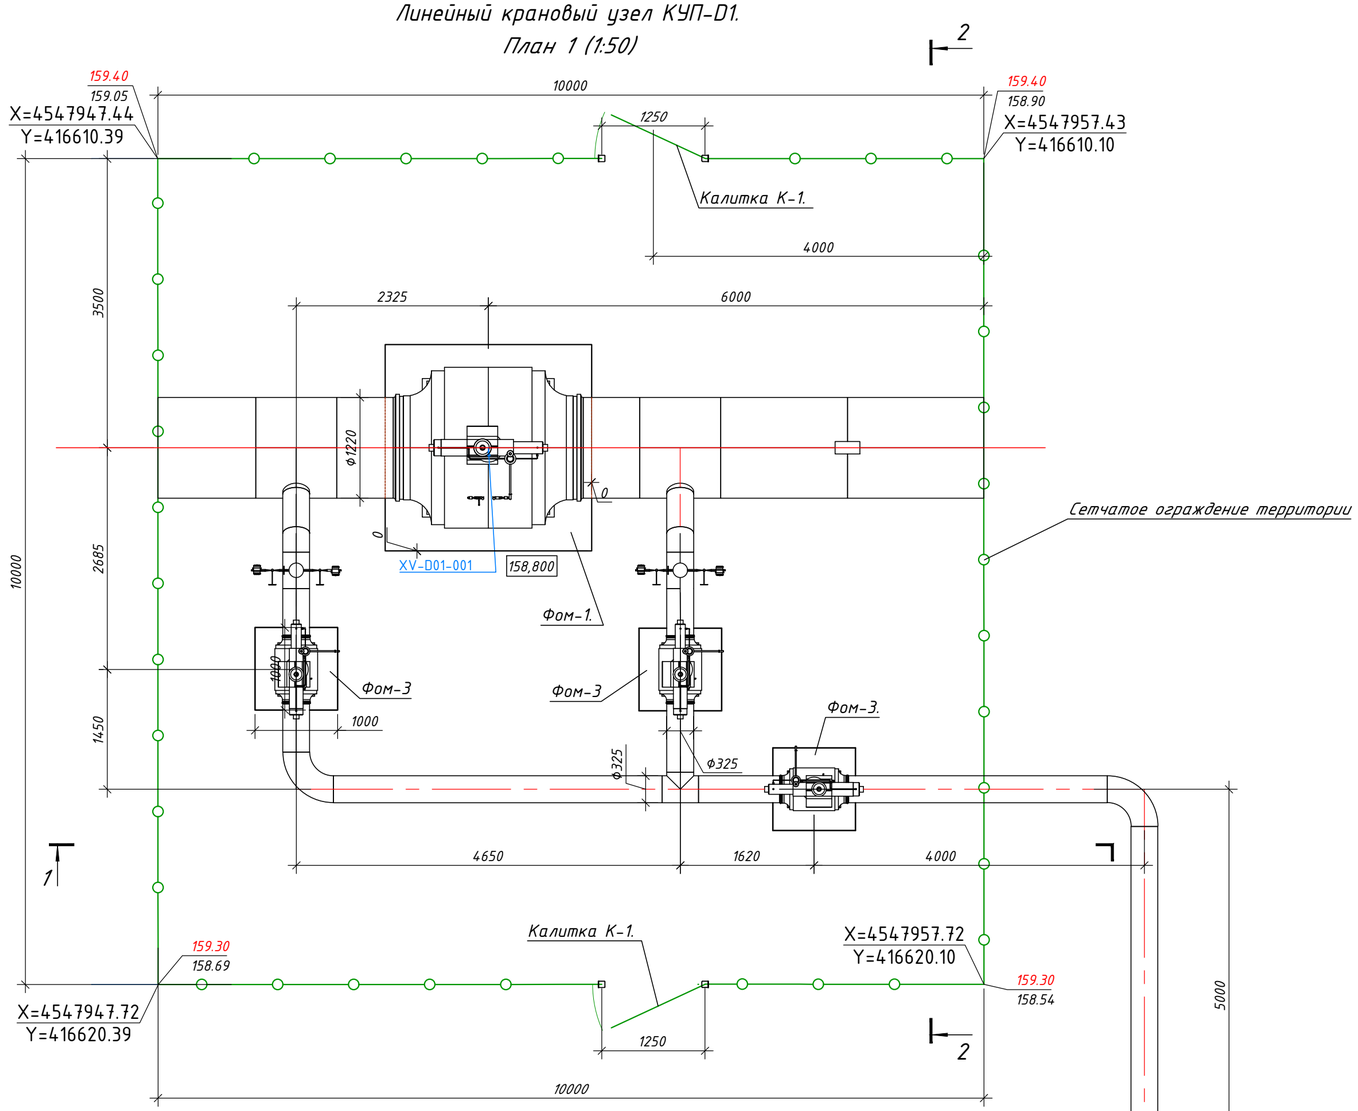

Спецификация элементов

Марка Поз.	Обозначение	Наименование	Кол. шт.	Масса ед.кг	Примеч.
		Линейный крановый узел КУП-D1.			
Фом-1	EWE0426-MGL1-STR-054-DRW-700504	Фундамент оборудования, монолитный Фом-1	1		
Фом-2	EWE0426-MGL1-STR-054-DRW-700505	Фундамент оборудования, монолитный Фом-2	1		
Фом-3	EWE0426-MGL1-STR-054-DRW-700506	Фундамент оборудования, монолитный Фом-3	3		

Примечание:

1. *Установка кранового узла КУП-D1 (Ду1200) расположена на ПК0+31 трассы проектного газопровода, подключение к газопроводу Газли-Нукус I нитка;*

A1	09.09.2026	Выпущено для строительства		
R1	16.07.2026	Выпущено для рассмотрения		
Рев	Дата	Назначение ревизии	Проверил	Утвердил

ЗАКАЗЧИК: ГЕНЕРАЛЬНЫЙ ПОДРЯДЧИК: ПОДРЯДЧИК: ГЕНЕРАЛЬНЫЙ ПРОЕКТИРОВЩИК:

Изм.	Кол.уч.	Лист	№ док.	Подпись	Дата
ГИП		Кирпичников С.			09.09.26
Нач.отд.		Каршиев А.			09.09.26
Исполн.		Хабиров Х.			09.09.26
Н.контр		Кирпичников С.			09.09.26

EWE0426-MGL1-STR-054-DRW-700502-A1

«СТРОИТЕЛЬСТВО НОВЫХ НИТОК (УЧАСТКОВ) ГАЗОПРОВОДОВ «ГАЗЛИ – САРИМОЙ» И «АКЧАЛОК – ГАЗЛИ – НУКУС» ОБЩЕЙ ПРОТЯЖЕННОСТЬЮ НЕ МЕНЕЕ 275 КМ».

ГАЗОПРОВОД "ГАЗЛИ-САРИМОЙ" (54 КМ) Линейный крановый узел DN1200 КУП-D1

Стадия	Лист	Листов
РП	1	1

Схема расположения кранового узла КУП-D1.

ООО "EAST-WEST Engineering" г. Ташкент 2026г.

Взам. инв. №

Подпись и дата

Инв.№ подл.

Формат / Format A2