
Разрез 1 – 1 м 1:25.

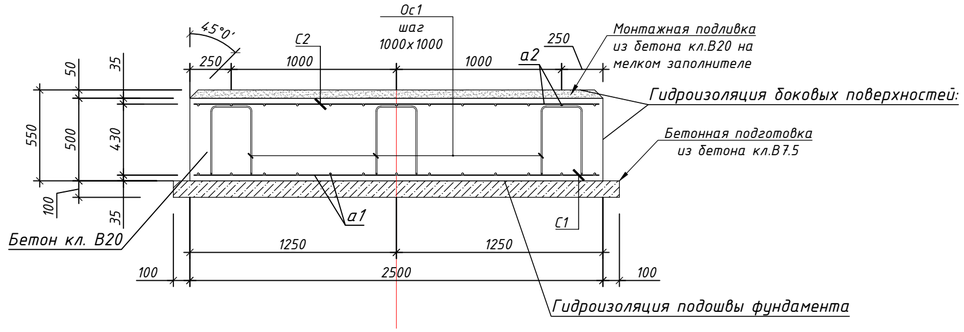

Ведомость деталей


Поз.	Эскиз
Ос1	250, 410, 410, 250, 250, L=1570

Размеры хомутов даны по центру стержня.


Спецификация элементов

Марка Поз.	Обозначение	Наименование	Кол.шт	Масса ед., кг	Прим.
		Фундамент Фом-1			
		Сборные единицы			
С1	См. данный лист	Сетка С1	1		127.18
С2	См. данный лист	Сетка С2	1		56.53
		Сетка С1			
а1	ГОСТ 34028-2016	Ф18 А500 L=2450 мм	26	4.89	127.18
		Детали			
Ос1	ГОСТ 34028-2016	Ф12 А240 L=1570 мм	13	1.39	18.11
		Сетка С2			
а2	ГОСТ 34028-2016	Ф12 А500 L=2450 мм	26	2.17	56.53
		Материалы			
	на подливку	Бетон на мелком заполнителе кл. В20, W6, F50			0.30 м³
		Бетон кл. В20, W6, F50			3.13 м³
	на подготовку	Бетон кл. В7.5			0.73 м³
		Гидроизоляция фундамента на площади:			18,55 м²

План фундамента Фом-1 м 1:50.

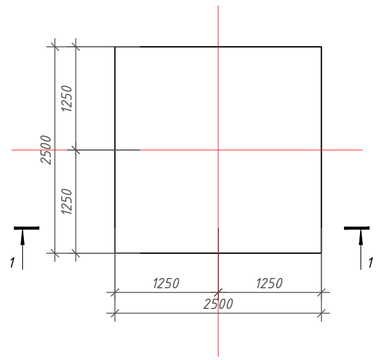

Сетка С1 м 1:50.

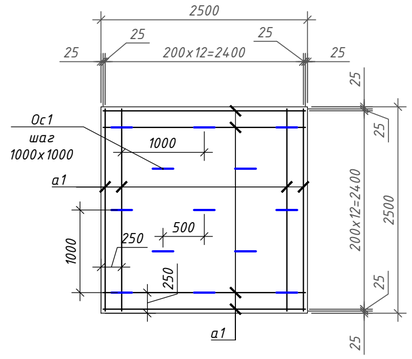

Примечания:

1. Объединение арматурных стержней в плоские сетки или пространственные каркасы выполнять вязальной стальной отожженной проволокой d=0.8-1.0мм. Применение ручной электродуговой сварки не допускается.
2. Подливку выполнить из бетона кл. В20 на мелком заполнителе.
3. Фундамент Фом-1 разработан под шаровой кран. Бетонирование выполнять после получения оборудования и сверки с паспортными данными.
4. Фиксаторы для крепления двух сеток марки Ос-1 устанавливать в шахматном порядке.
5. Расположение фундамента смотри чертёж: Схема расположения кранового узла КУП-D1.
6. Фундаментов Фом-1 изготовить в количестве - 1шт.
7. Бетон для фундамента применять на сульфатостойком портландцементе.

Гидроизоляция фундамента из двух слоев полимерной мастики на основе эмали ХВ-785 по ГОСТ 7313-2002 толщиной 25 мкм по грунтовке из лака ХВ-784 ГОСТ 7313-2002 толщиной слоя 20 мкм.

Ведомость расхода стали, кг

Марка элемента	Изделия арматурные					Всего	Общий расход
	Арматура класса						
	А240		А500				
	ГОСТ 34028-2016		ГОСТ 34028-2016				
	Ф12	Итого	Ф18	Ф12	Итого		
Фундамент Фом1	18.11	18.11	127.18	56.53	183.71	201.82	201.82

Рев	Дата	Назначение ревизии	Проверил	Утвердил
А1	09.09.2026	Выпущено для строительства		
R1	16.07.2026	Выпущено для рассмотрения		

ЗАКАЗЧИК: UTG UZTRANSGAZ

ГЕНЕРАЛЬНЫЙ ПОДРЯДЧИК: UET

ПОДРЯДЧИК: PBG

ГЕНЕРАЛЬНЫЙ ПРОЕКТИРОВЩИК: EAST WEST ENGINEERING

EWE0426-MGL1-STR-054-DRW-700504-A1

«СТРОИТЕЛЬСТВО НОВЫХ НИТОК (УЧАСТКОВ) ГАЗОПРОВОДОВ «ГАЗЛИ – САРИМОЙ» И «АКЧАЛОК – ГАЗЛИ – НУКУС» ОБЩЕЙ ПРОТЯЖЕННОСТЬЮ НЕ МЕНЕЕ 275 КМ».

Изм.	Кол.уч.	Лист	№ док.	Подпись	Дата			
ГИП		Кирпичников С.			09.09.26	ГАЗОПРОВОД "ГАЗЛИ-САРИМОЙ" (54 КМ) Линейный крановый узел DN1200 КУП-D1	Стадия	Лист	Листов
Нач.отд.		Каршиев А.			09.09.26		РП	1	1
Исполн.		Хабиров Х.			09.09.26	Фундамент Фом-1.	ООО "EAST-WEST Engineering" г. Ташкент 2026г.		
Н.контр		Кирпичников С.			09.09.26				

Взам. инв. №

Подпись и дата

Инв.№ подл.

Формат / Format A2