
Линейный крановый узел КУП-D1.

Схема расположения сетчатого ограждения (1:50).

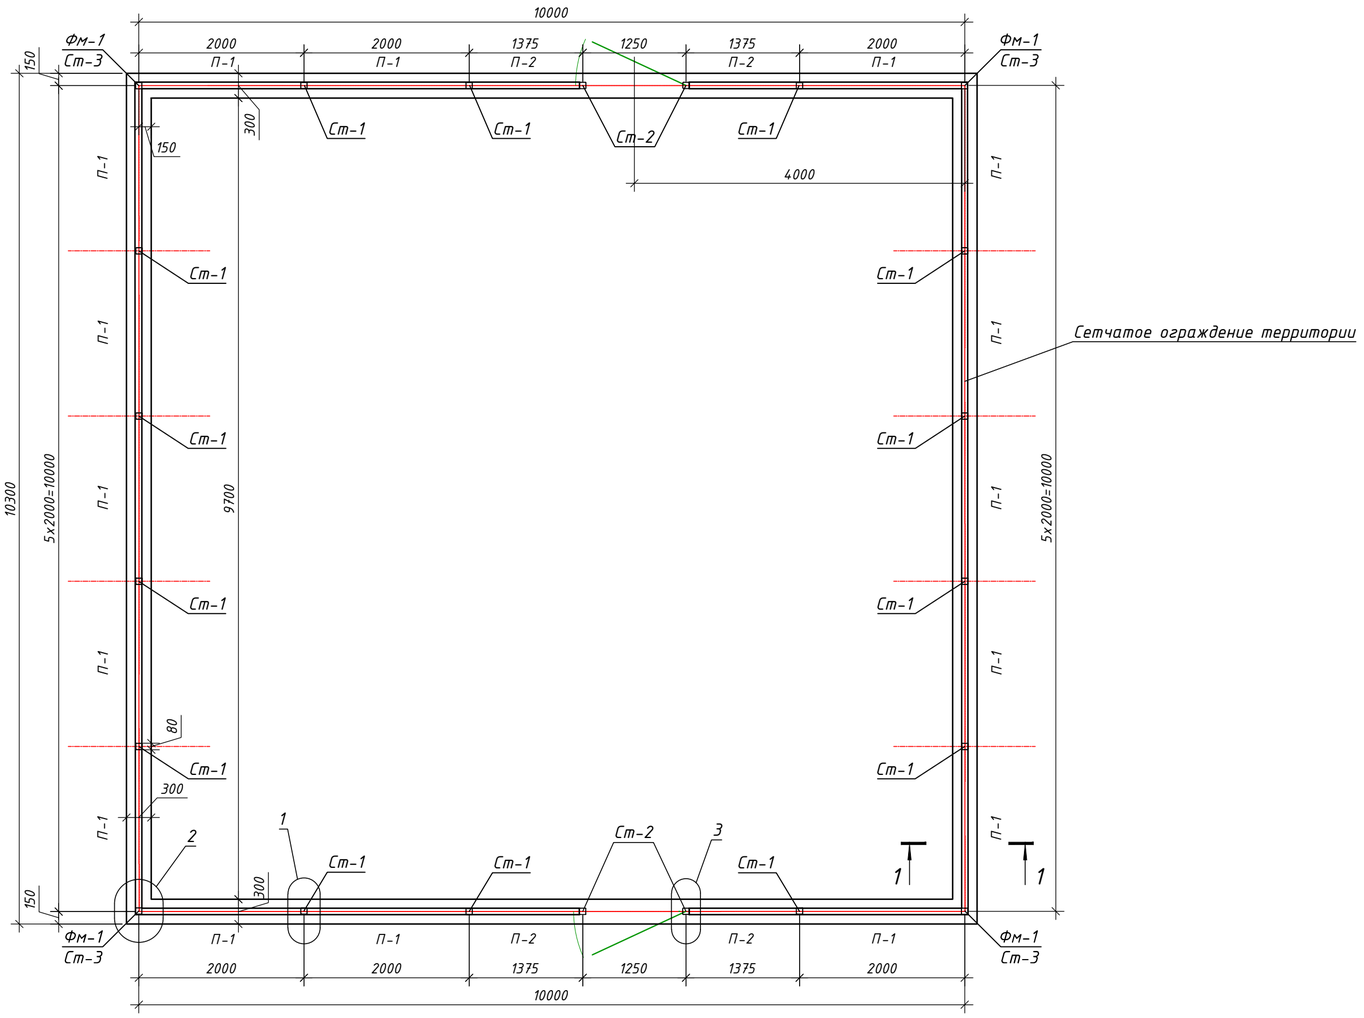


Спецификация элементов

Марка Поз.	Обозначение	Наименование	Кол. шт.	Масса ед.кг	Примеч.
		Линейный крановый узел КУП-D1.			
Фм-1	EWE0426-MGL1-STR-054-DRW-700509	Фундамент ленточный, монолитный Фм-1	1		
Ст-1	EWE0426-MGL1-STR-054-DRW-700510	Стойка ограждения Ст-1	14		
Ст-2	EWE0426-MGL1-STR-054-DRW-700511	Стойка ограждения Ст-2	4		
Ст-3	EWE0426-MGL1-STR-054-DRW-700512	Стойка ограждения Ст-3	4		
П-1	EWE0426-MGL1-STR-054-DRW-700513	Панель ограждения П-1	16		
П-2	EWE0426-MGL1-STR-054-DRW-700514	Панель ограждения П-2	4		
К-1	EWE0426-MGL1-STR-054-DRW-700515	Калитка К-1	2		
КД1	EWE0426-MGL1-STR-054-DRW-700516	Крепежная деталь КД1	24		
КД2	EWE0426-MGL1-STR-054-DRW-700516	Крепежная деталь КД2	28		


Примечания:

1. Данный чертёж читать совместно с ленточным фундаментом Фм-1.
2. Изготовить общее количество узлов:
- узел 1 - 14 шт.
- узел 2 - 4шт.
- узел 3 - 4шт.


Узел 1

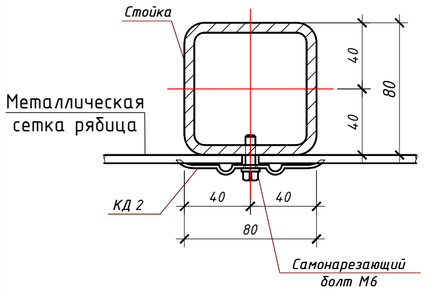

Узел 2

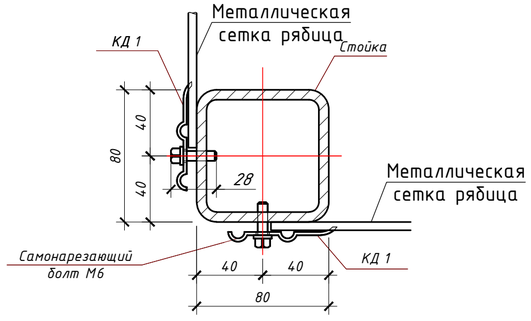

Узел 3

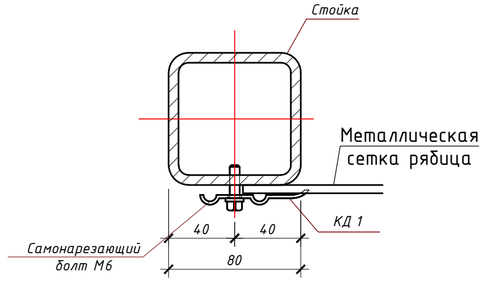

Рев	Дата	Назначение ревизии	Проверил	Утвердил
A1	09.09.2026	Выпущено для строительства		
R1	16.07.2026	Выпущено для рассмотрения		

ЗАКАЗЧИК: UTG | ГЕНЕРАЛЬНЫЙ ПОДРЯДЧИК: UET | ПОДРЯДЧИК: PBG | ГЕНЕРАЛЬНЫЙ ПРОЕКТИРОВЩИК: EAST WEST ENGINEERING

EWE0426-MGL1-STR-054-DRW-700507-A1

«СТРОИТЕЛЬСТВО НОВЫХ НИТОК (УЧАСТКОВ) ГАЗОПРОВОДОВ «ГАЗЛИ - САРИМОЙ» И «АКЧАЛОК - ГАЗЛИ - НУКУС» ОБЩЕЙ ПРОТЯЖЕННОСТЬЮ НЕ МЕНЕЕ 275 КМ».

Изм.	Кол.уч.	Лист	№ док.	Подпись	Дата
ГИП		Кирпичников С.			09.09.26
Нач.отд.		Каршиев А.			09.09.26
Исполн.		Хабиров Х.			09.09.26
Н.контр		Кирпичников С.			09.09.26

ГАЗОПРОВОД "ГАЗЛИ-САРИМОЙ" (54 КМ) Линейный крановый узел DN1200 КУП-D1

Схема расположения сетчатого ограждения.

Стадия	Лист	Листов
РП	1	1

ООО "EAST-WEST Engineering" г. Ташкент 2026г.

Взам. инв. №

Подпись и дата

Инв.№ подл.

Формат / Format A2