



Стойка ограждения Ст-2

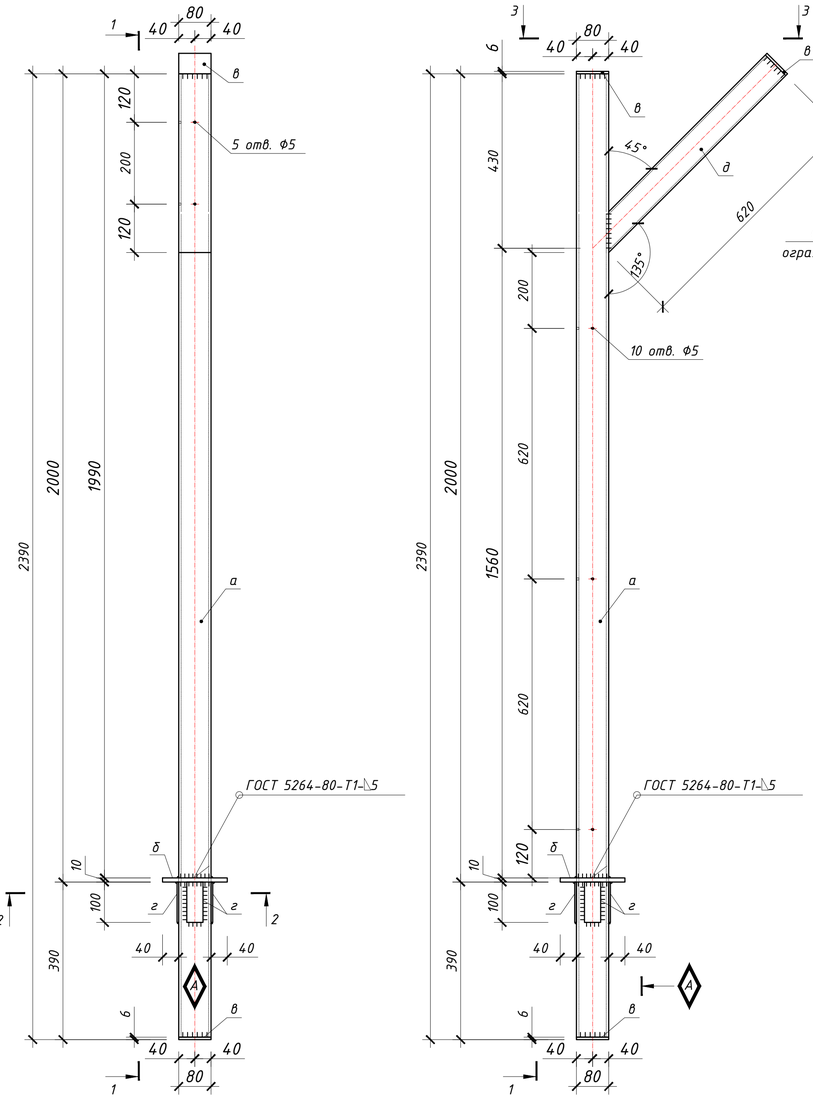


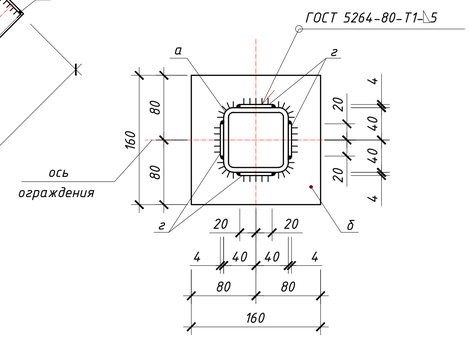

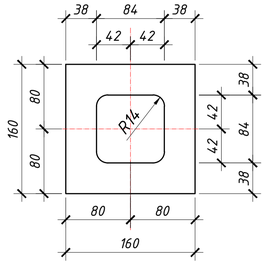

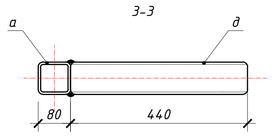

Деталь срезки стойки Ст-1. (поз. а)

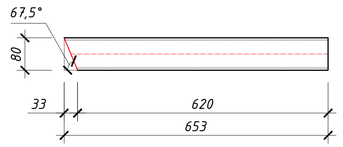

Спецификация элементов на одну марку

Марка поз.	Обозначение	Наименование	Кол. шт.	Масса ед.кг	Примечание
Ст-2	ГОСТ 30245-2003	Стойка ограждения Ст-2		27,6	вес на 1 стойку
а	ГОСТ 30245-2003	Профиль 80х80х4 ГОСТ 30245-2003 С255 ГОСТ 27772-2015 L=2390мм	1	24,55	24,55
б	ГОСТ 19903-90*	Лист t=10 ГОСТ 19903-90 С245 Гост 27772-2015 160х160мм	1	2,01	2,01
в	ГОСТ 19903-90*	Лист t=4 ГОСТ 19903-90 С245 Гост 27772-2015 80х80мм	2	0,20	0,4
г	ГОСТ 19903-90*	Лист t=4 ГОСТ 19903-90 С245 Гост 27772-2015 40х124мм	4	0,16	0,64
д	ГОСТ 30245-2003	Профиль 80х80х4 ГОСТ 30245-2003 С255 ГОСТ 27772-2015 L=620мм	1	5,72	5,72
		Материалы:			
		Окраска металлоконструкций масляной краской за 2 раза			1,14м²

Примечания:
1. Сварку вести электродами Э42А ГОСТ 9467-75.
2. Конструкция должна быть покрыта масляной краской за 2 раза по грунтовке.
3. Элемент "г" следует приварить к "а" в первую очередь.
4. Деталь-1 - деталь срезки стойки Ст-1. (поз. в)
5. Крепления стойки смотри Фундамента Фм-1.

А - Знак ориентации. Нанести несмываемой краской!

Отверстие для болта
Болт постоянный, нормальной точности
Болт временный, нормальной точности
Сварной шов заводской
Сварной шов монтажный

А1	09.09.2026	Выпущено для строительства		
R1	16.07.2026	Выпущено для рассмотрения		
Рев	Дата	Назначение ревизии	Проверил	Утвердил

ЗАКАЗЧИК: UTG UZTRANSGAZ ИНЖИНИРИНГ
ГЕНЕРАЛЬНЫЙ ПОДРЯДЧИК: UET UZBEKNEFTEGAZ
ПОДРЯДЧИК: PBG Pro Build Generation
ГЕНЕРАЛЬНЫЙ ПРОЕКТИРОВЩИК: EAST WEST ENGINEERING

EWE0426-MGL1-STR-054-DRW-700511-A1

«СТРОИТЕЛЬСТВО НОВЫХ НИТОК (УЧАСТКОВ) ГАЗОПРОВОДОВ «ГАЗЛИ - САРИМОЙ» И «АКЧАЛОК - ГАЗЛИ - НУКУС» ОБЩЕЙ ПРОТЯЖЕННОСТЬЮ НЕ МЕНЕЕ 275 КМ».

Изм.	Кол.уч.	Лист	№ док.	Подпись	Дата
ГИП		Кирпичников С.			09.09.26
Нач.отд.		Каршиев А.			09.09.26
Исполн.		Хабиров Х.			09.09.26
Н.контр		Кирпичников С.			09.09.26

ГАЗОПРОВОД "ГАЗЛИ-САРИМОЙ" (54 КМ) Линейный крановый узел DN1200 КУП-D1

Стойка ограждения Ст-2.

Стадия	Лист	Листов
РП	1	1

EAST WEST ENGINEERING
ООО "EAST-WEST Engineering"
г. Ташкент 2026г.

Взам. инв. №
Подпись и дата
Инв.№ подл.

Формат / Format A4X3