
Поз. обозна-чение	Наименование	Кол.	Примечание
	Кабель универсальный инструментальный КУИН нг(А) ВЭК		
	1х2х1,0	37	м
	8х2,5	55	м
			A1
	Труба ПНД 50	14	м
	Провод ПуГВ-Т 1х6 ж-з.	70	м

Наименование параметра и место установки	Давление		Температура	Температура
	См. таблицу применимости	См. таблицу применимости	См. таблицу применимости	См. таблицу применимости
Позиция	См. таблицу применимости	См. таблицу применимости	См. таблицу применимости	См. таблицу применимости

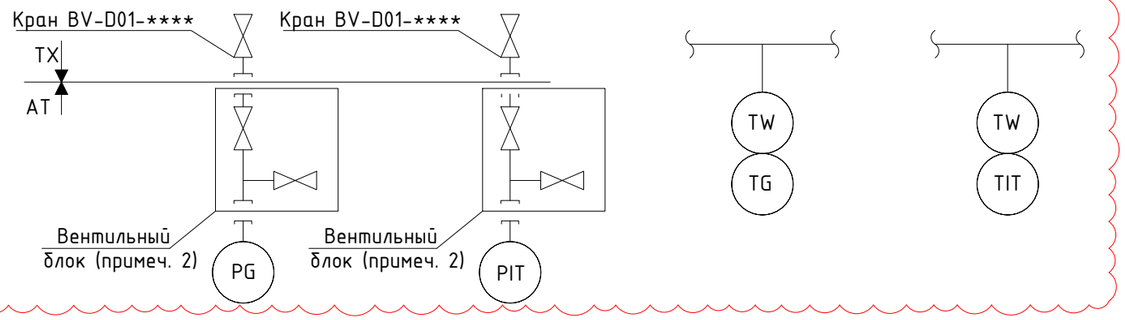

A1

Условные обозначения:

- Заземление
- Экран кабеля
- OS — Общий экран кабеля отогнуть и изолировать
- S — Индивидуальный экран кабеля отогнуть и изолировать
- Броня кабеля
- Заземление брони кабеля через кабельный ввод

Таблица применимости

Позиция прибора (**-****)	Место установки	Подключение к процессу
PG-D01-001	Тов. газ на линии тр. 50-GT-63CS02-HH-D0104	Кран BV-D01-020 1/2" NPT-F
PG-D01-002	Тов. газ на линии тр. 50-GT-63CS00-N-D01005	Кран BV-D01-017 1/2" NPT-F
PIT-D01-001	Тов. газ на линии тр. 50-GT-63CS00-N-D01004	Кран BV-D01-021 1/2" NPT-F
PIT-D01-002	Тов. газ на линии тр. 50-GT-63CS02-HH-D0105	Кран BV-D01-018 1/2" NPT-F
TIT-D01-001 TW-D01-001	Тов. газ на линии тр. 1200-GT-63CS00-N-D0101	Бобышка 3/4" NPT-F

A1

1. Схема разработана на основании P&ID EWE0426-MGL1-PRE-054-SCM-610102 ... EWE0426-MGL1-PRE-054-SCM-610120.
2. Двухвентильный блок поставляется комплектно с манометром или датчиком давления.
3. Свободные жилы кабеля и экран со стороны приборов изолировать от проводящих конструкций и грунта.
4. Броню кабелей присоединить к системе уравнивания потенциалов в устройствах кабельного ввода.
5. Длины кабелей даны с 10% запасом на изгибы, повороты и отходы.
6. Заземление приборов КИП выполнить присоединением провода ПуГВ-Т 1х6 ж-з к металлоконструкции стойки приборной КИПиА.
7. Корпус шкафа телемеханики и соединительных коробок присоединить к контуру заземления проводом ПуГВ-Т 1х6 ж-з.
8. Экран кабелей со стороны шкафа телемеханики присоединить к контору защитного заземления.
9. Подключение кабеля к пневмоприводу крана XV-* выполнить к клеммам, согласно принципиальной схемы крана.

Рев.	Дата	Назначение ревизии	Проверил	Утвердил
A1	18.08.2026	Утверждено для строительства		
R1	09.07.2026	Выпущено для рассмотрения		

ЗАКАЗЧИК: UTG UZKIMYOGAZ

ГЕНЕРАЛЬНЫЙ ПОДРЯДЧИК: UET UZBEKENERGOTAMIR

ПОДРЯДЧИК: PBG Pre Build Generation

ГЕНЕРАЛЬНЫЙ ПРОЕКТИРОВЩИК: EAST WEST ENGINEERING

Изм.	Кол.уч.	Лист	№док.	Подпись	Дата	
ГИП		Схабицкий А.			08.2026	
Нач.отд.		Кабулова Е.			08.2026	
Исполн.		Махмудов И.			08.2026	
Н.контр		Схабицкий А.			08.2026	

EWE0426-MGL1-SYS-054-SCM-700305-A1

«СТРОИТЕЛЬСТВО НОВЫХ НИТОК (УЧАСТКОВ) ГАЗОПРОВОДОВ «ГАЗЛИ - САРИМОЙ» И «АКЧАЛОК - ГАЗЛИ - НУКУС» ОБЩЕЙ ПРОТЯЖЕННОСТЬЮ НЕ МЕНЕЕ 275 КМ».

Газопрвод «Газли-Сарымой» (54 КМ) Линейный крановый узел DN1200 КУП-D1

Стадия	Лист	Листов
РД	1	3

Схема соединений и подключения внешних проводок

EAST WEST ENGINEERING

ООО "EAST-WEST Engineering" г. Ташкент 2026г.


Взам. инв. №

Подпись и дата

Инв.№ подл.

Формат / Format A3

Наименование параметра и место отбора импульса	Датчик температуры	Датчик давления		Пневмопривод крана	Пневмопривод крана
	Контроль температуры	Контроль давления		Управление краном	Управление краном
	Трубопровод 1200-GT-63CS00-HH-D0101	Трубопровод 50-GT-63CS02-HH-D0104	Трубопровод 50-GT-63CS02-HH-D0105	Трубопровод 1200-GT-63CS00-HH-D0101	Трубопровод 300-GT-63CS02-HH-D0102
Обозначение чертежа установки	EWE0426-MGL1-SYS-054-PLA-700306				
Позиция	TIT-D01-001	PIT-D01-001	PIT-D01-002	XV-D01-001	XV-D01-002

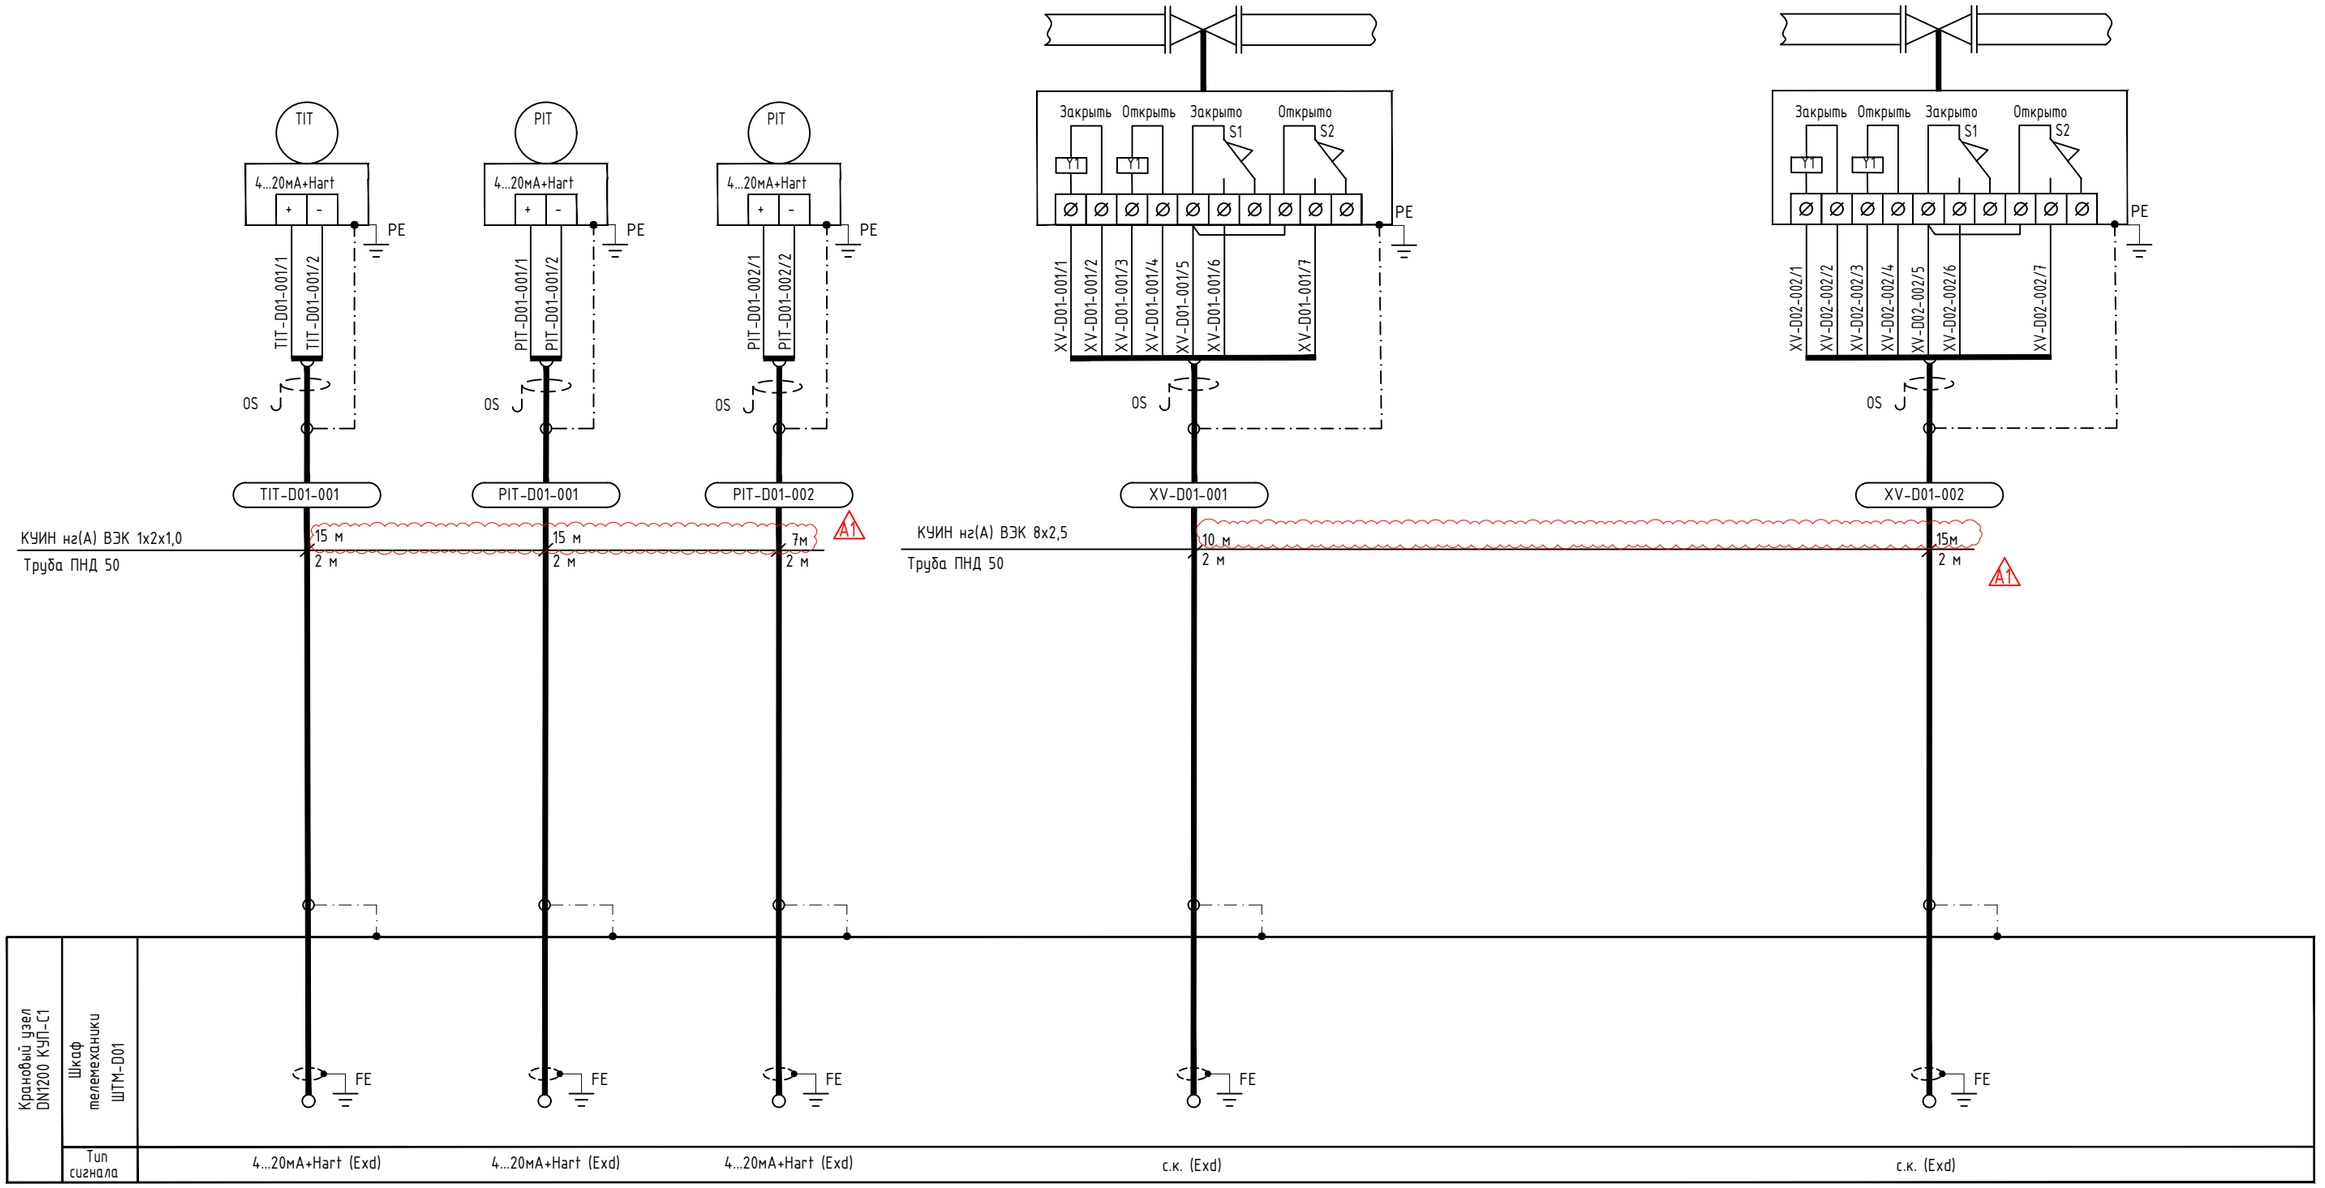

Крановый узел DN1200 КУП - D1

Изм.	Кол.уч	Лист	№ док.	Подпись	Дата	EWE0426-MGL1-SYS-054-SCM-700305-A1	Лист 2

Формат А3


Согласовано:

Взамен инв. №

Подпись и дата

Инв.№ подл.

Наименование параметра и место отбора импульса	Пневмопривод крана	Пневмопривод крана
	Управление краном	Управление краном
	Трубопровод 300-GT-63CS02-HH-D0103	Трубопровод 300-GT-63CS02-HH-D0102
Обозначение чертежа установки		
Позиция	XV-D01-003	XV-D01-004

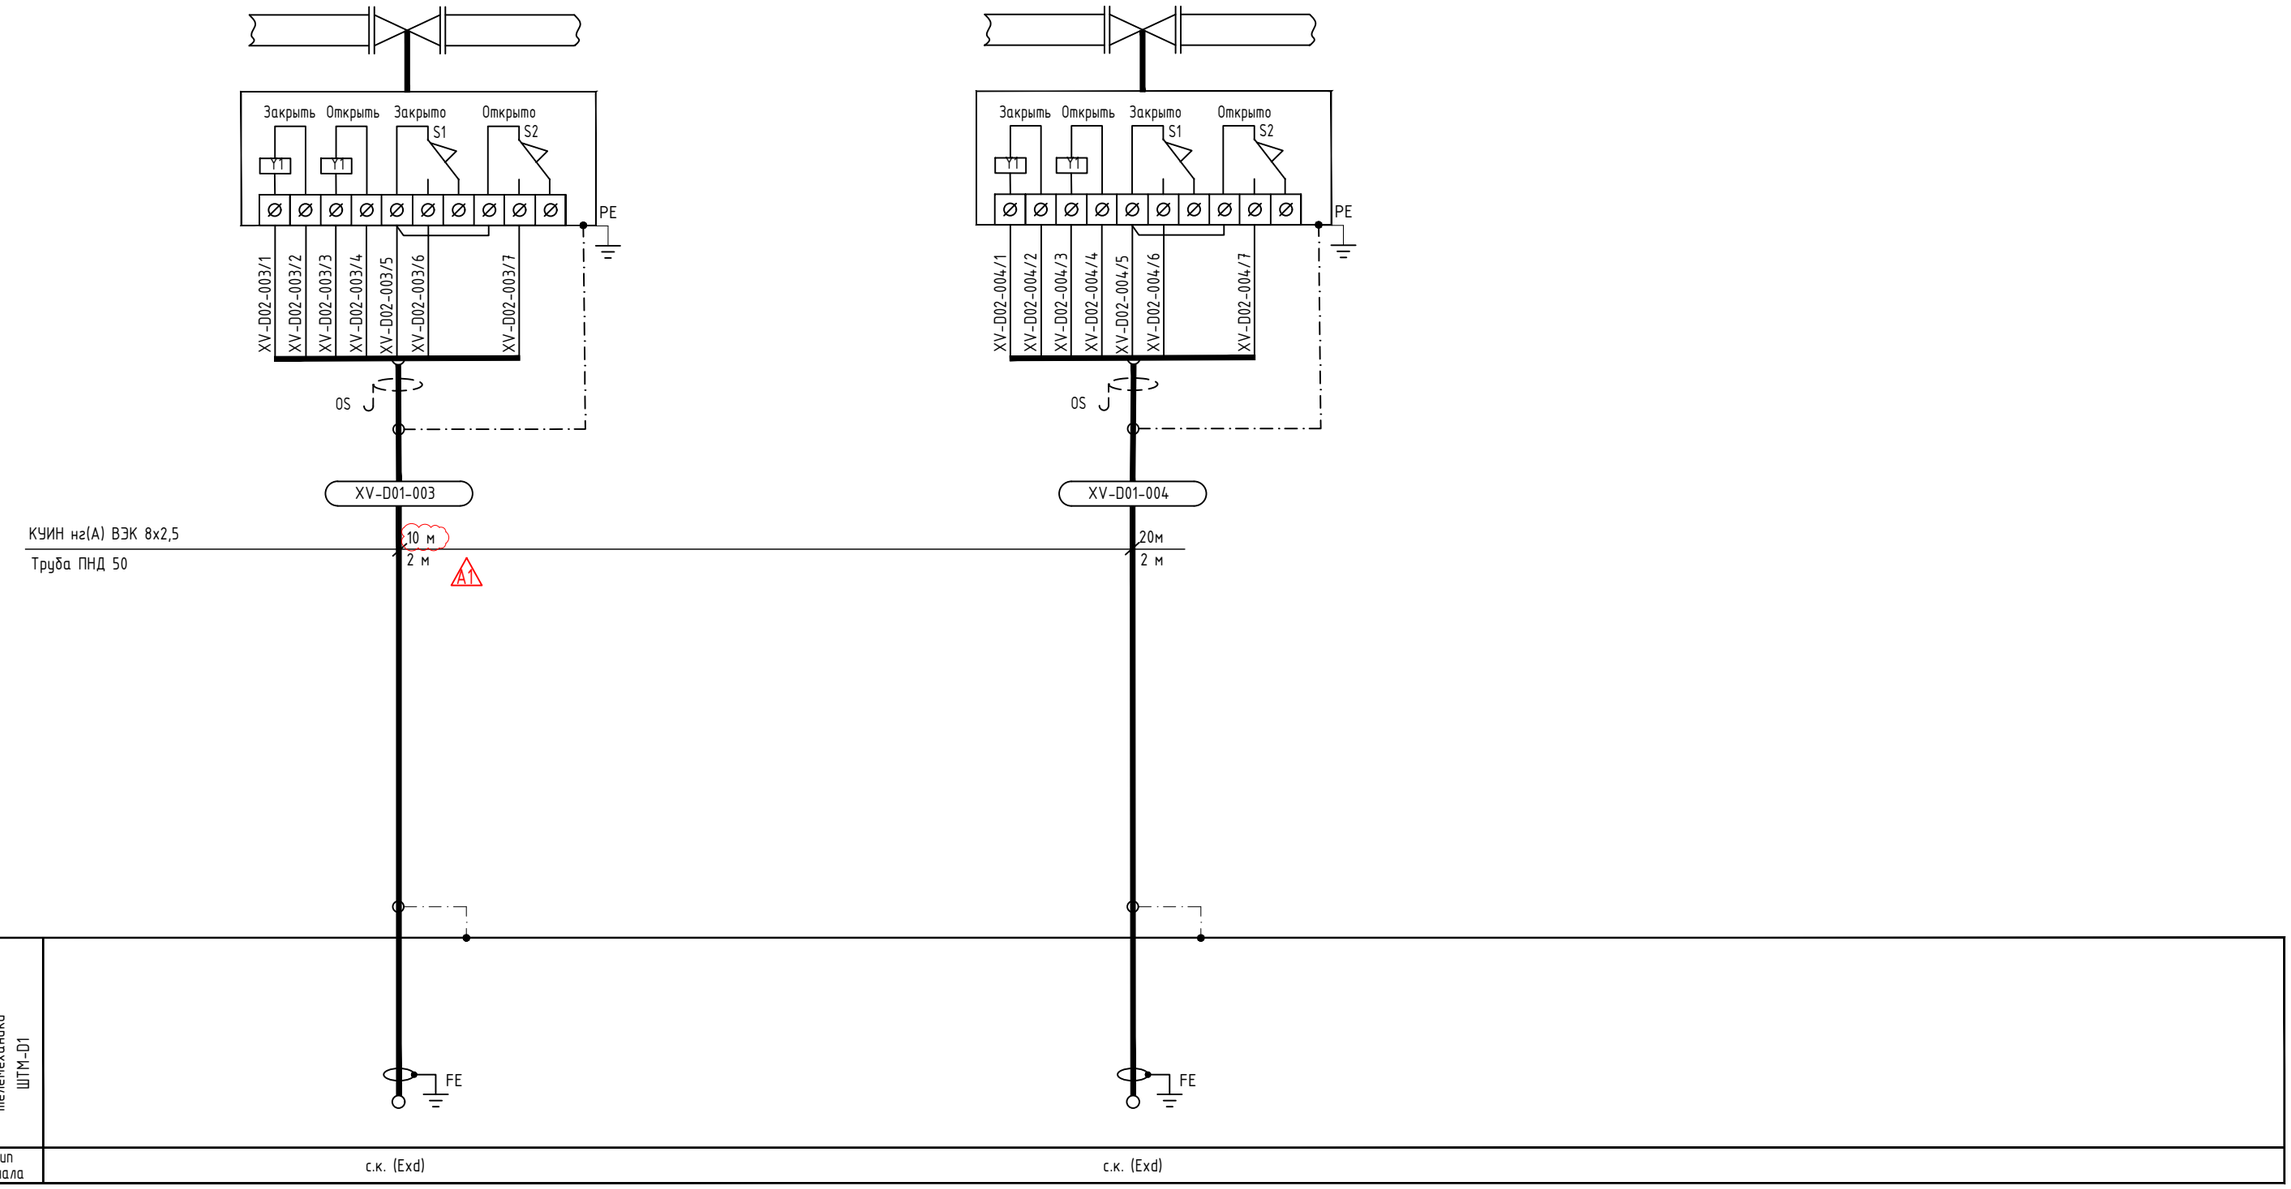

Согласовано:

Взамен инв. №

Подпись и дата

Инв.№ подл.

Изм.	Кол.уч	Лист	№ док.	Подпись	Дата	EWE0426-MGL1-SYS-054-SCM-700305-A1	Лист 3

Формат А3